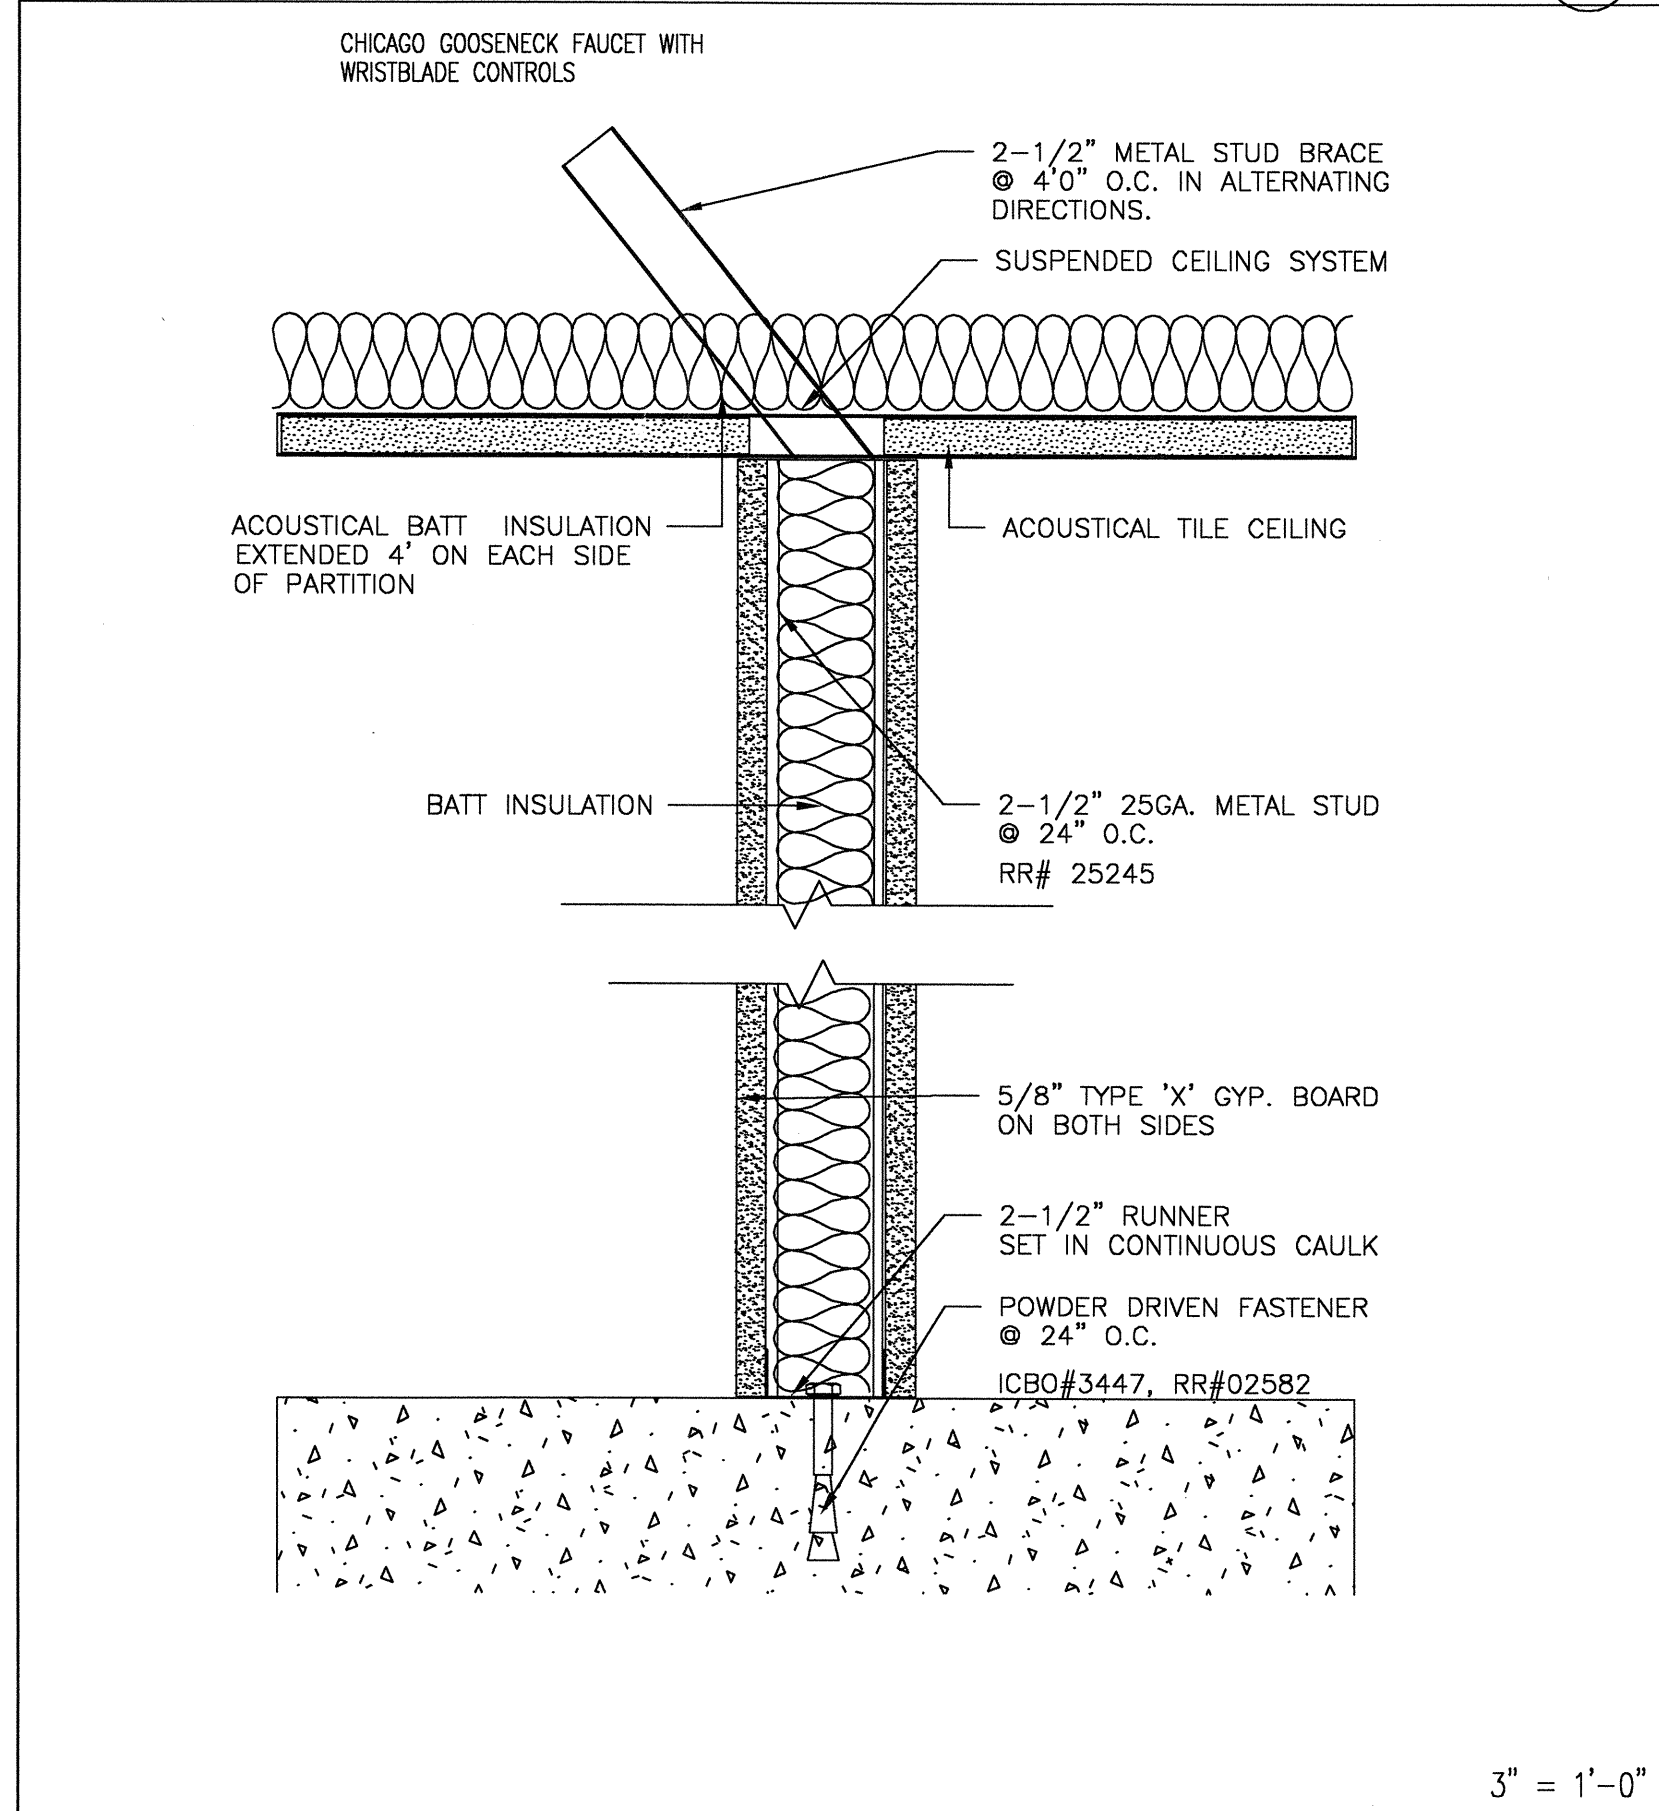
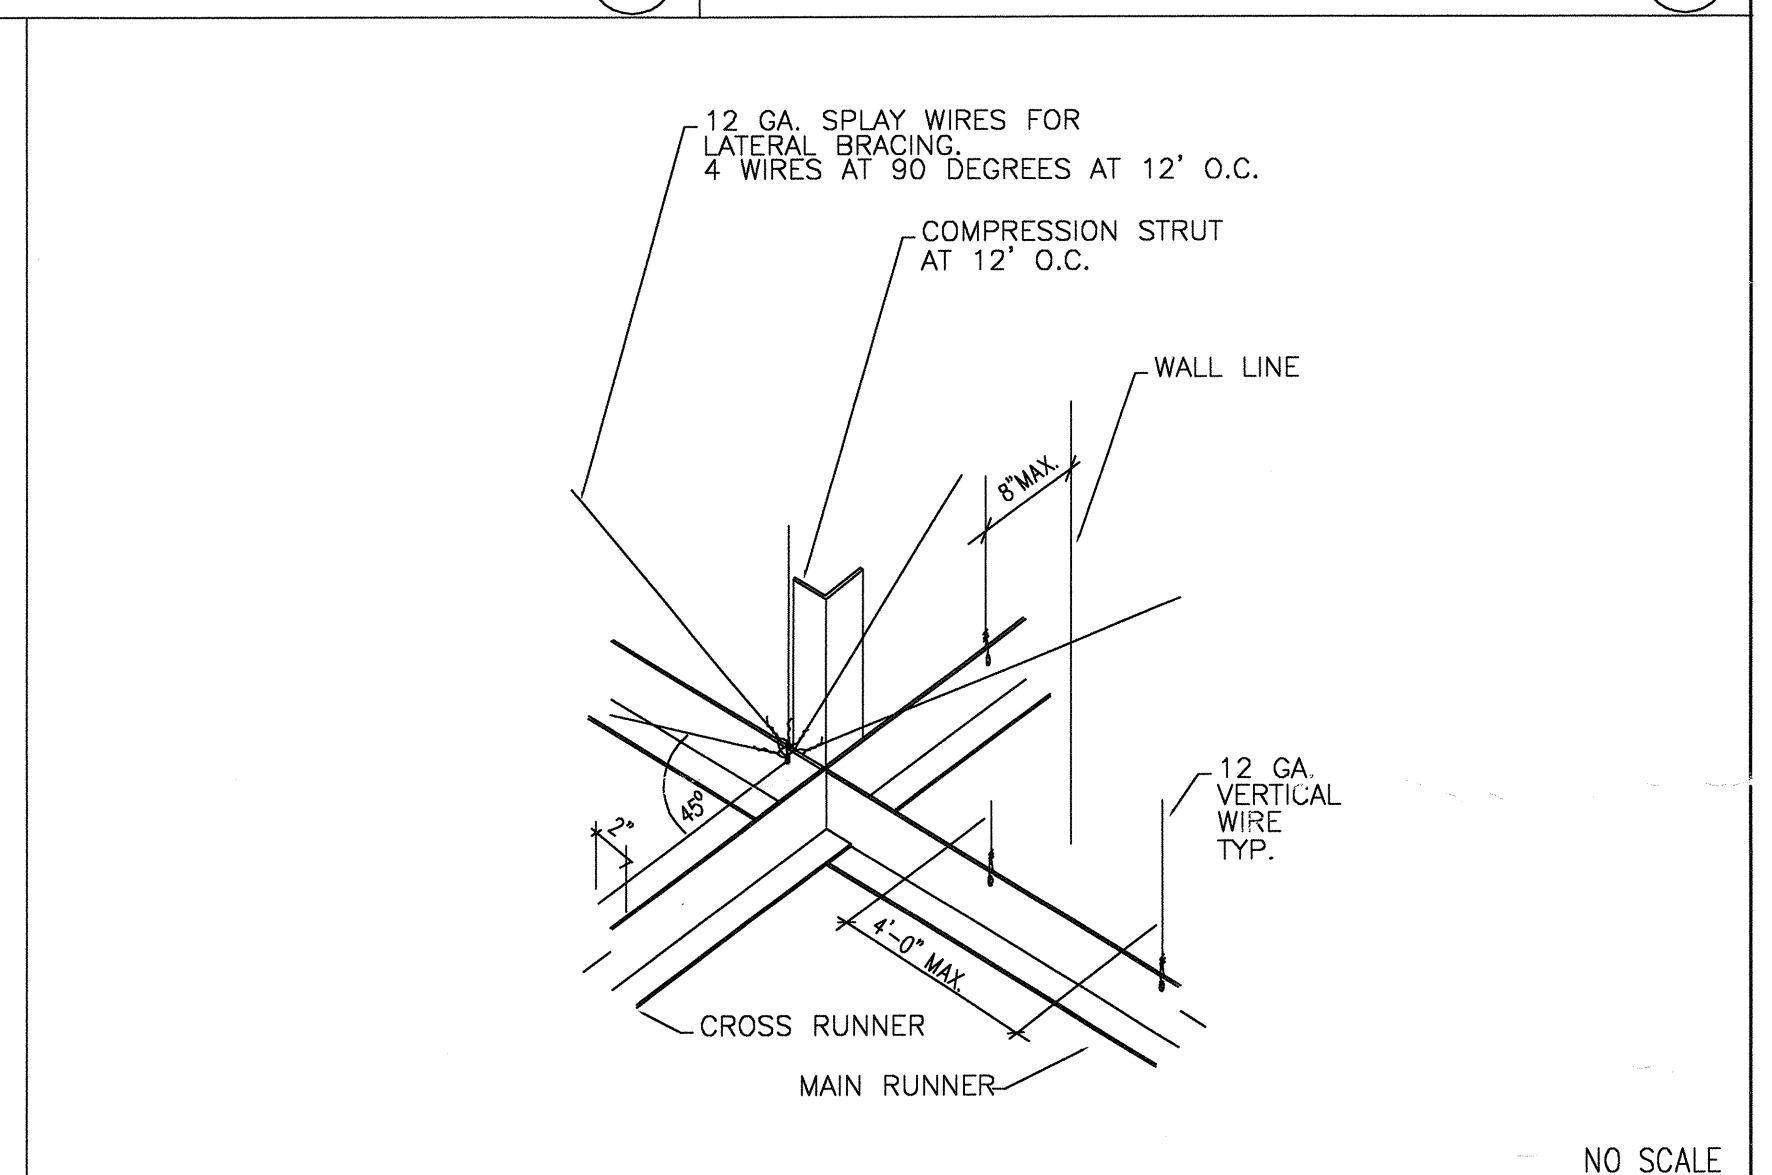
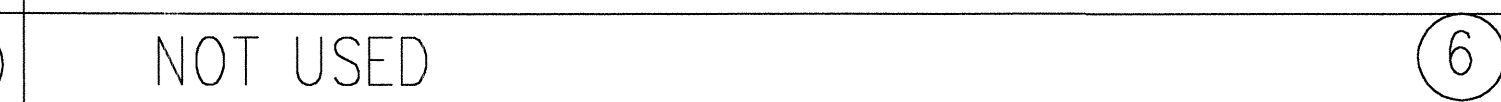
 
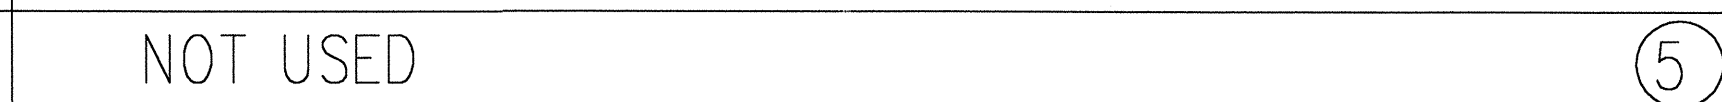
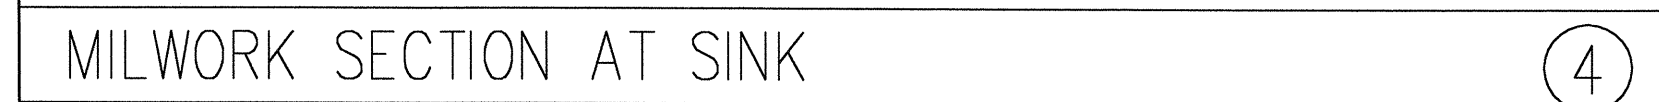
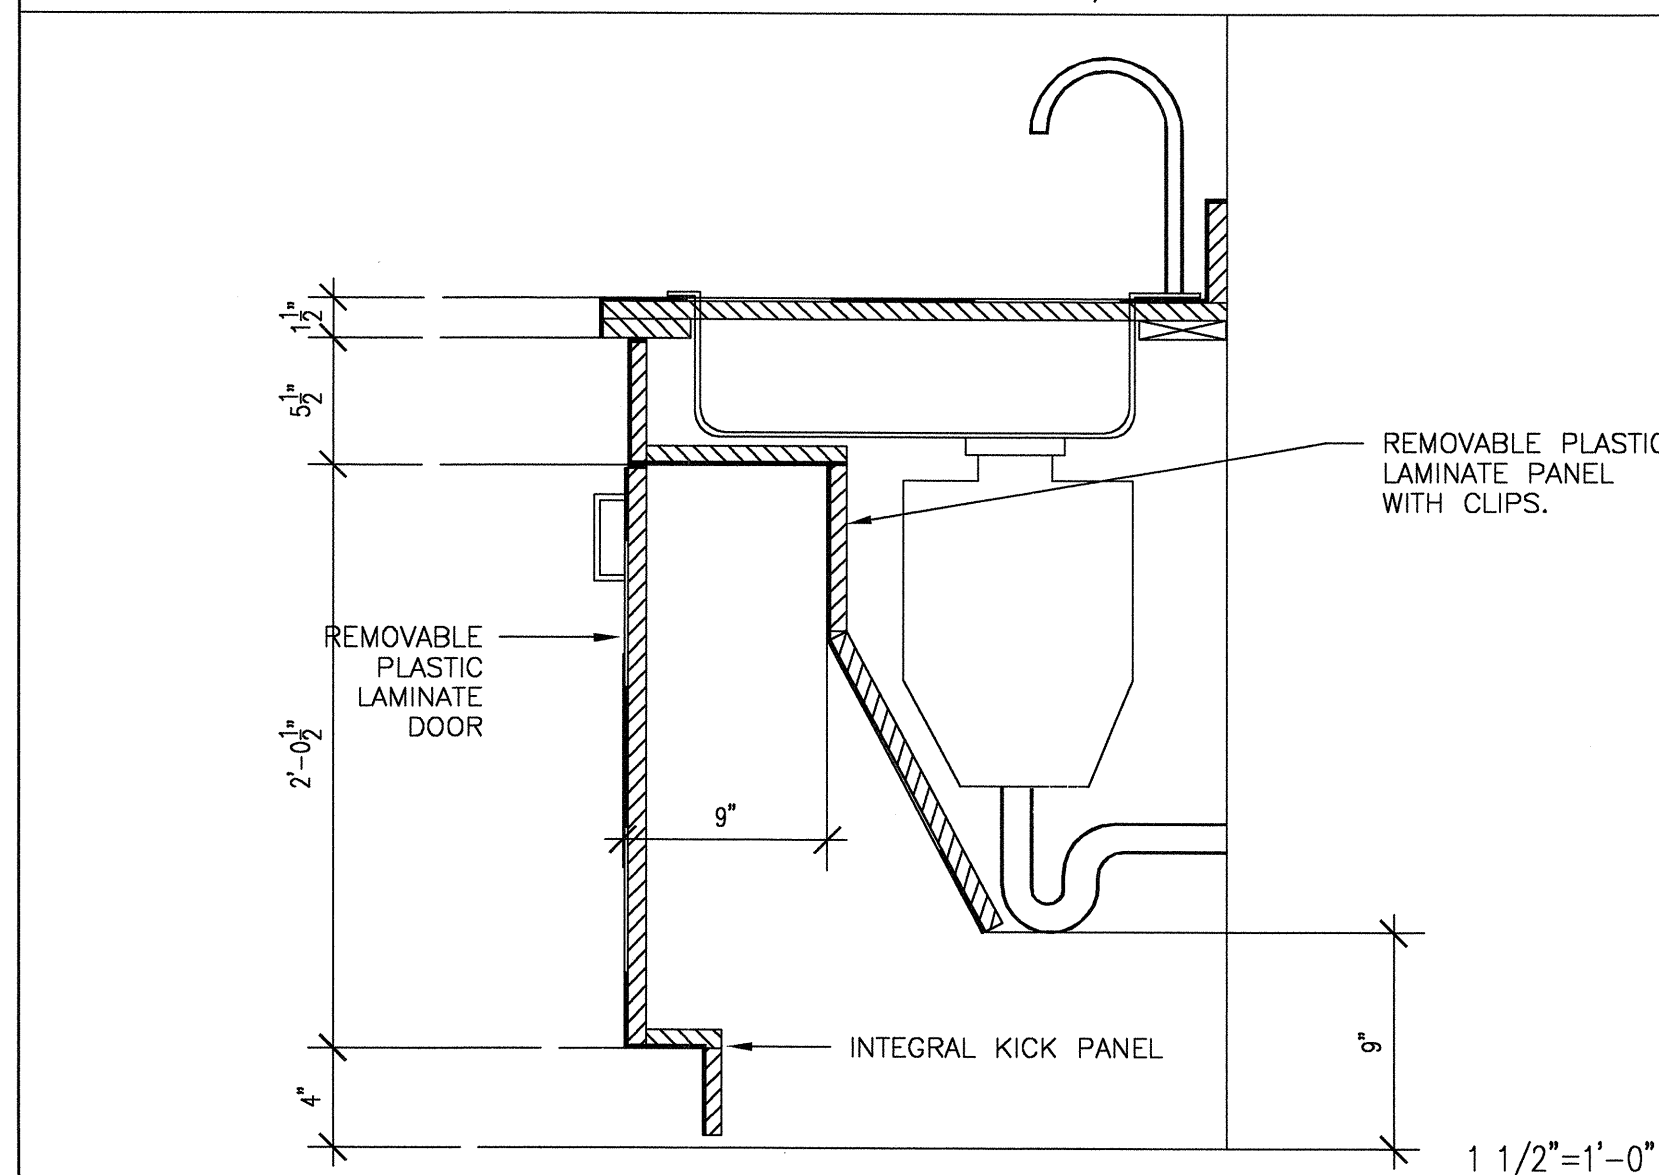
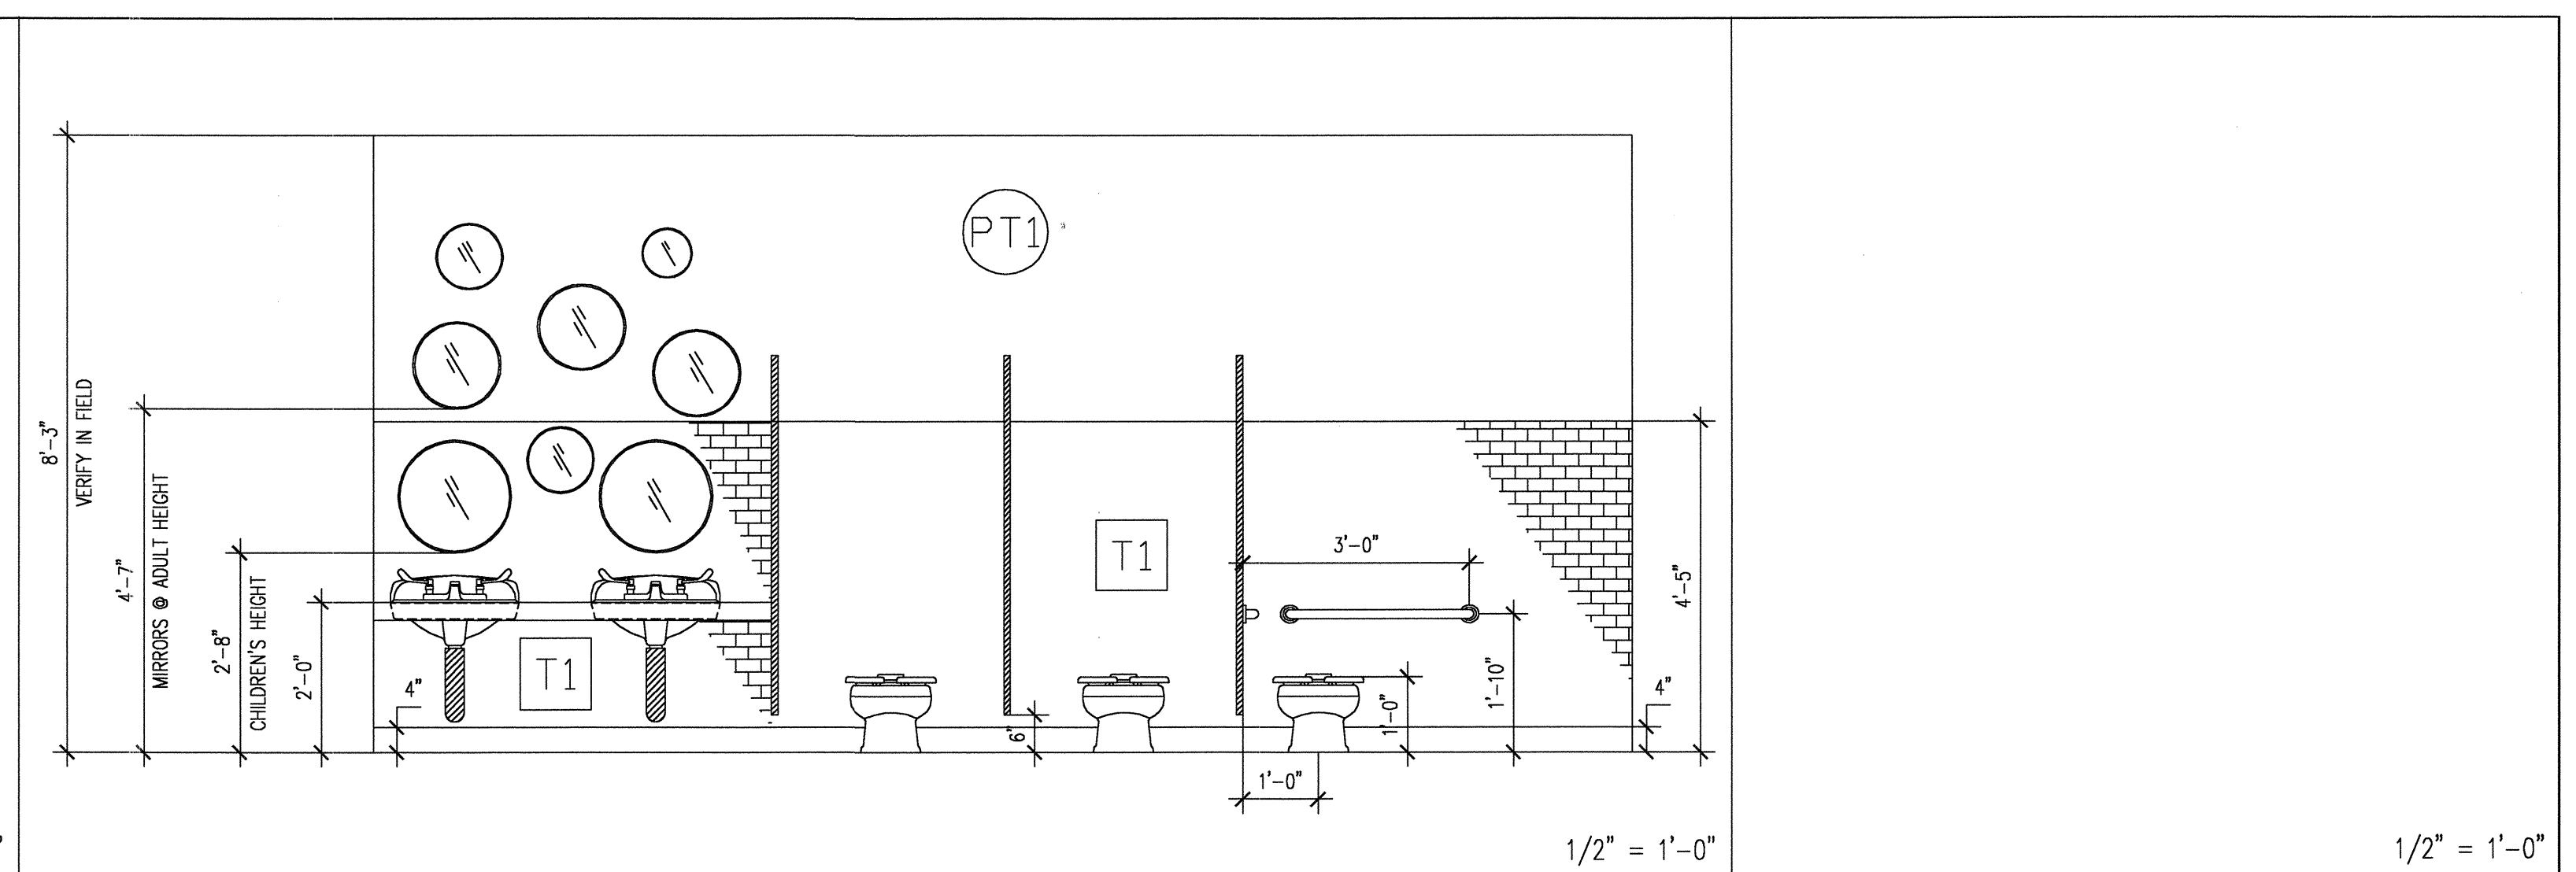
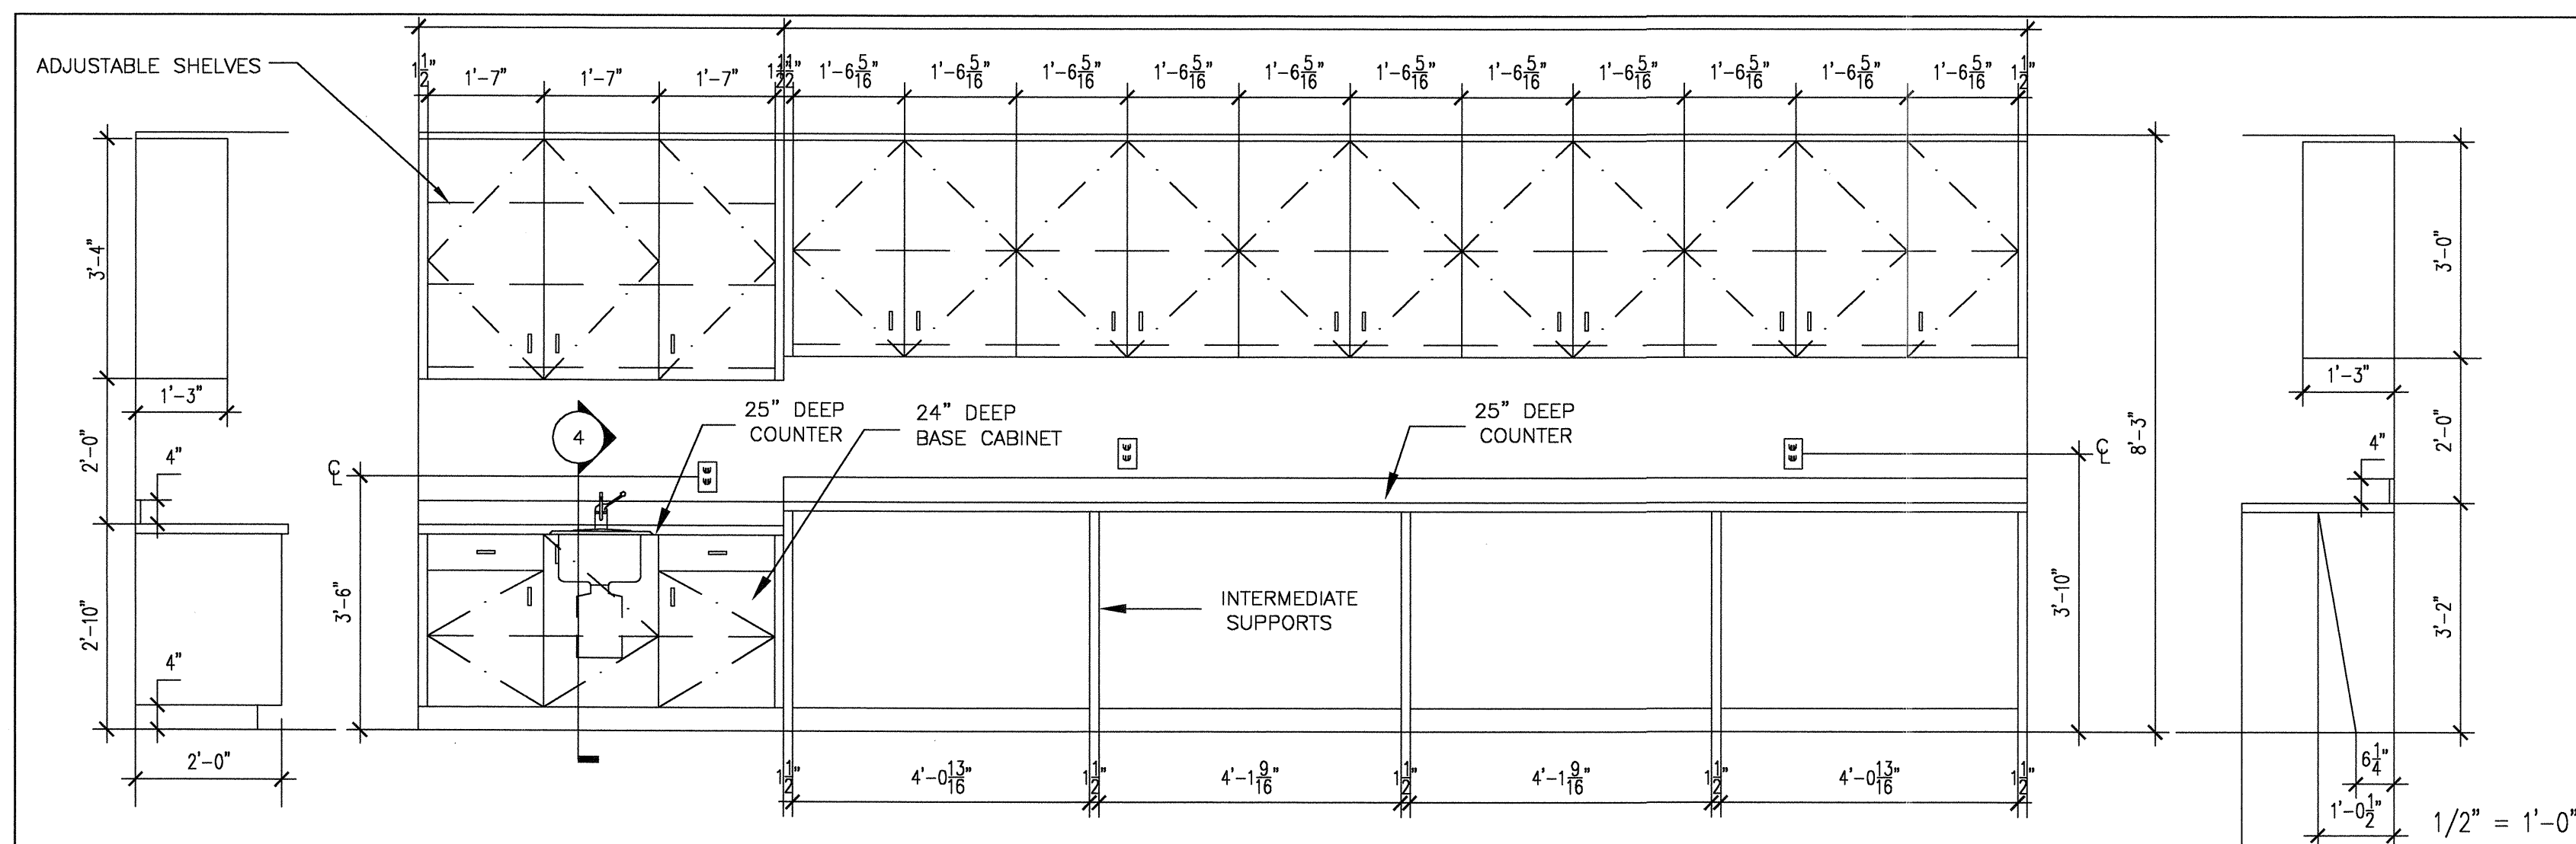
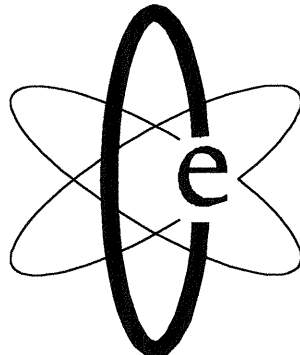


A	ISSUED FOR PRICING	10.16.03
REVISION #	SUBMISSION	DATE
ST. EDMUNDS CHURCH NURSERY SCHOOL 2975 HUNTINGTON DR. SAN MARINO, CA		
 Creative Energy architecture and interiors 61 East Colorado Boulevard Suite 200 Pasadena California 91105 phone 626.304.0505 fax 626.304.0715		
DRAWING TITLE	ELEVATIONS, SECTIONS AND DETAILS	
SEAL	DATE 9.23.03	PROJECT NO. 03-118
	SCALE 1/8" = 1'-0"	
	DRAWING NUMBER	REVISION
	A-5 A	