


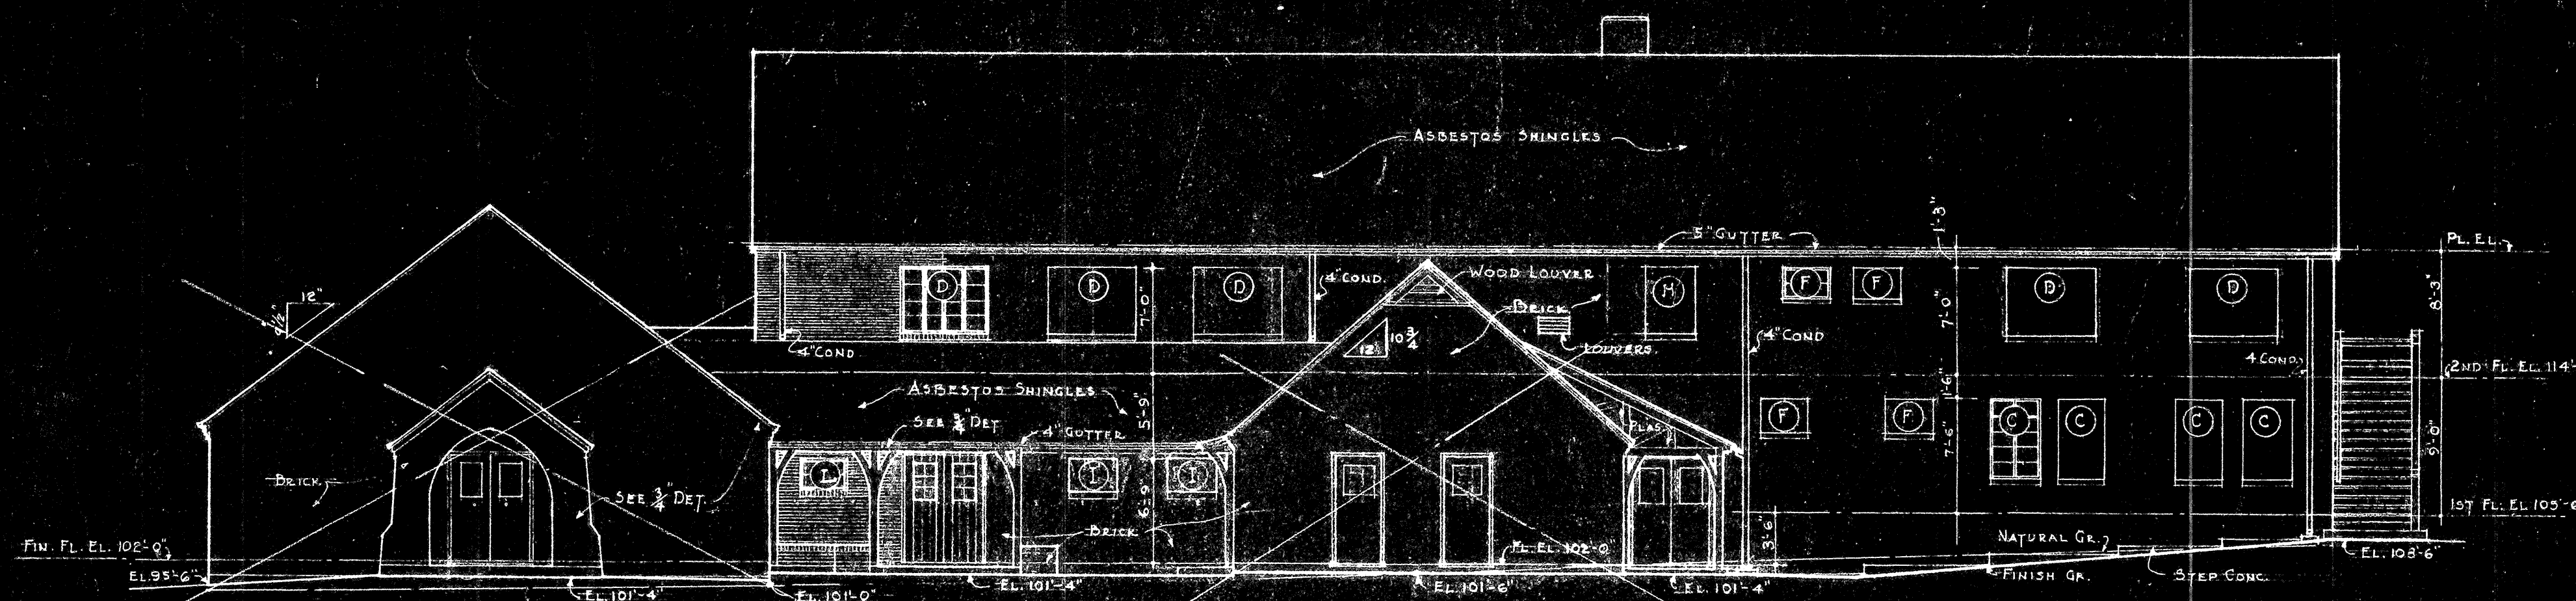


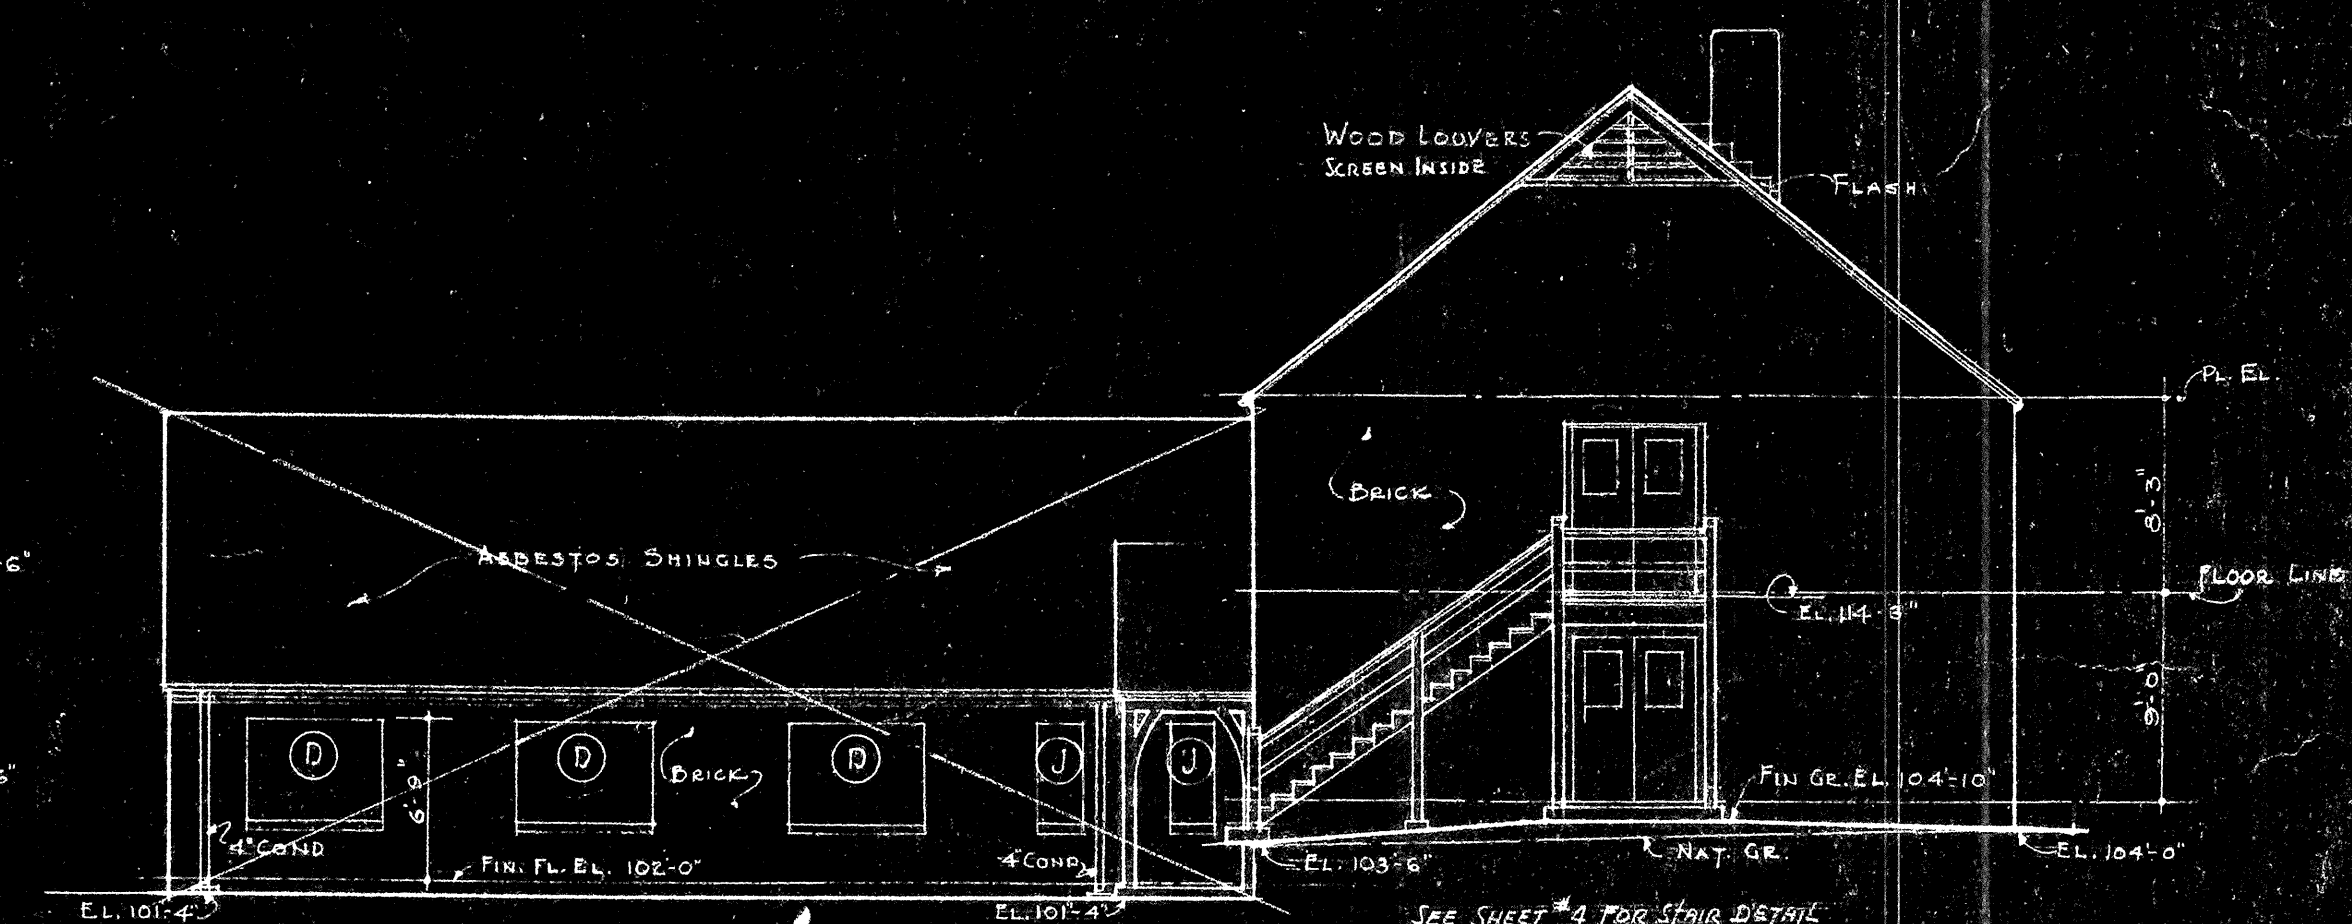


• EAST ELEVATION •
SCALE 1/8"=1'-0"

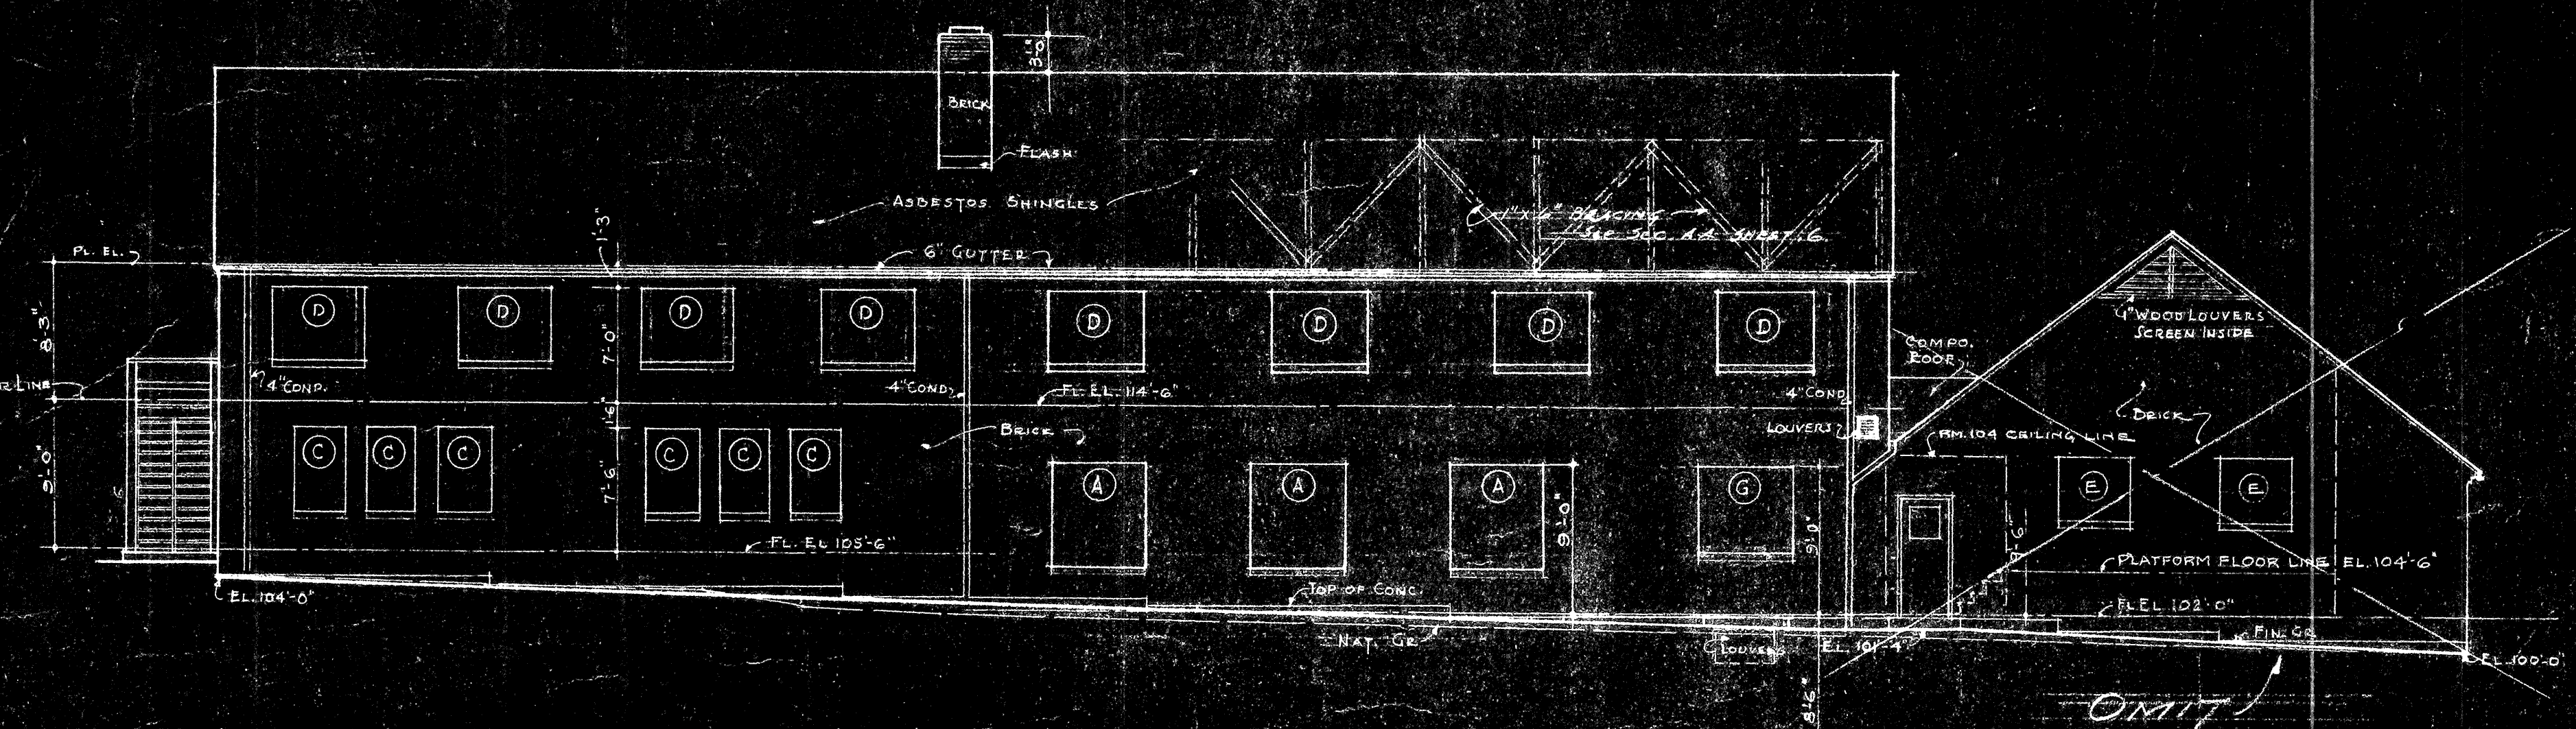


• NORTH ELEVATION •
SCALE 1/8"=1'-0"

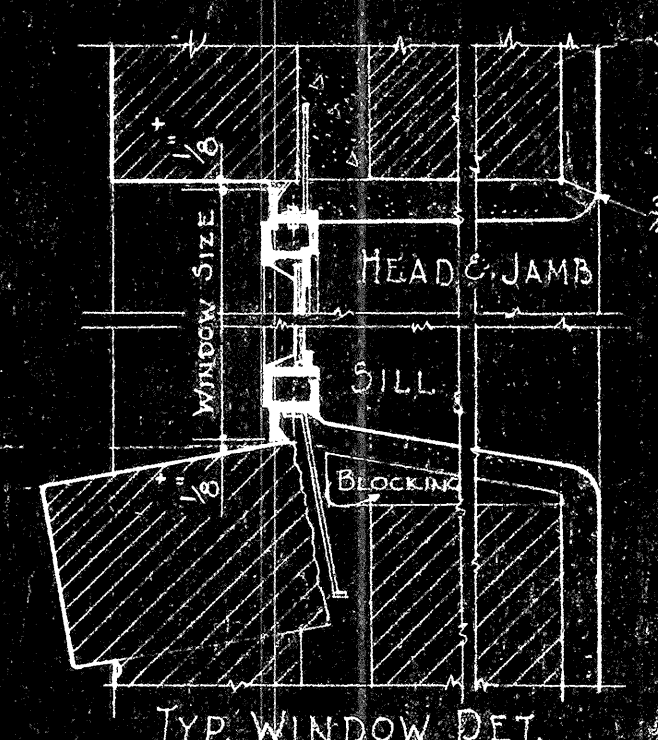


• WEST ELEVATION •
SCALE 1/8"=1'-0"

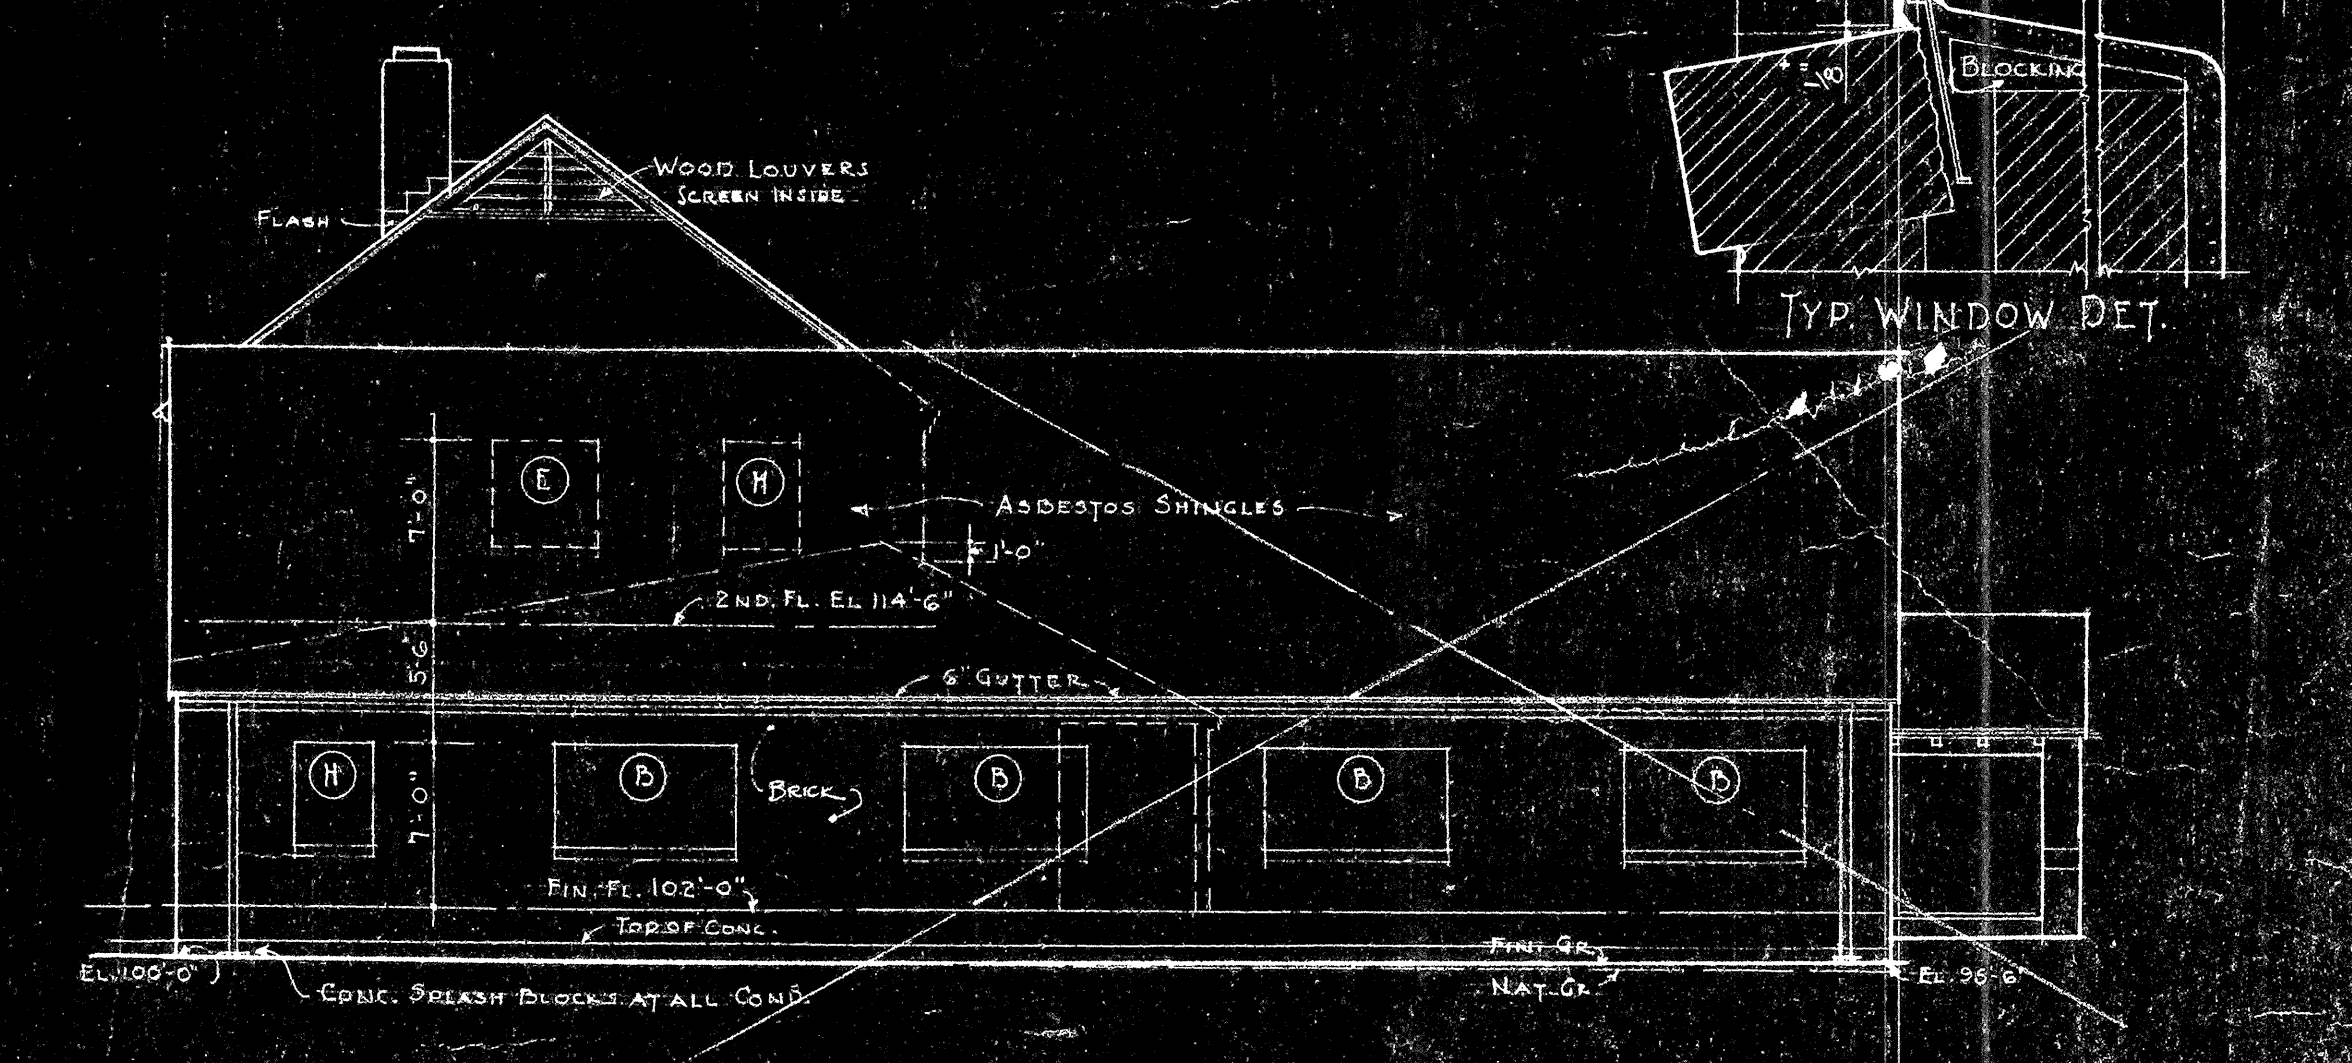


• SOUTH ELEVATION •
SCALE 1/8"=1'-0"

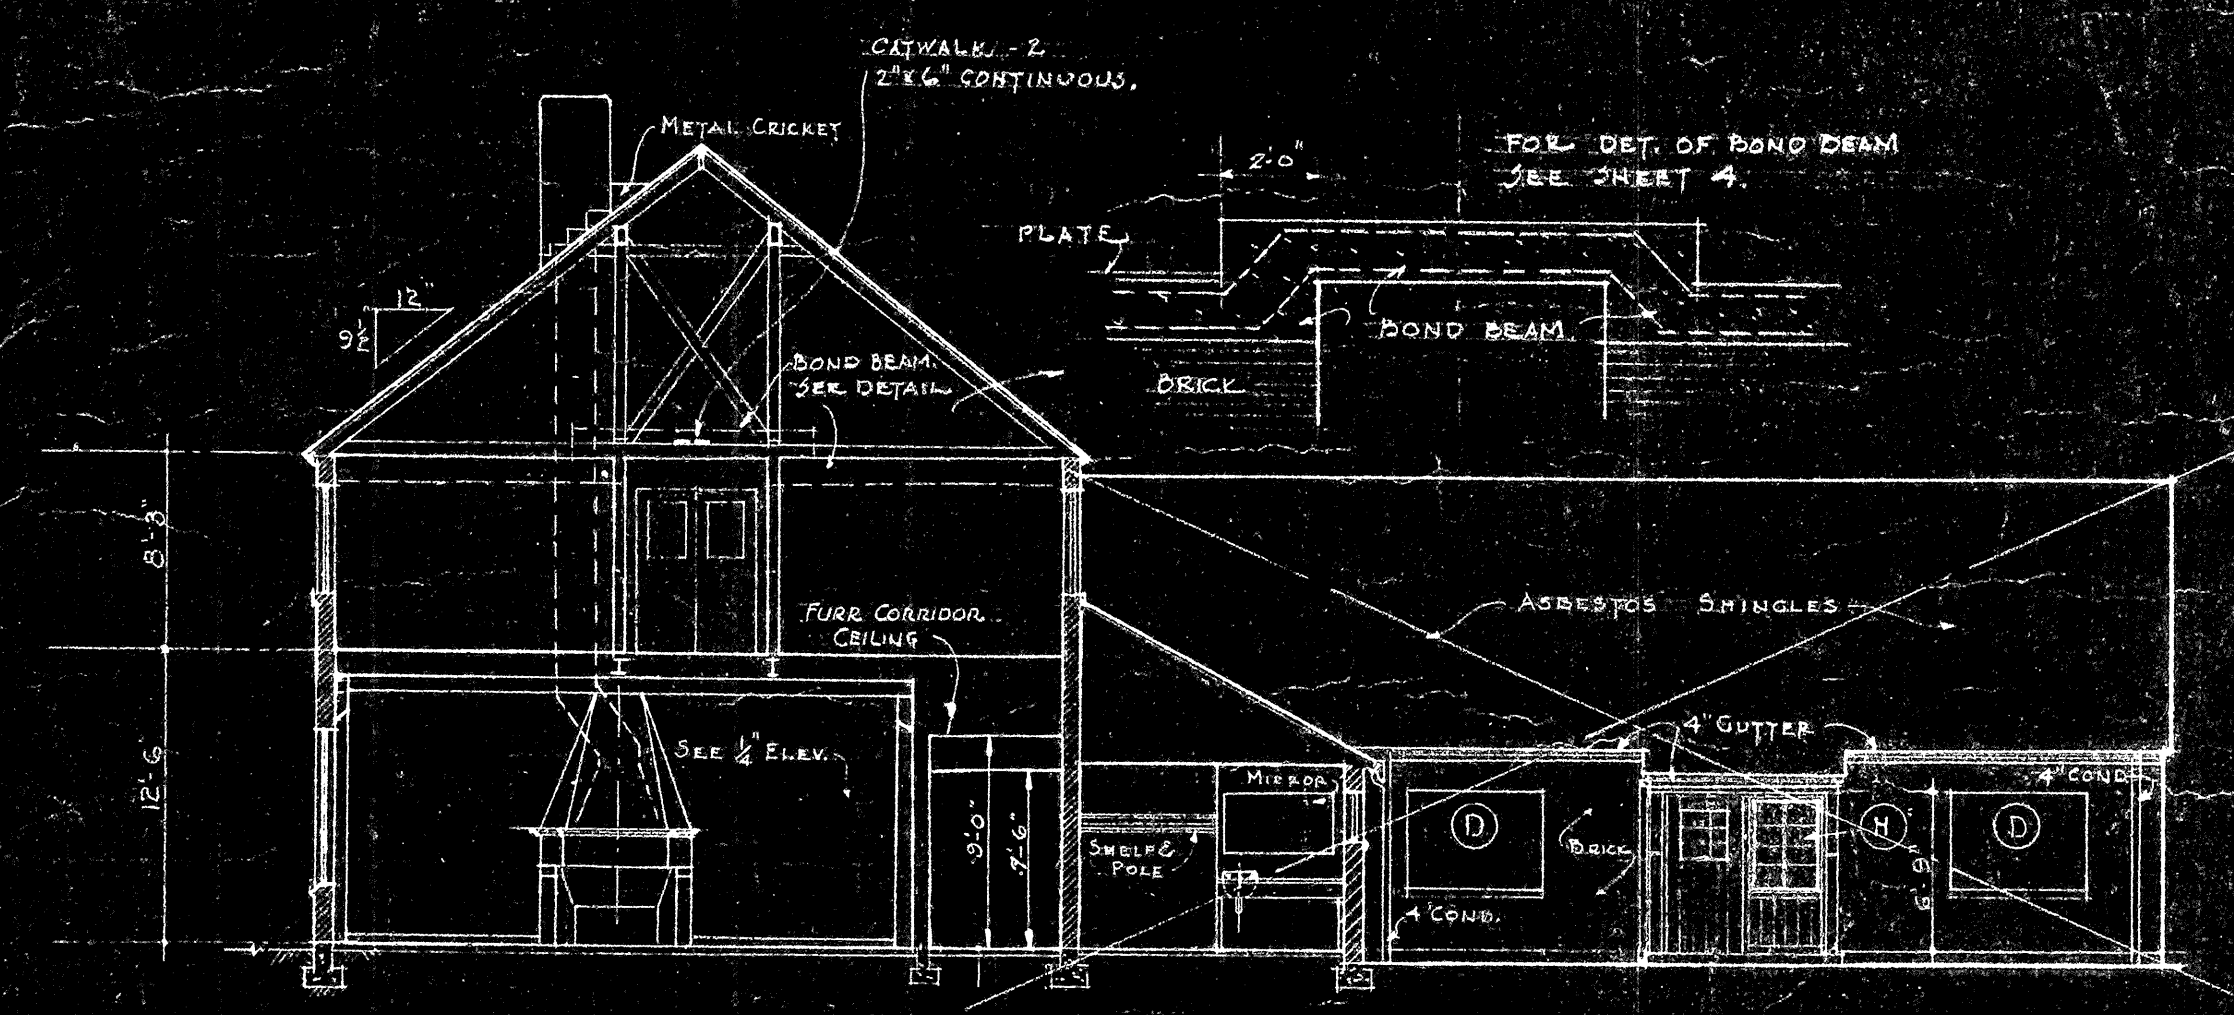

• SECTION B-B •
SECTION 1/8"=1'-0"

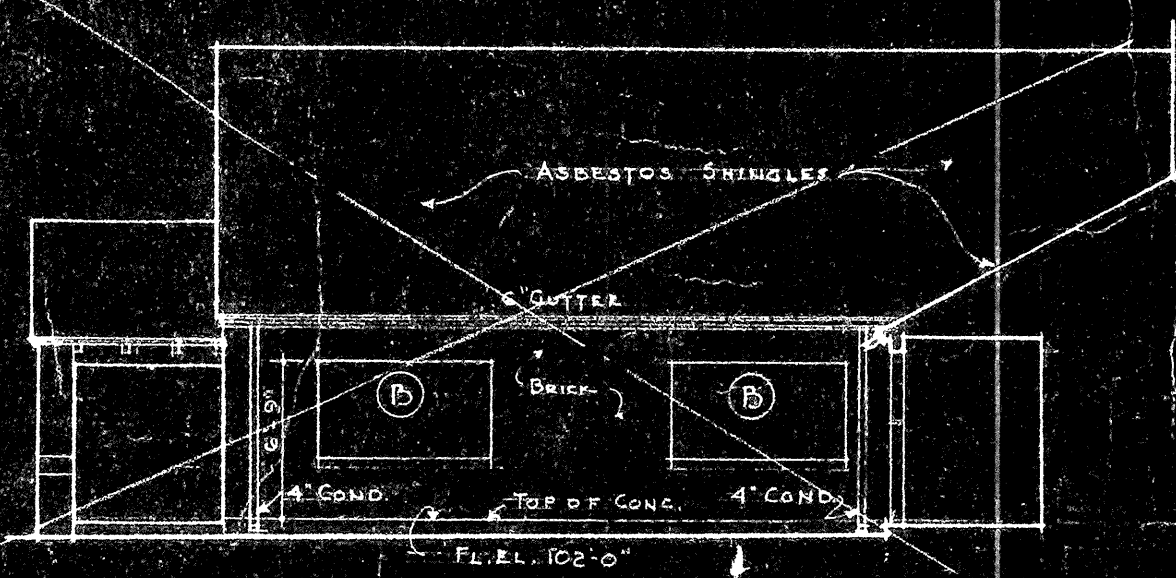

• NORTH ELEVATION OF PARISH HALL •
SECTION 1/8"=1'-0"

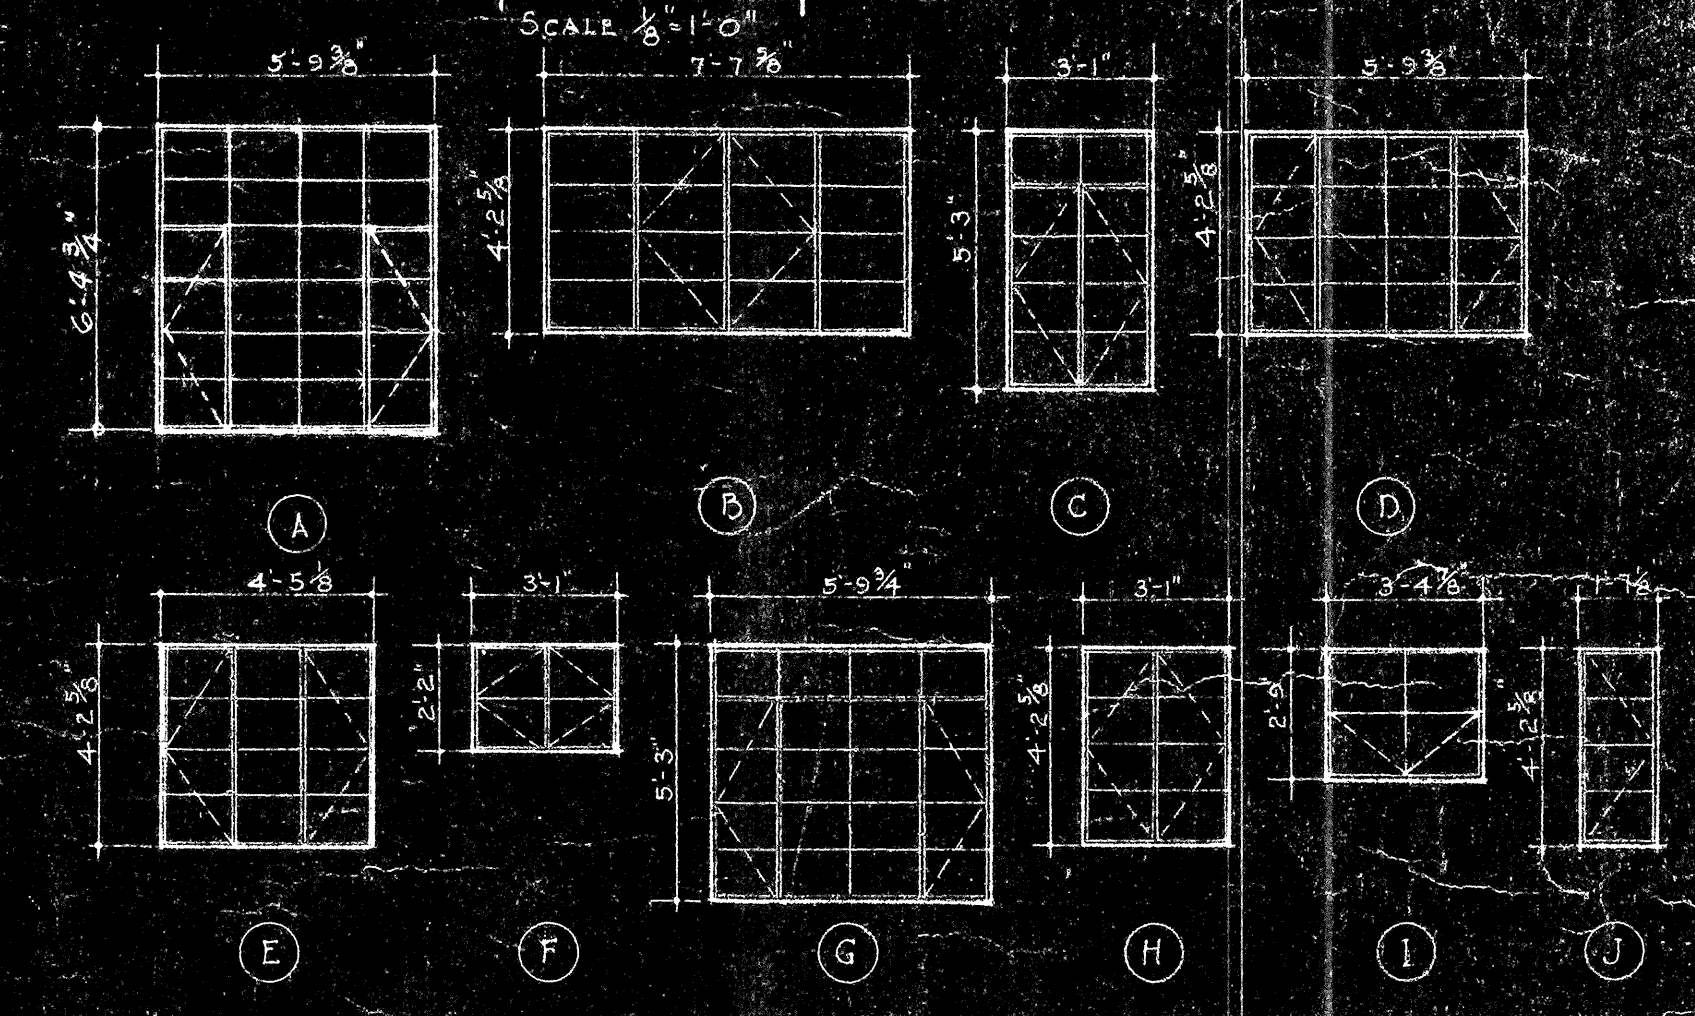

• WINDOW SCHEDULE •
REVISOR: J. VAN DER BEEK

DATE: 10-1-35		SHEET: 3	
PROJECT: 452		ARCHITECTS: QUINTIN & WESTBERG	
LOCATION: ALHAMBRA, CALIFORNIA		CLIENT: A PARISH HALL AND CHURCH SCHOOL FOR ST. EDMUNDS EPISCOPAL CHURCH - SAN MARINO	
CONTRACTOR TO VERIFY ALL DIMENSIONS AT BUILDING			