




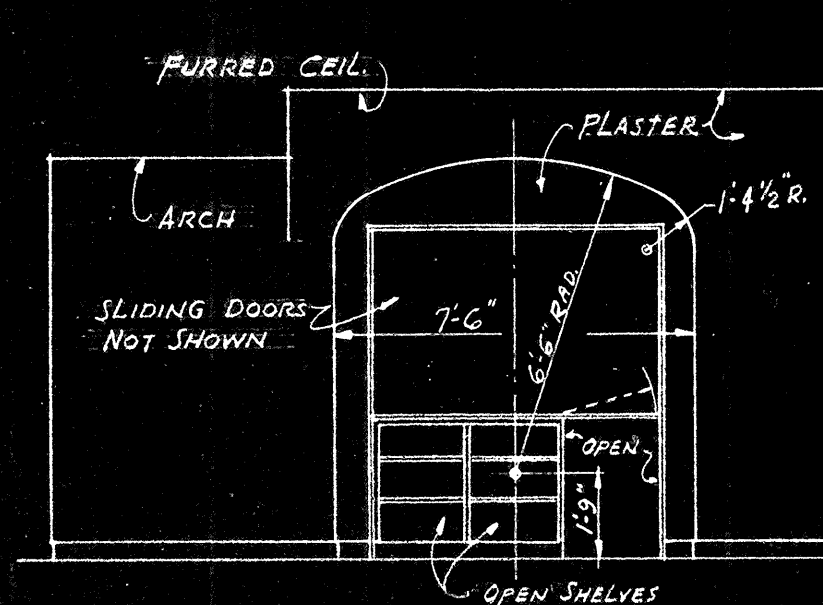


ELEVATION - WEST WALL OF HALL
SCALE 1/4" = 1'-0"

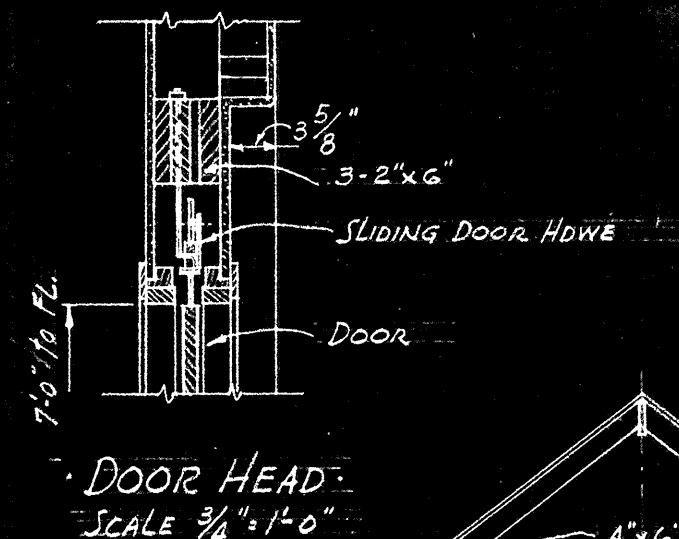


DOOR HEAD
SCALE 3/4" = 1'-0"

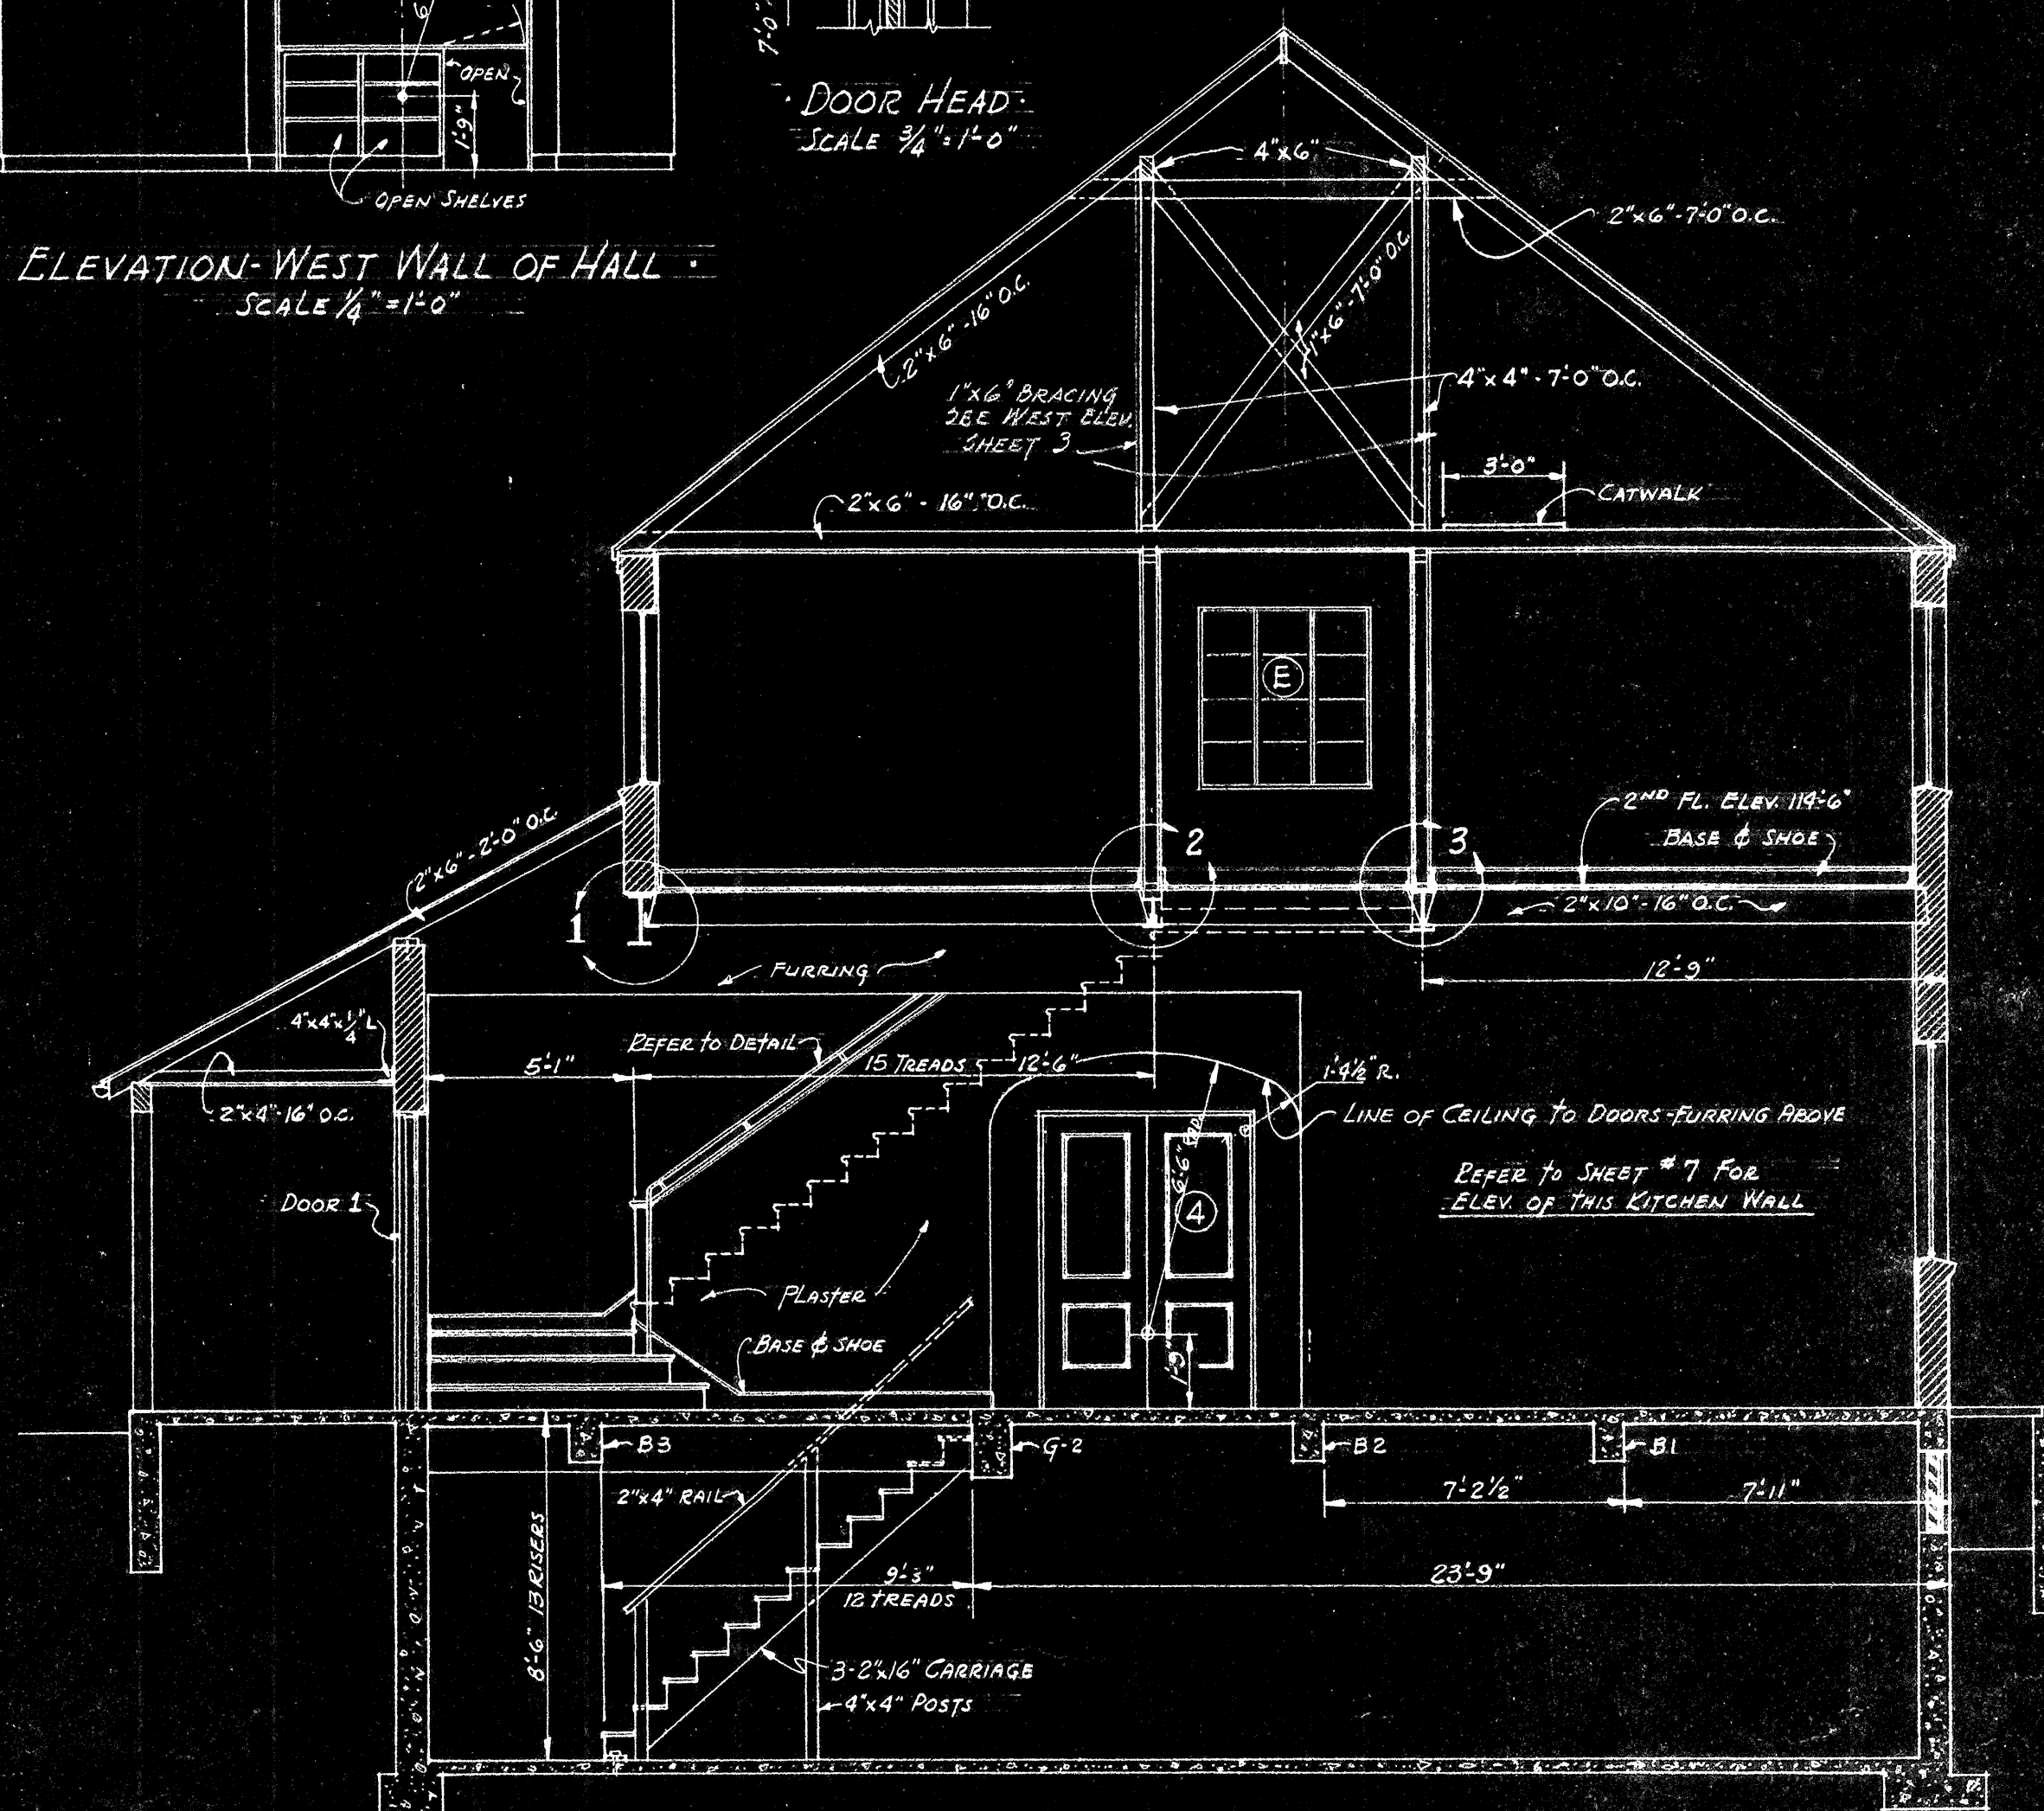


SECTION A-A
SCALE 1/4" = 1'-0"

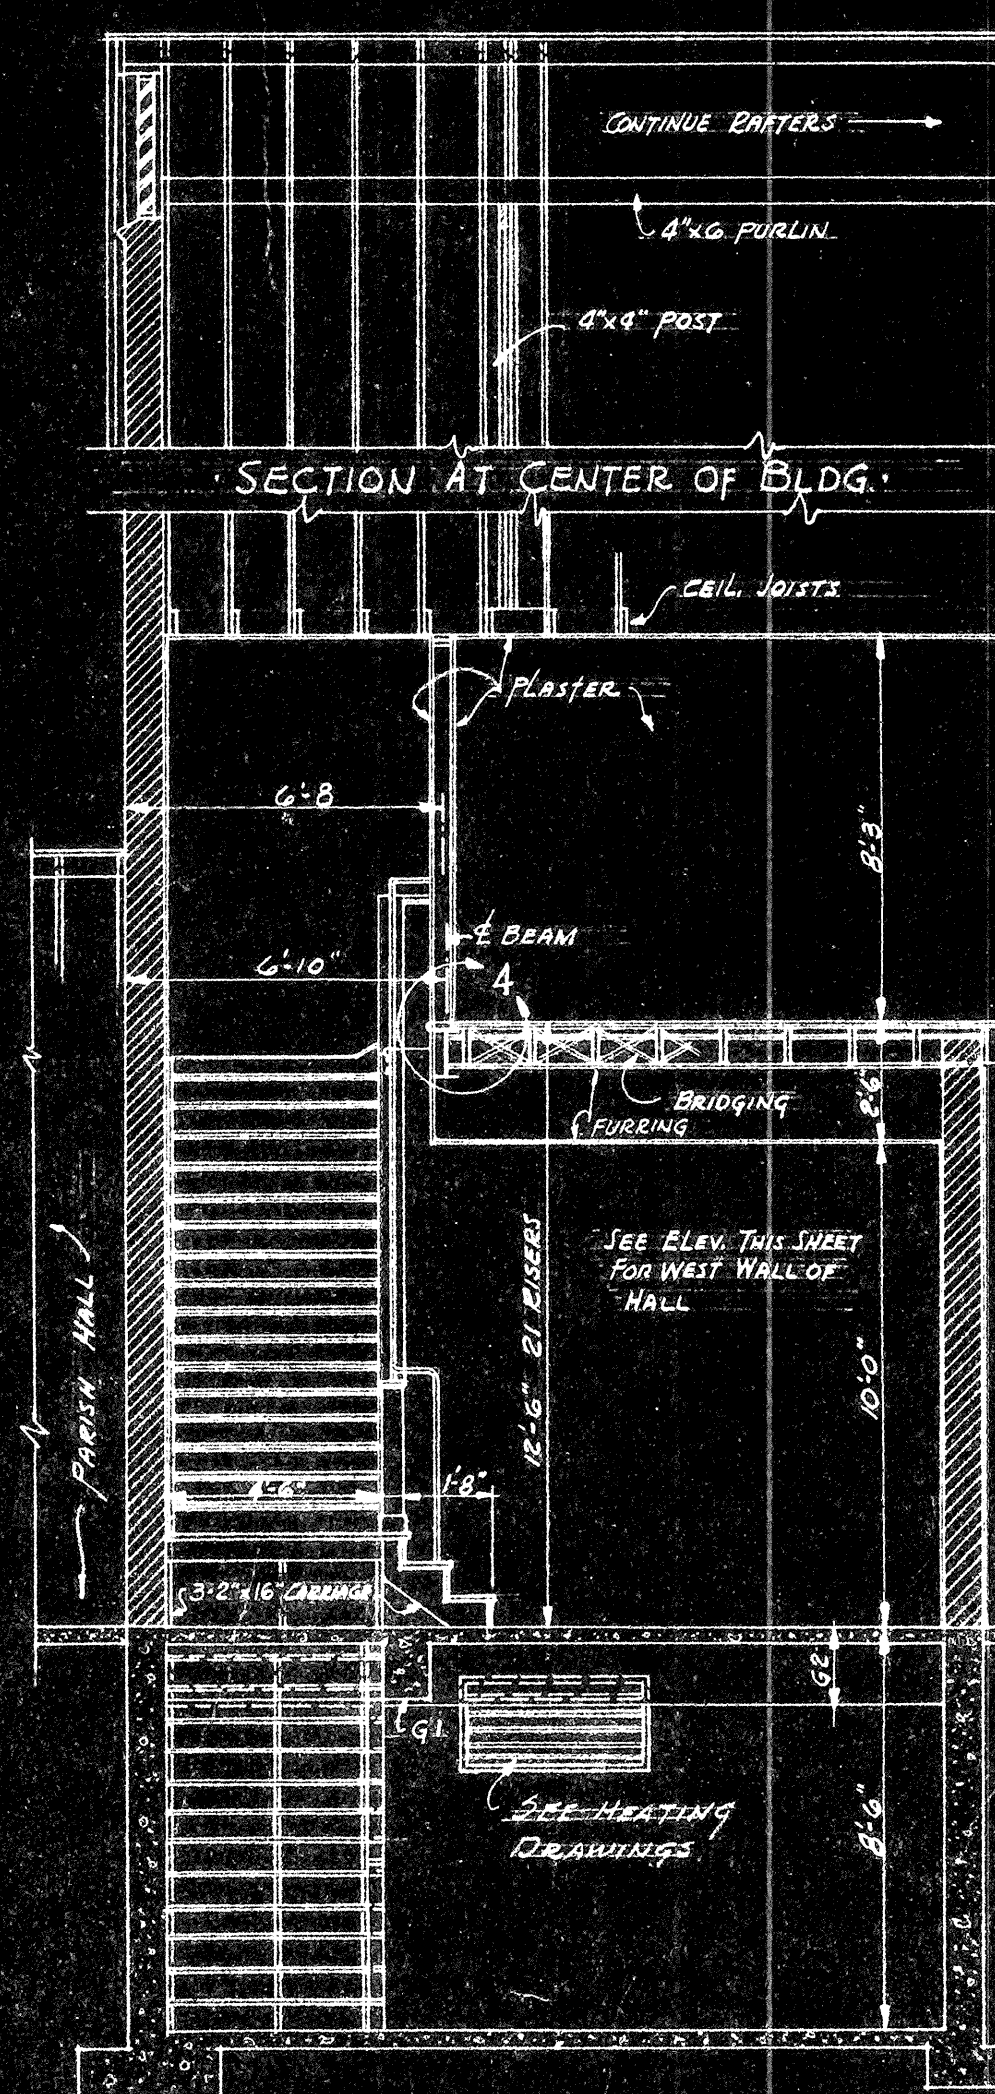


SECTION C-C
SCALE 1/4" = 1'-0"

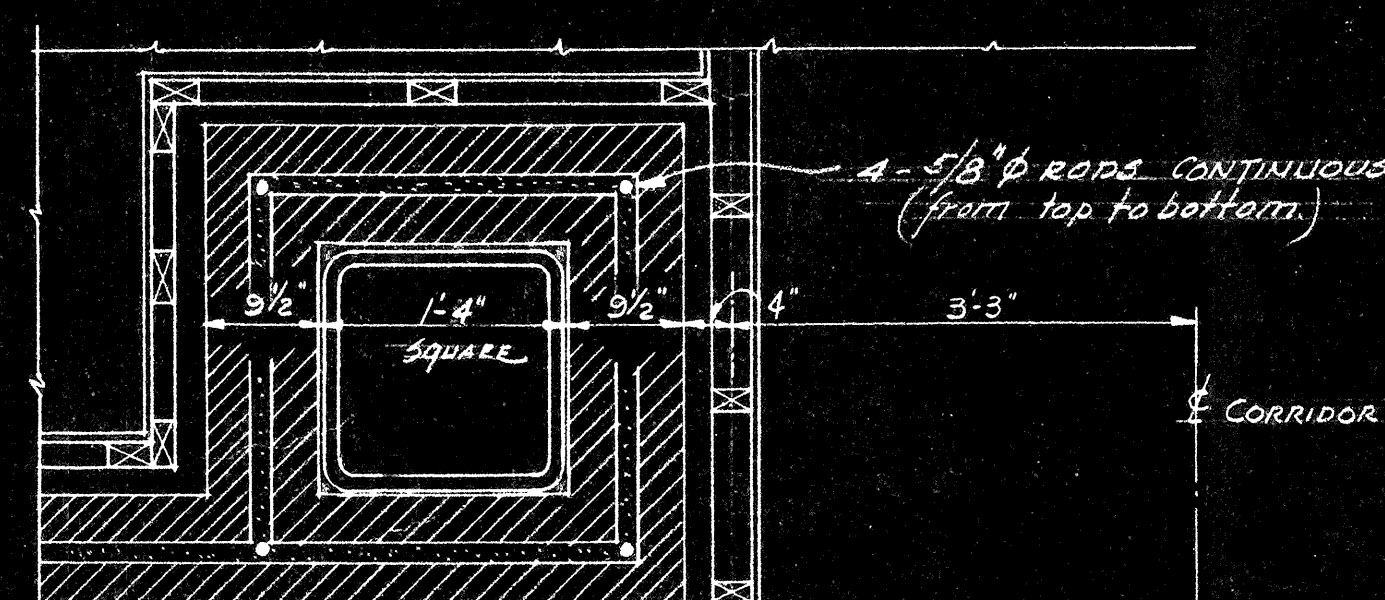


PLAN SECTION OF CHIMNEY

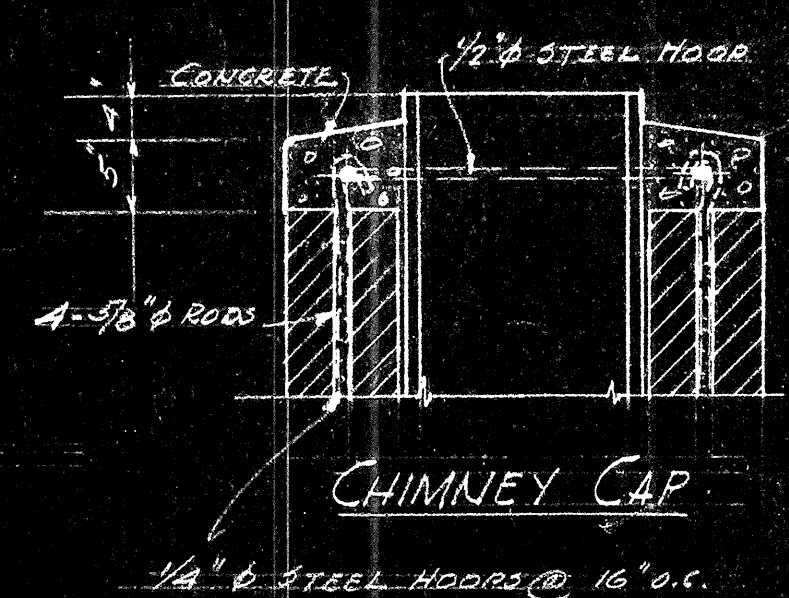


CHIMNEY CAP
SCALE 1/4" = 1'-0"

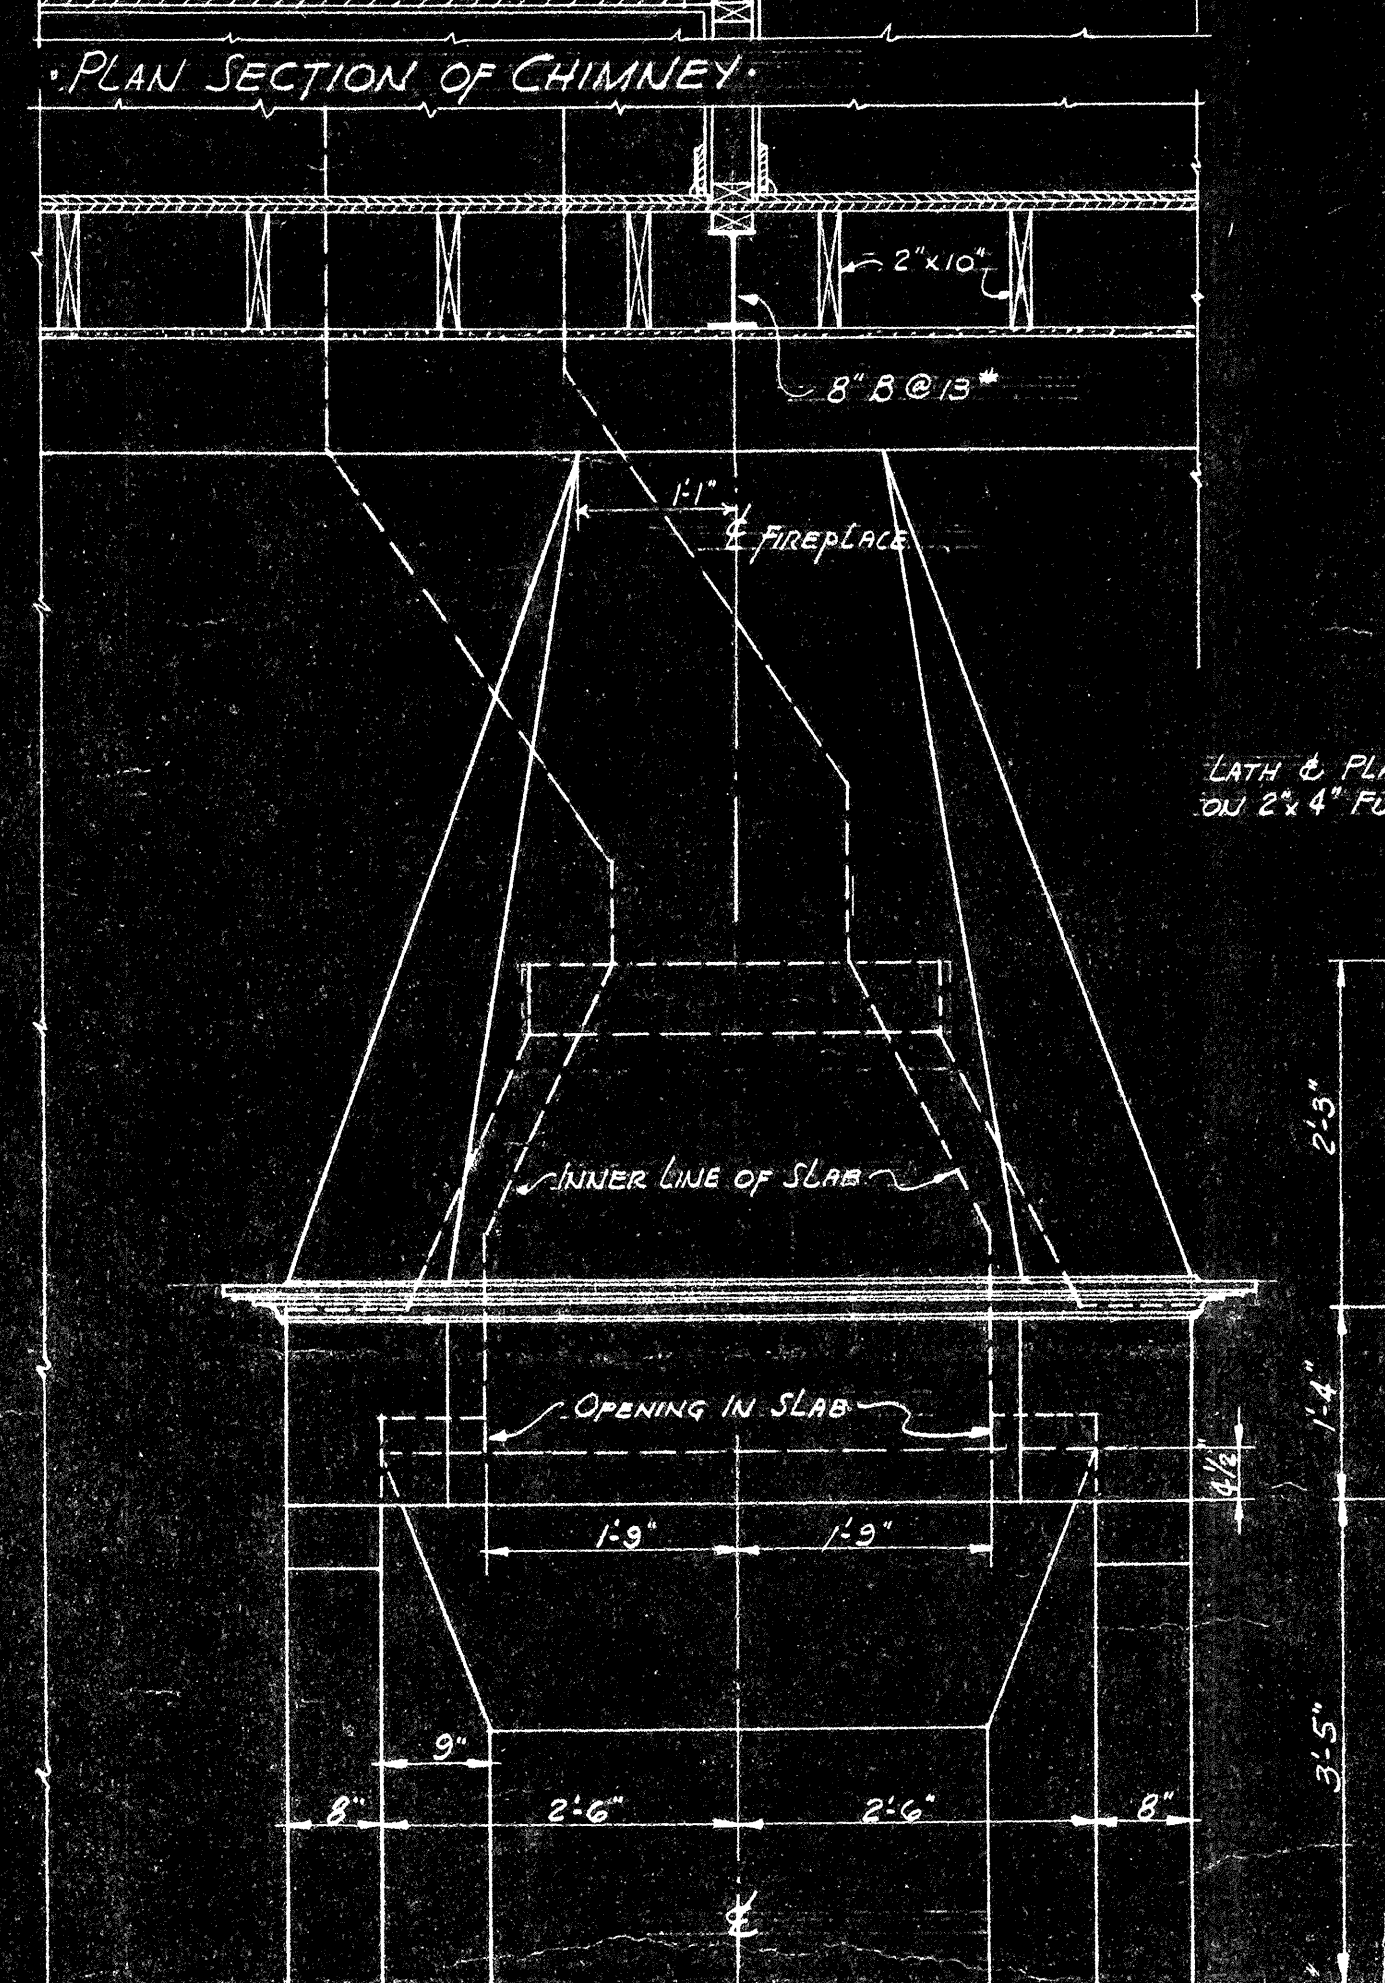


ELEVATION

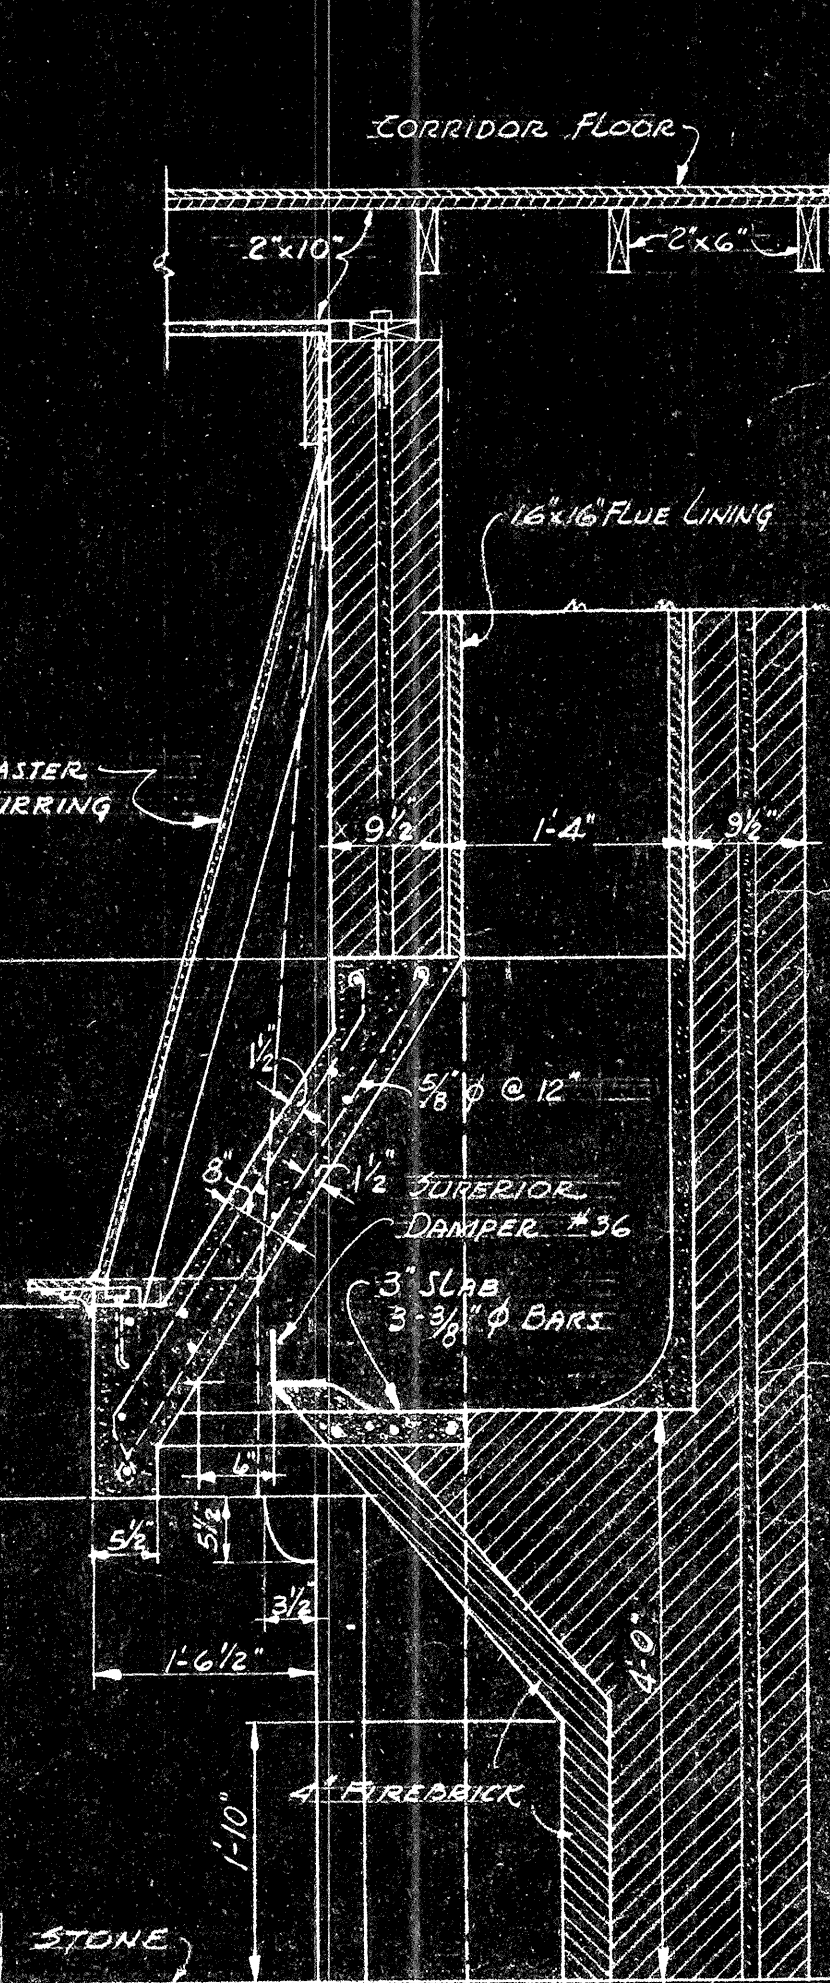


SECTION

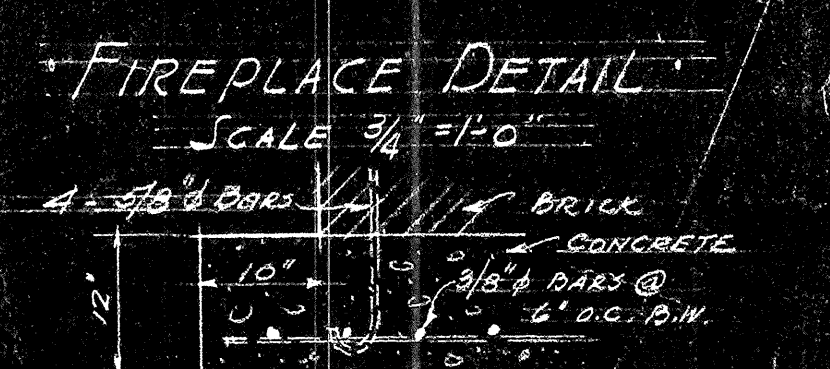

FIREPLACE DETAIL
SCALE 3/4" = 1'-0"

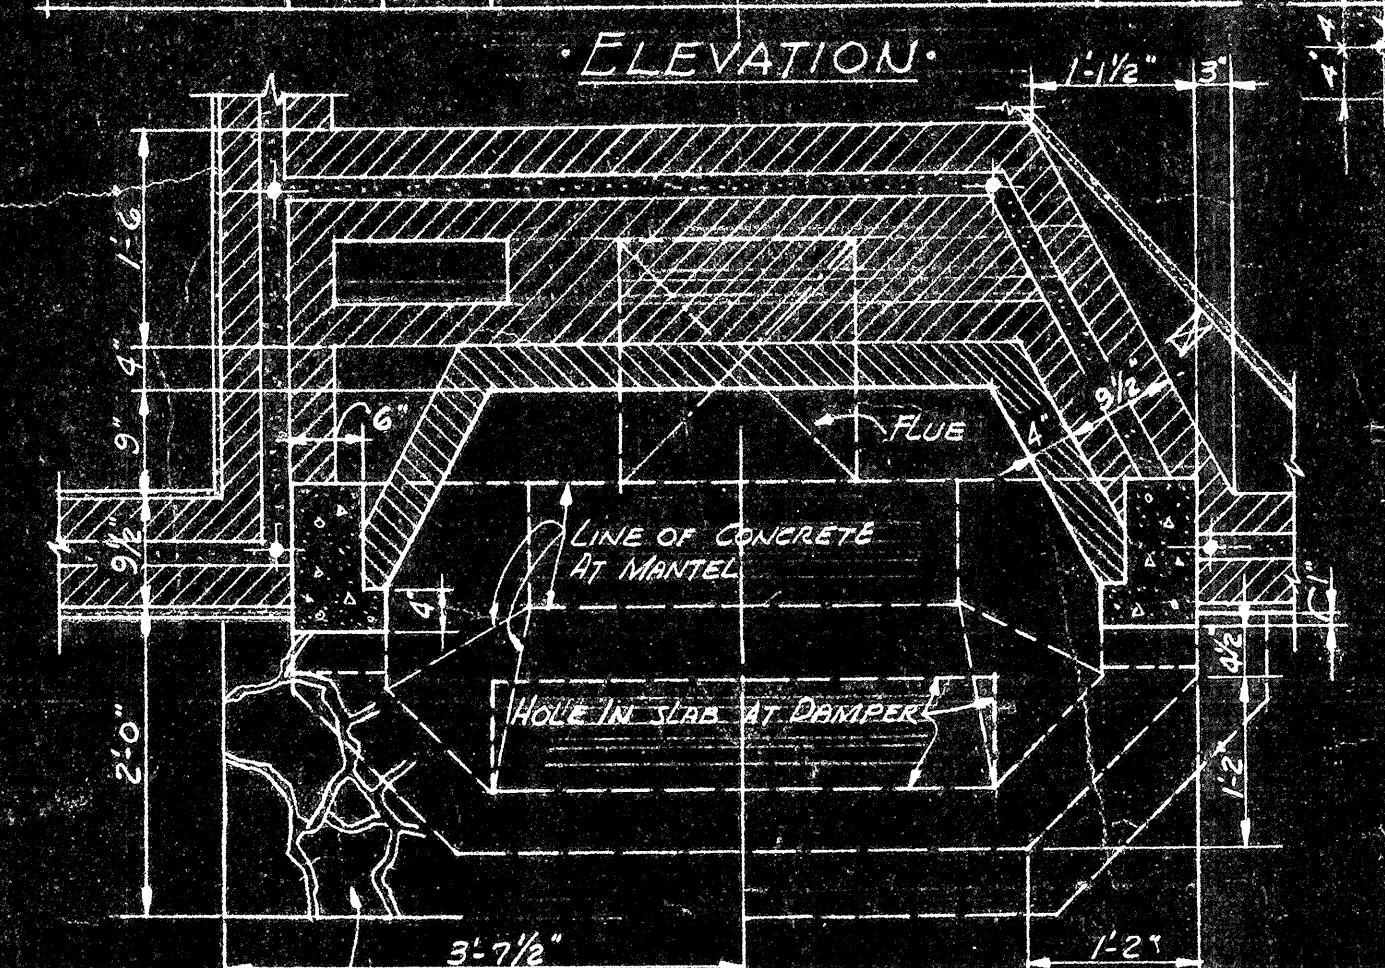


PLAN

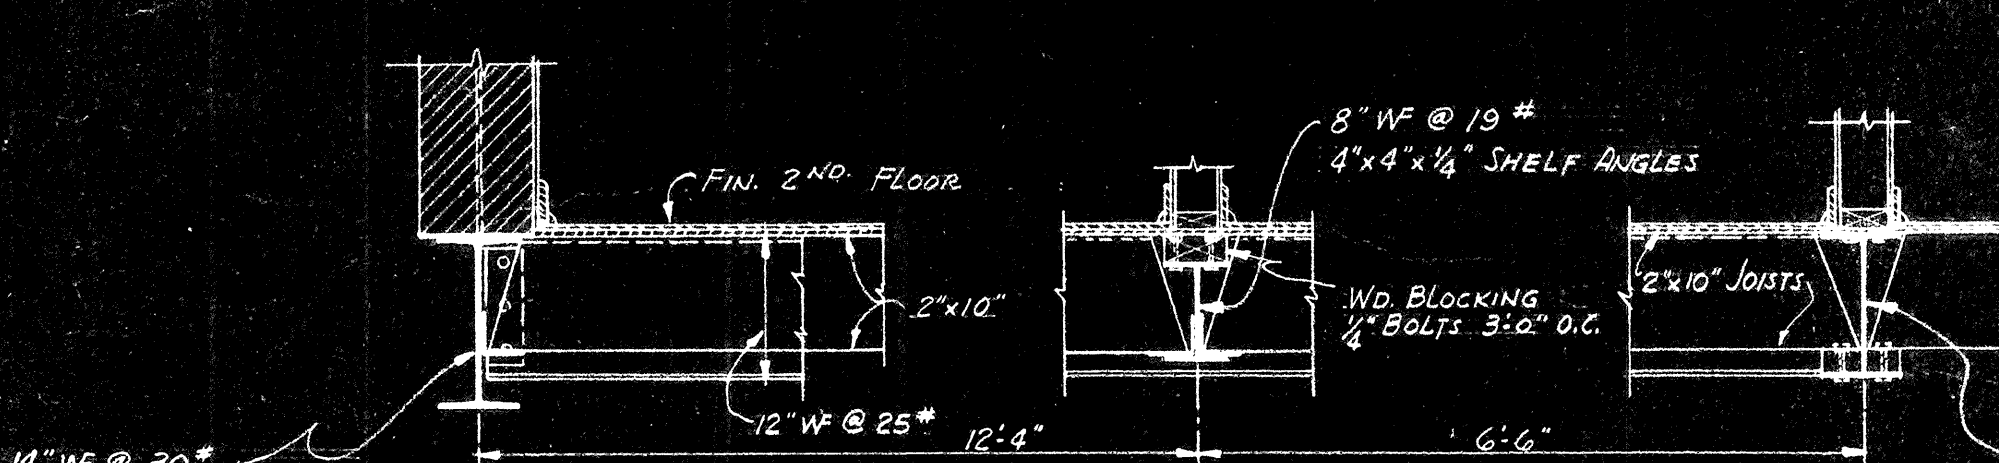


DETAIL 1

DETAIL 2
SCALE 3/4" = 1'-0"


DETAIL 3

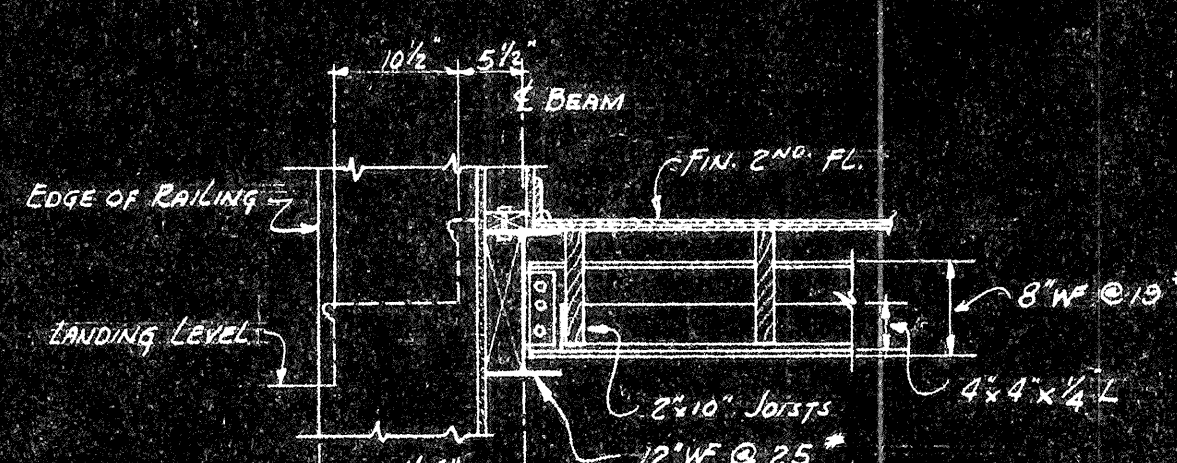

DETAIL 4
SCALE 3/4" = 1'-0"

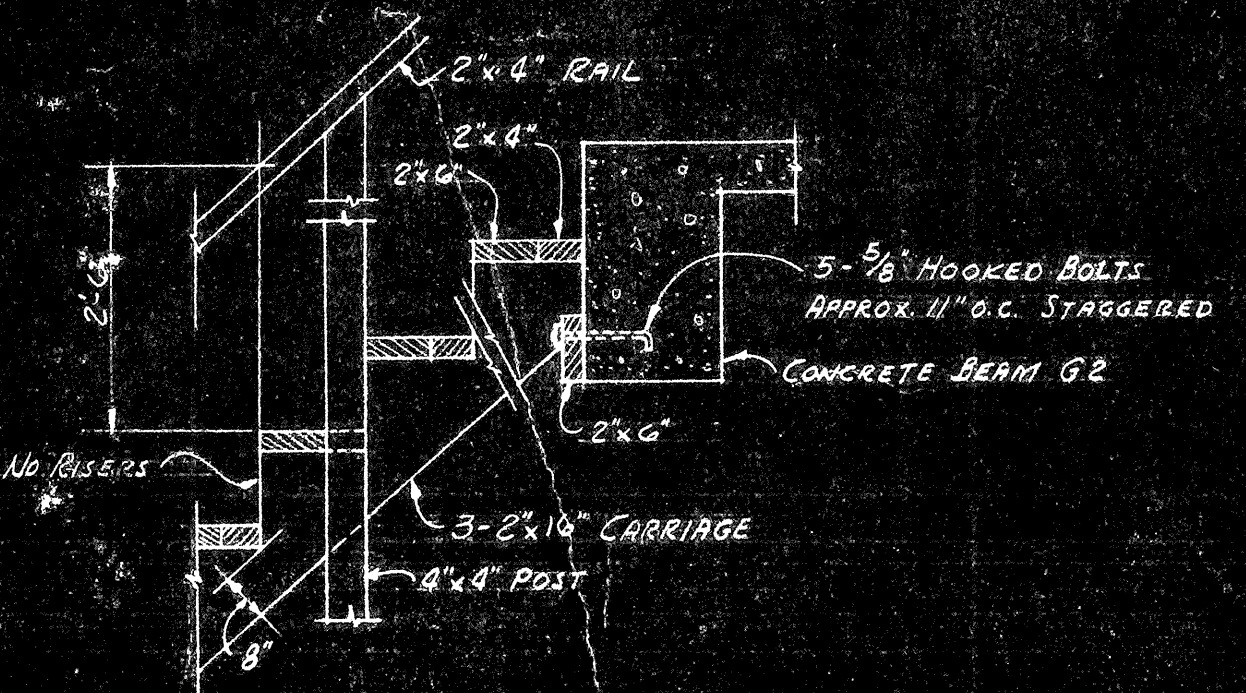

DETAIL OF BASEMENT STAIRWAY
SCALE 3/4" = 1'-0"

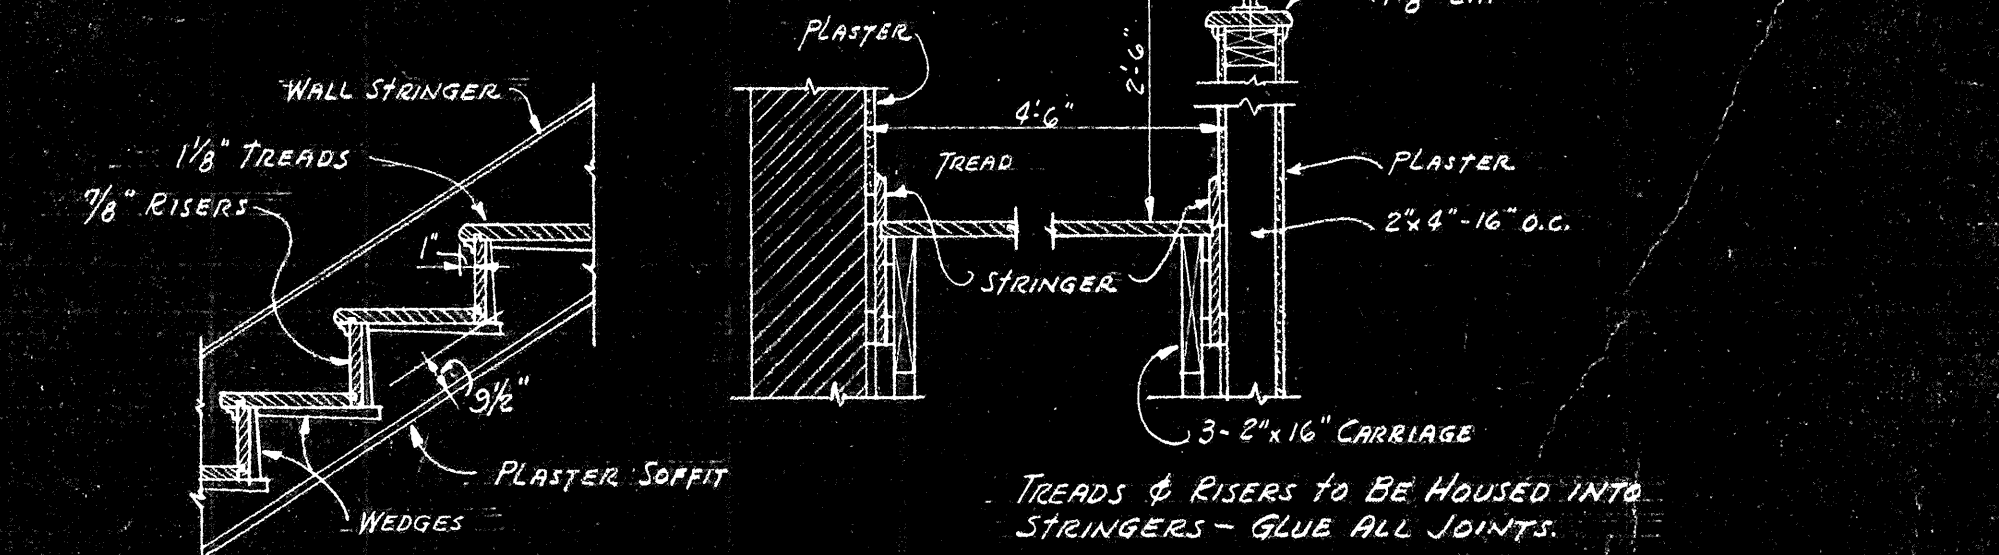

FIRST TO SECOND FL. STAIR DETAILS
SCALE 3/4" = 1'-0"

SECTIONS & DETAILS			
DATE	10-1-45	QUINTIN & WESTBERG	SHEET
BY	452	ARCHITECTS	6
FOR	ALHAMBRA, CALIFORNIA		
TITLE OF BLDG. A PARISH HALL AND CHURCH SCHOOL FOR ST. EDMUNDS EPISCOPAL CHURCH - SAN MARINO			
CONTRACTOR CONCEPT ALL DIMENSIONS IN BUILDING			