

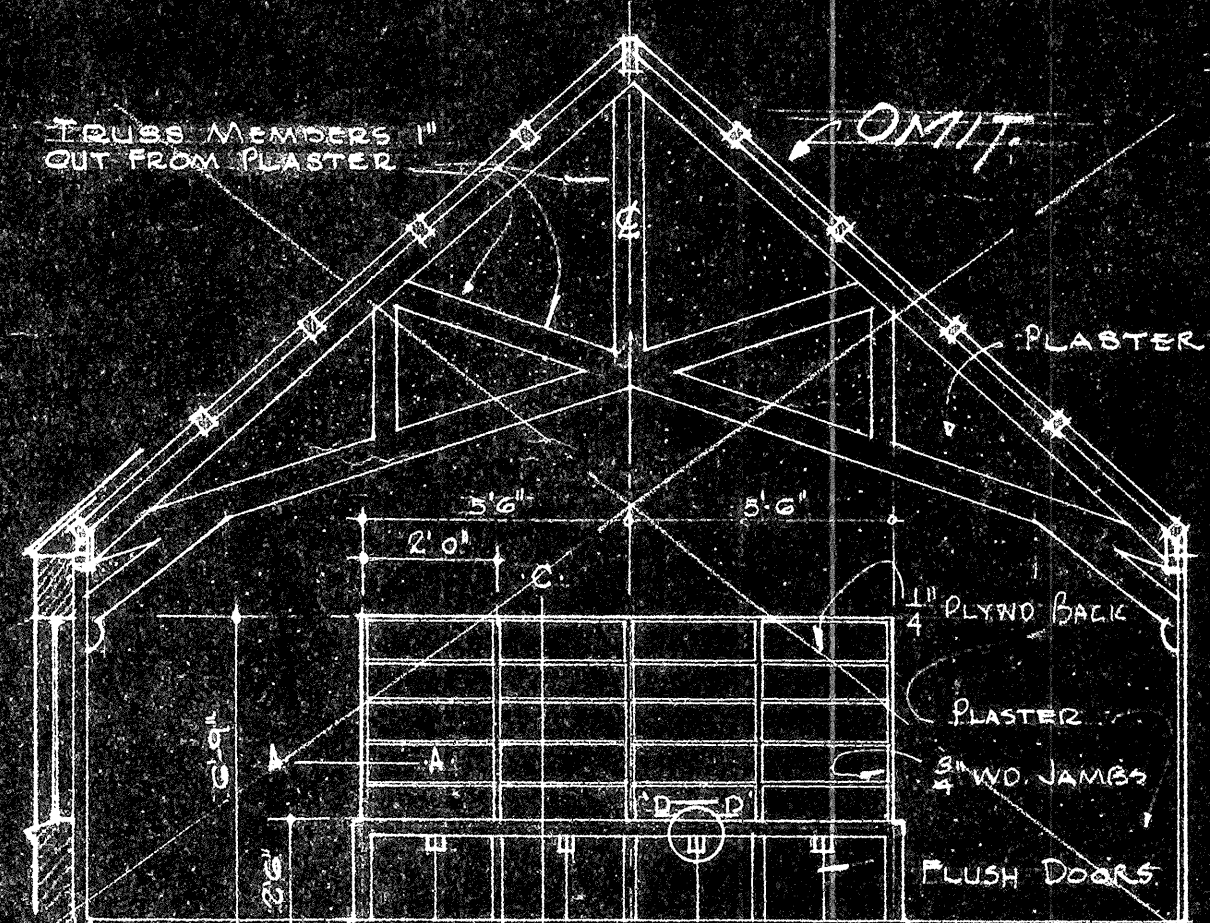
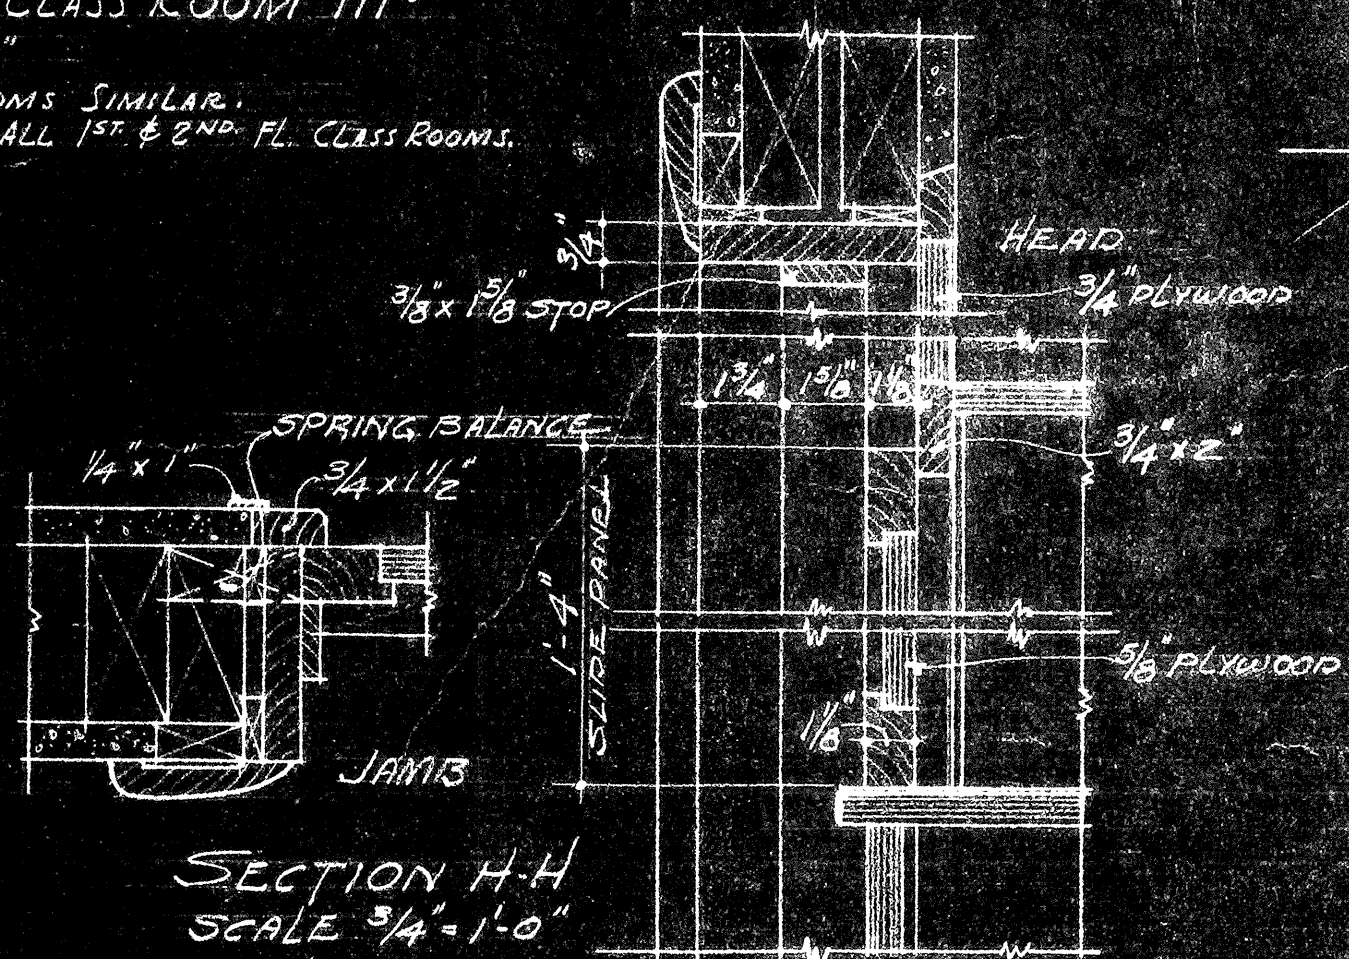
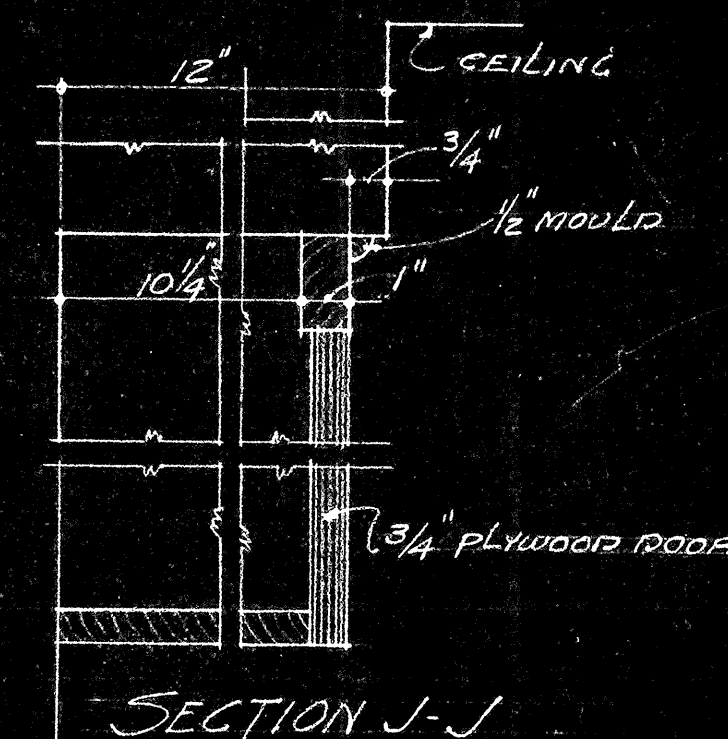
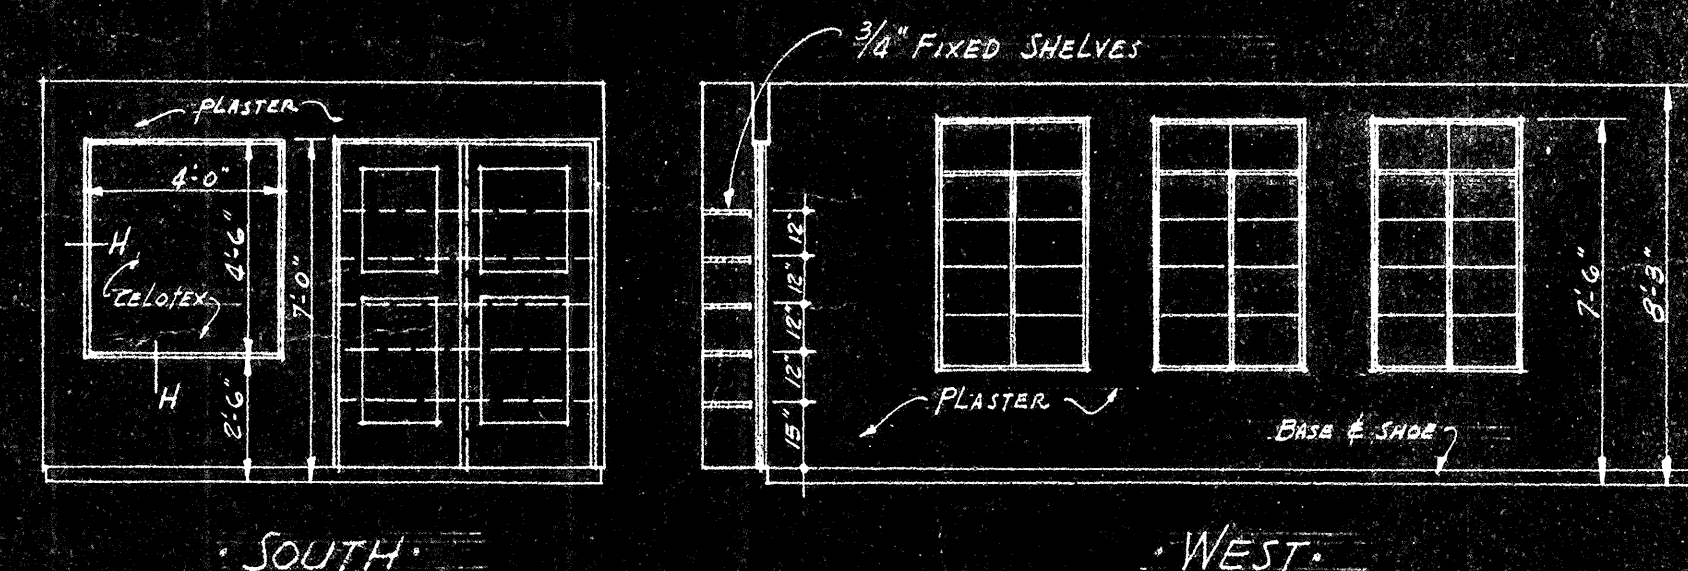
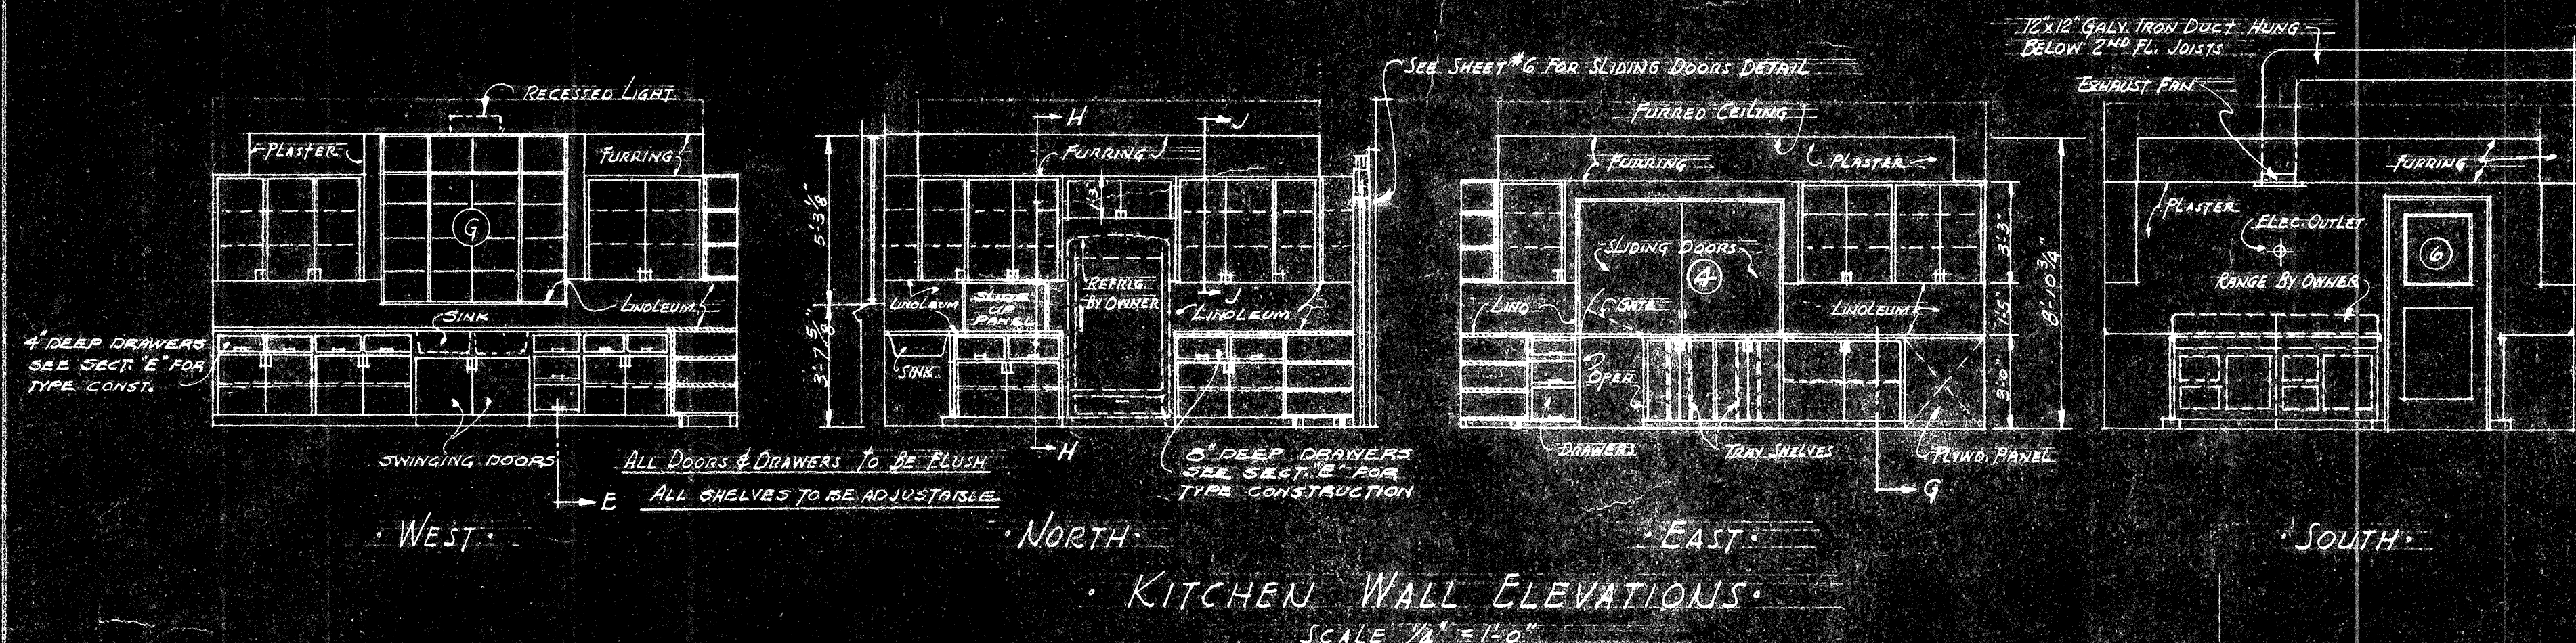
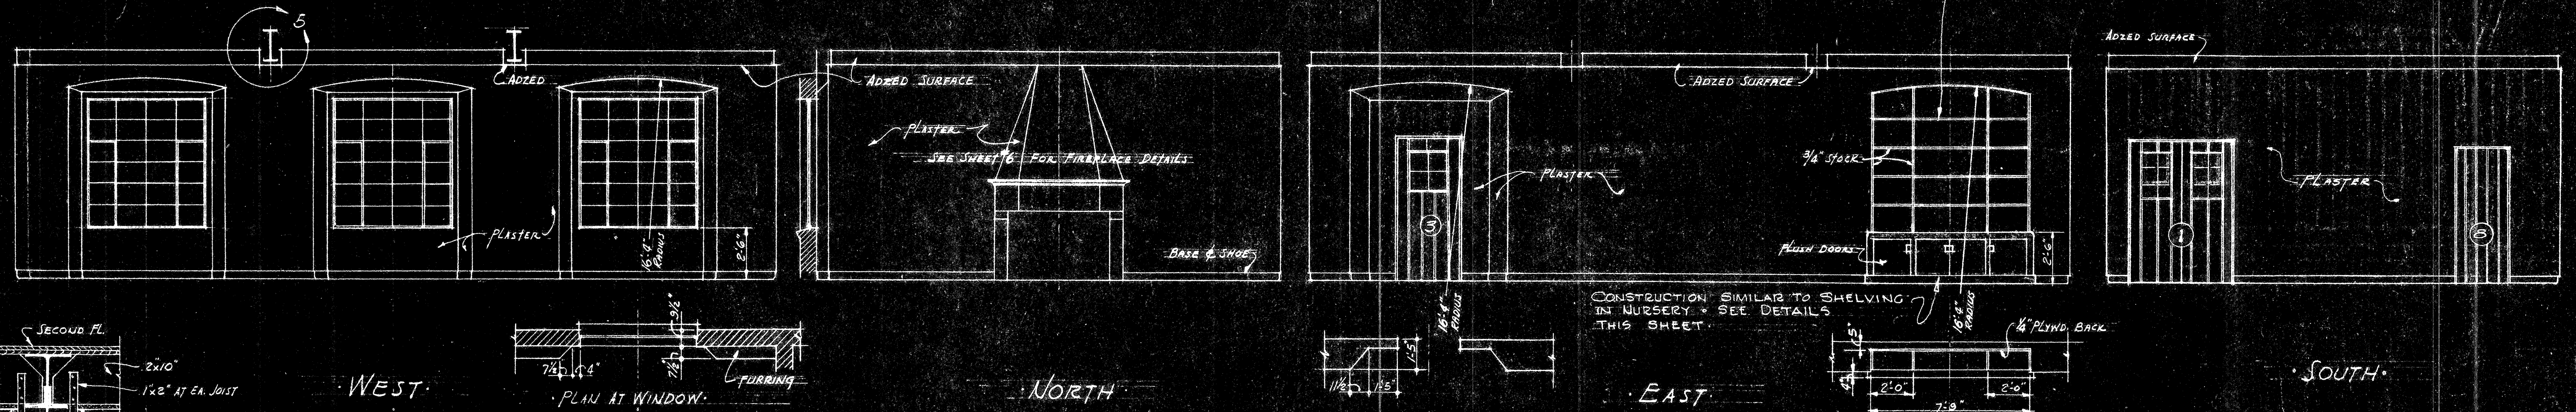


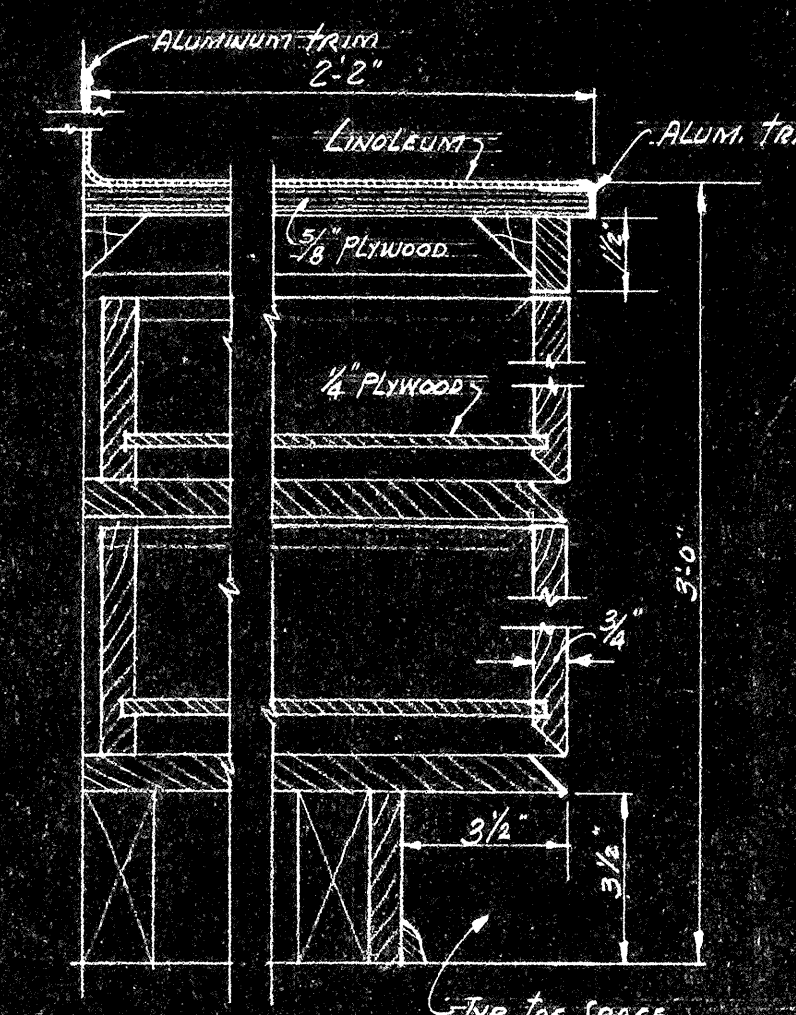

ELEVATION EAST END
SCALE 1/4" = 1'-0"


INTERIOR ELEVATION NURSERY

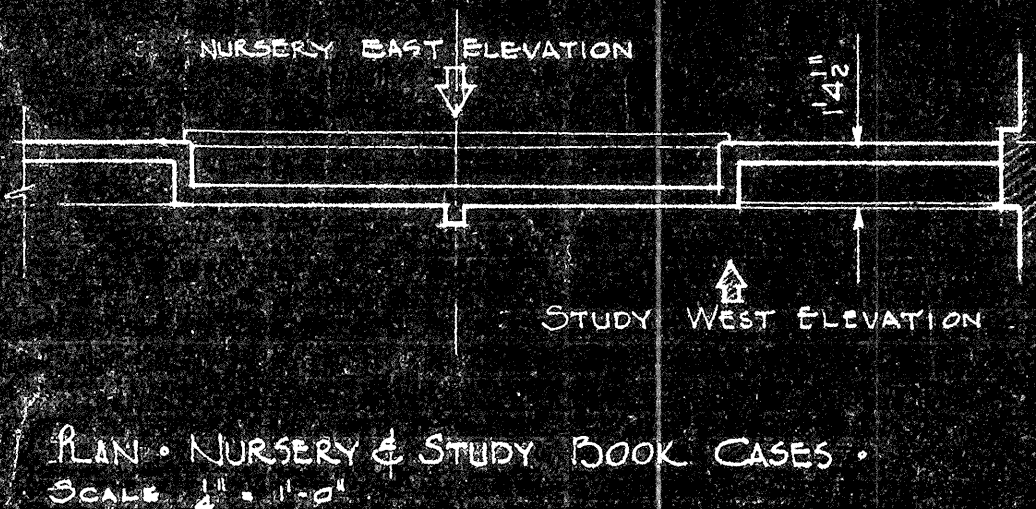

SECTION G
SCALE 3/4" = 1'-0"

ELEVATION
SCALE 3/4" = 1'-0"

NOTE: HEAD SIMILAR TO SEC. H-H WITH 2"x8" HEADERS

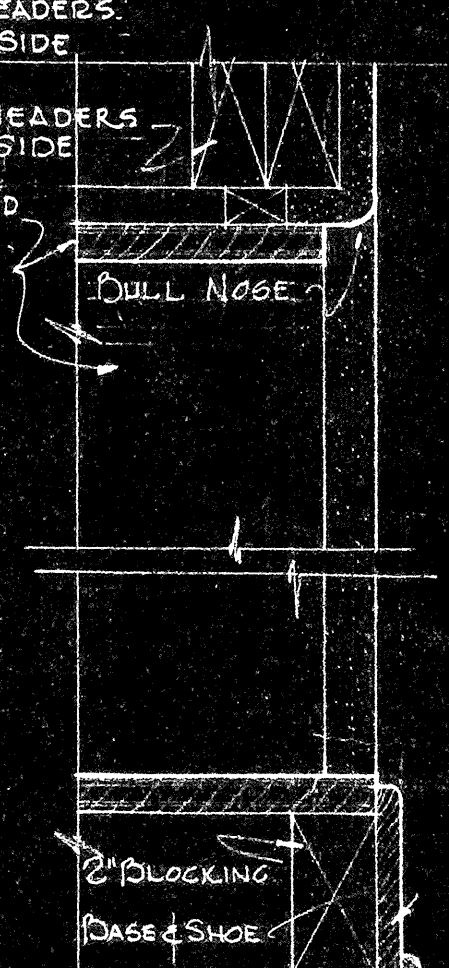

SECTION A-A - JAMB DETAIL
SCALE 3/4" = 1'-0"



SECTION D-D
SCALE 3/4" = 1'-0"

SECTION D-D
SCALE 3/4" = 1'-0"

SECTION C-C
SCALE 3/4" = 1'-0"

TITLE OF SHEET			
INTERIOR DETAILS			
10-1-45	WESTBERG	7	
452	ALHAMBRA		
684	ALHAMBRA		
A PARISH HALL AND CHURCH SCHOOL for ST. EDMUND'S EPISCOPAL CHURCH - SAN MARINO			