

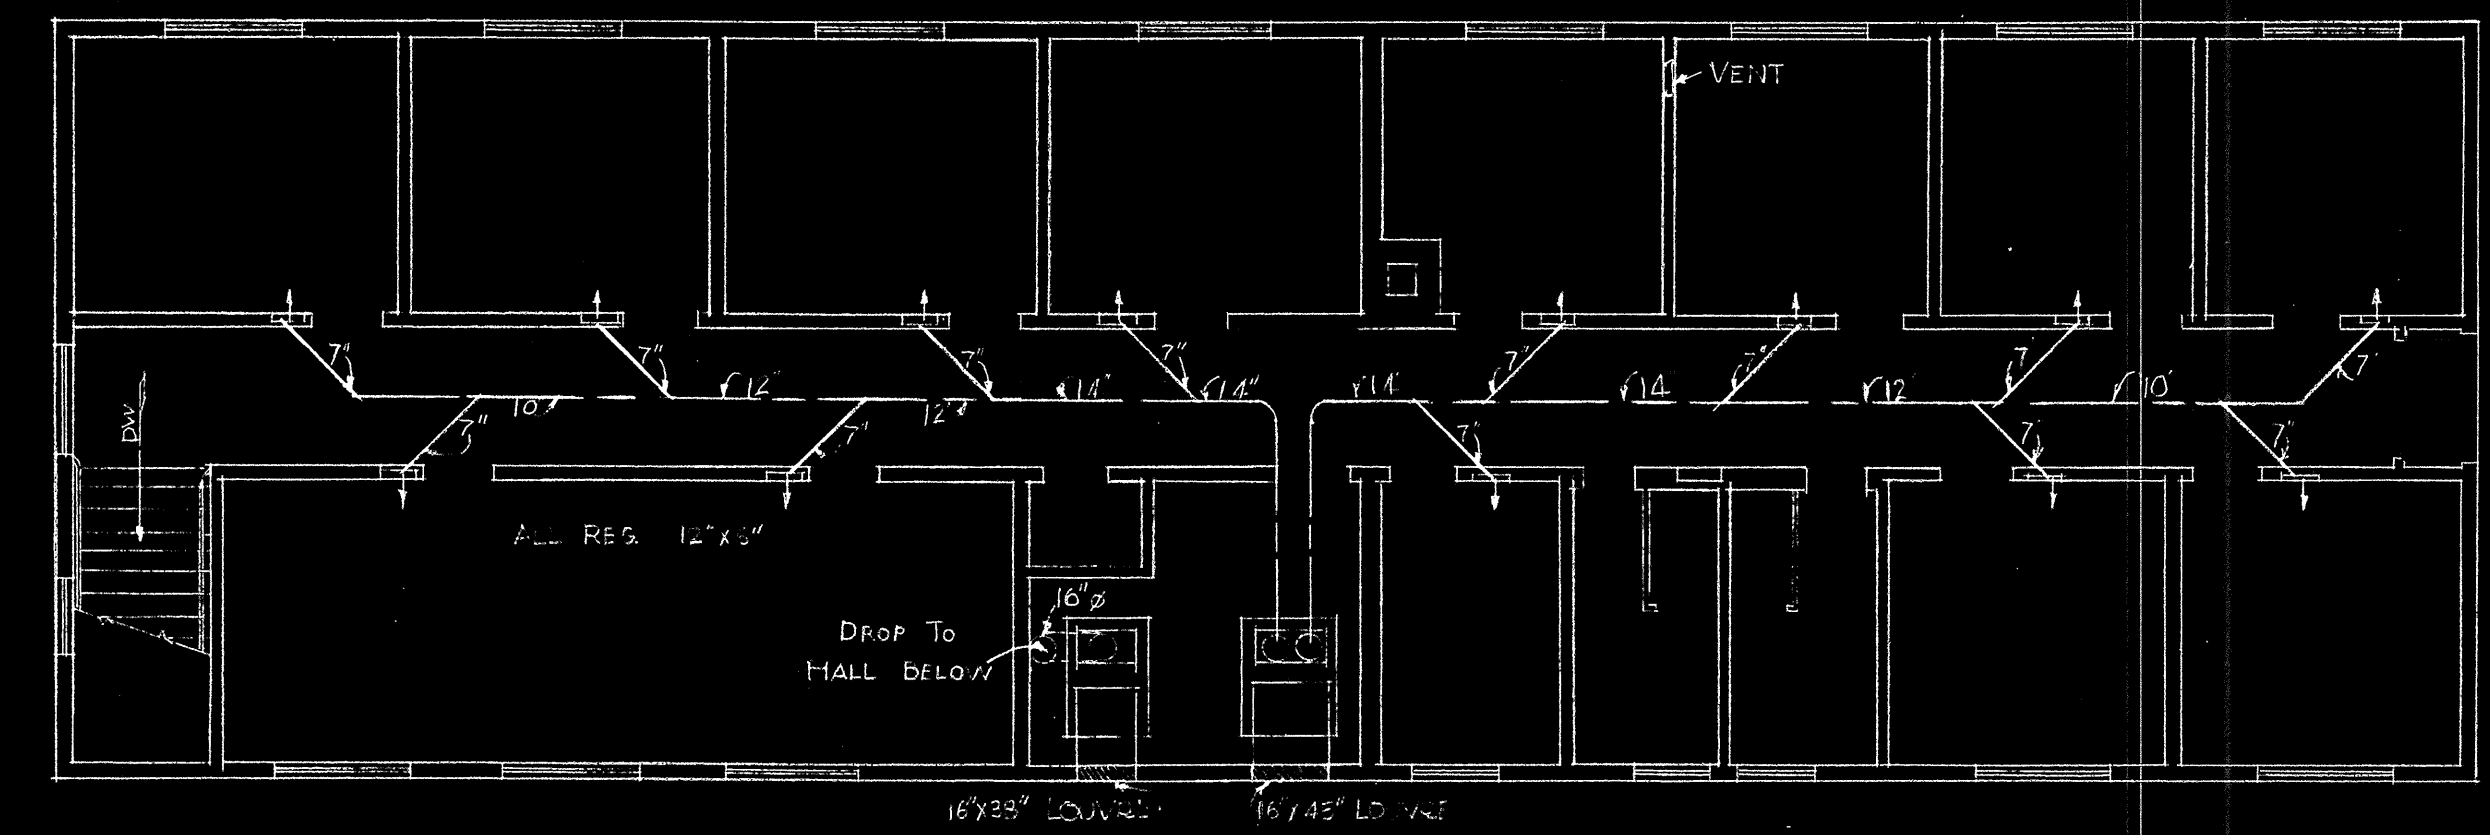



FOUNDATION PLAN
SCALE $\frac{1}{8}'' = 1'-0''$

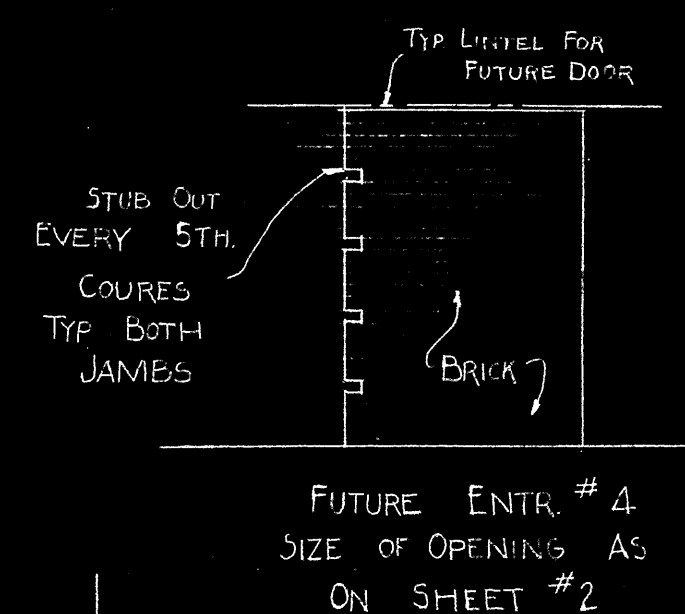

SECOND FLOOR PLAN
SCALE $\frac{1}{8}" = 1'-0"$

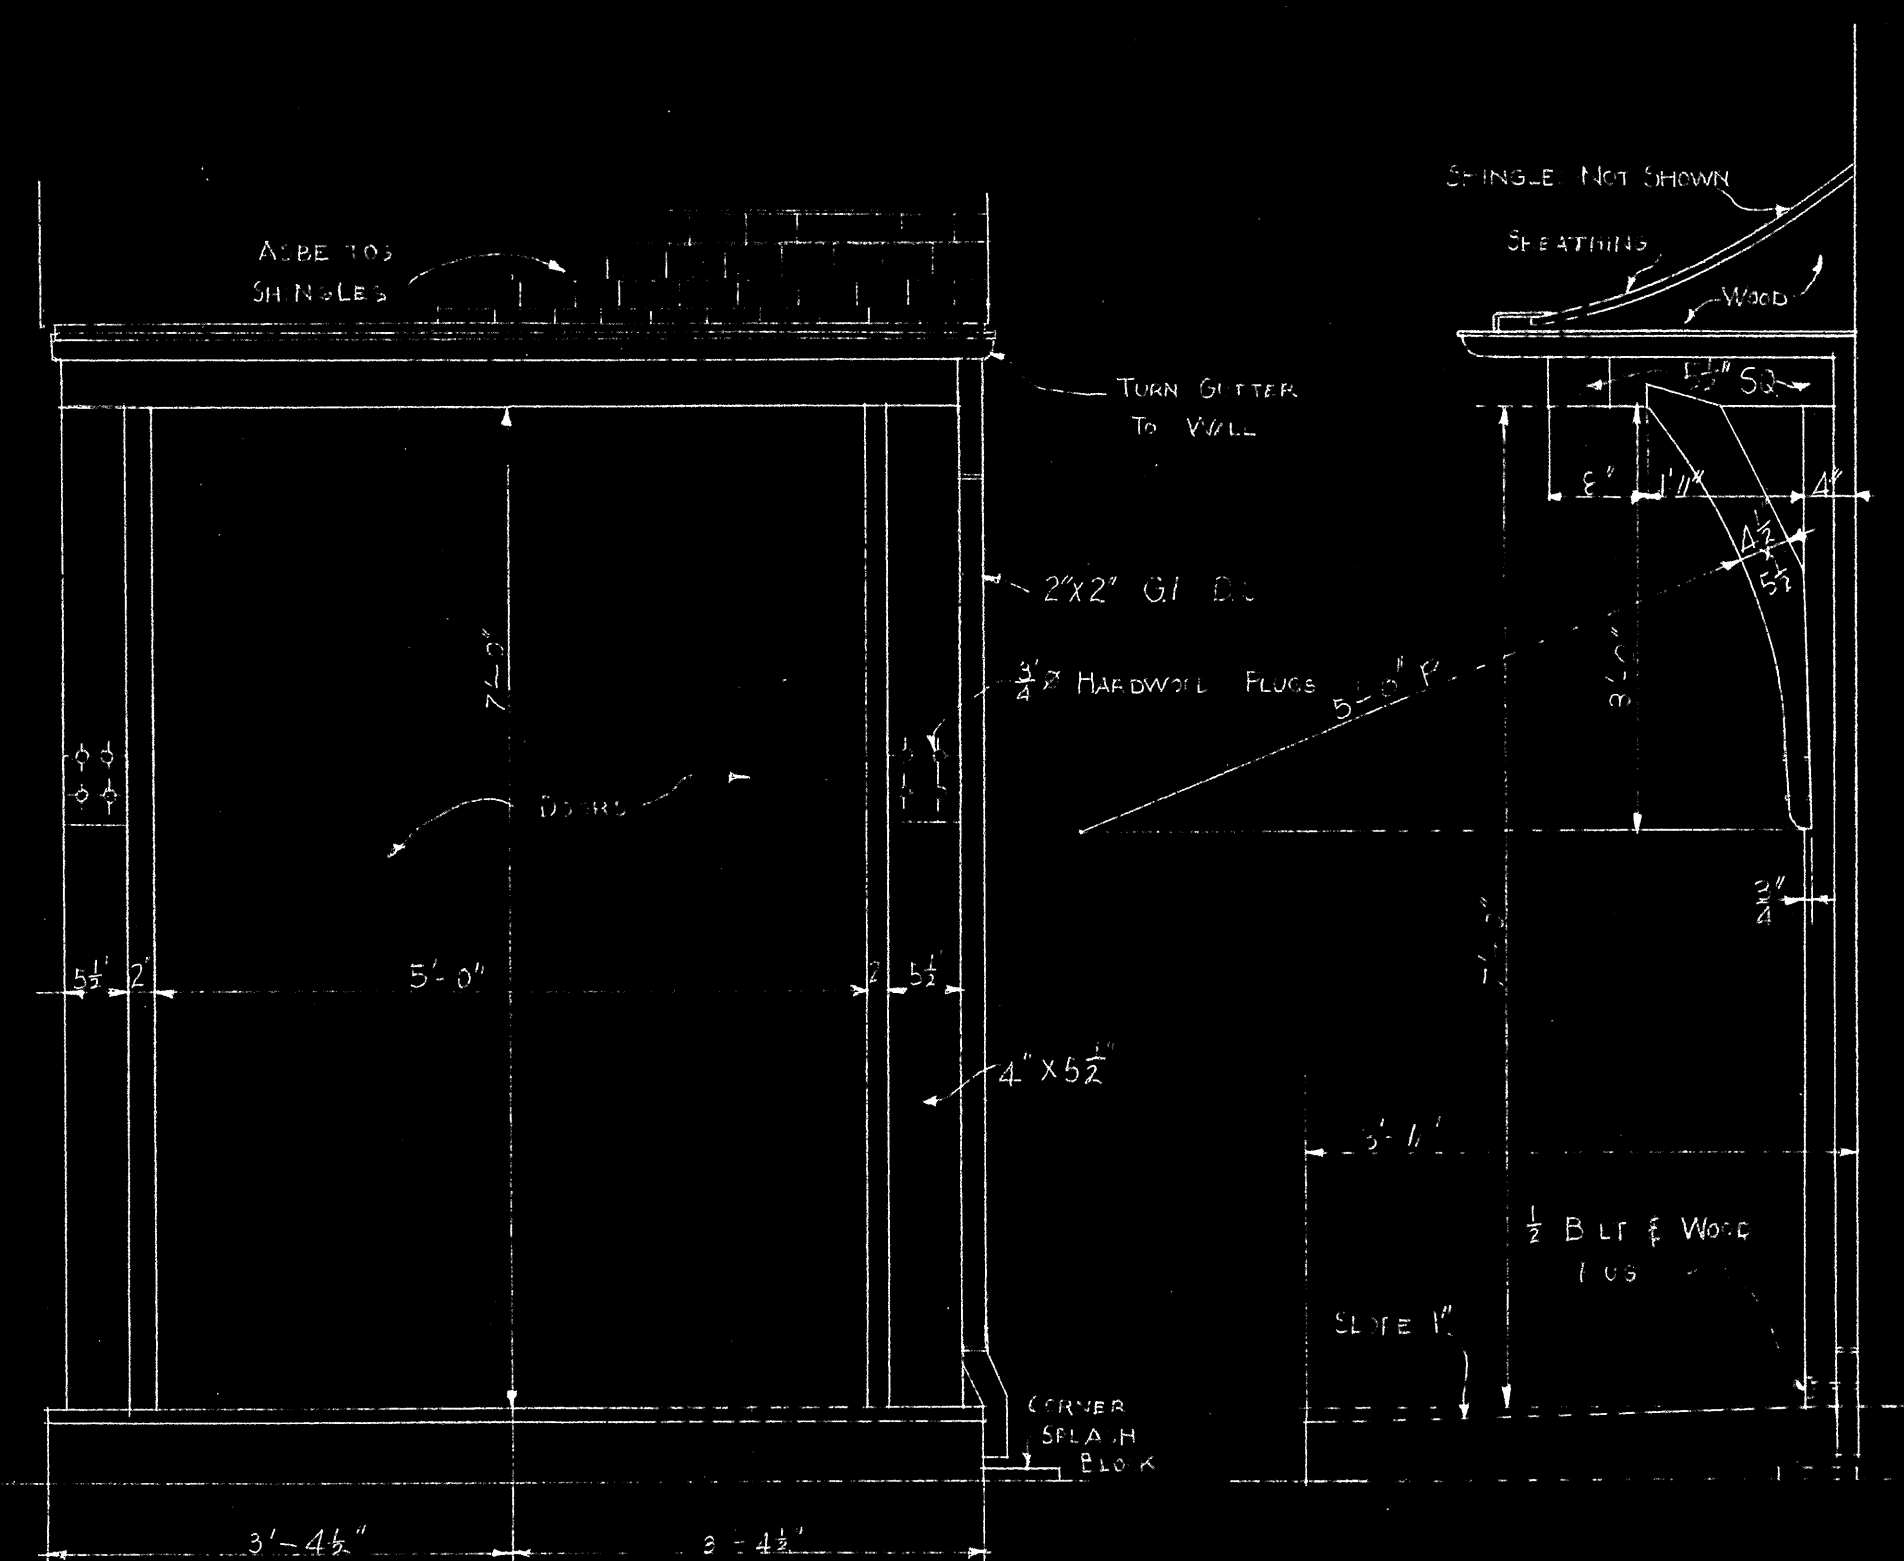


FUTURE ENTR. #4
SIZE OF OPENING AS
ON SHEET #2

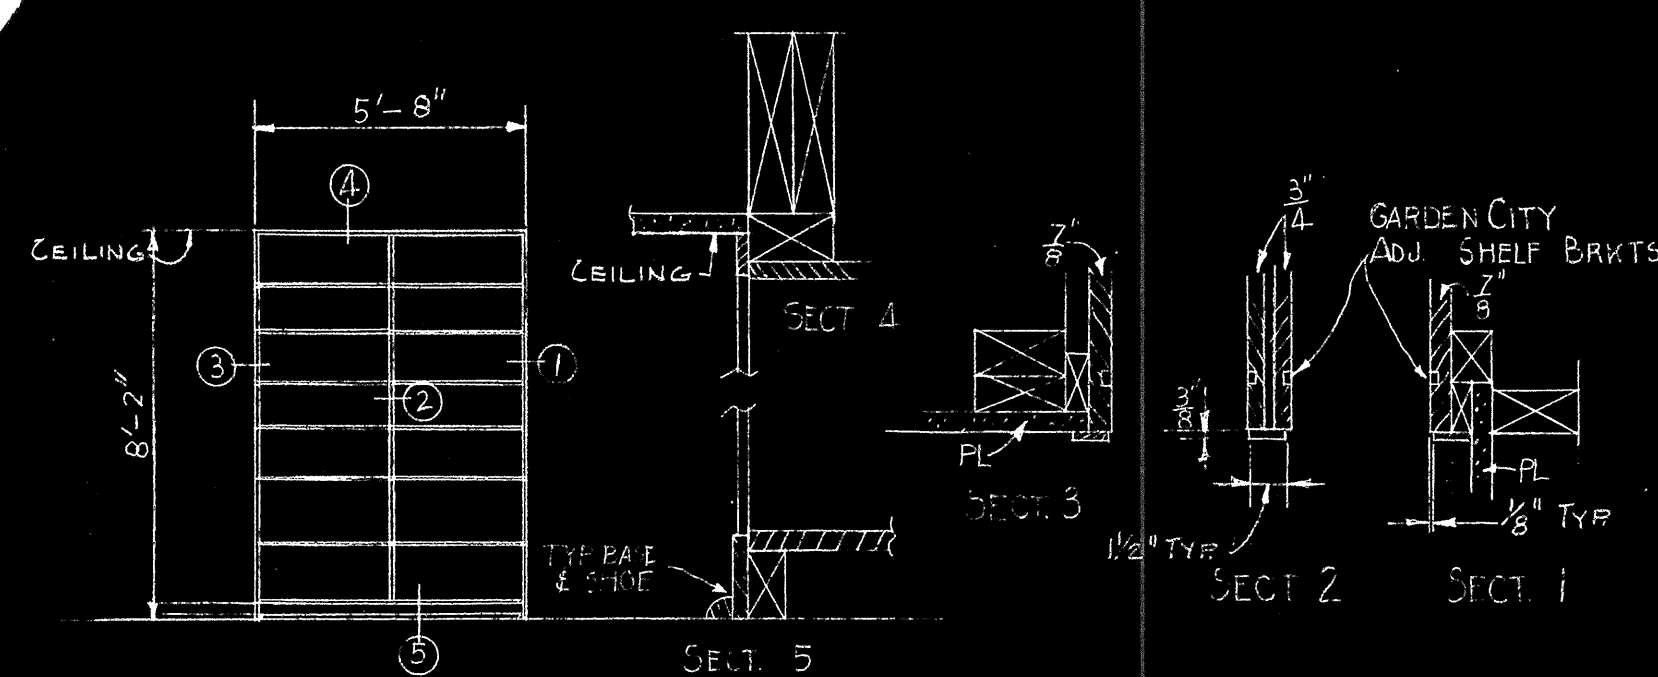


SCALE $\frac{1}{4}'' = 1'-0''$

SCALE $1\frac{1}{2}" = 1'-0"$

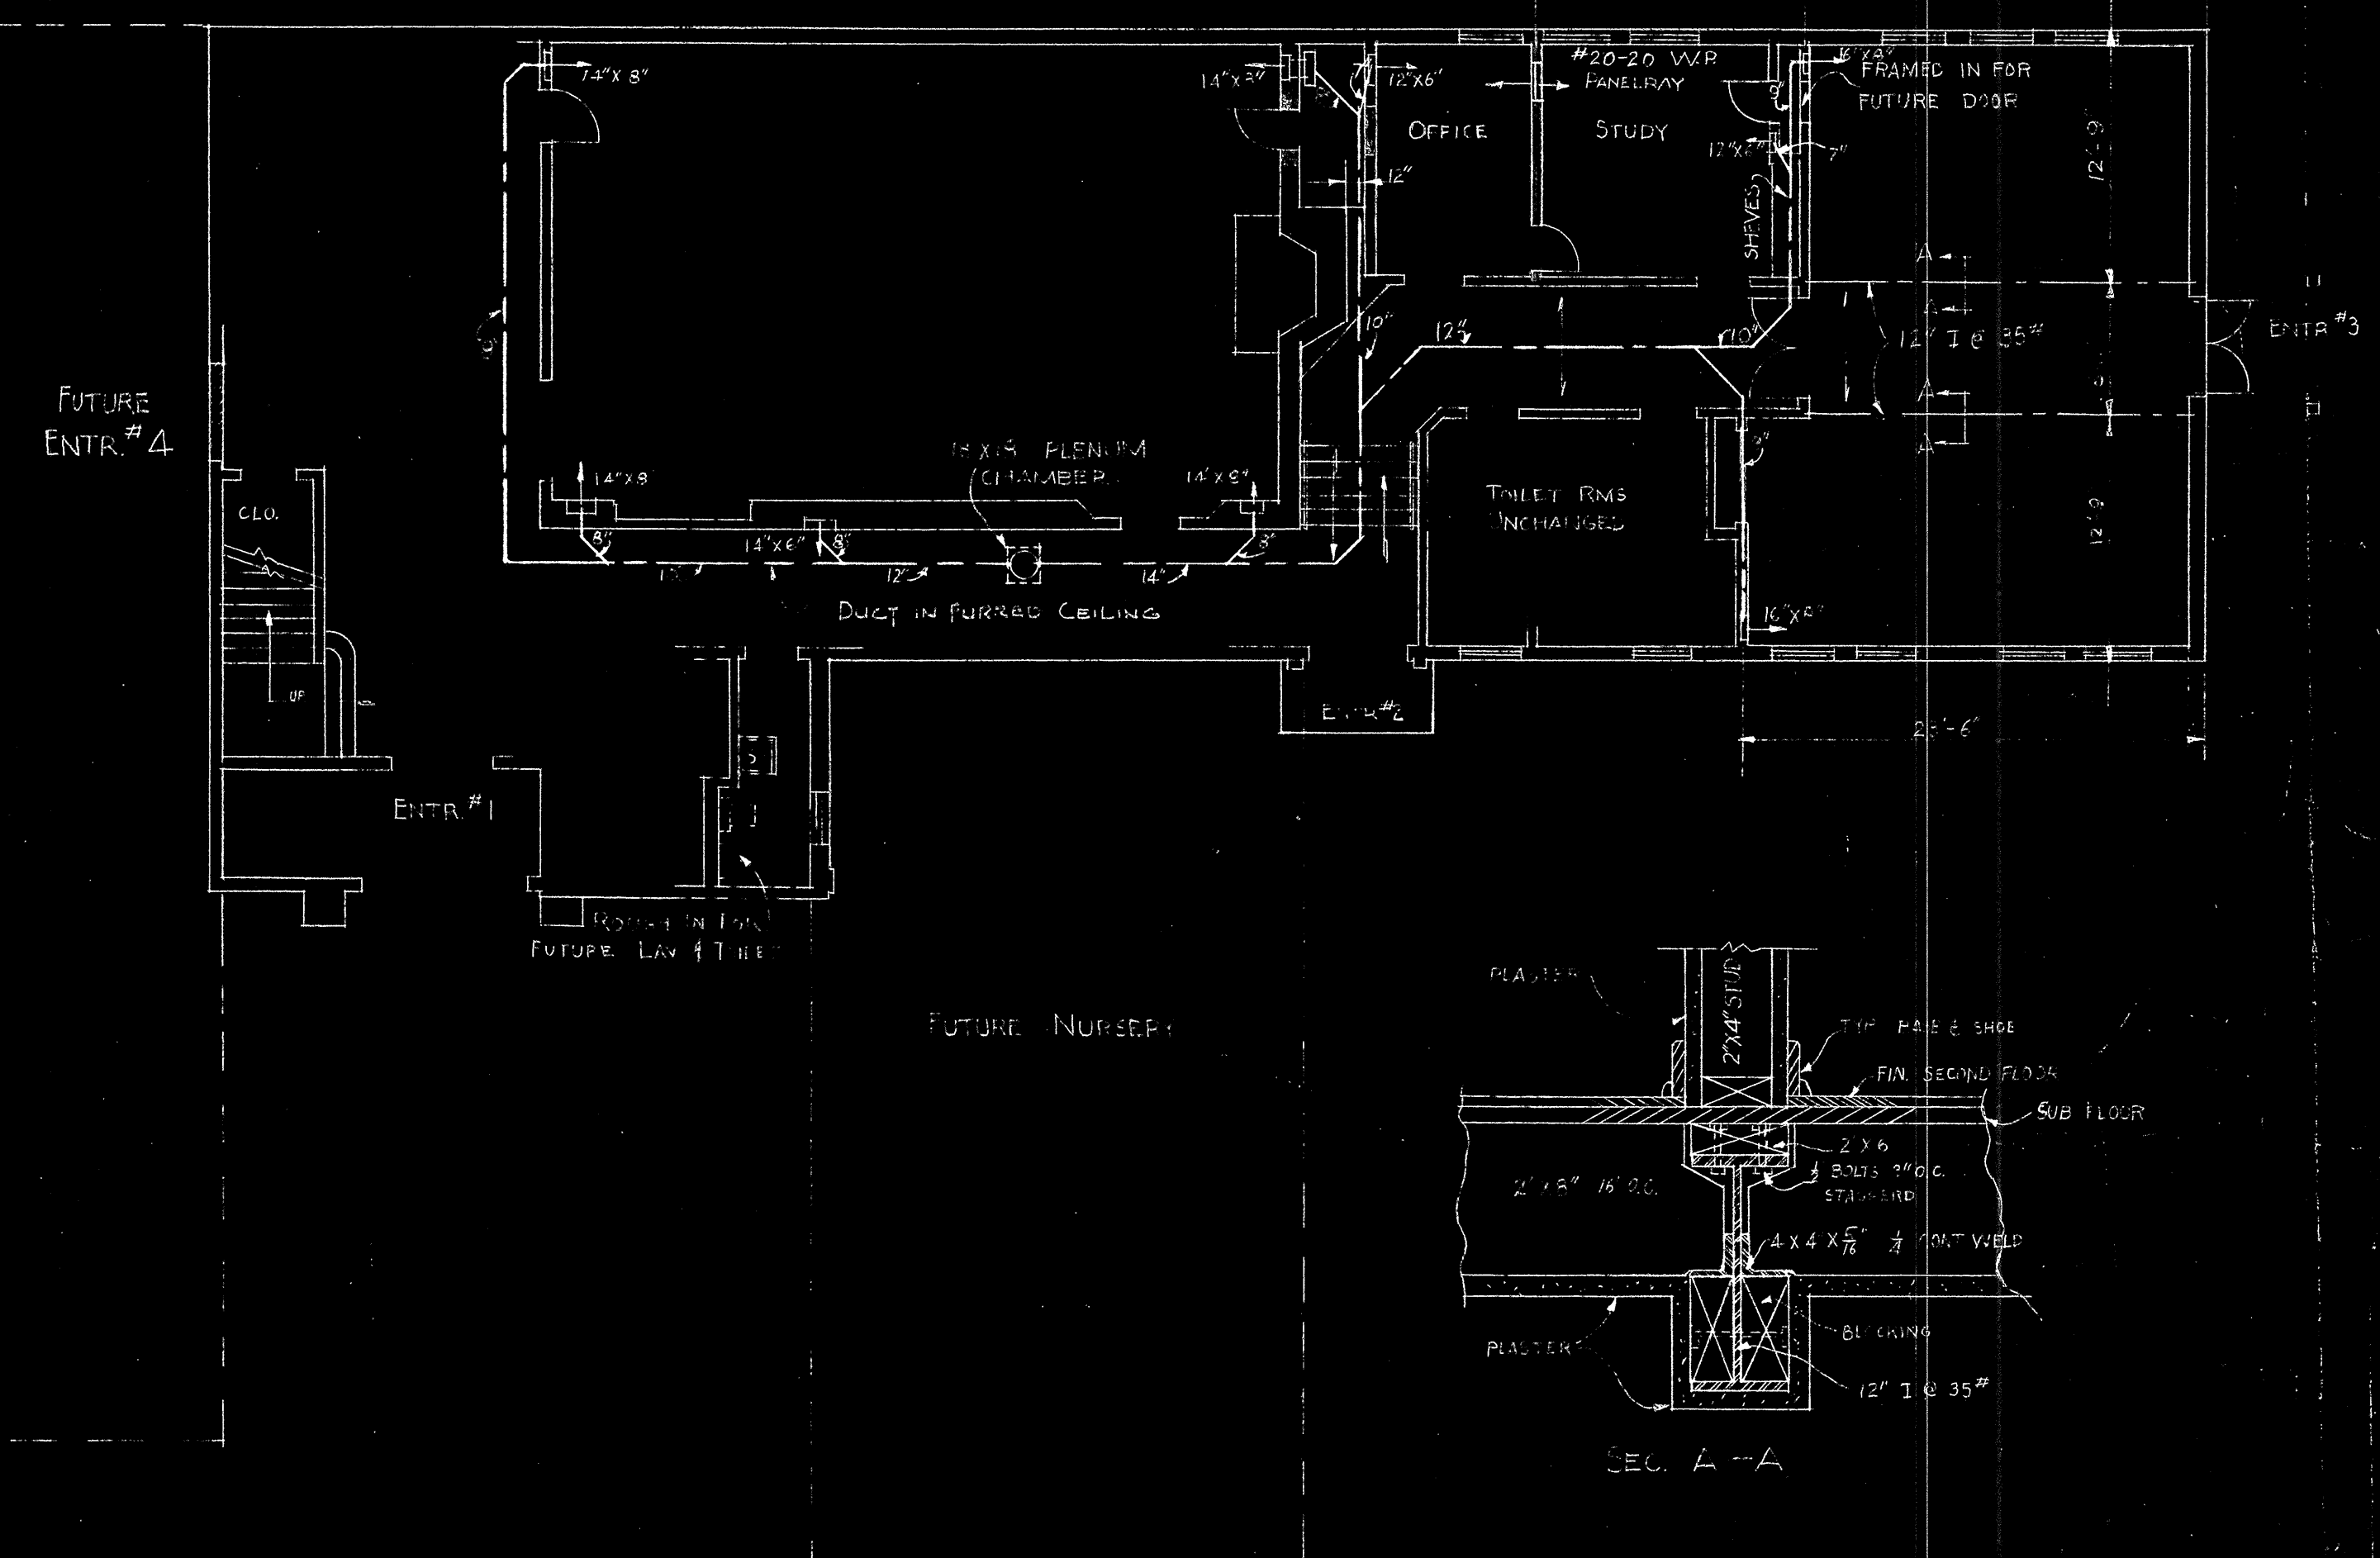

FIRST FLOOR PLAN
SCALE $\frac{1}{8}'' = 1'-0''$

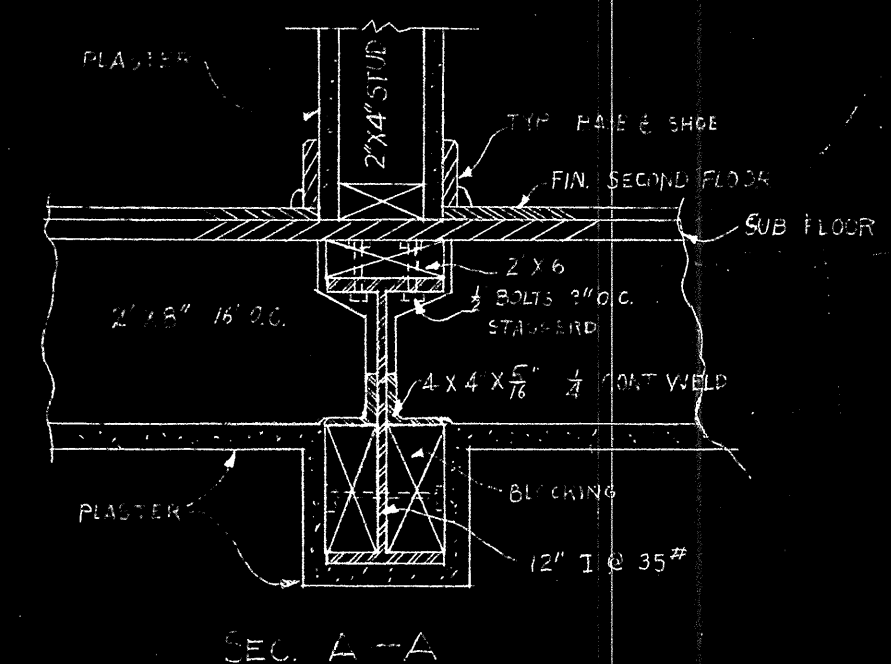

SEC. A-A

REVISED PLANS

1-17-26
452
A-1

A PARISH HALL AND
CHURCH SCHOOL for ST. EDMUNDS
EPISCOPAL CHURCH - SAN MARINO