



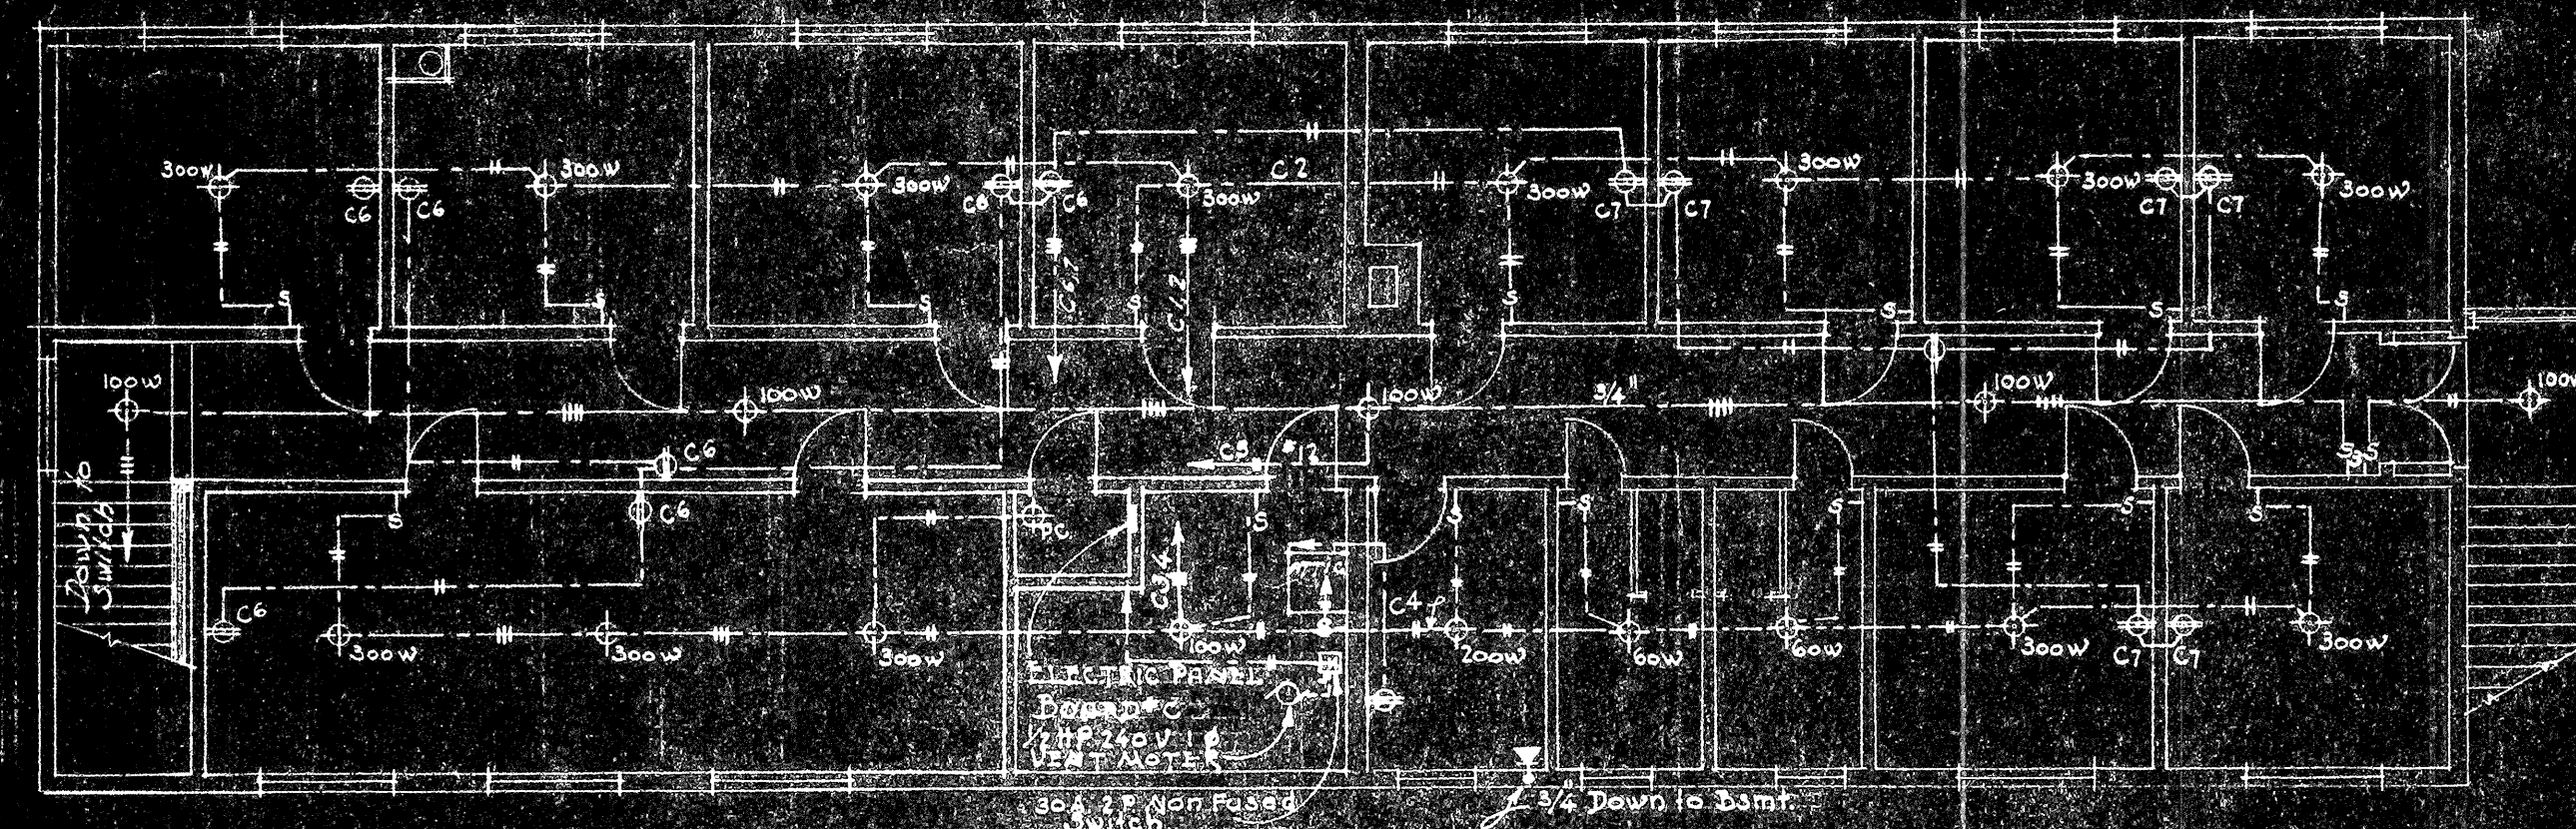


SECOND FLOOR PLAN
ELECTRICAL
SCALE 1/8" = 1'-0"

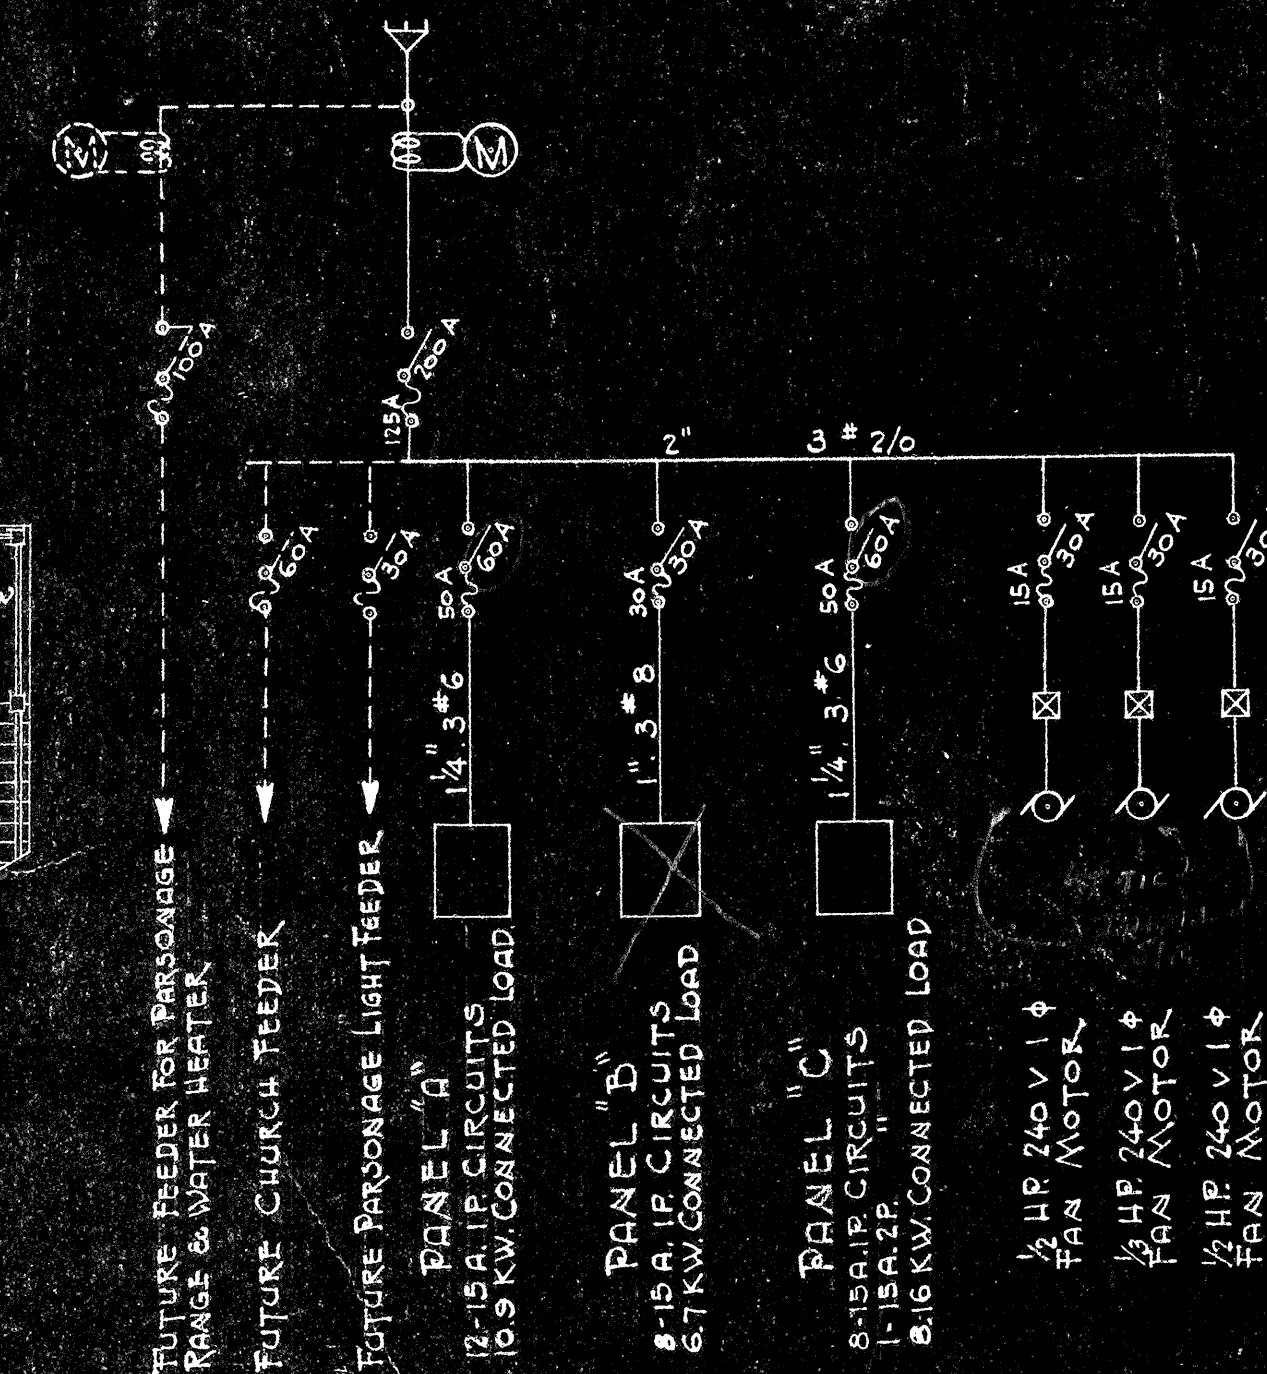


SERVICE DIAGRAM
No Scale

- SYMBOLS**
- CEILING OUTLET
 - CONVENIENCE OUTLET
 - MOTOR
 - FLOOR OUTLET
 - FUSED "XO" SWITCH
 - NON "X" SWITCH
 - MOTOR STARTER
 - BRACKET OUTLET
 - WALL SWITCH
 - 3-WAY SWITCH
 - CONDUIT RUN IN CEILING OR WALL
 - CONDUIT RUN UNDER FLOOR OR GROUND
 - CONDUIT ONLY
 - PULL CHAIN
 - FLUSH LIGHT
 - FUEL GAS
 - TELEPHONE
- NOTE**
- WIRE ABOVE FLOOR SHALL BE TYPE "R" OR "SN"
WIRE UNDERGROUND & BELOW FIRST FLOOR
SHALL BE TYPE "RV" OR "SNW".
- SUBSCRIPT INDICATES
OUTLET CONTROLLED
- SIZE IS 1/2" WITH #12
WIRE UNLESS
OTHERWISE MARKED.
CROSS MARKS
INDICATE NO. OF WIRES.

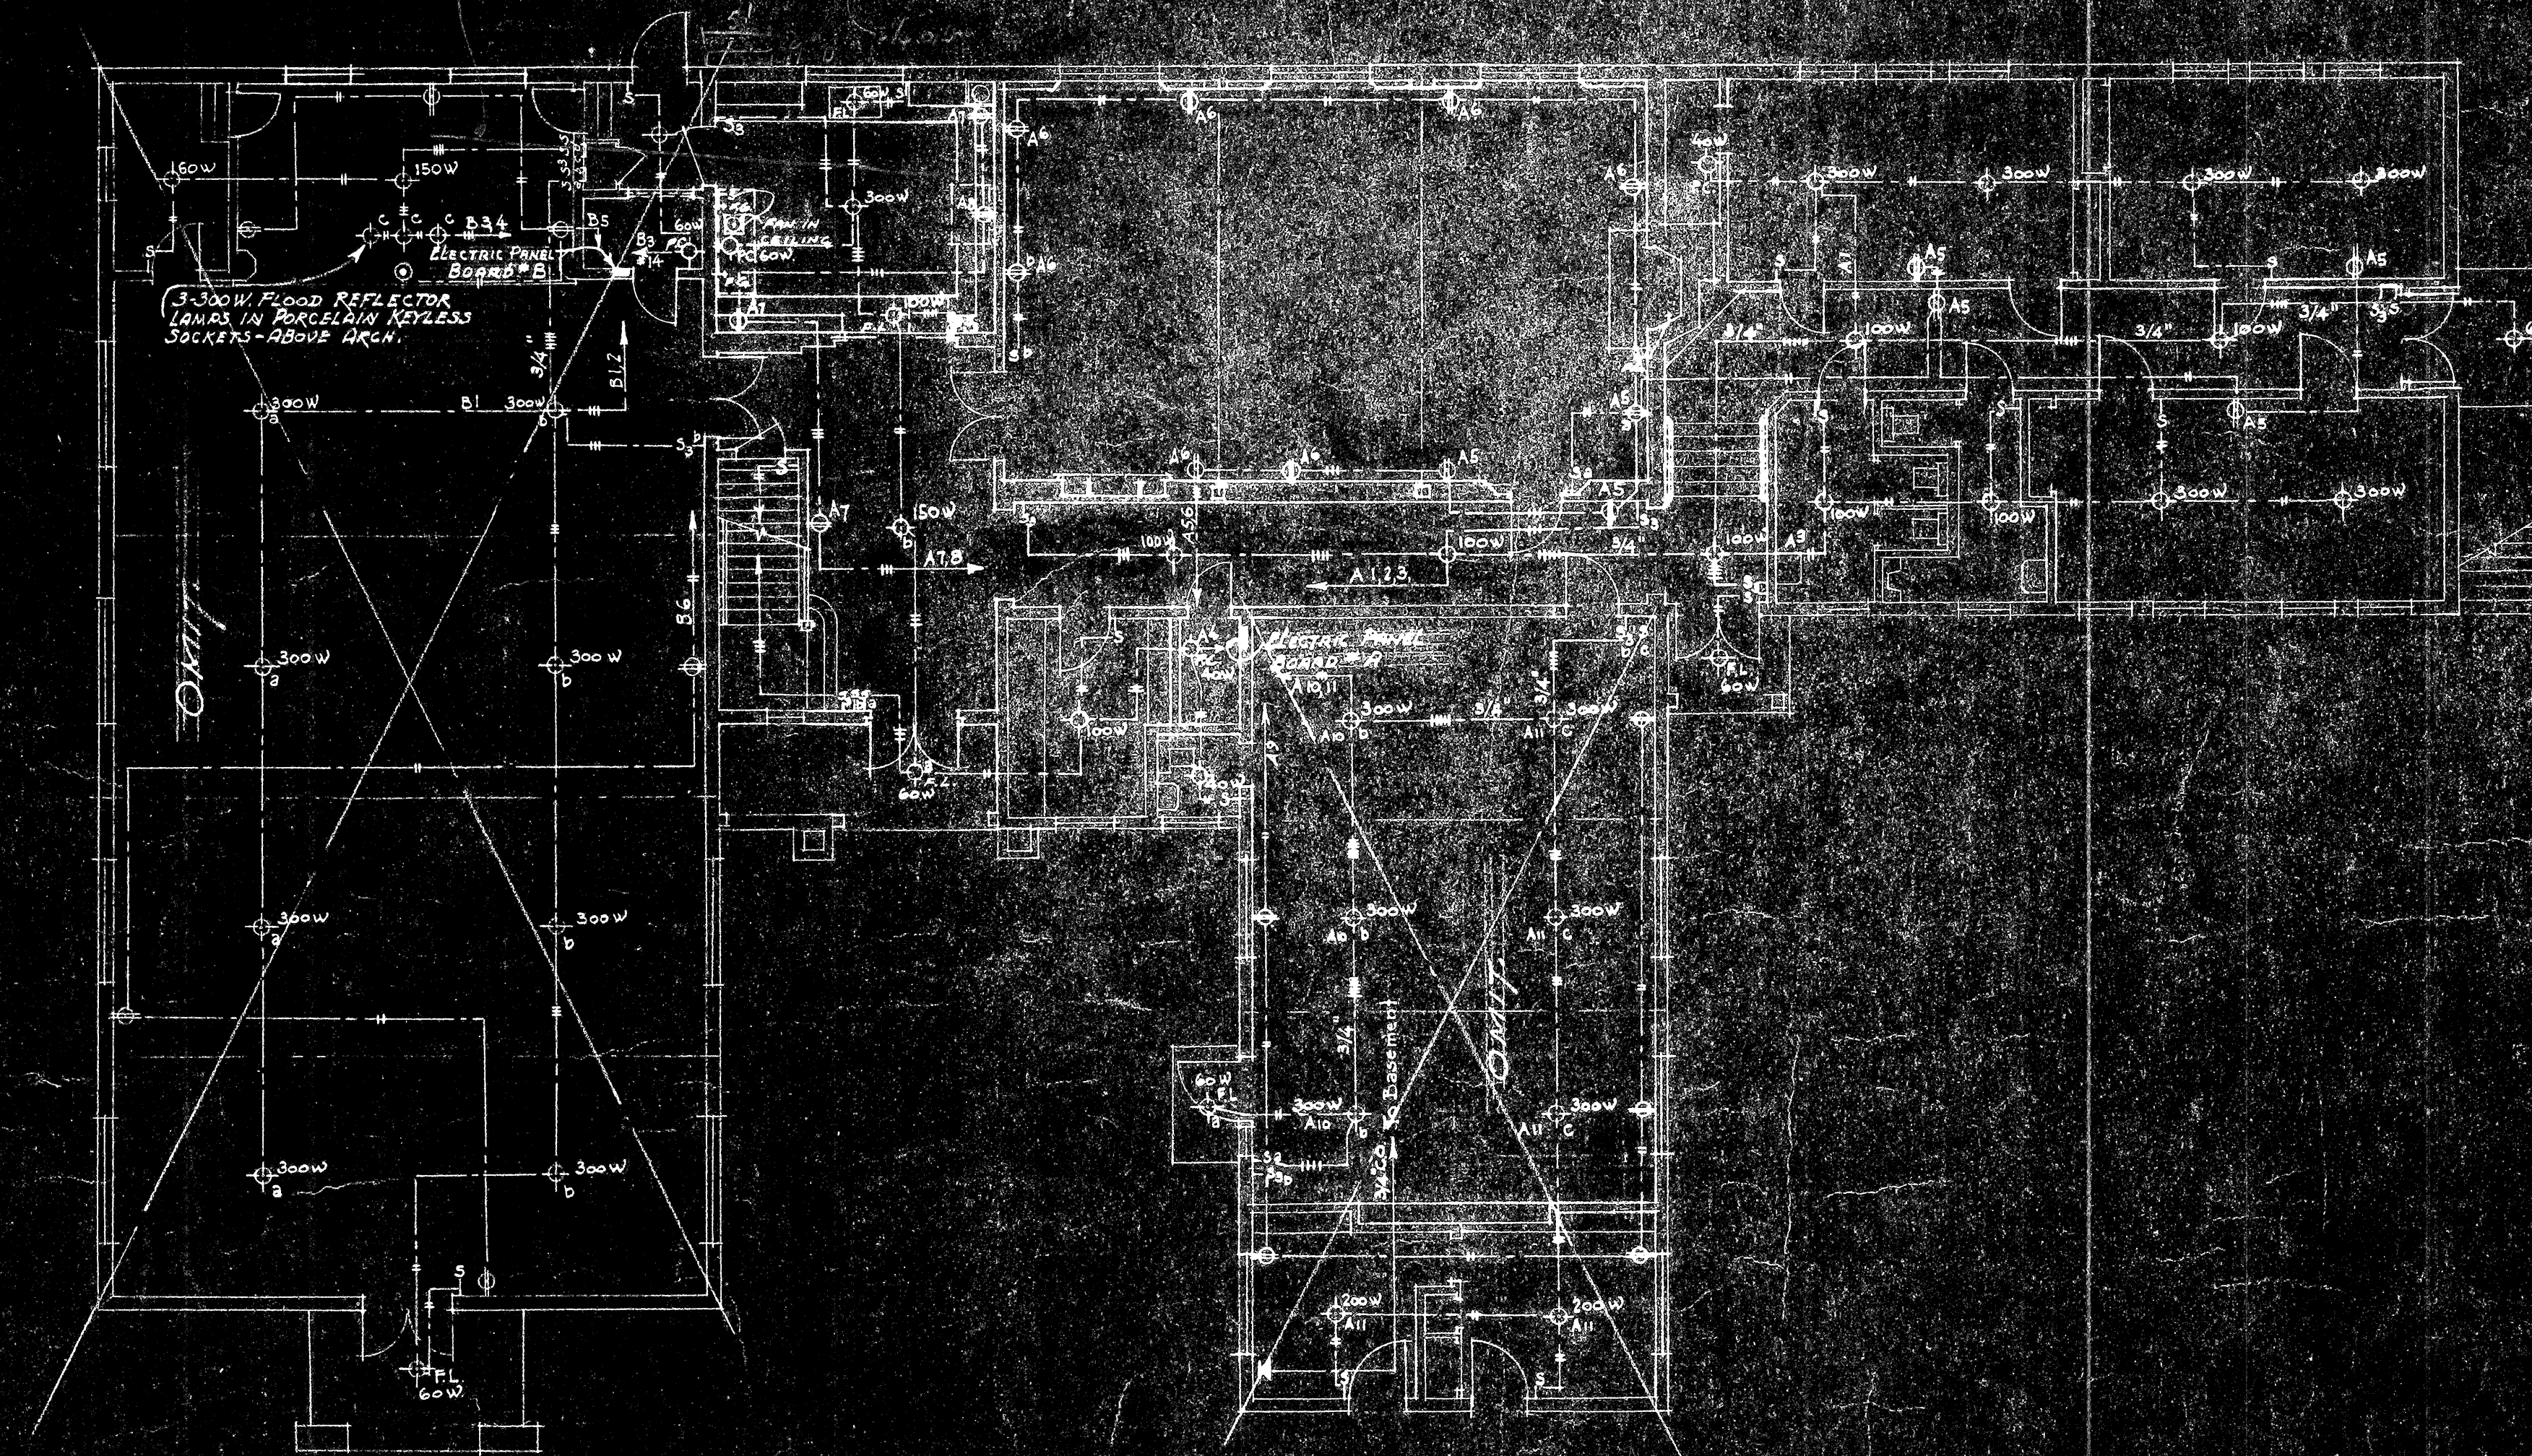

FIRST FLOOR PLAN
ELECTRICAL
SCALE 1/8" = 1'-0"

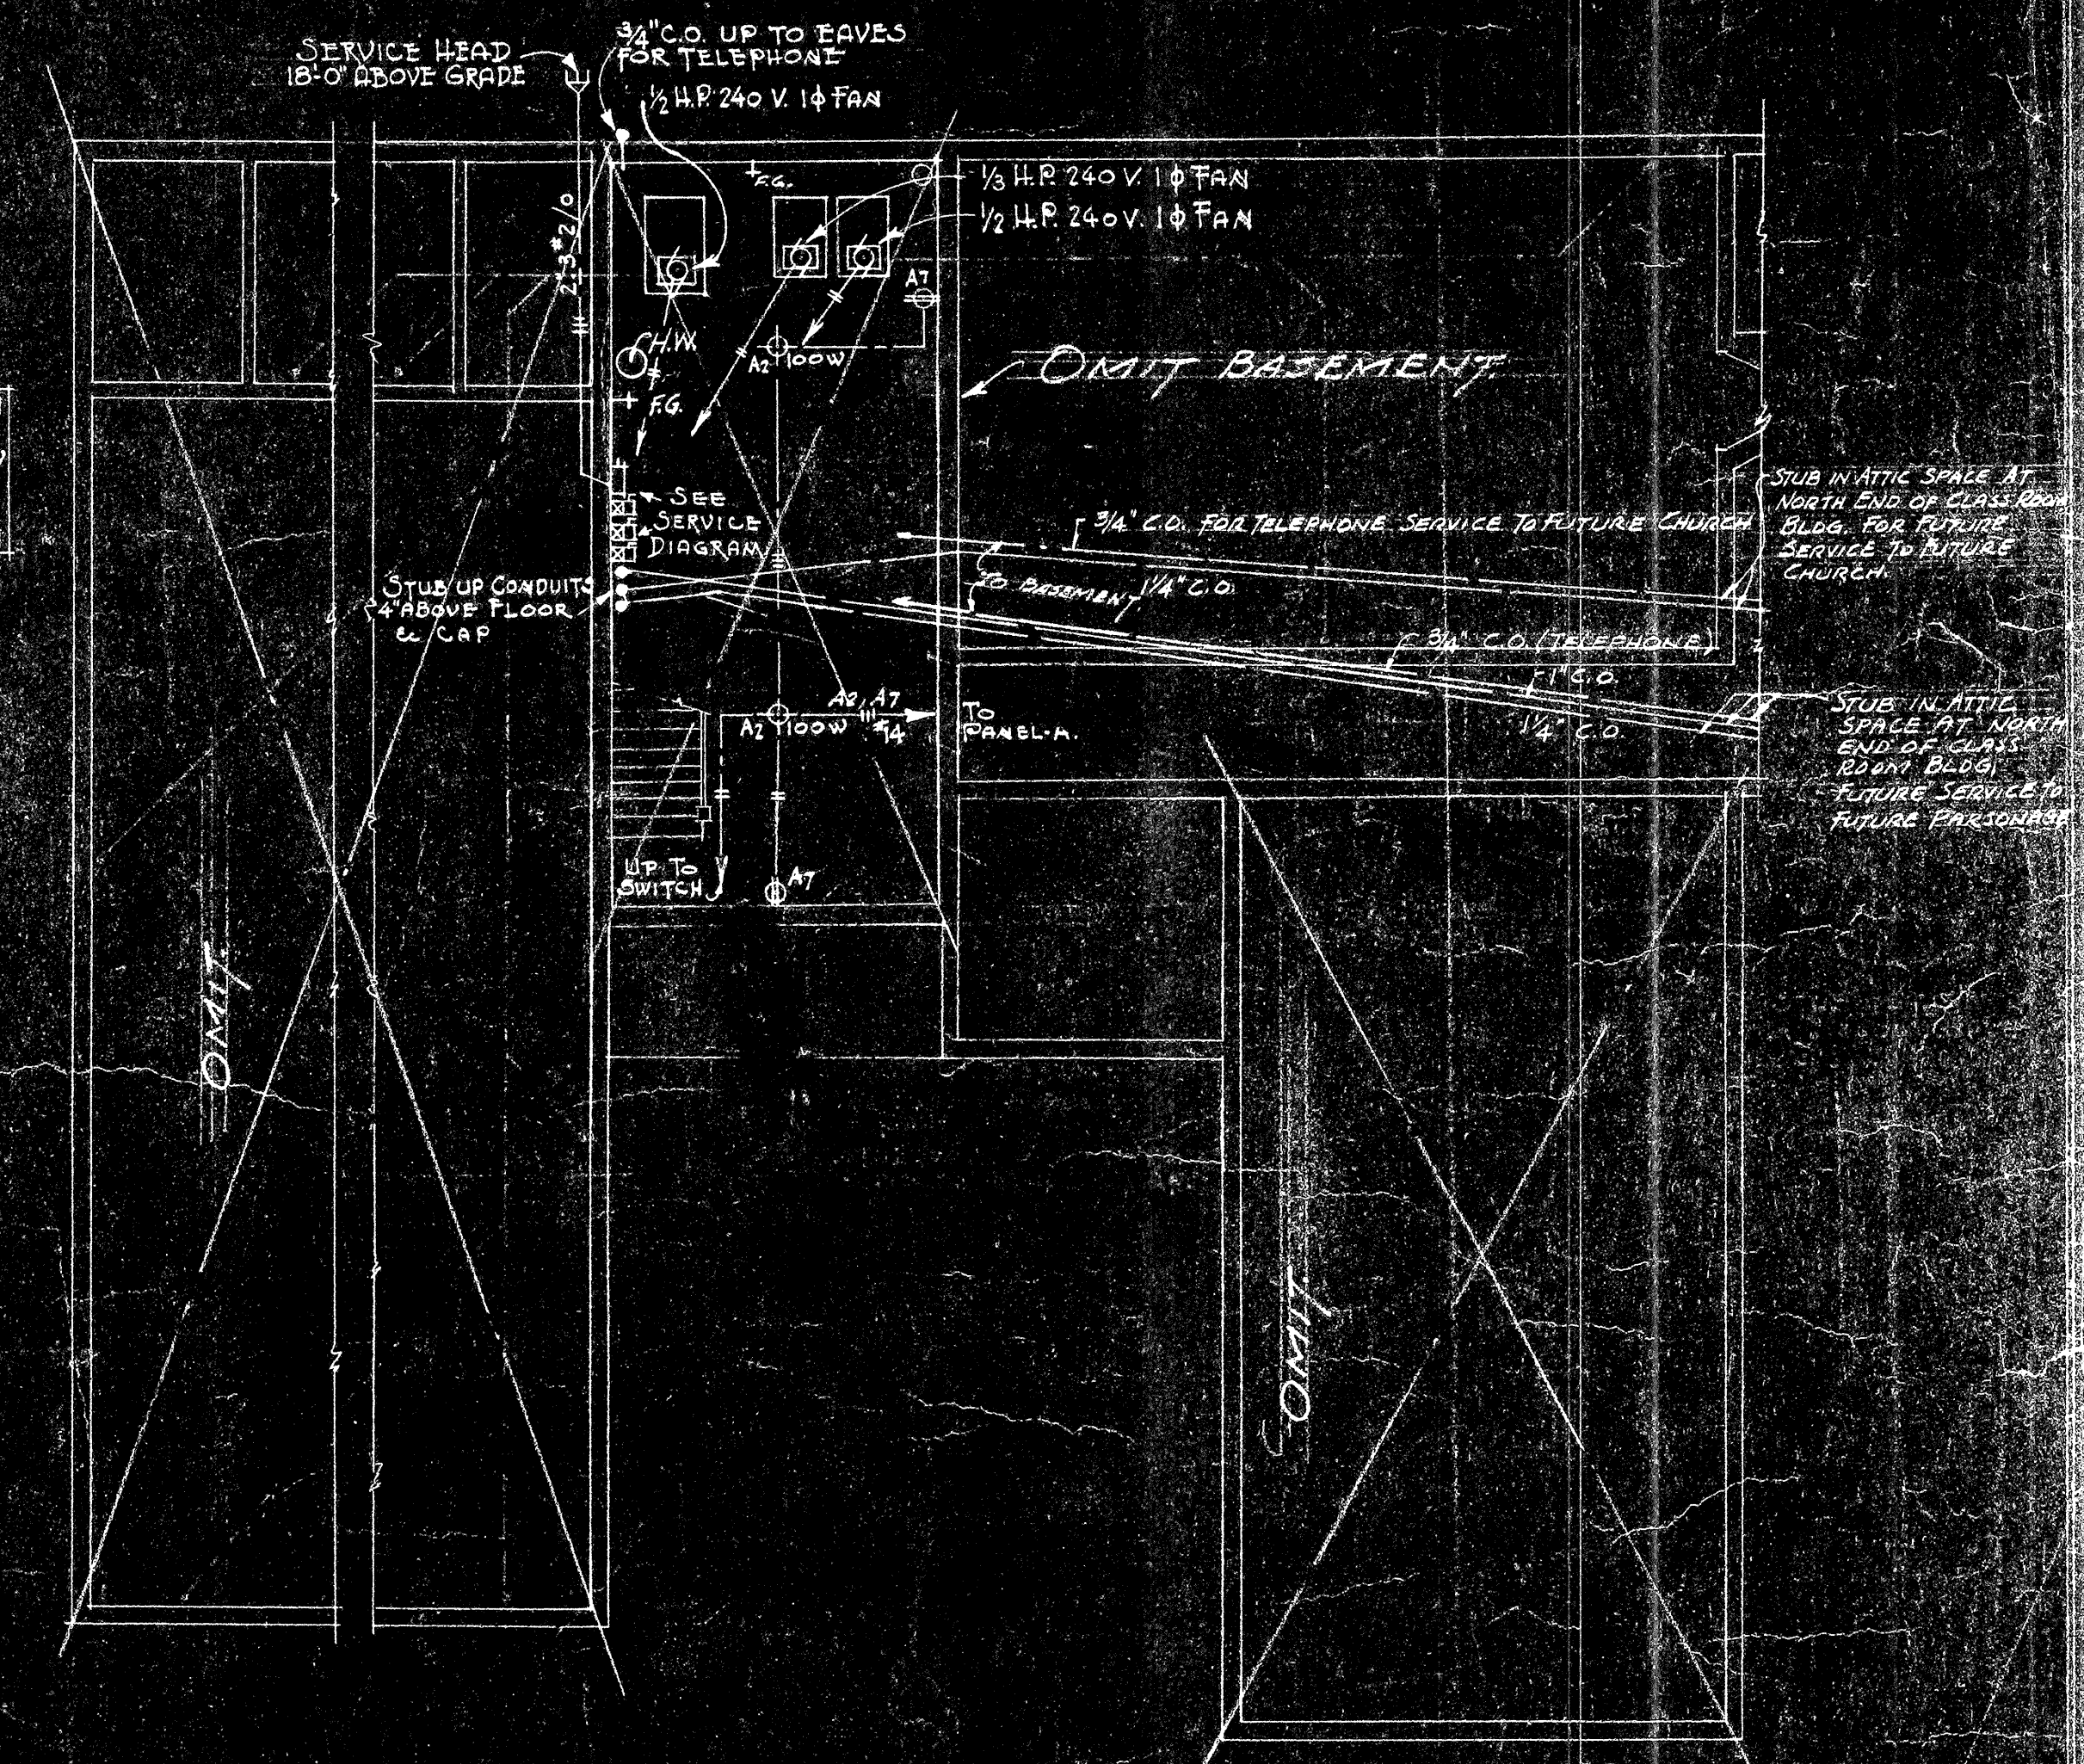

BASEMENT FLOOR PLAN
ELECTRICAL
SCALE 1/8" = 1'-0"

REVISED JAN. 25, 1946

TITLE OF SHEET		8
ELECTRICAL PLAN		
BY	QUINTIN WESTBERG	ARCHITECTS
DATE	1945	
PROJECT		ALHAMBRA, CALIFORNIA
TITLE OF BUILDING		
A PARISH HALL AND CHURCH SCHOOL for ST. EDMUND'S EPISCOPAL CHURCH, SAN MARINO		
CONTRACTOR TO VERIFY ALL DIMENSIONS AT BUILDING		