

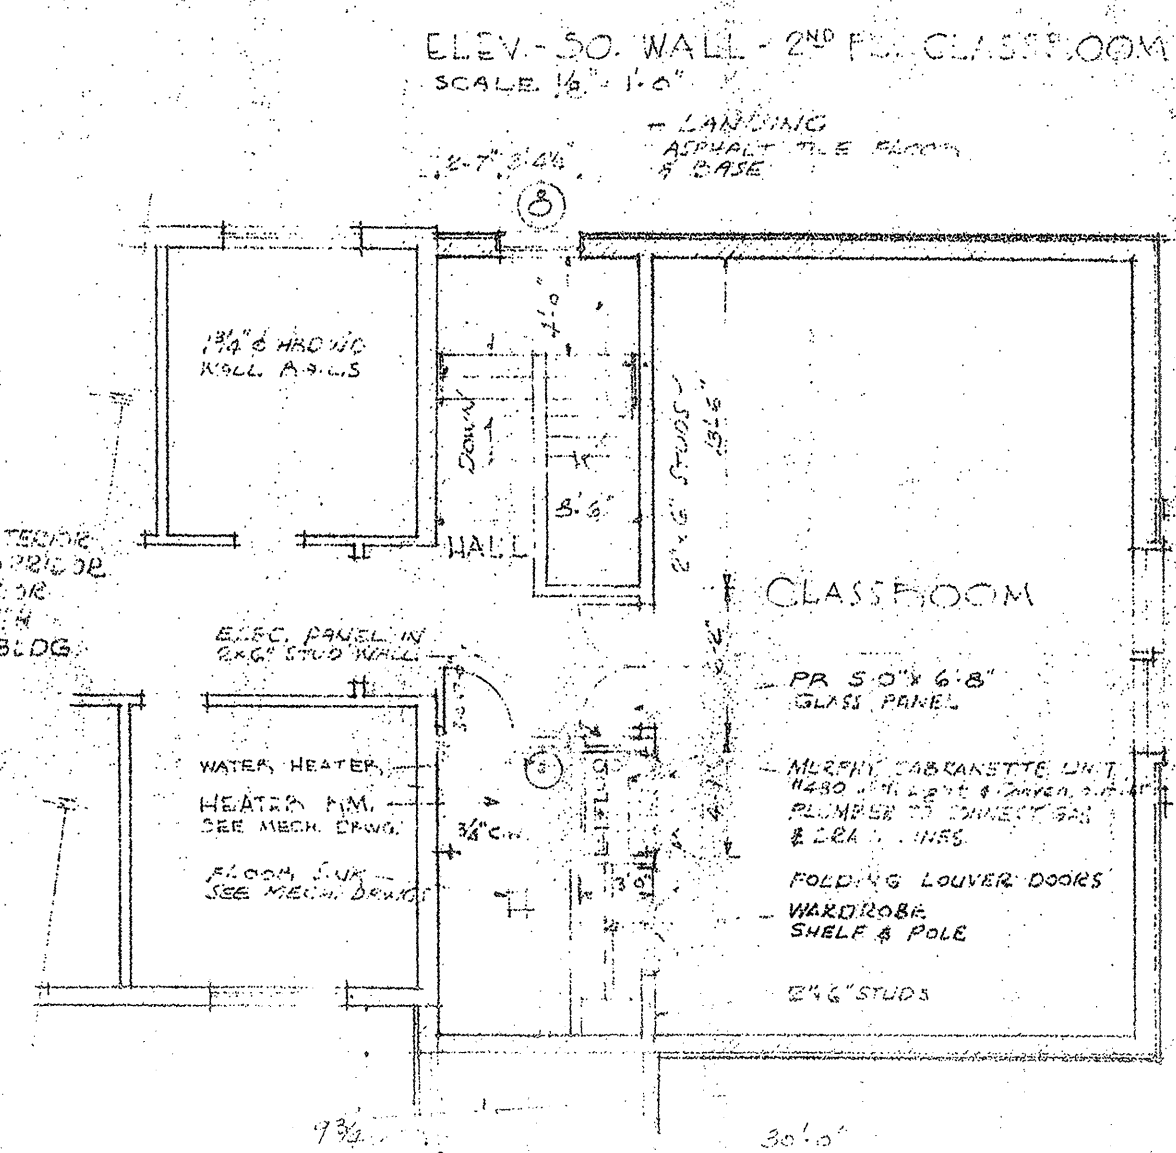
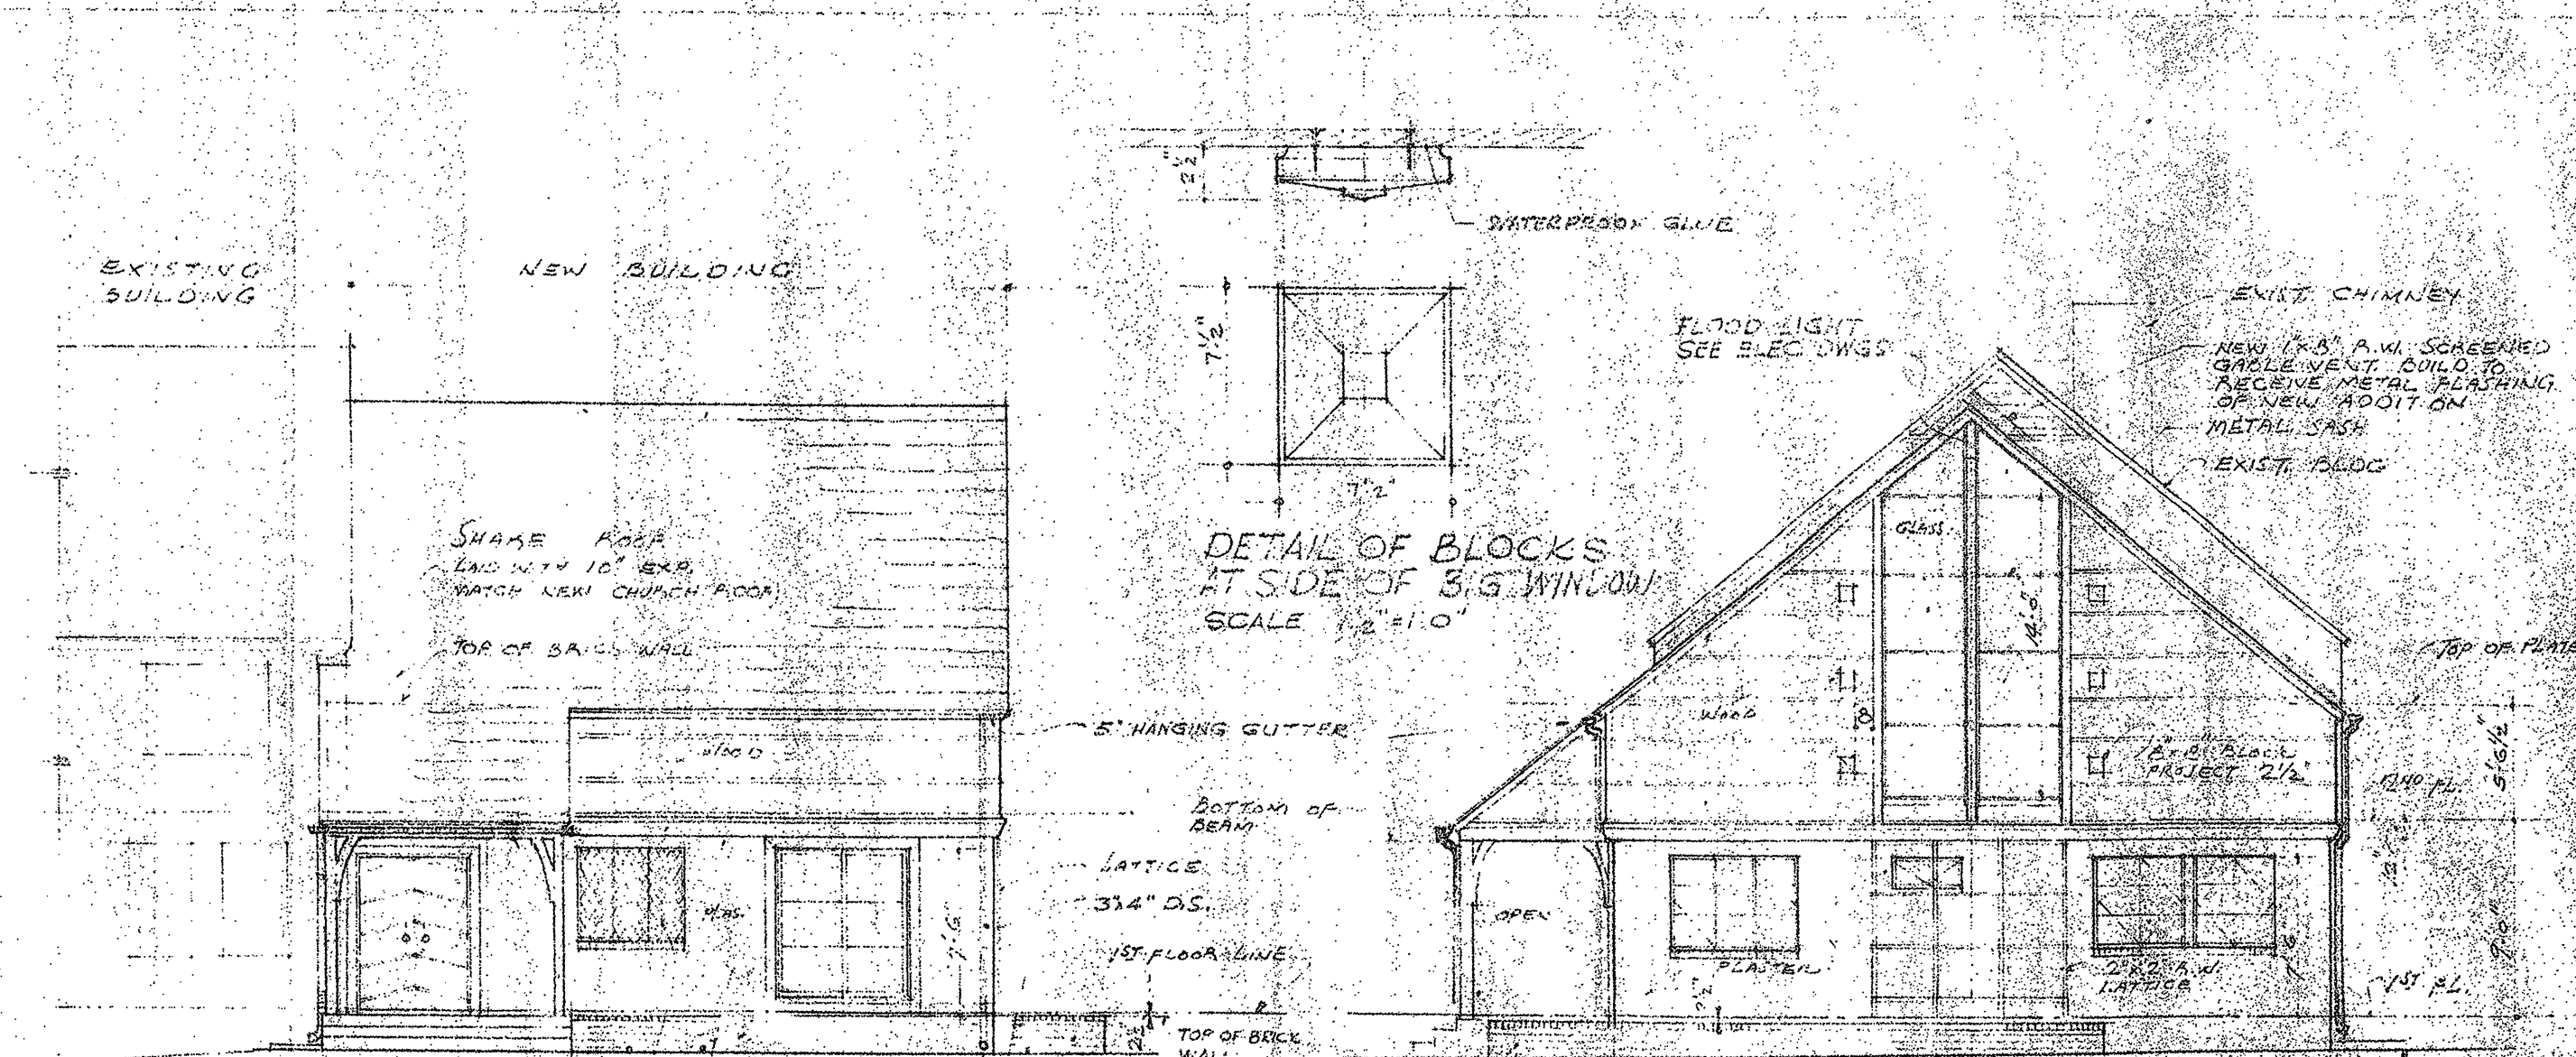
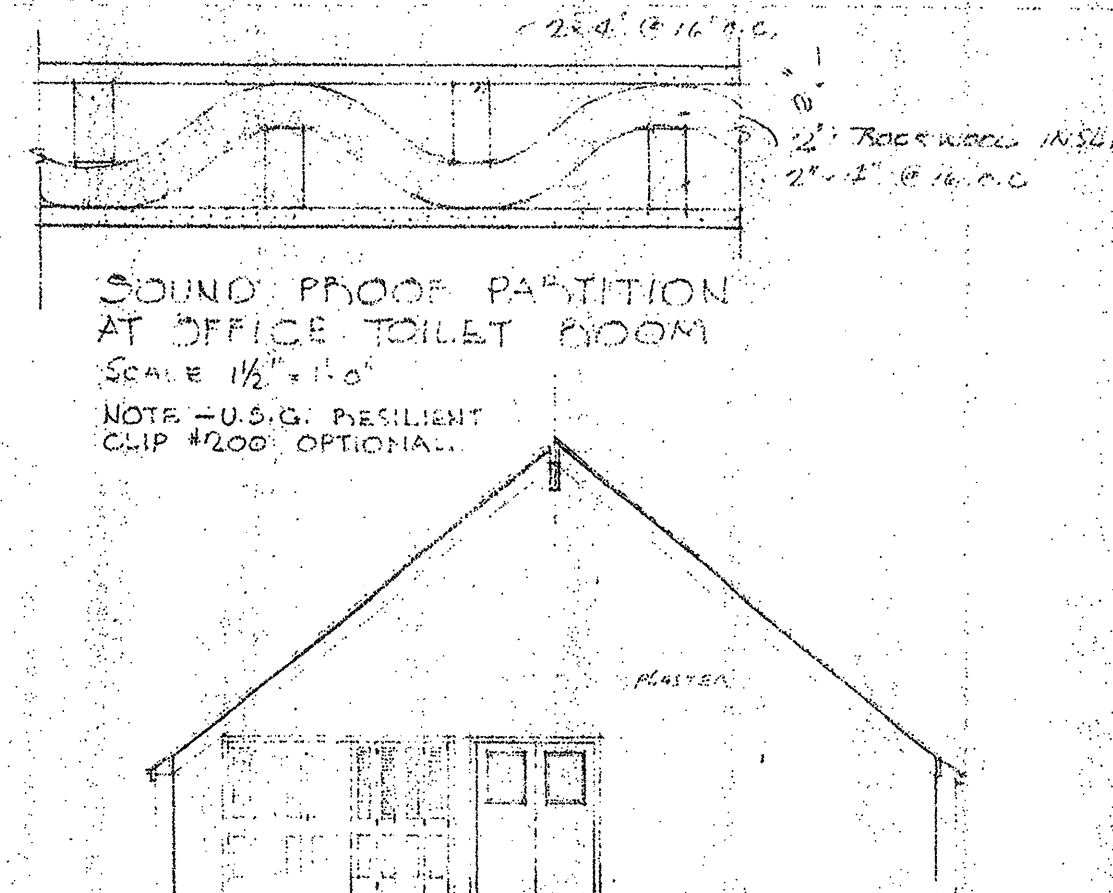


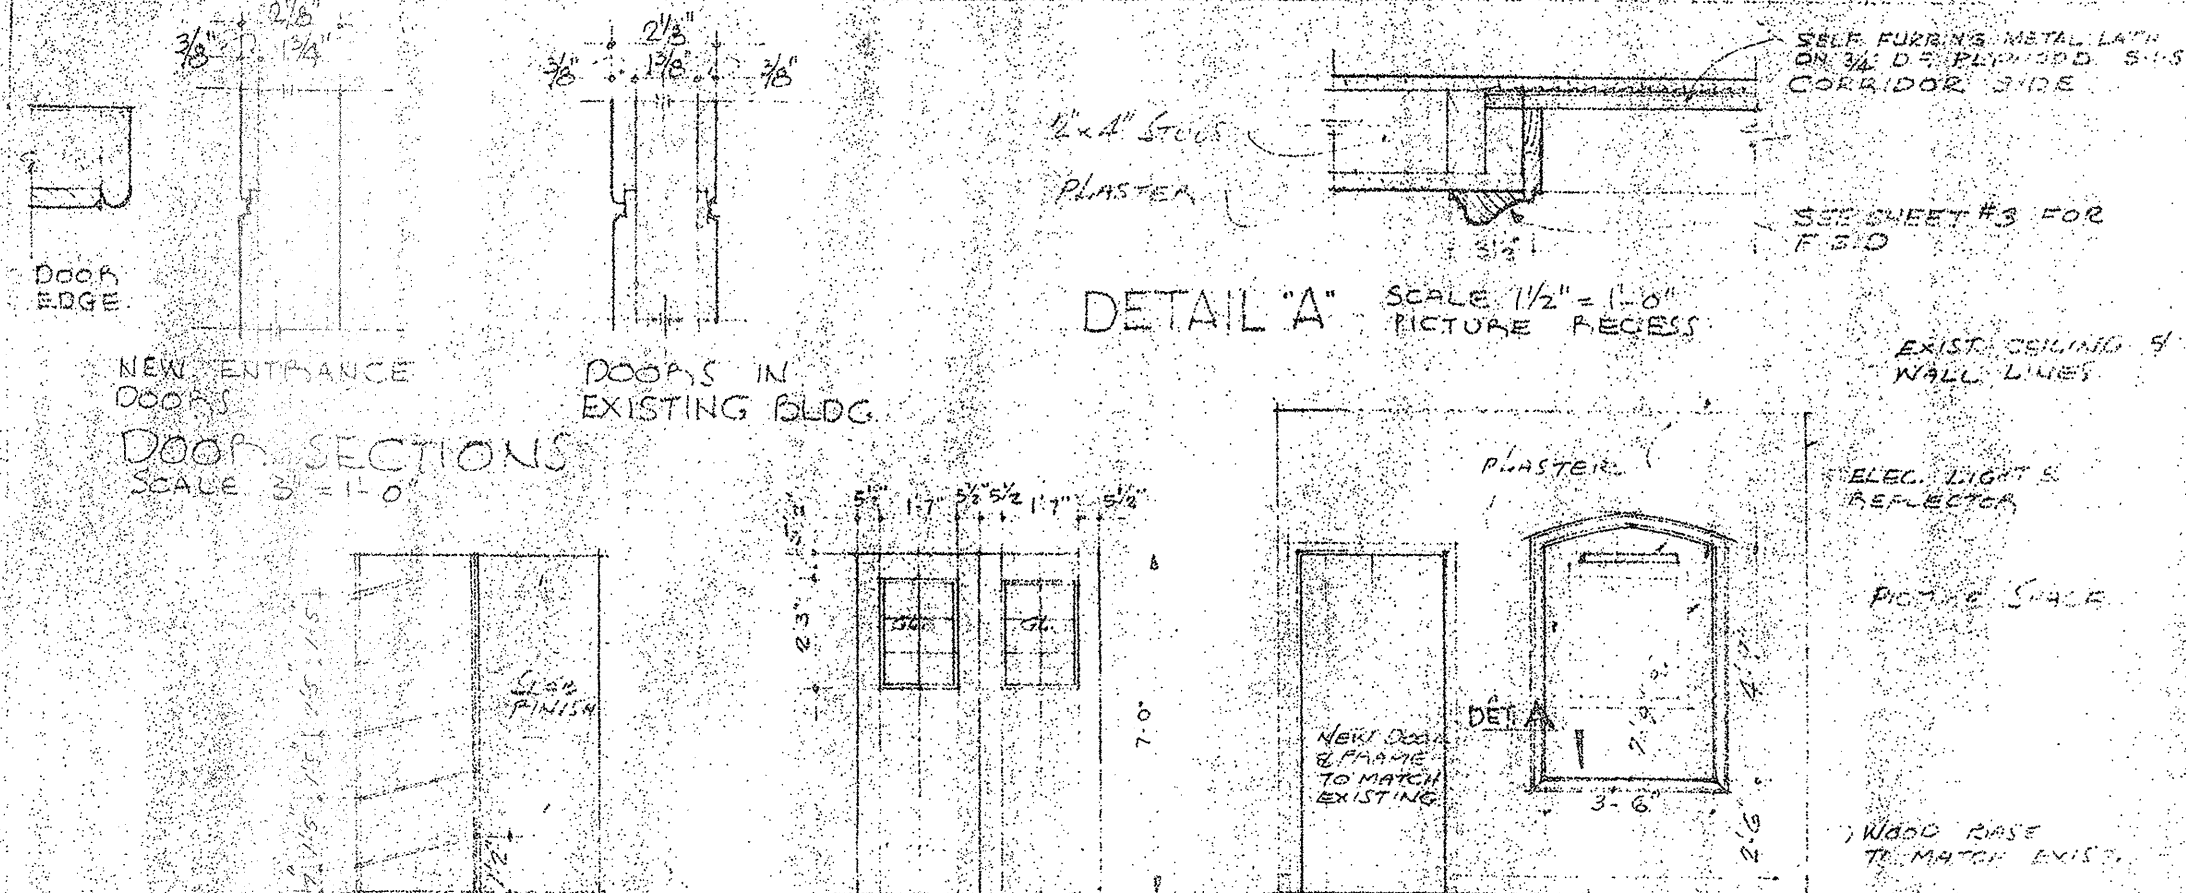


SECOND FLOOR PLAN
SCALE 1/8" = 1'-0"

- GENERAL NOTES**
1. ALL PARTITIONS, 2"x4" STUDS UNLESS OTHERWISE NOTED.
 2. ALL DIMENSIONS TO FACE OF STUDS OR FINISH.
 3. VERIFY ALL DIMENSIONS AT JOB.
 4. PLASTER WALLS TO BE STRUCK SMOOTH 4" ABOVE FLOOR TO RECEIVE RUBBER TILE BASE.
 5. ALL JOINTS IN RUNNING WOOD FINISH TO BE MITRED.
 6. ALL STRIPPING FOR ACOUSTIC TILE & SIDING TO BE SHIMED TO A STRAIGHT LINE.
 7. ALL ACOUSTIC TILE TO BE SCQUIRED TO WALLS & BEAMS.
 8. ALL SMOOTH PLASTER WALLS TO HEAVY STIPPLE PAINTED FINISH.
 9. SIZE, LOCATIONS & DEPTHS OF ALL EXISTING PLUMBING LINES INVOLVED IN THE WORK SHALL BE VERIFIED IN FIELD.
 10. FLOOR FINISH
FIRST FLOOR - "C" GROUP ASPHALT TILE IN OFFICES & HALL.
VINYL TILE IN OFFICE TOILET (FLOORING IN SETBACK).
JEMENT FLOOR IN LOWER TOILET & ENTRY.
RUBBER BASE FOR ALL FIRST FLOOR RESIDENT FLOORING TO BE MAINTAINED 6" HIGH.
STAIRS - HANDWOOD, EXPOSED TREADS & RISERS, WOOSTER NOSEINGS.
SECOND FLOOR - "C" GROUP ASPHALT TILE & WOOD BASE.
 11. FINISH HARDWARE FOR NEW ADDITION TO BE MASTER KEVED TO EXTG. SYSTEM.

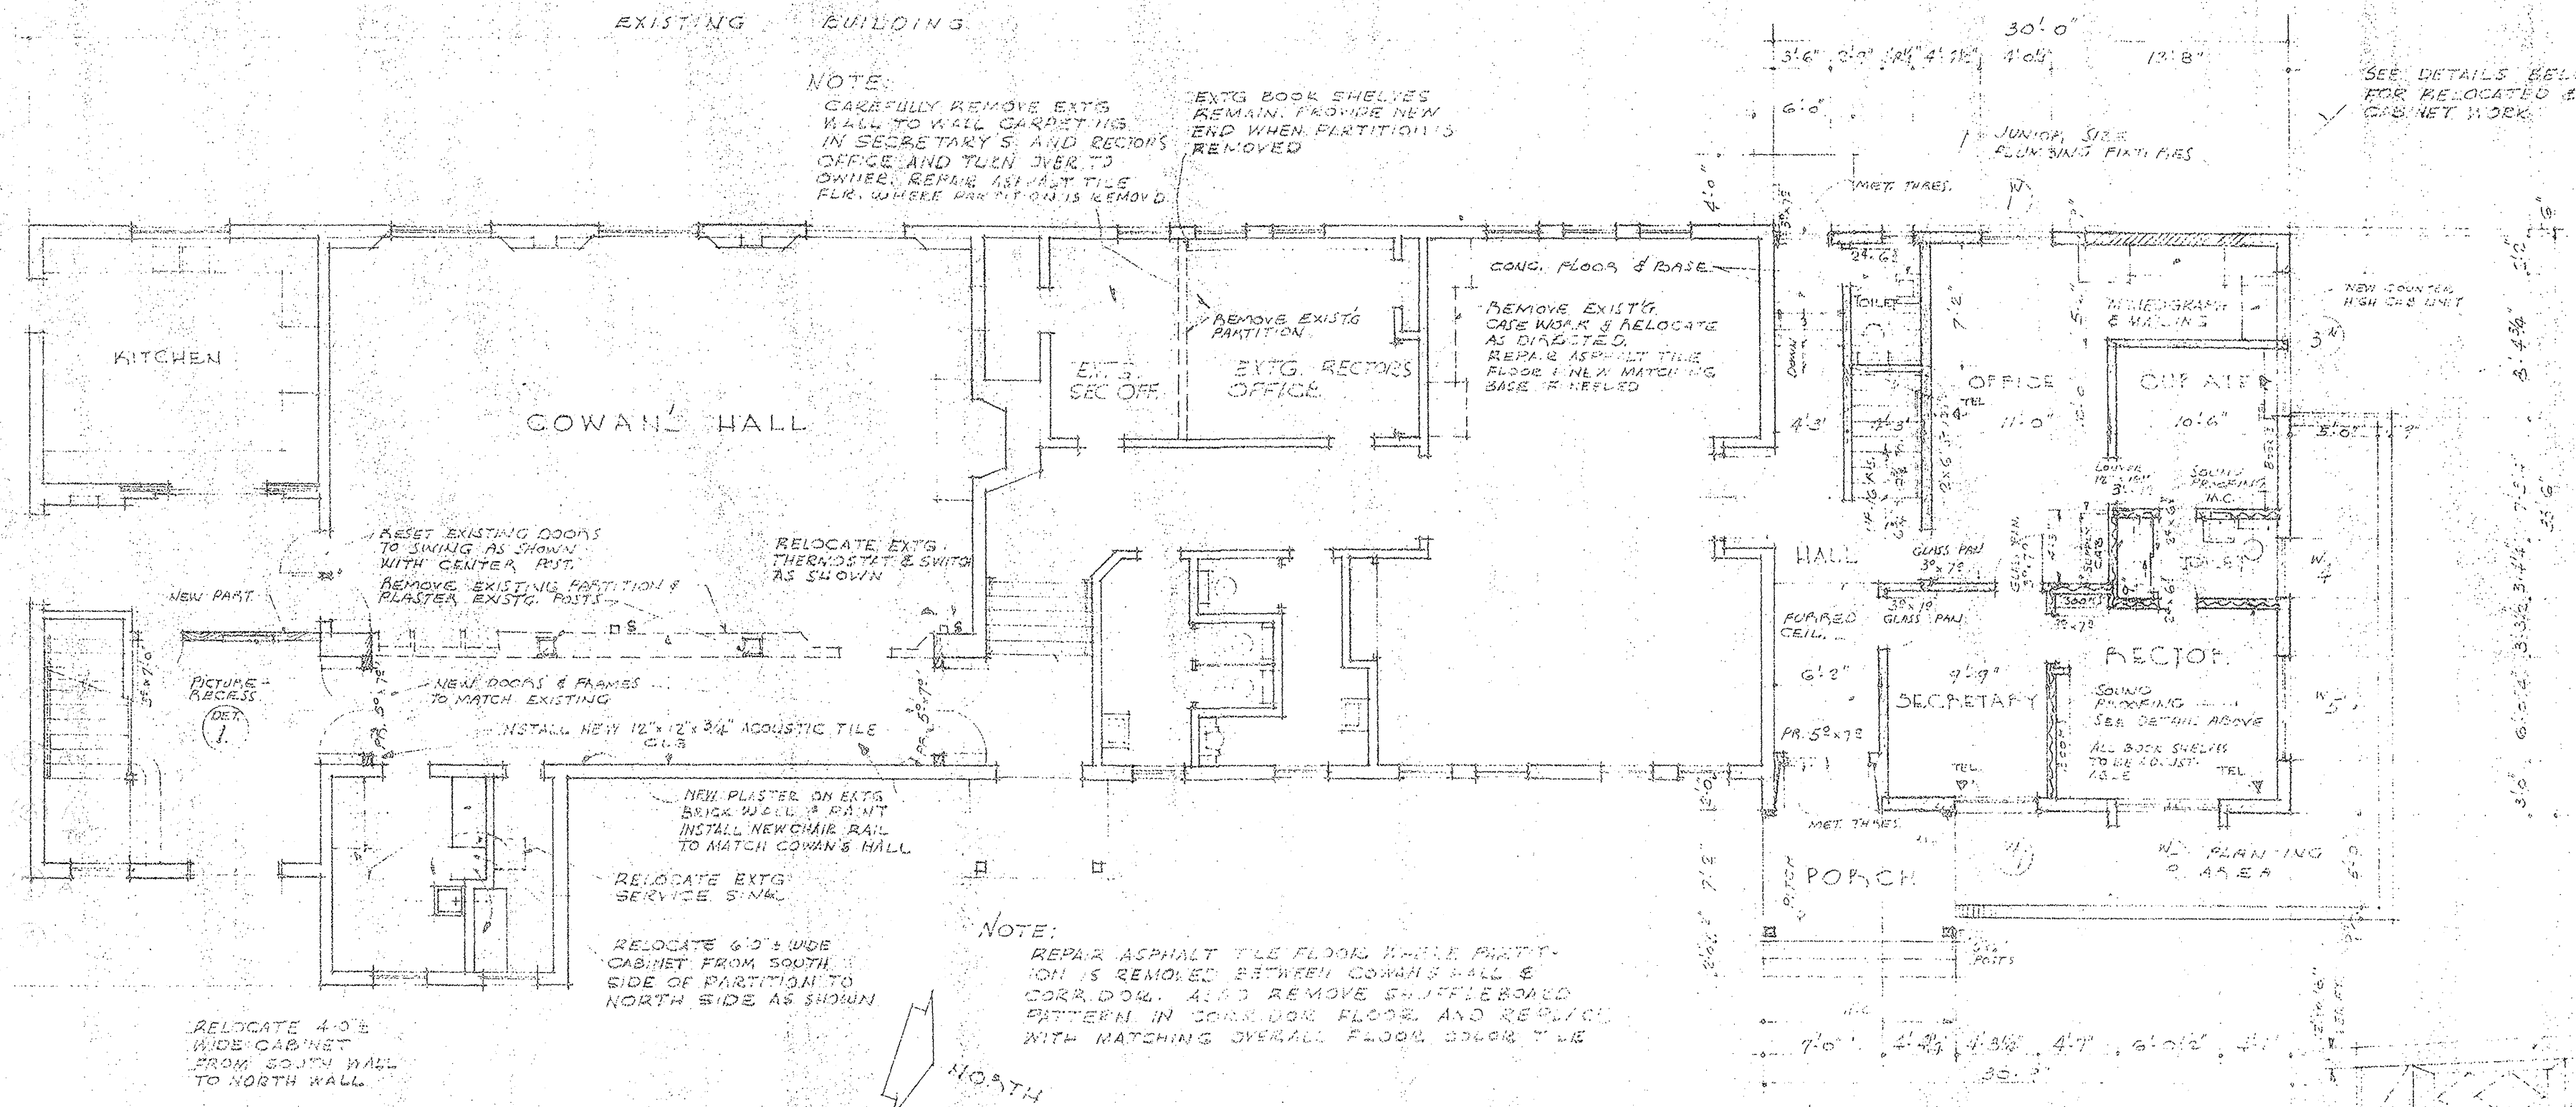

FIRST FLOOR PLAN
SCALE 1/8" = 1'-0"

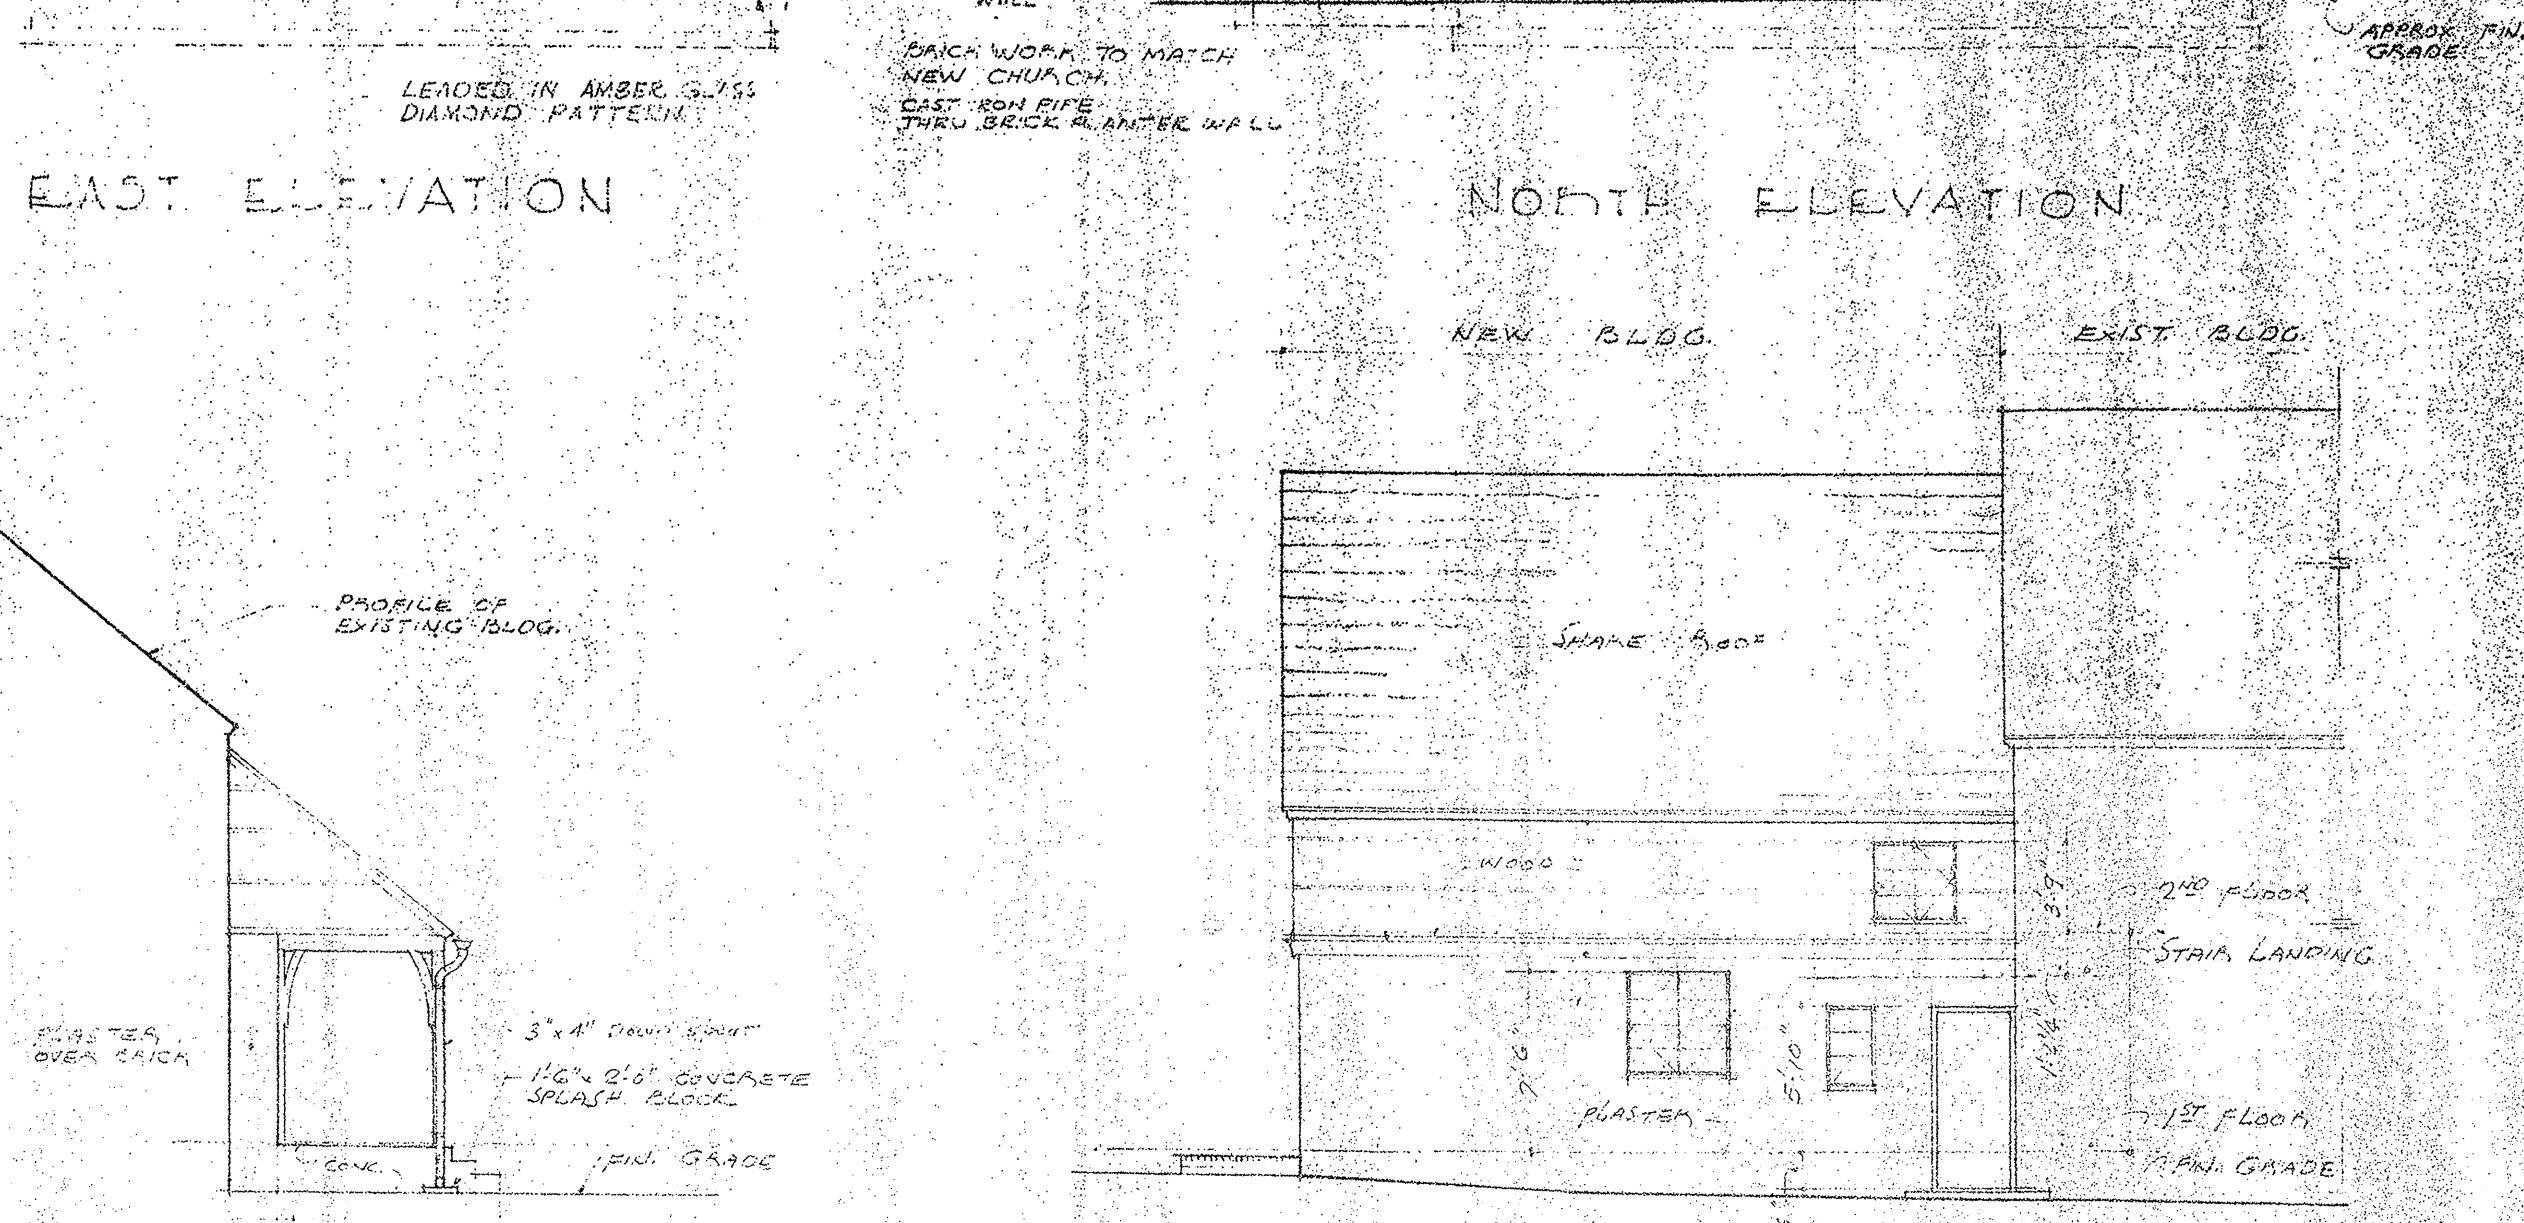

ALTERATIONS & ADDITIONS TO PARISH HALL
ST. EDMUNDS EPISCOPAL CHURCH
HUNTINGTON DRIVE & SAN GABRIEL AVE
SAN MARINO, CALIF.

AUSTIN FIELD & TRY
architects A.I.A.

2311 WEST THIRD STREET LOS ANGELES 5, CALIFORNIA DUNKIRK 8-1326

DATE 7-11-54
COMM 1157
DRAWN J. DANIELS
CHECK
SHEET 1