
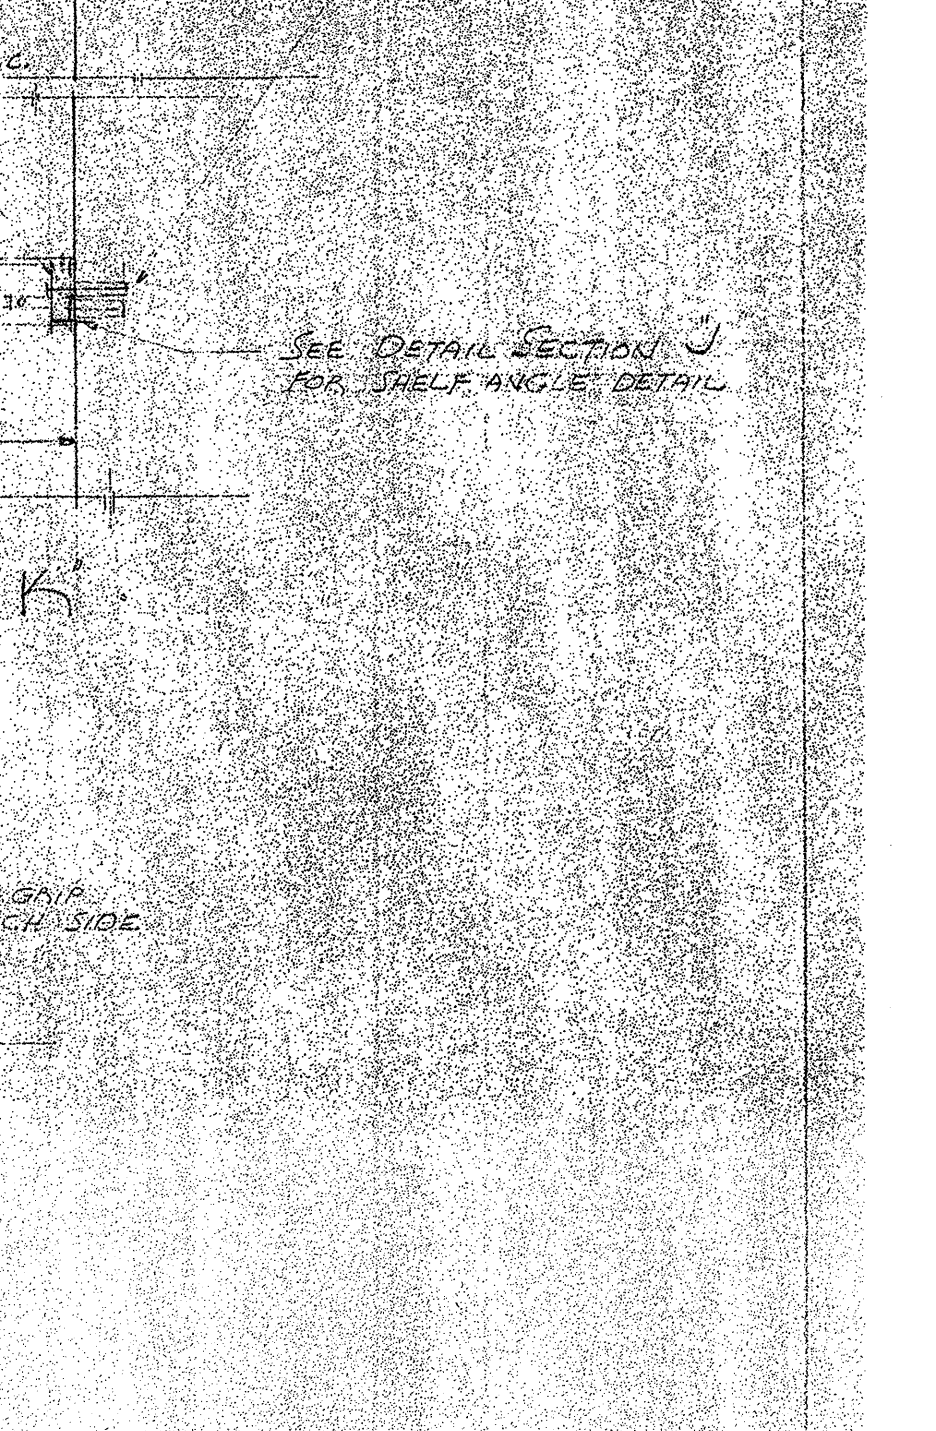
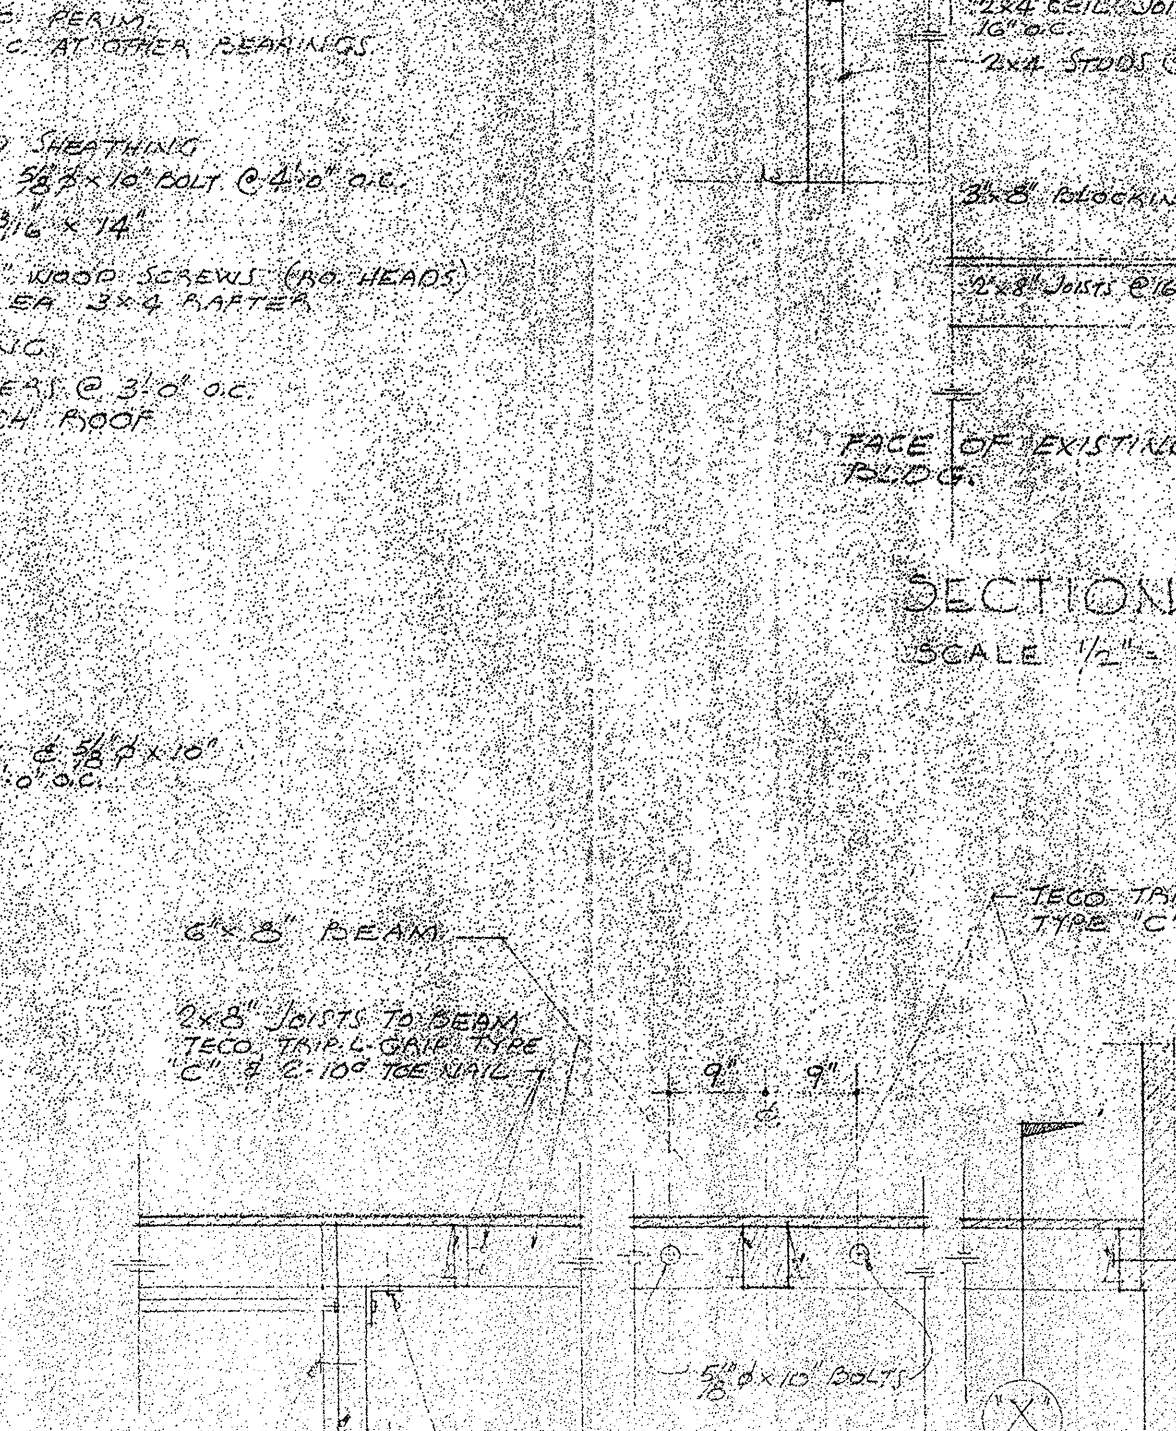
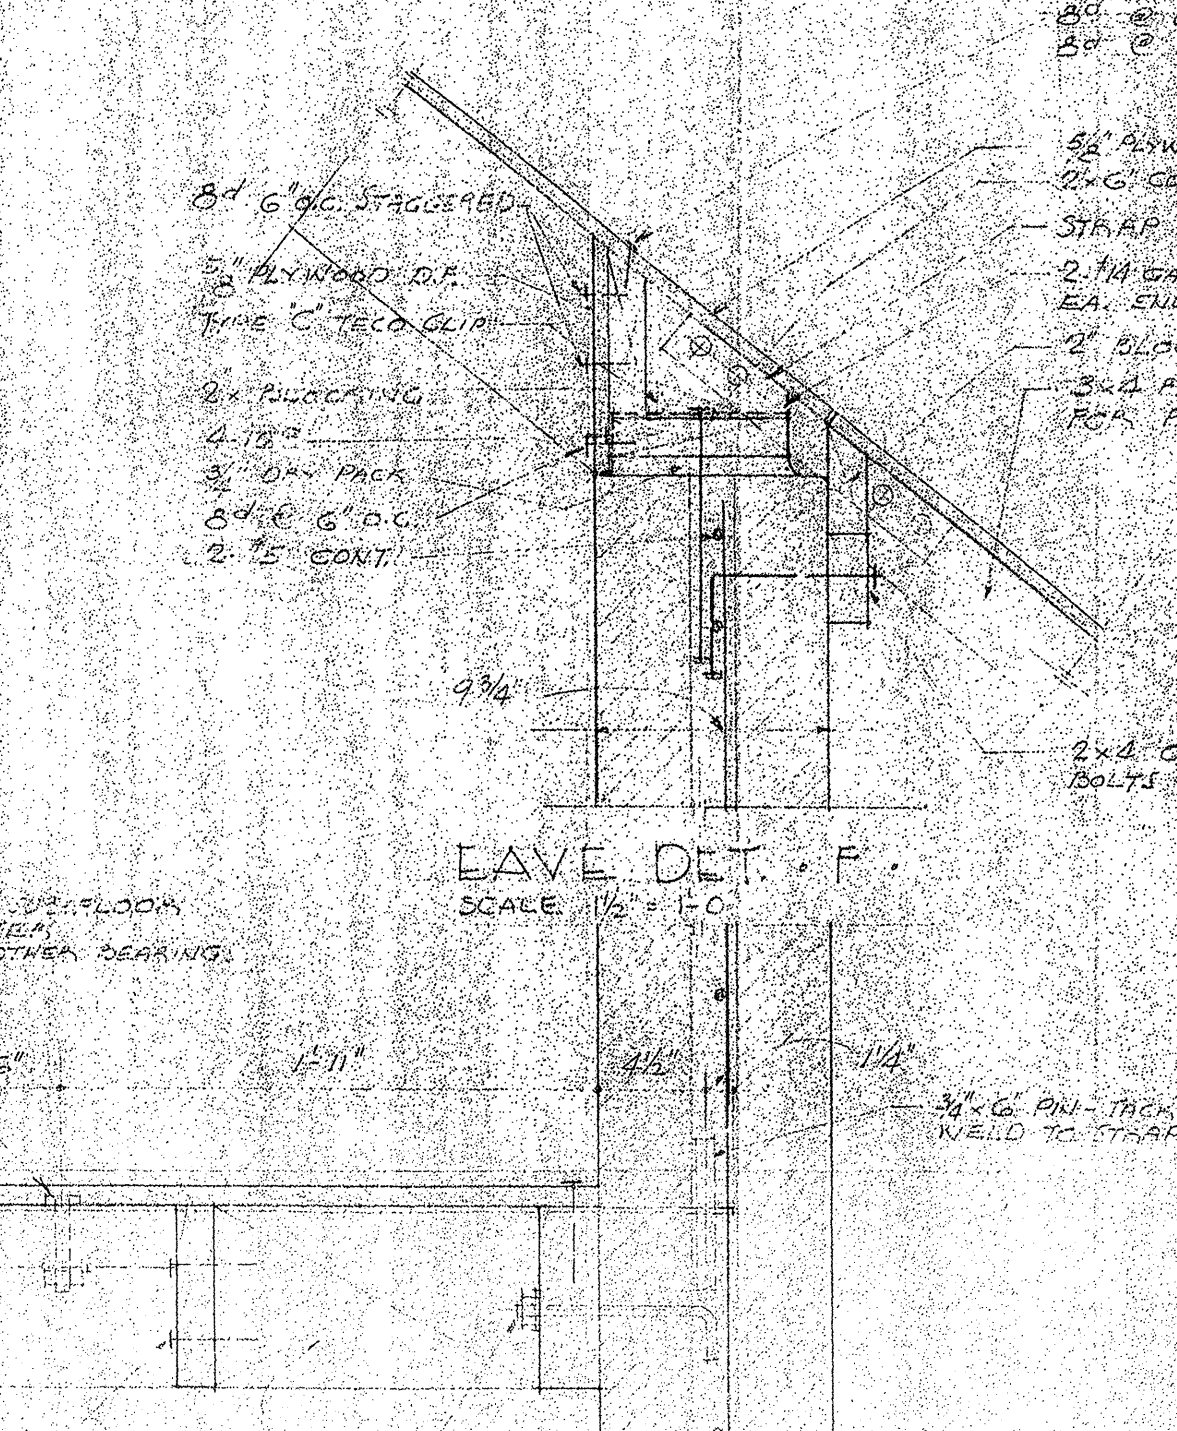
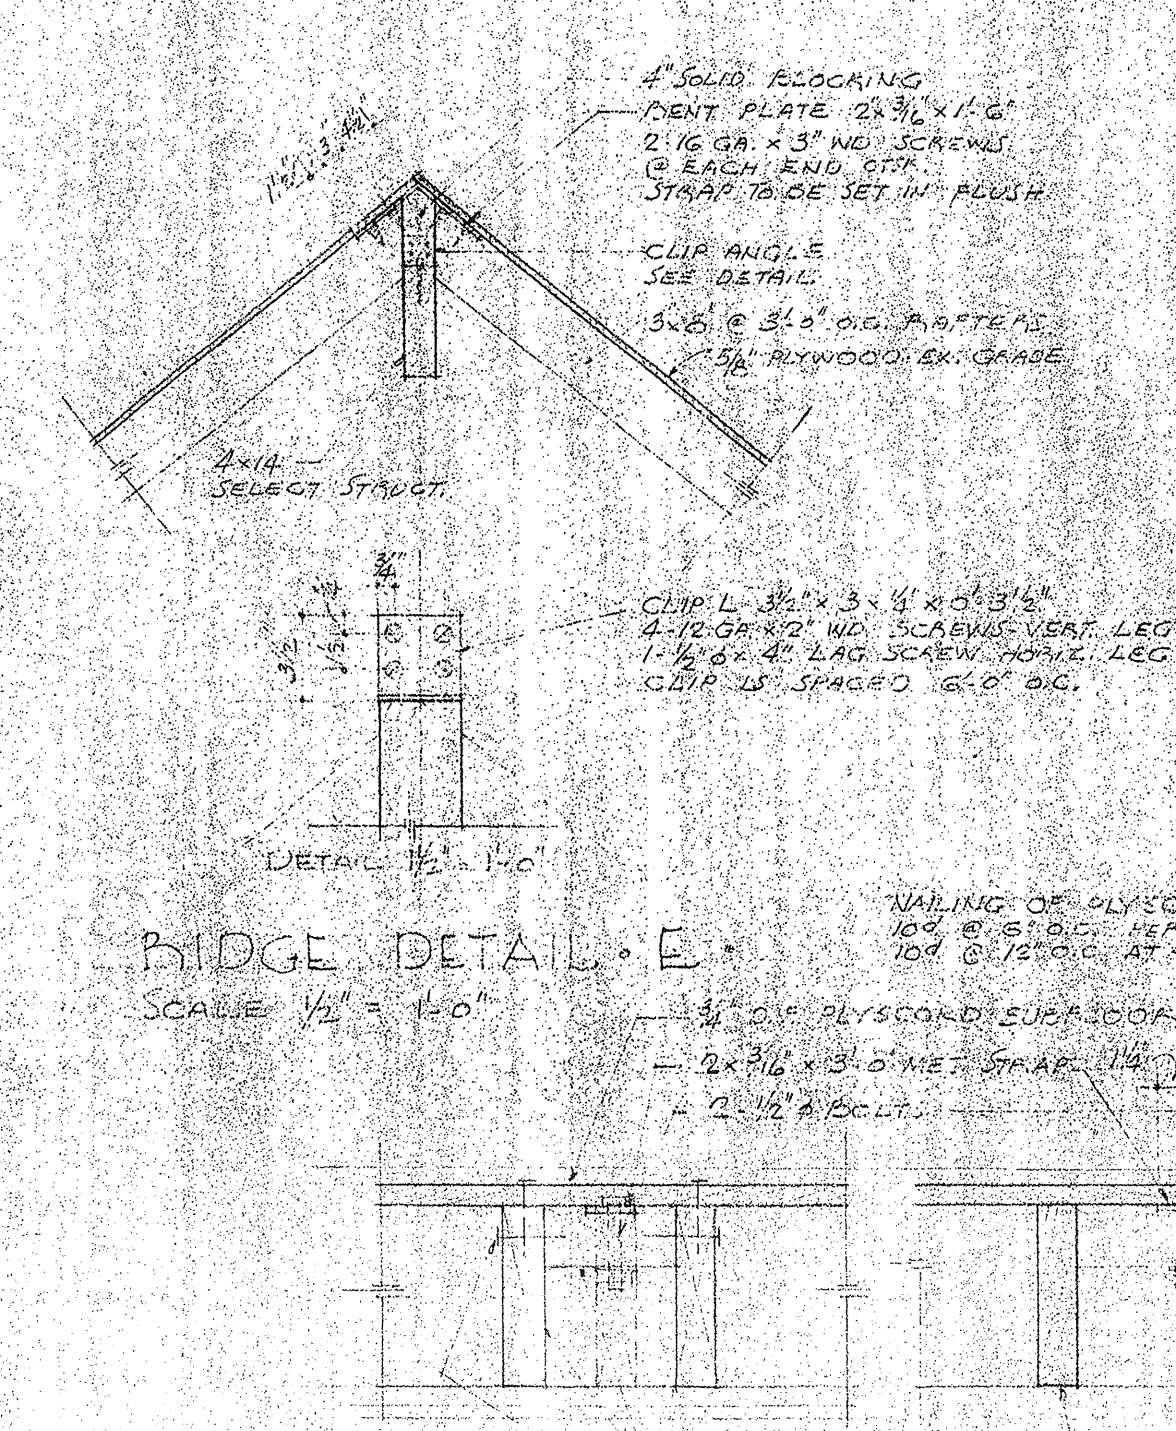
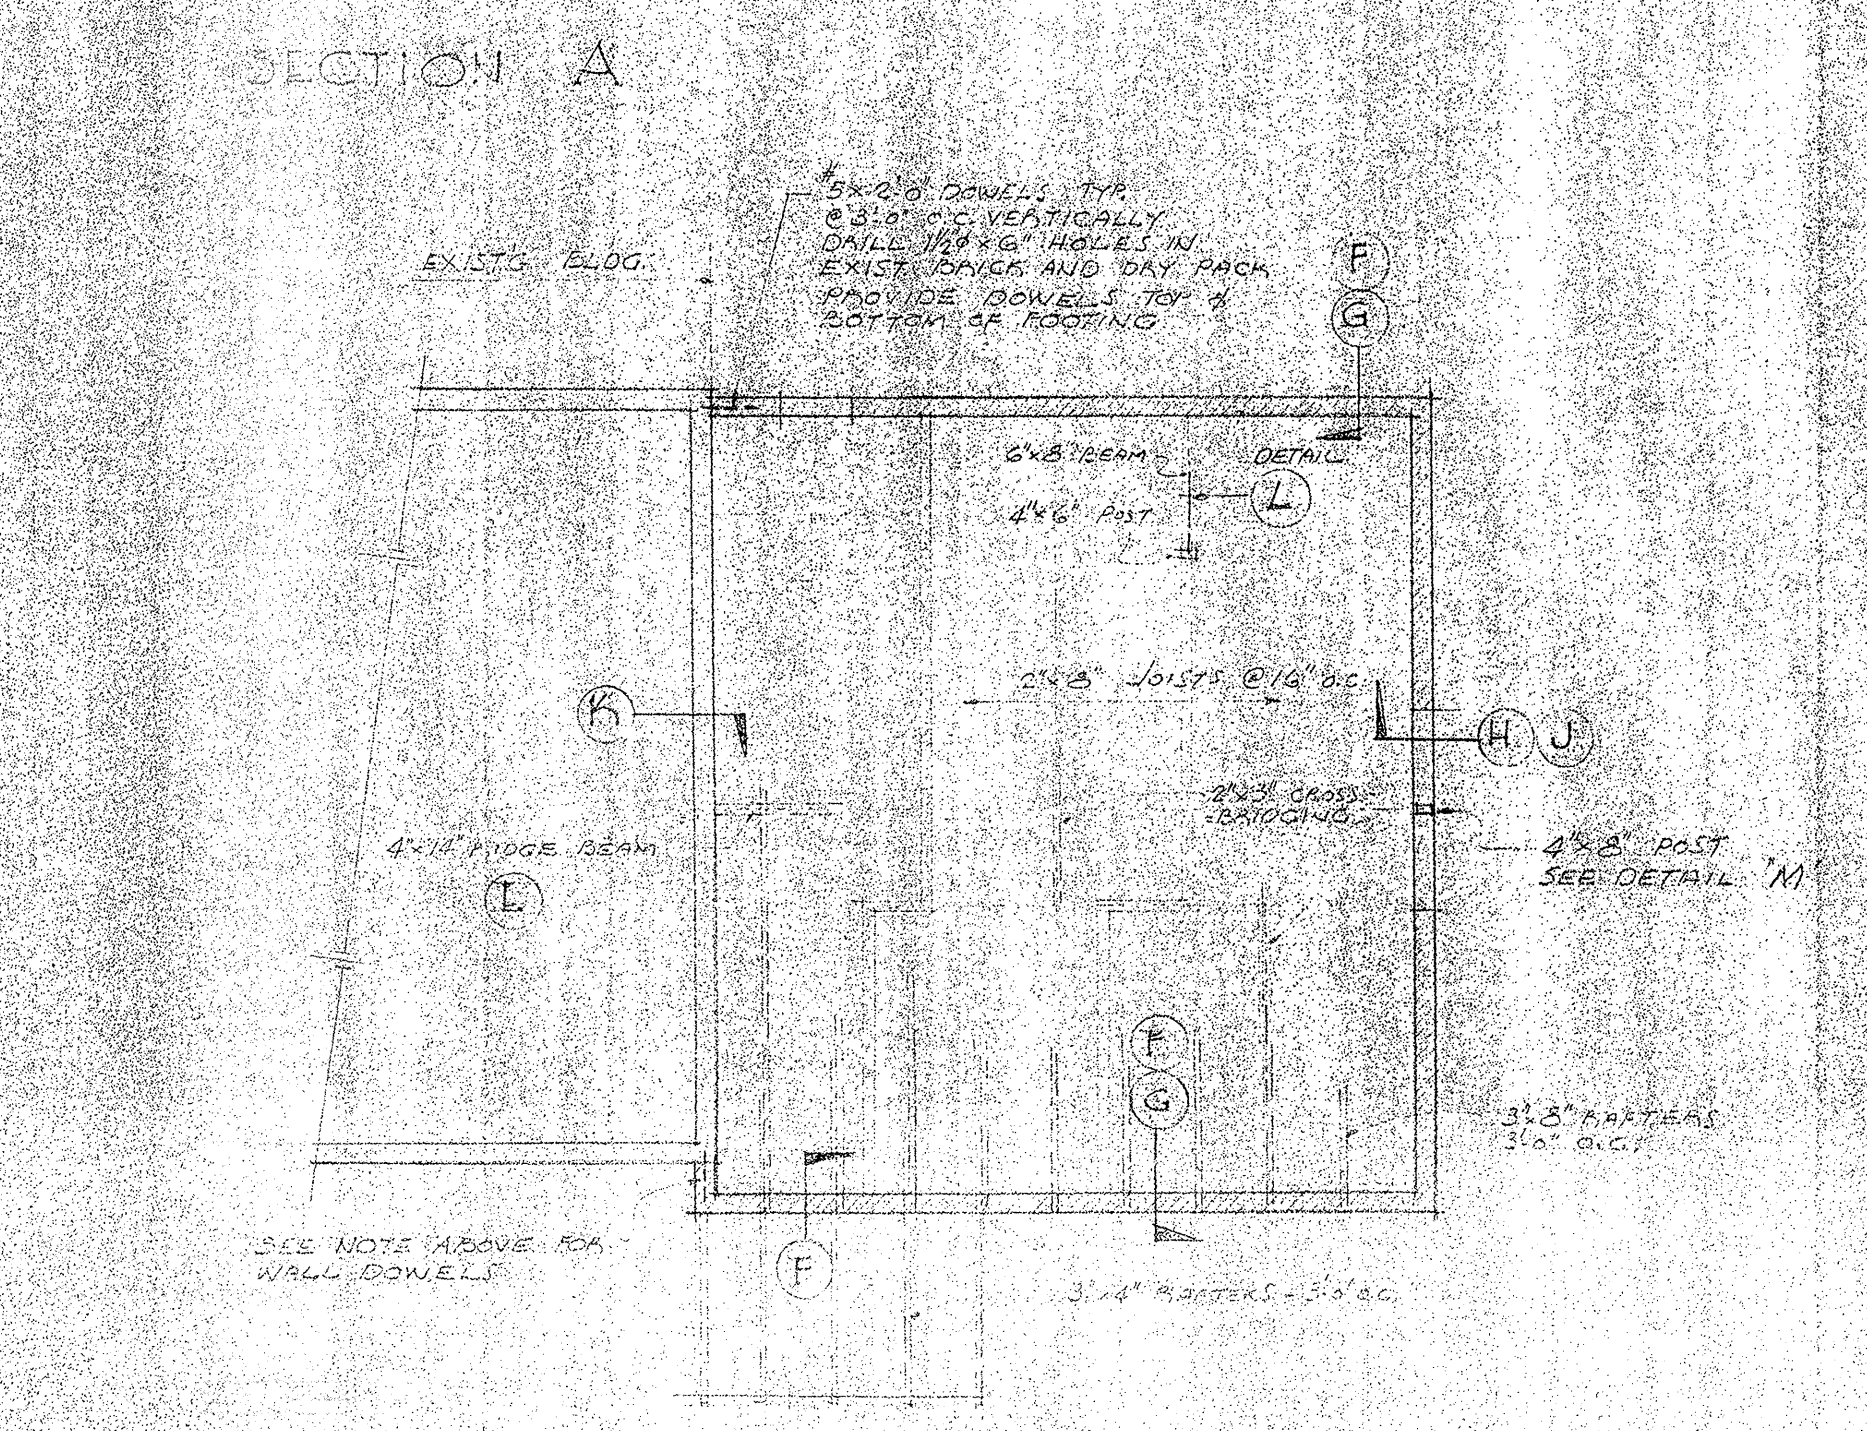
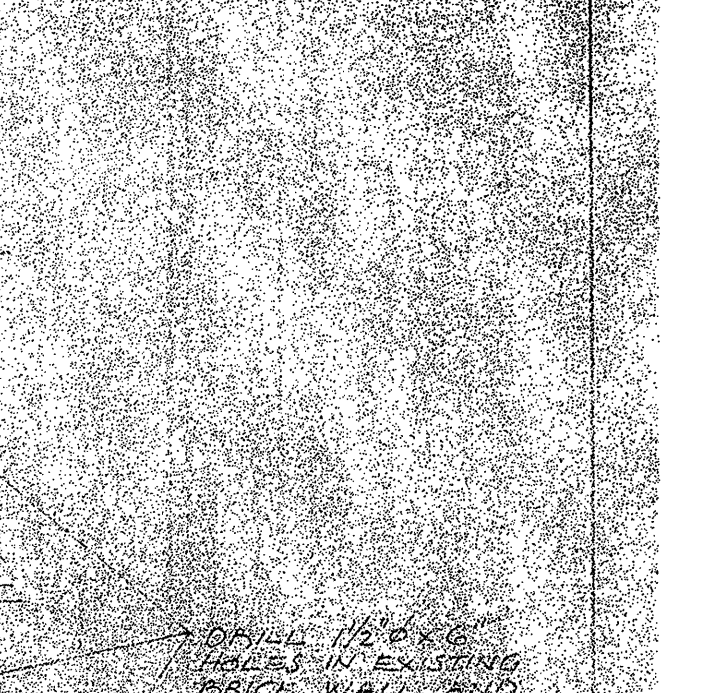
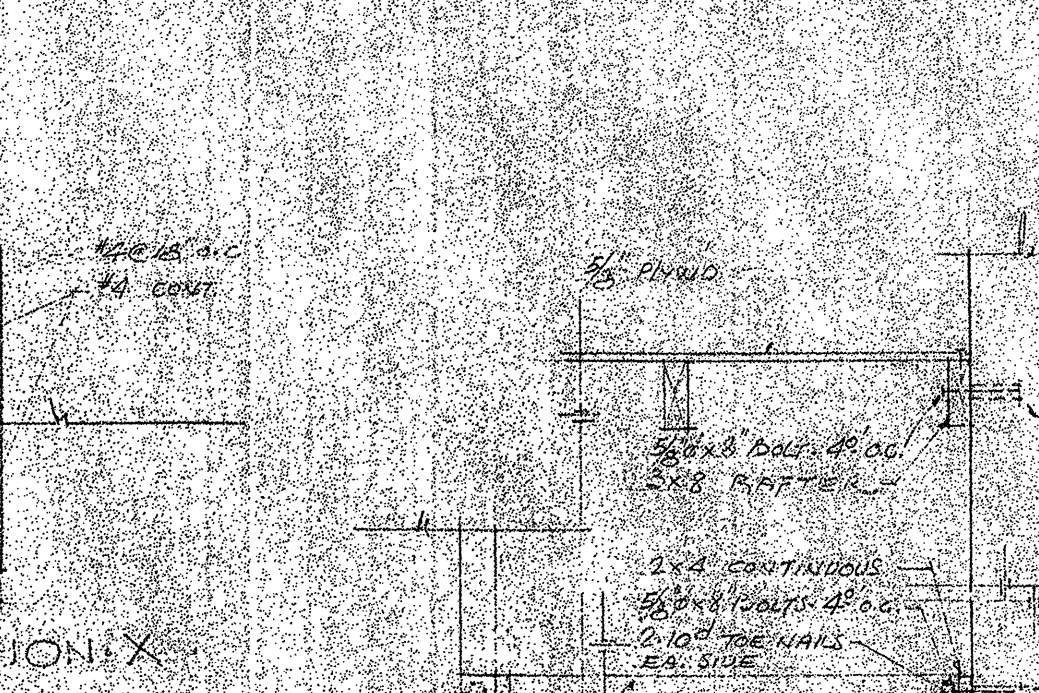
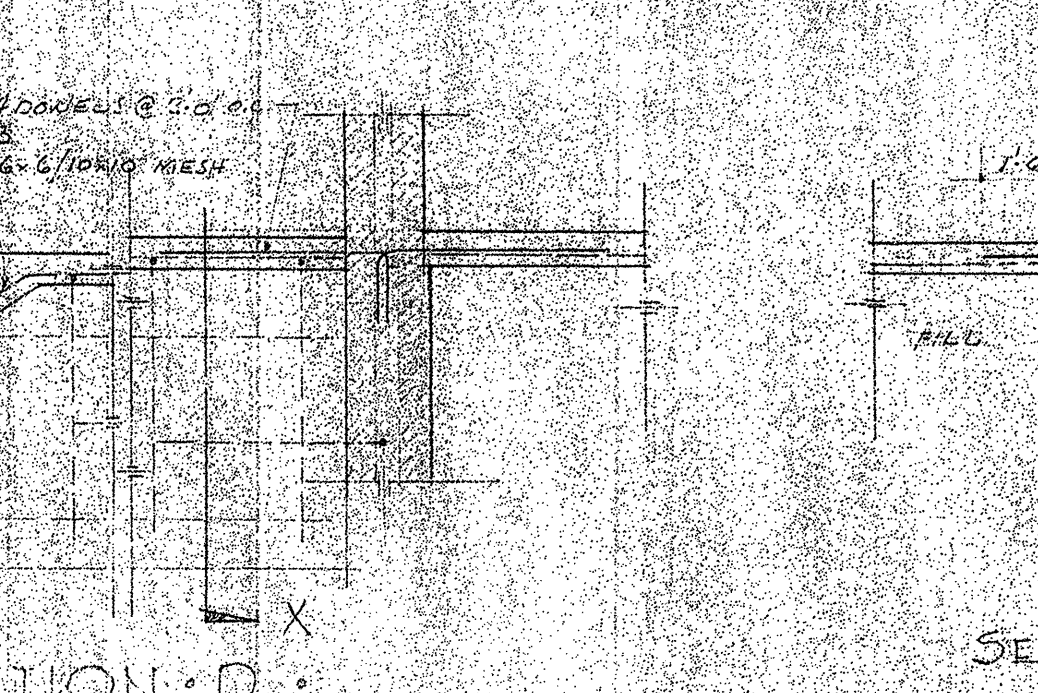
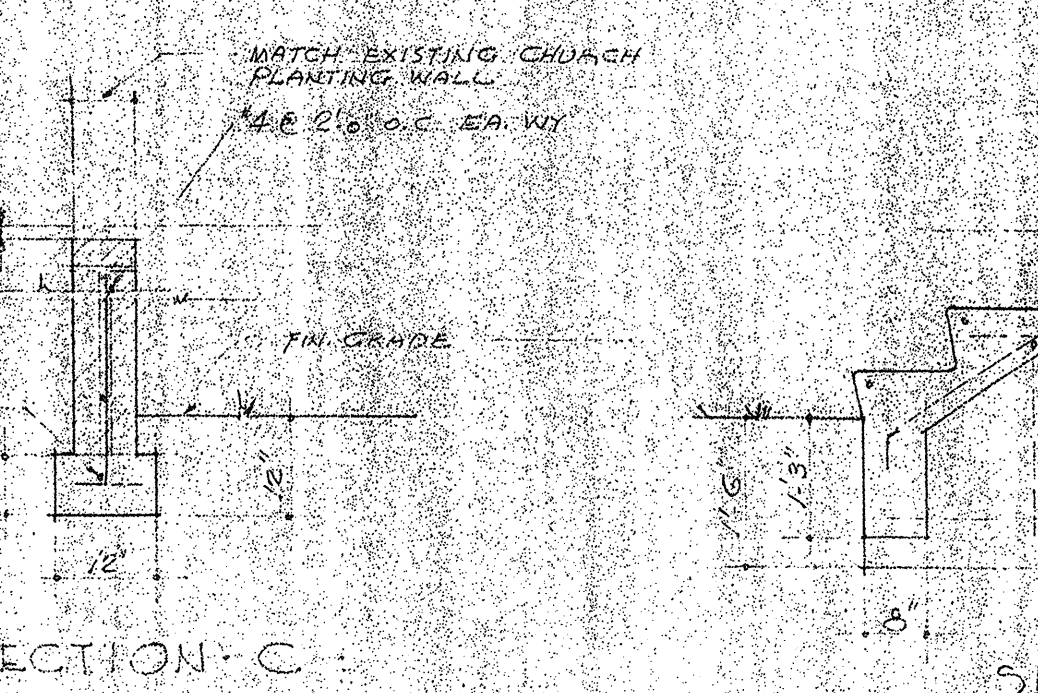
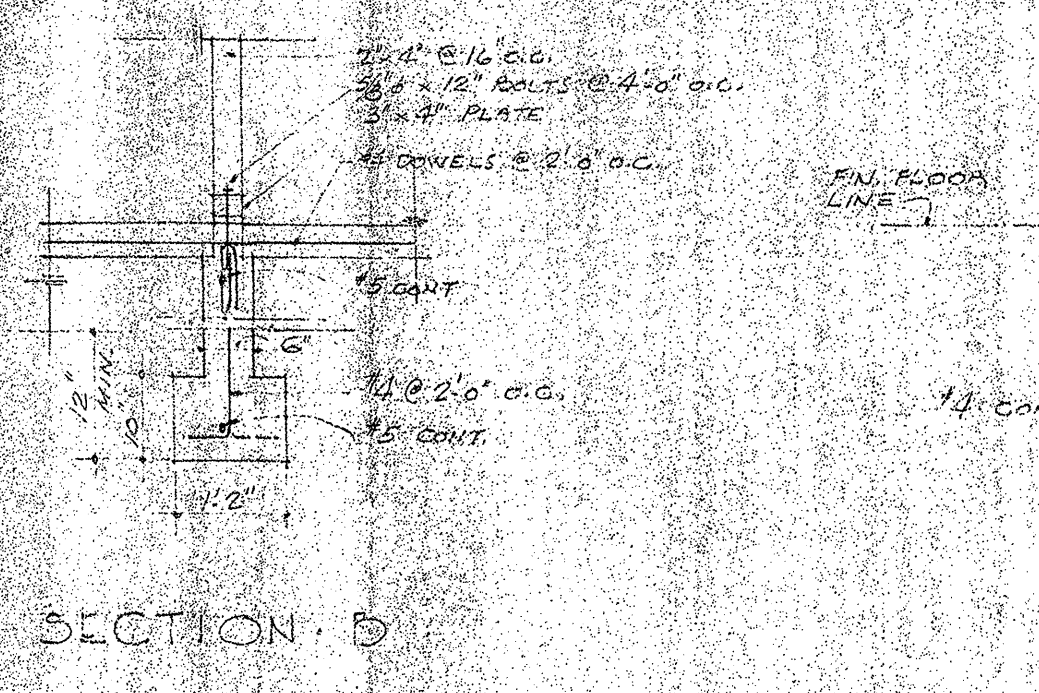


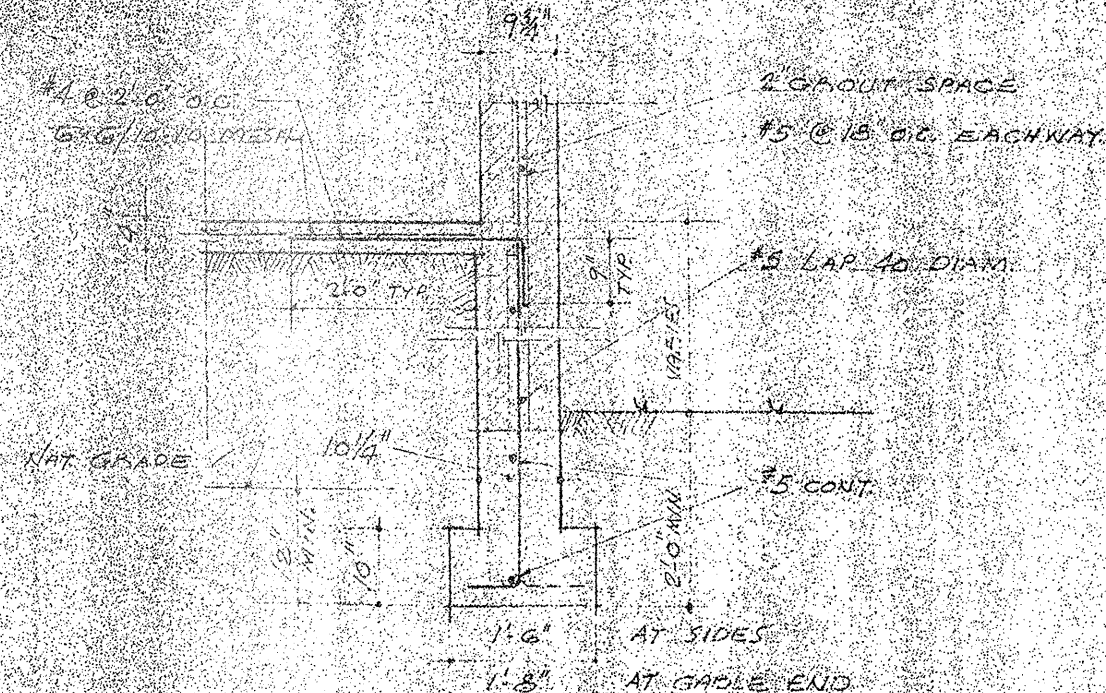

SECOND FLOOR & ROOF FRAMING

SECTION H

SECTION I

SECTION J

SECTION K






SECTION G

SECTION H

SECTION I

SECTION J

SECTION K

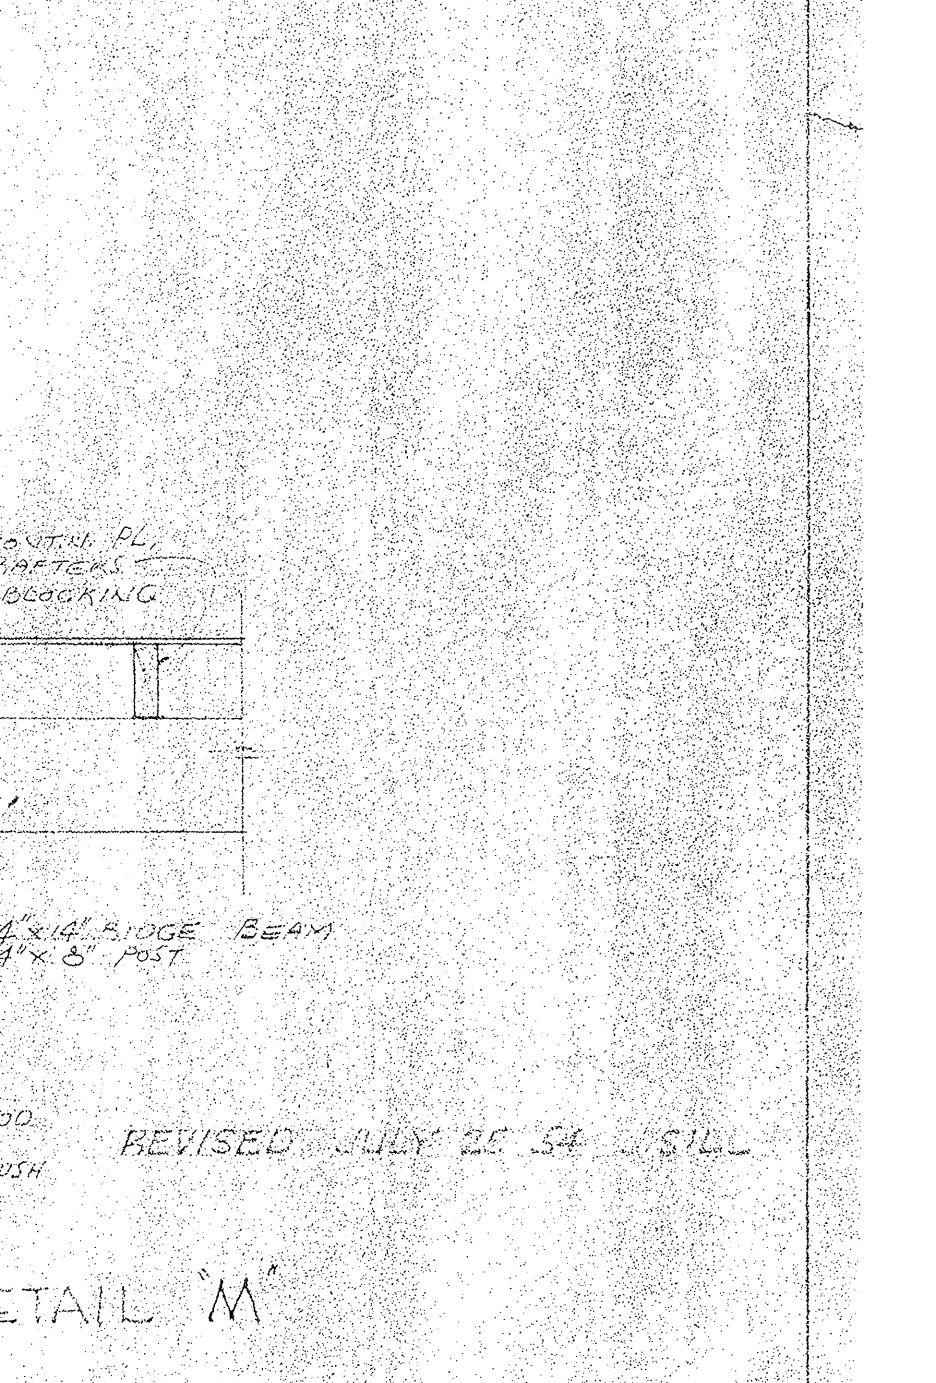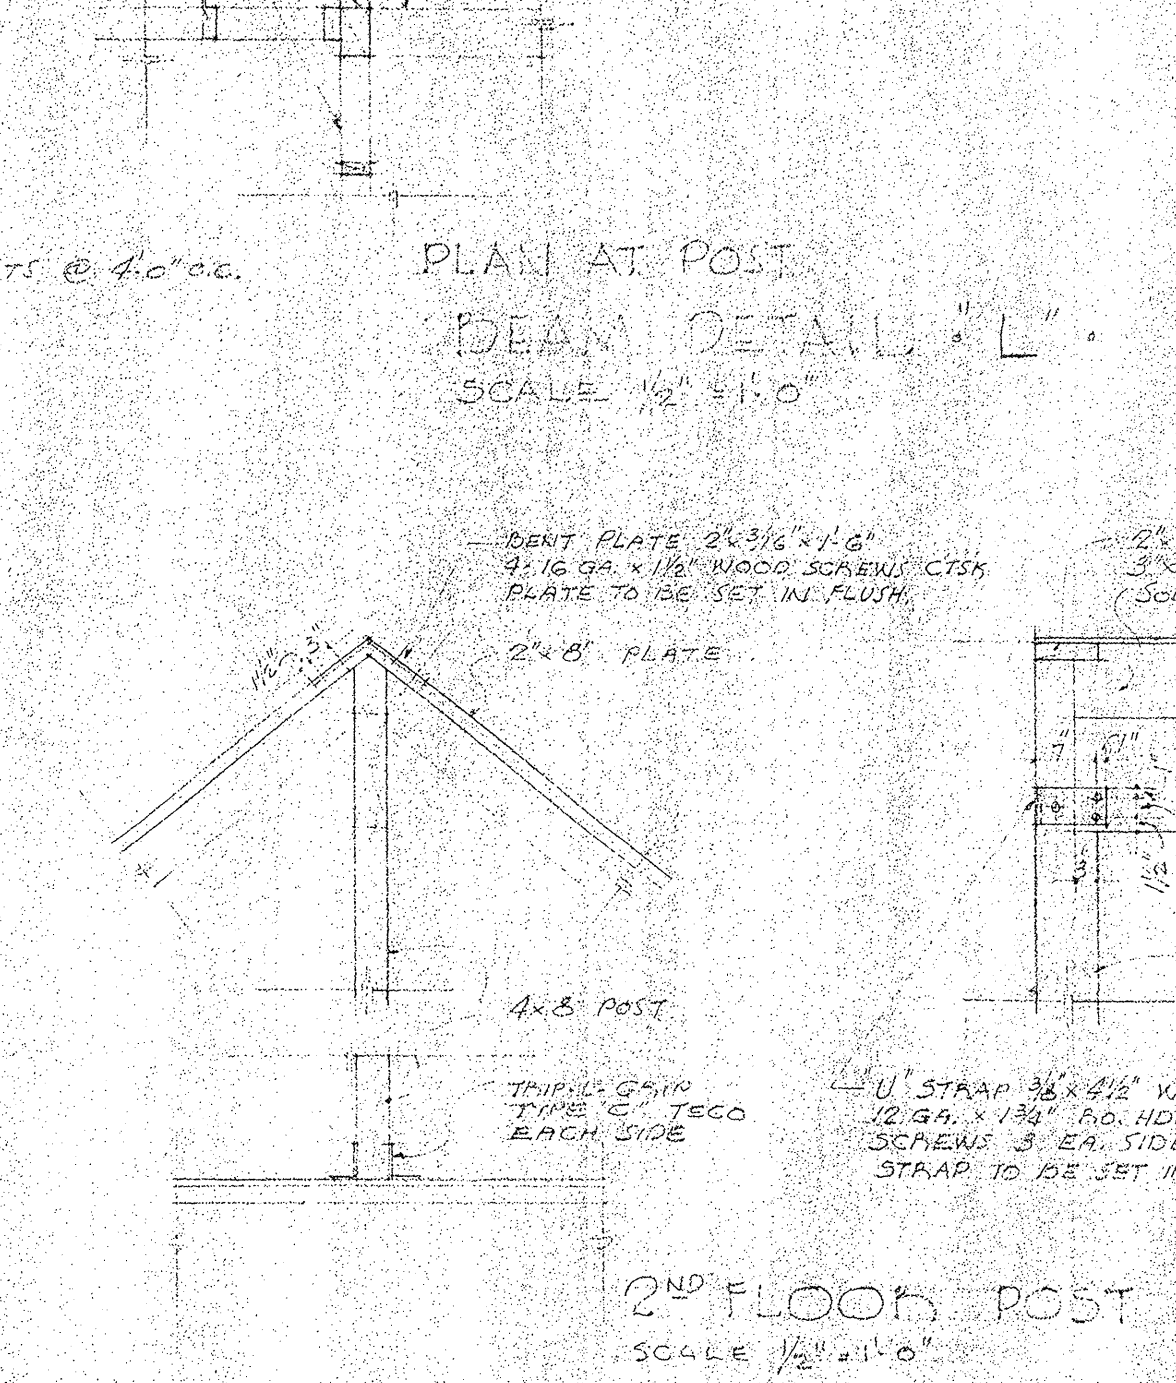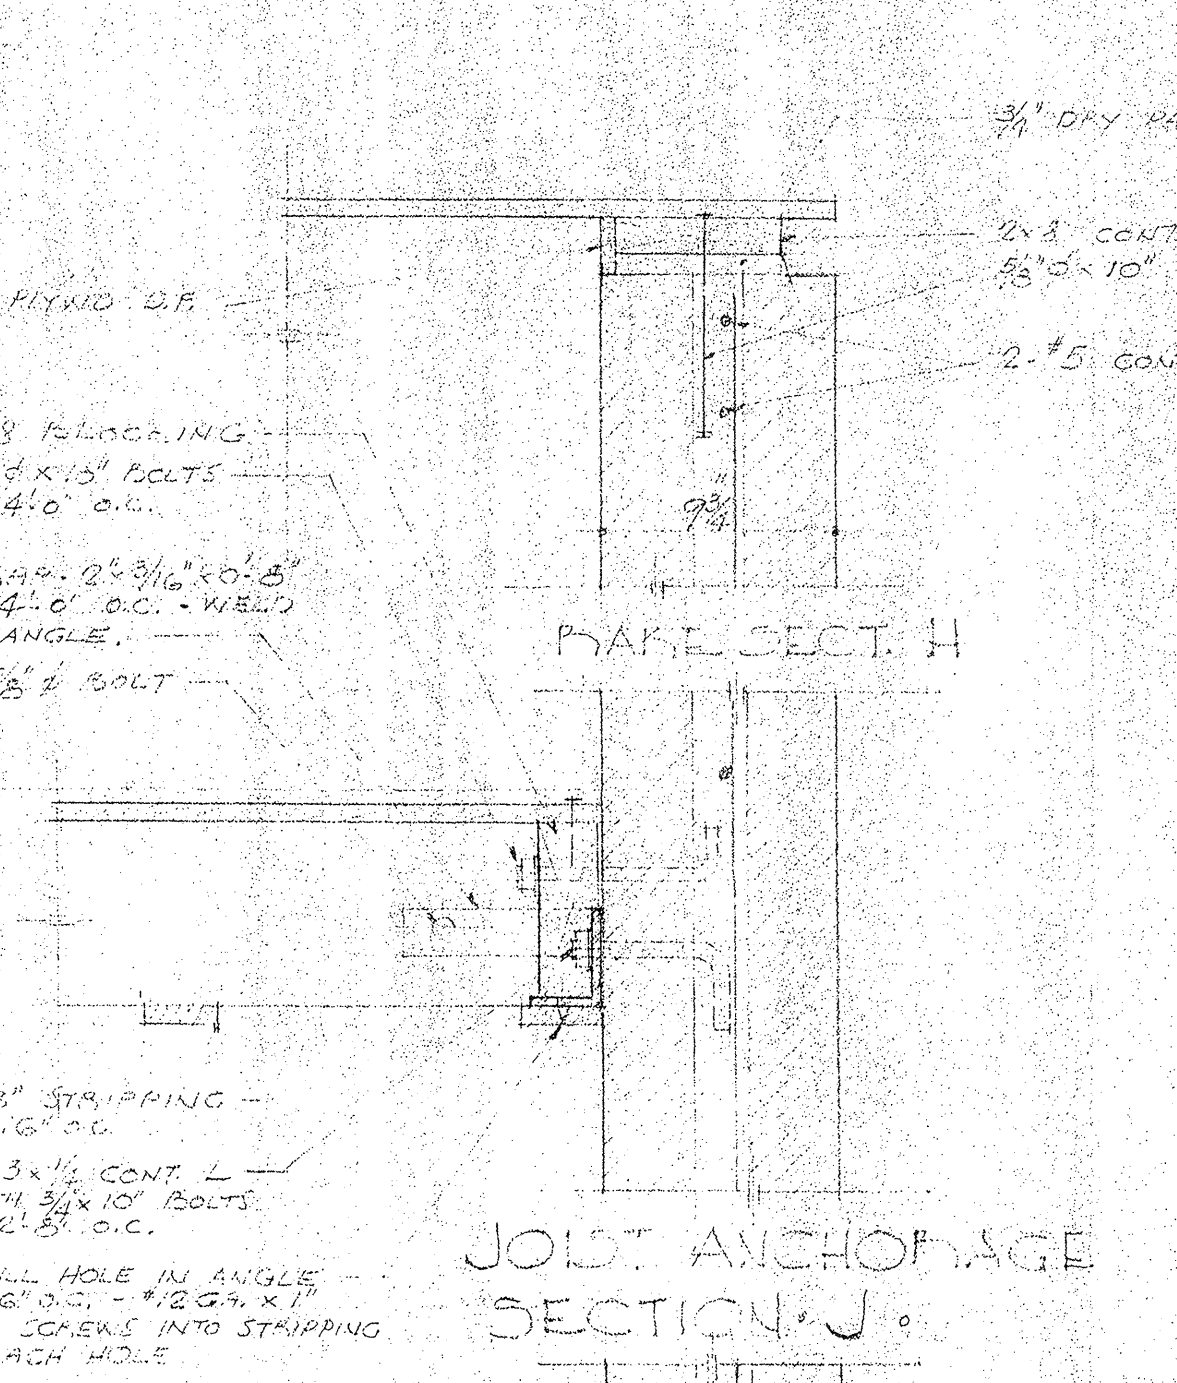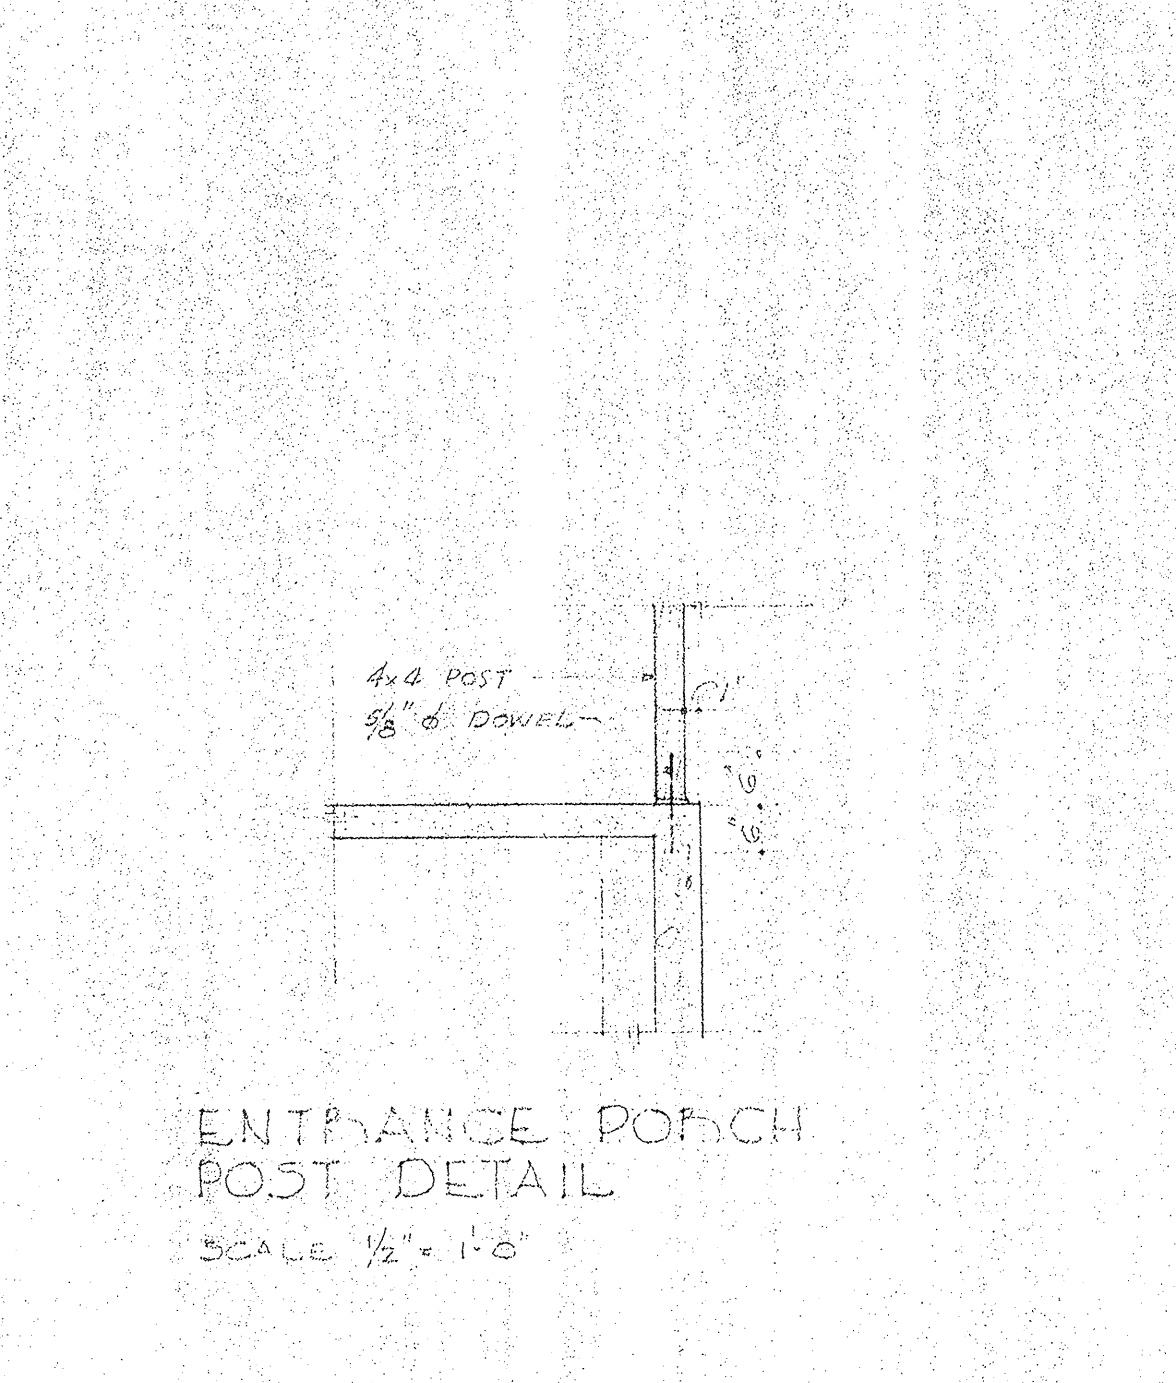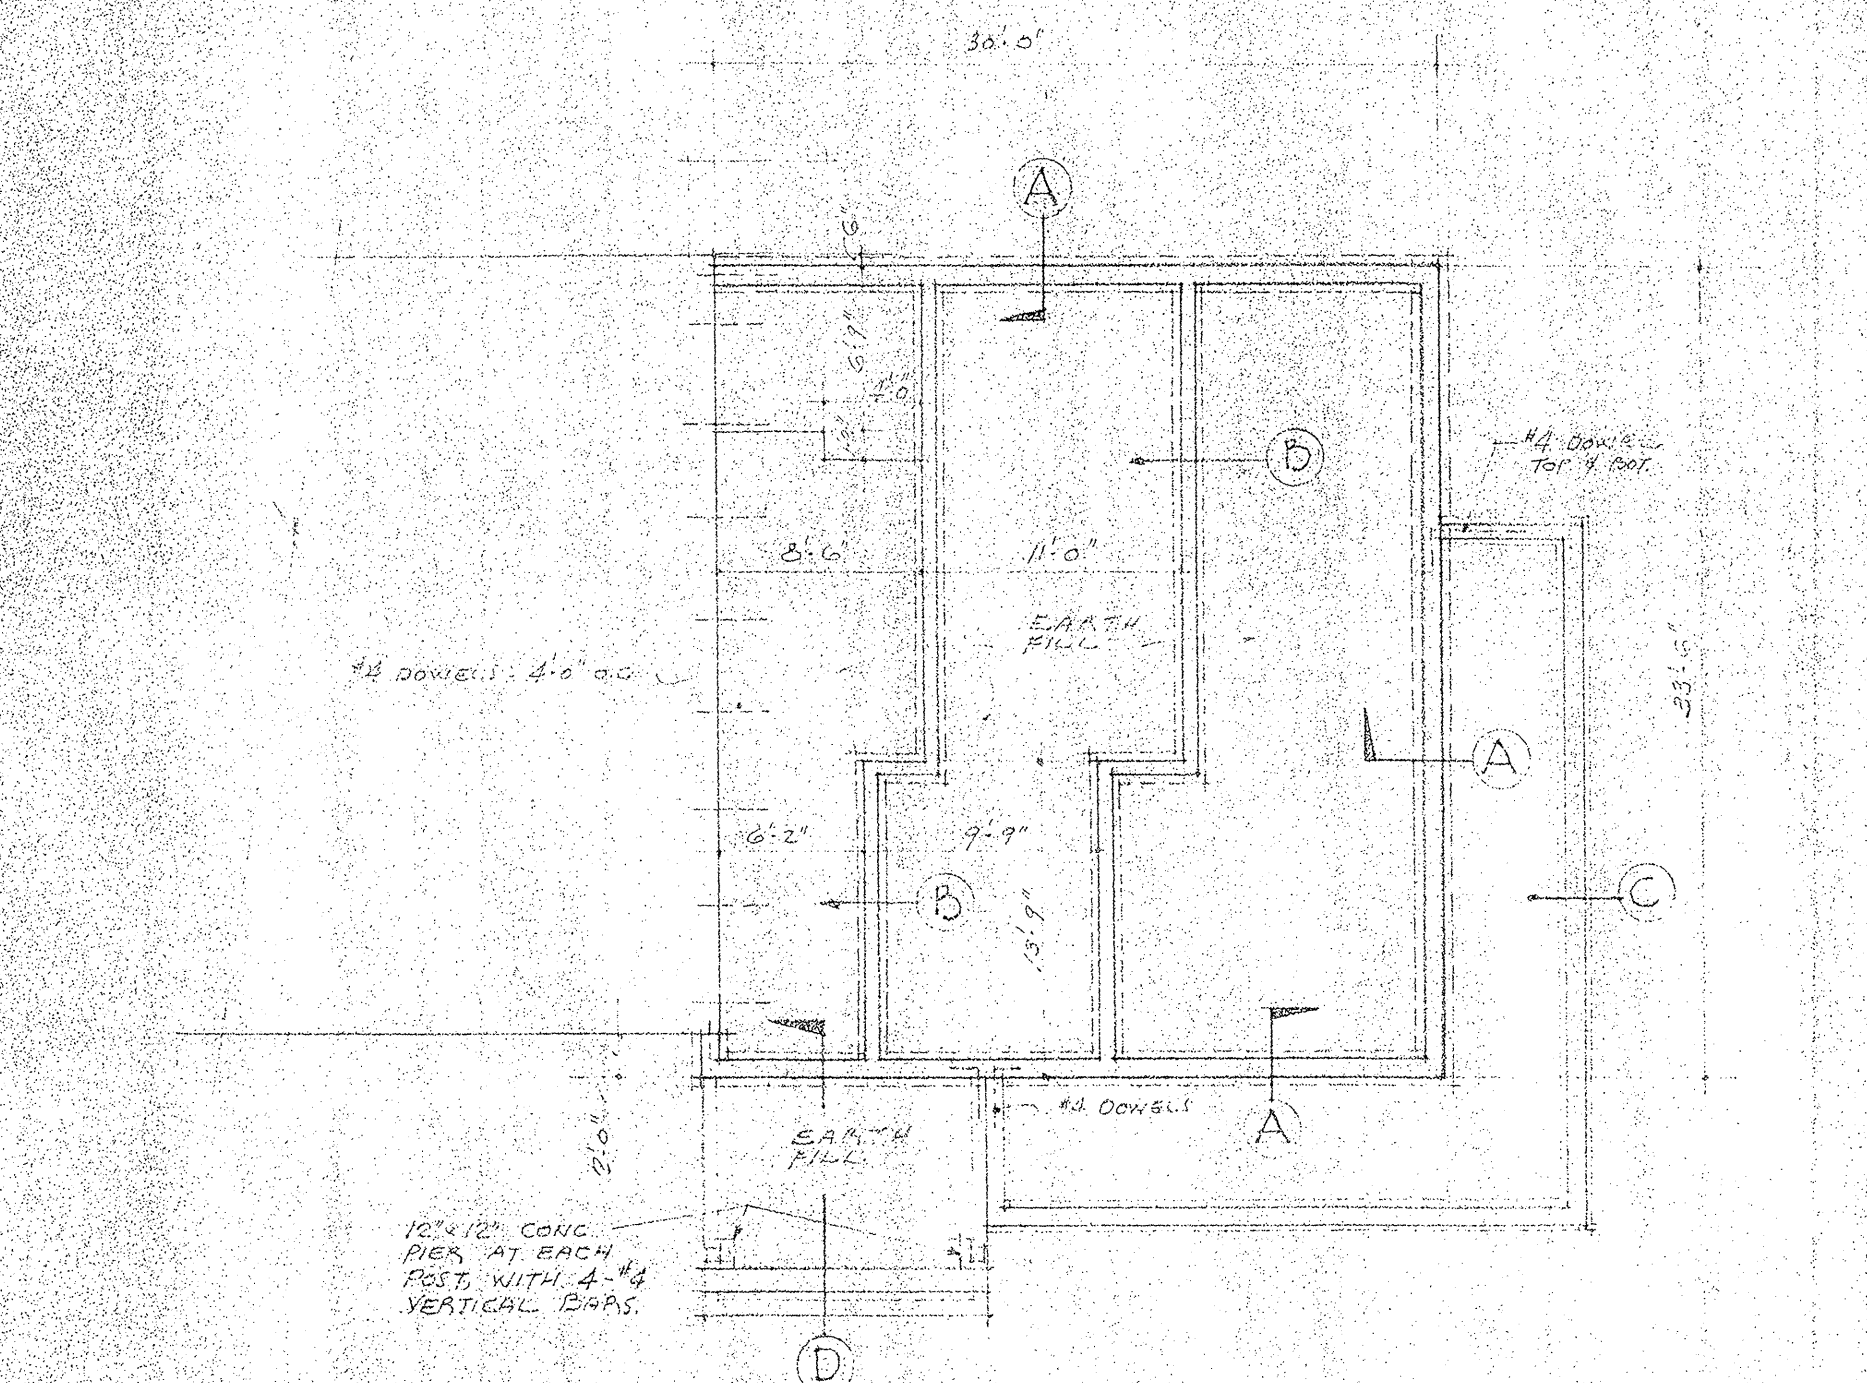

FOUNDATION

ENTRANCE PORCH POST DETAIL

JOINT ANCHORAGE

PLAN AT POST

2ND FLOOR POST DETAIL

SECTION L

SECTION M

SECTION N

SECTION O

SECTION P

SECTION L

SECTION M

SECTION N

SECTION O

SECTION P

SECTION L

SECTION M

SECTION N

SECTION O

SECTION P

SECTION L

SECTION M

SECTION N

SECTION O

SECTION P

ALTERATIONS & ADDITIONS TO PARISH HALL ST. EDMUNDS EPISCOPAL CHURCH HUNTINGTON DRIVE & SAN GABRIEL AVE. SAN MARINO CALIF.		DATE 7-1-54 COMM. 1157 DRAWN J. DANIELS CHECK SHEET 2
AUSTIN FIELD & IRY architects		
2311 WEST THIRD STREET LOS ANGELES 5, CALIFORNIA		DUNKIRK 8-1326