



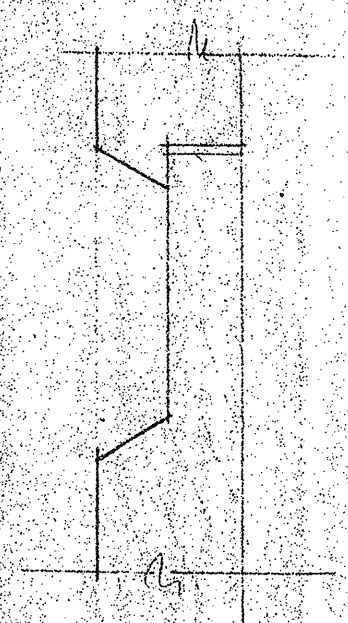


EXT. WOOD TRIM
@ PICTURE RECESS IN EXTG.
BUILDING ENTRY




SIDING DET.
FULL SIZE

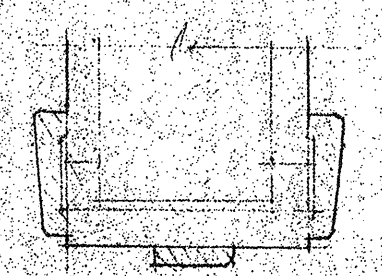



TYP. INT.
DOOR FRAME
SCALE 3"=1'-0"

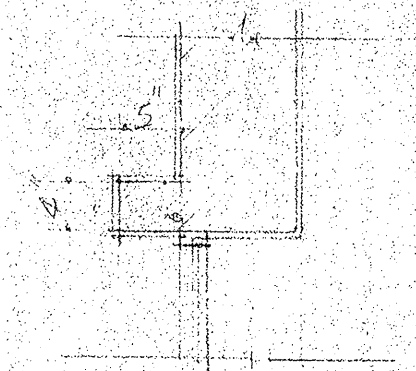


TYPICAL WINDOW
SILL & HEAD FOR
WINDOW #6

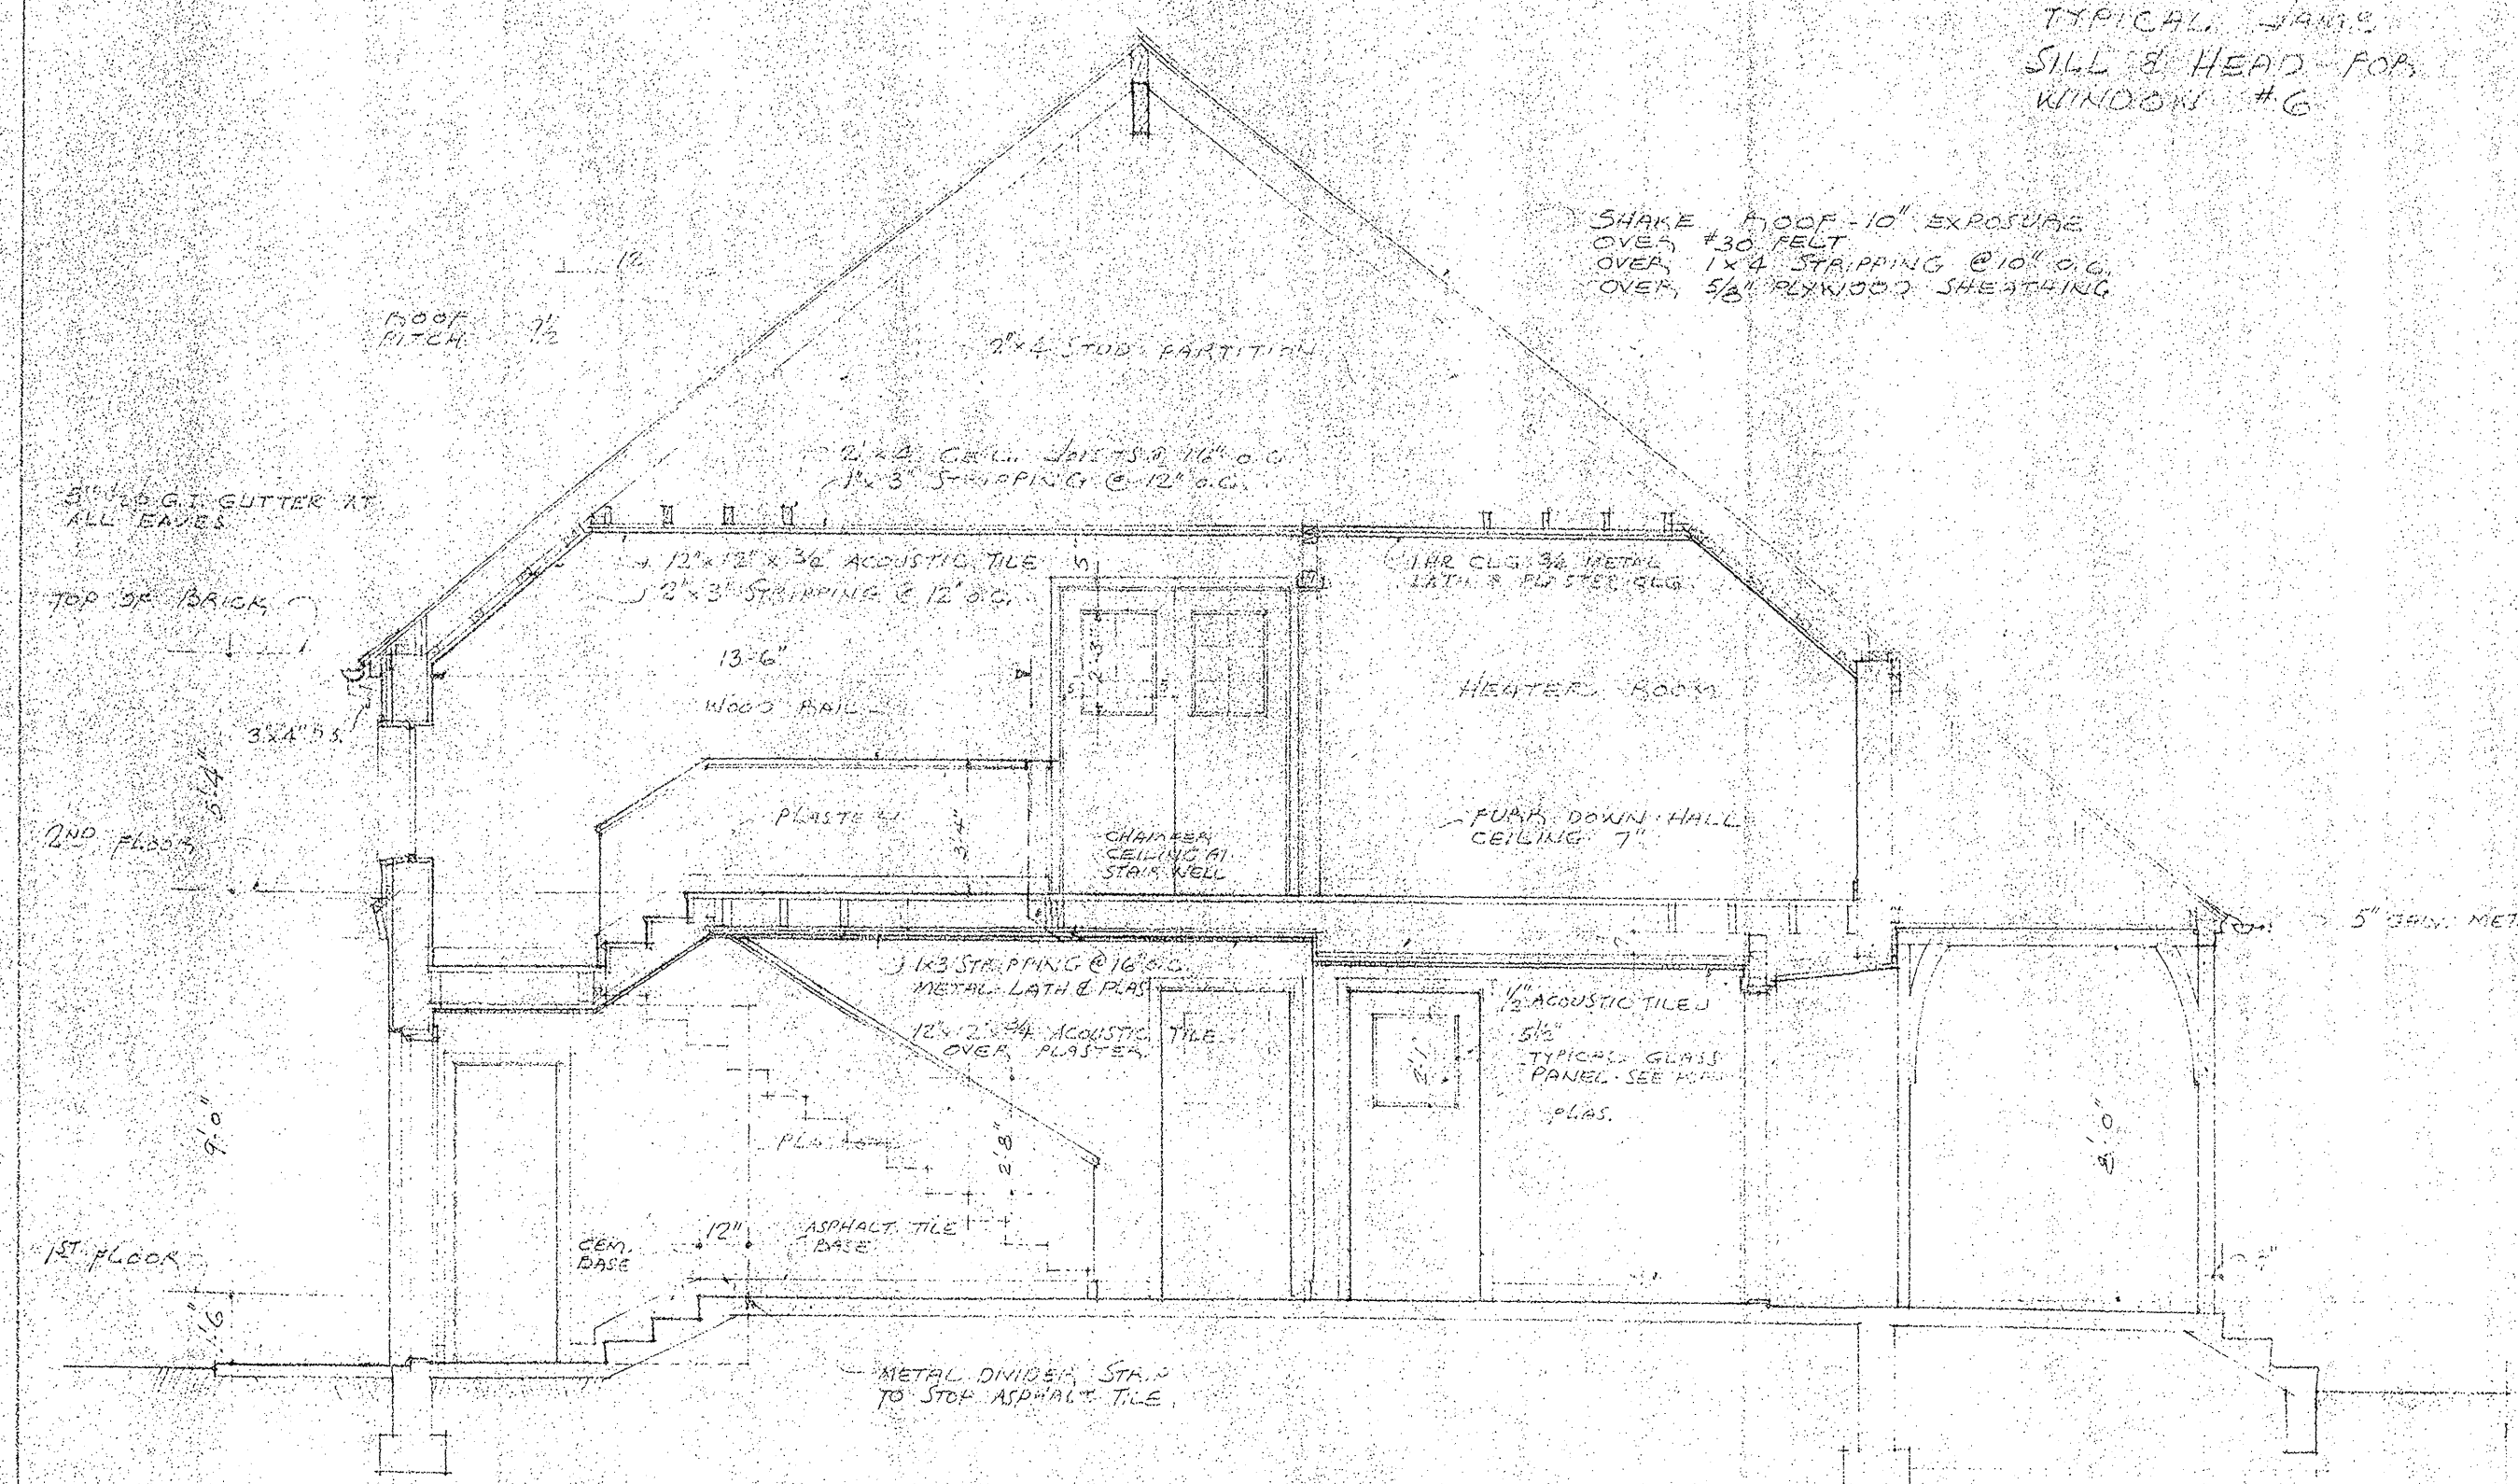


SECTION A
SCALE 1/4"=1'-0"

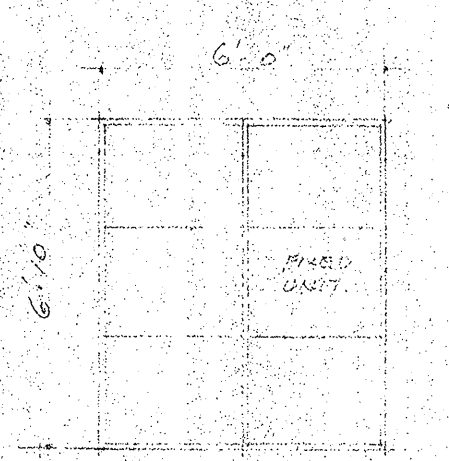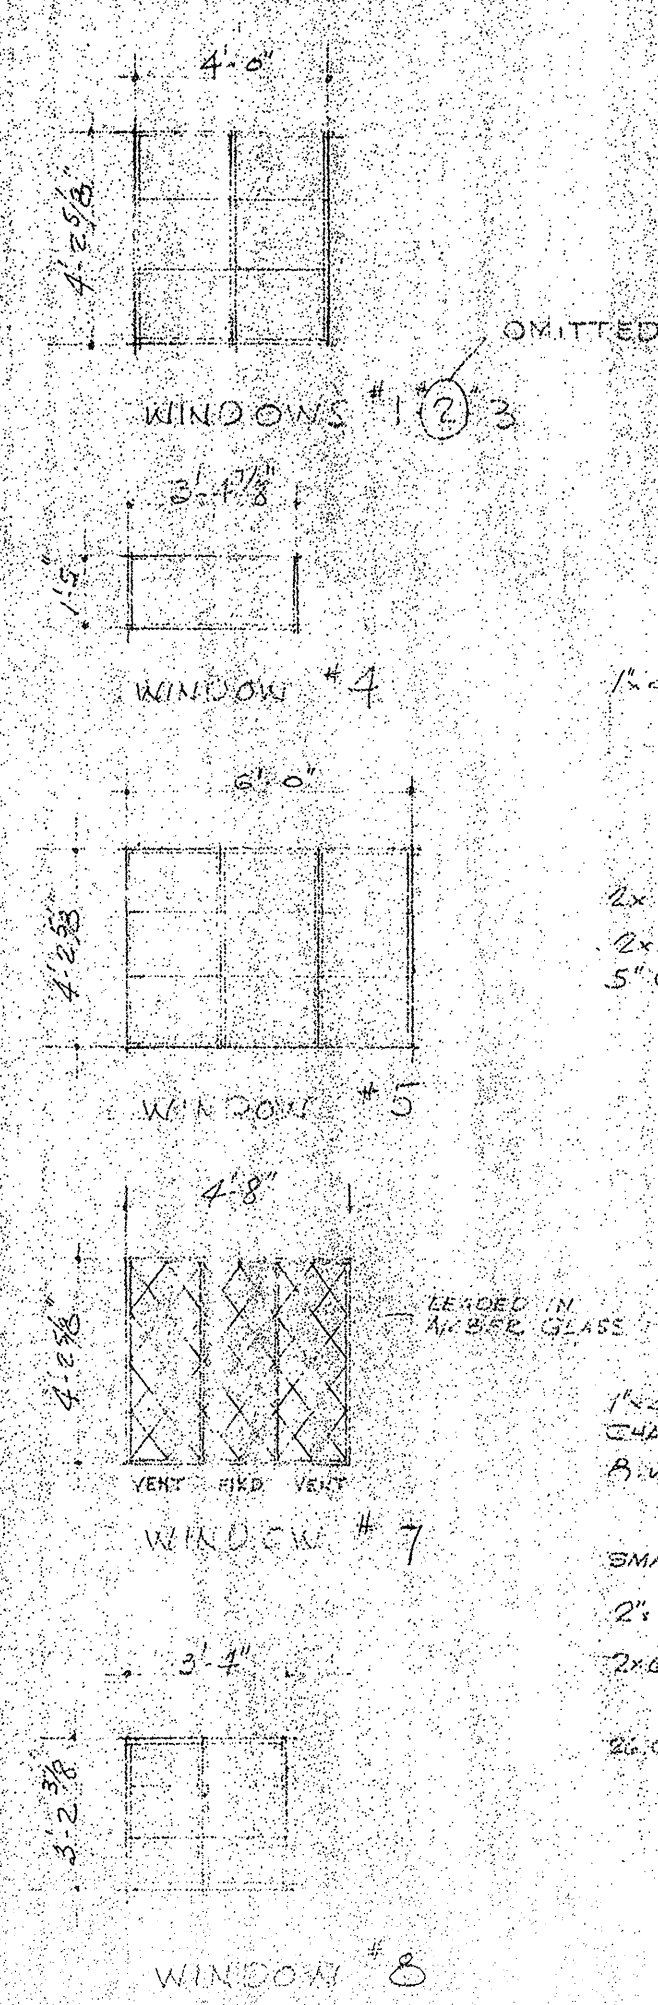


WINDOW #6
ARCADIA DOOR

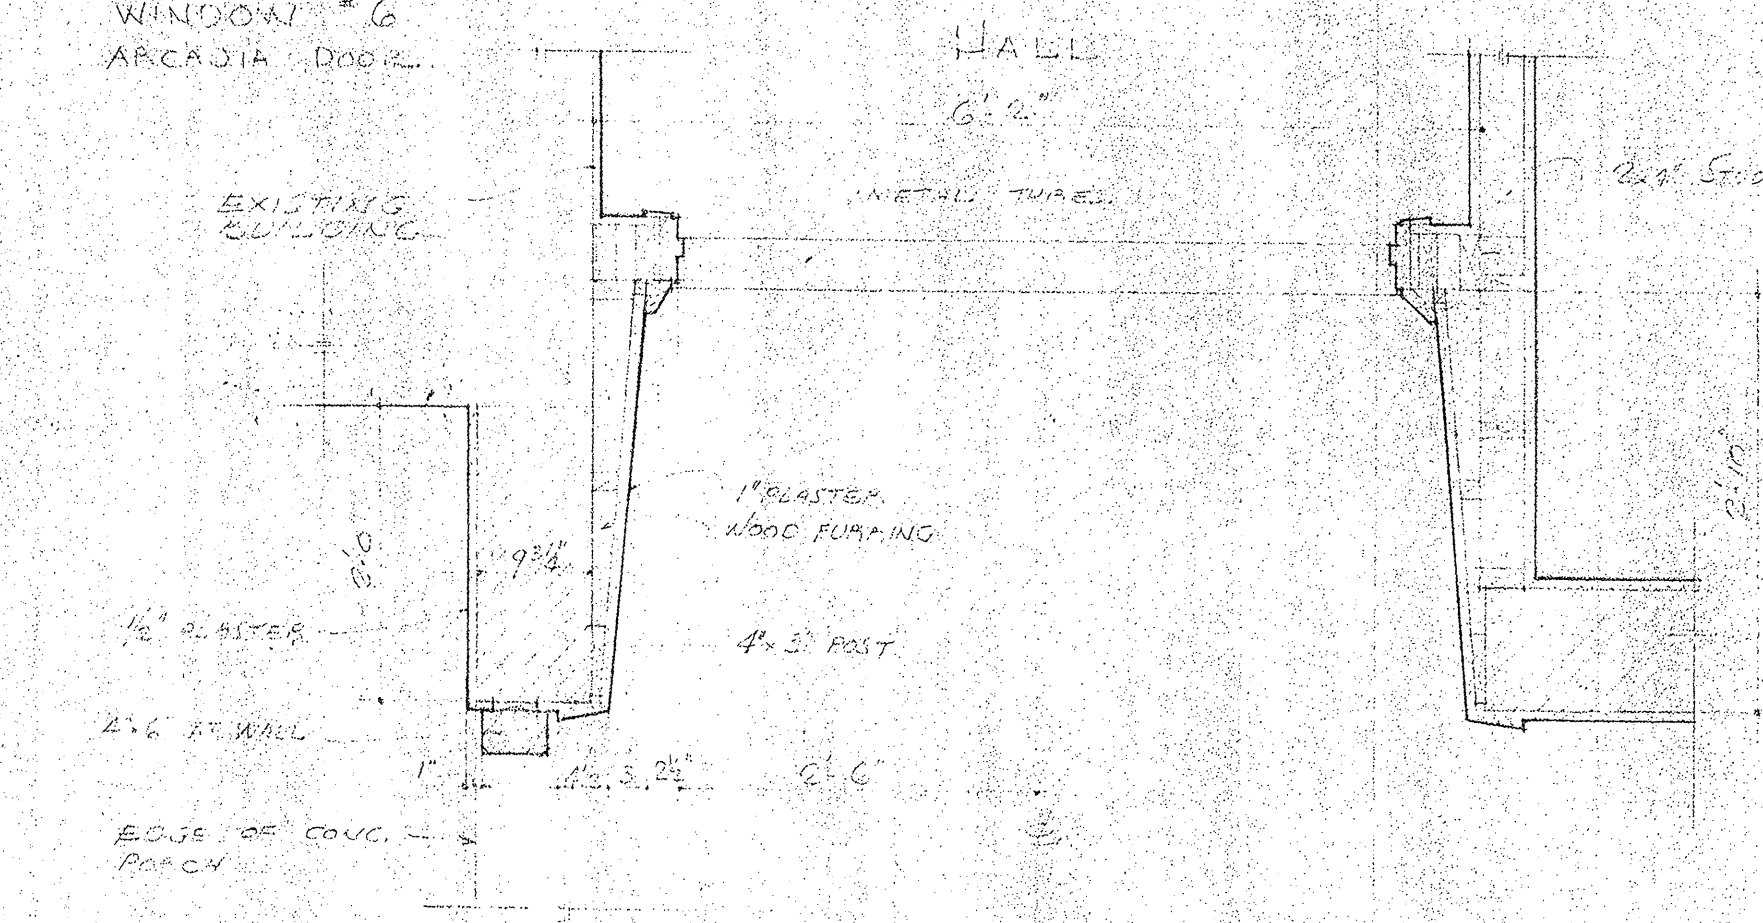


PLAN DETAIL OF
MAIN ENTRANCE
SCALE 1/4"=1'-0"

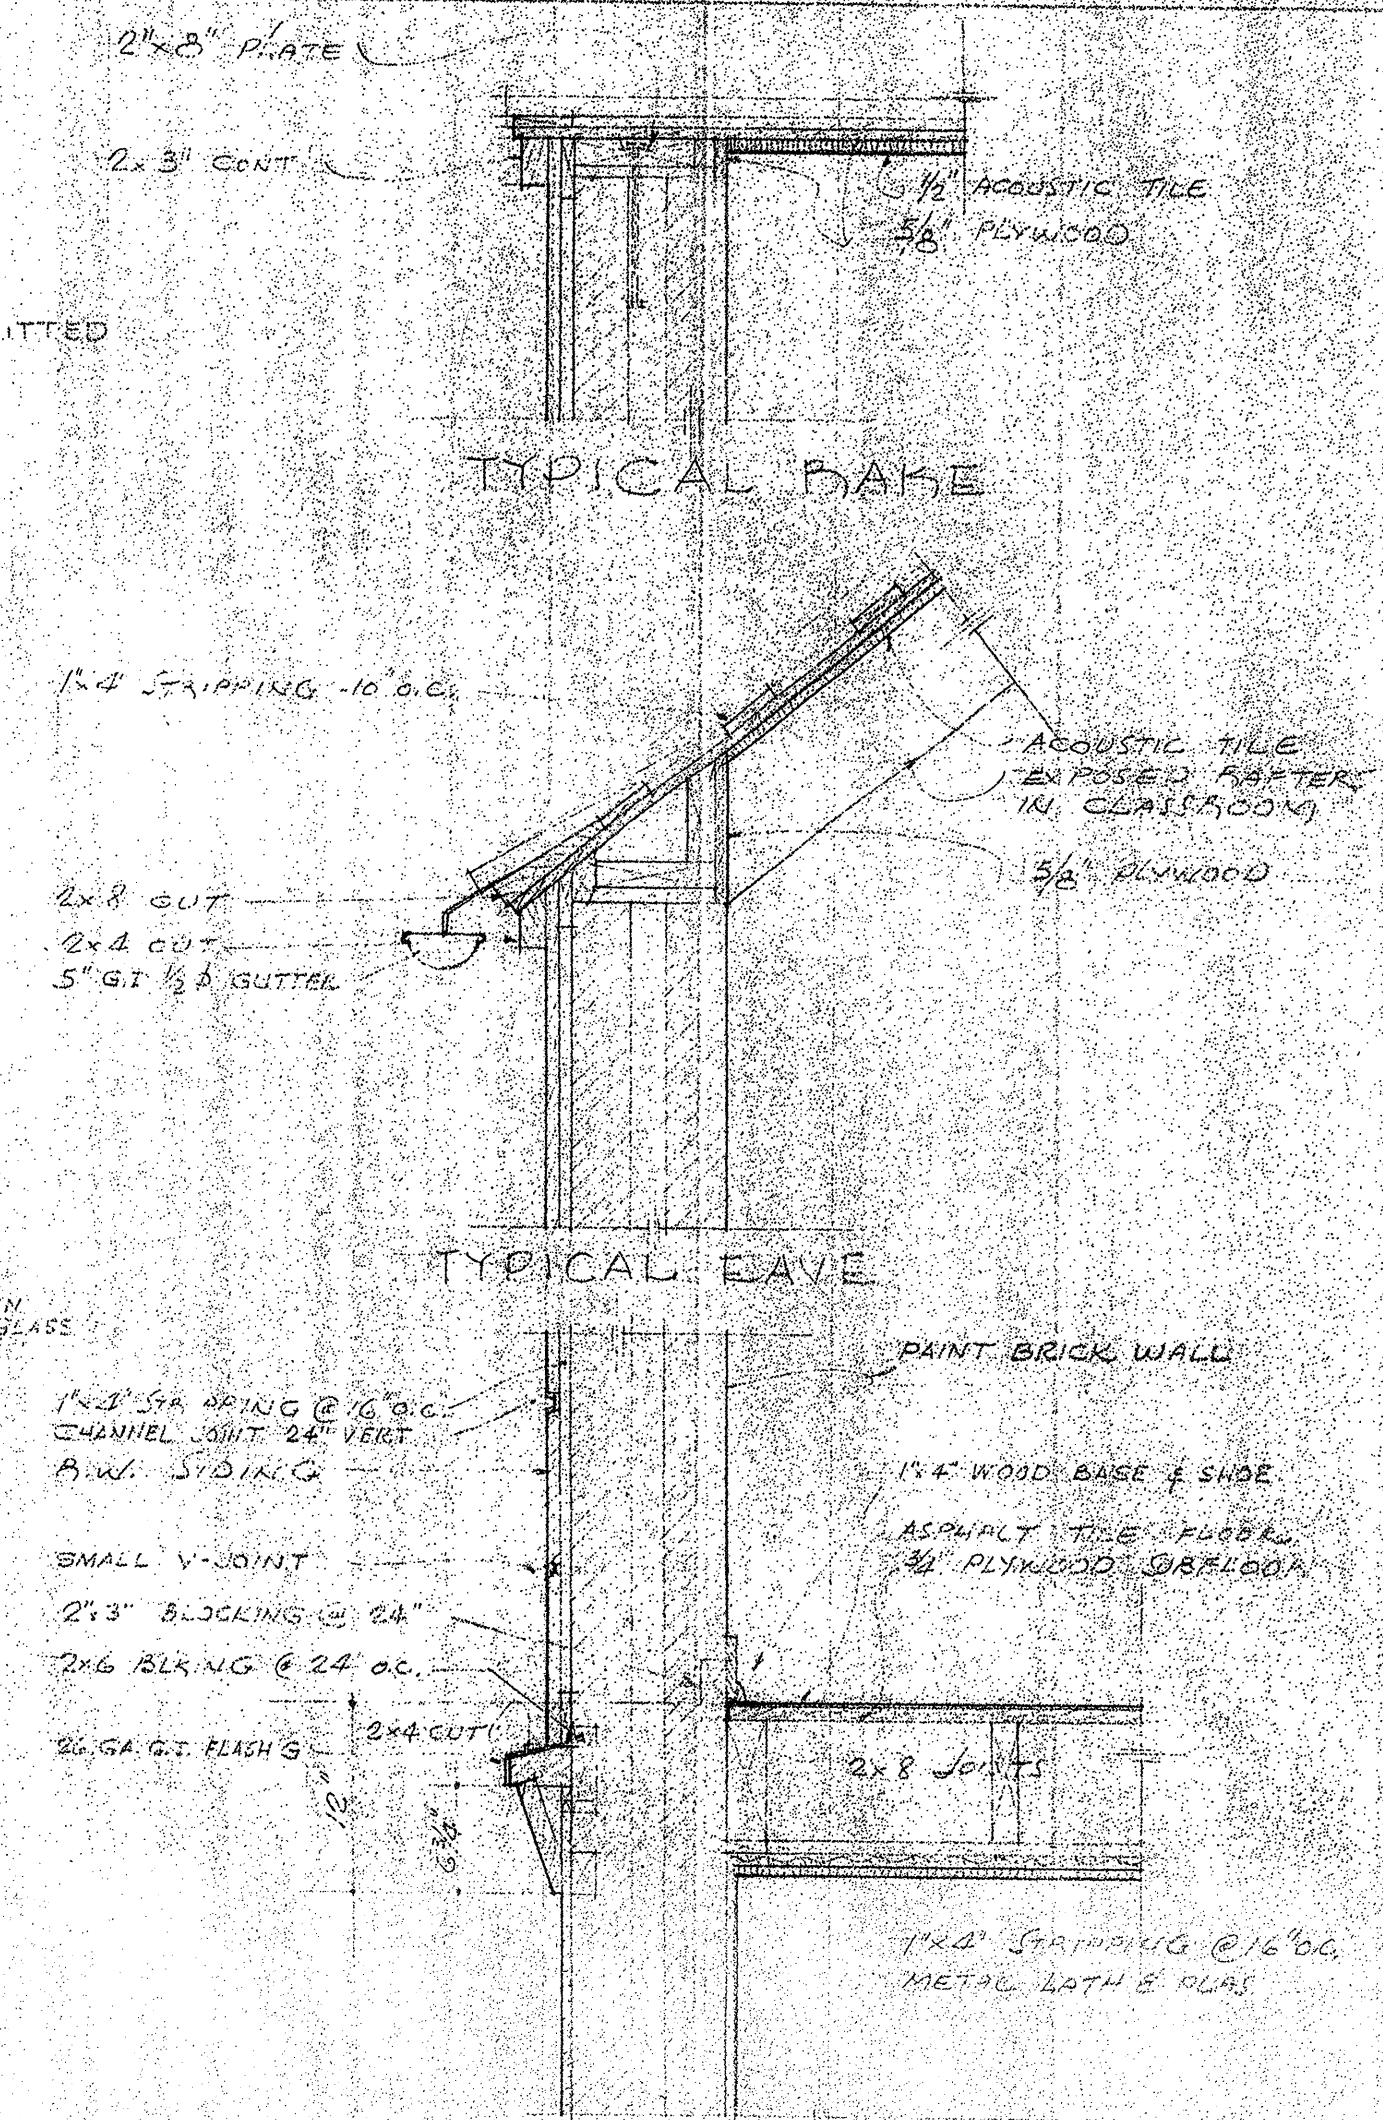

2ND FLOOR - WATER TABLE
SCALE 1"=1'-0"

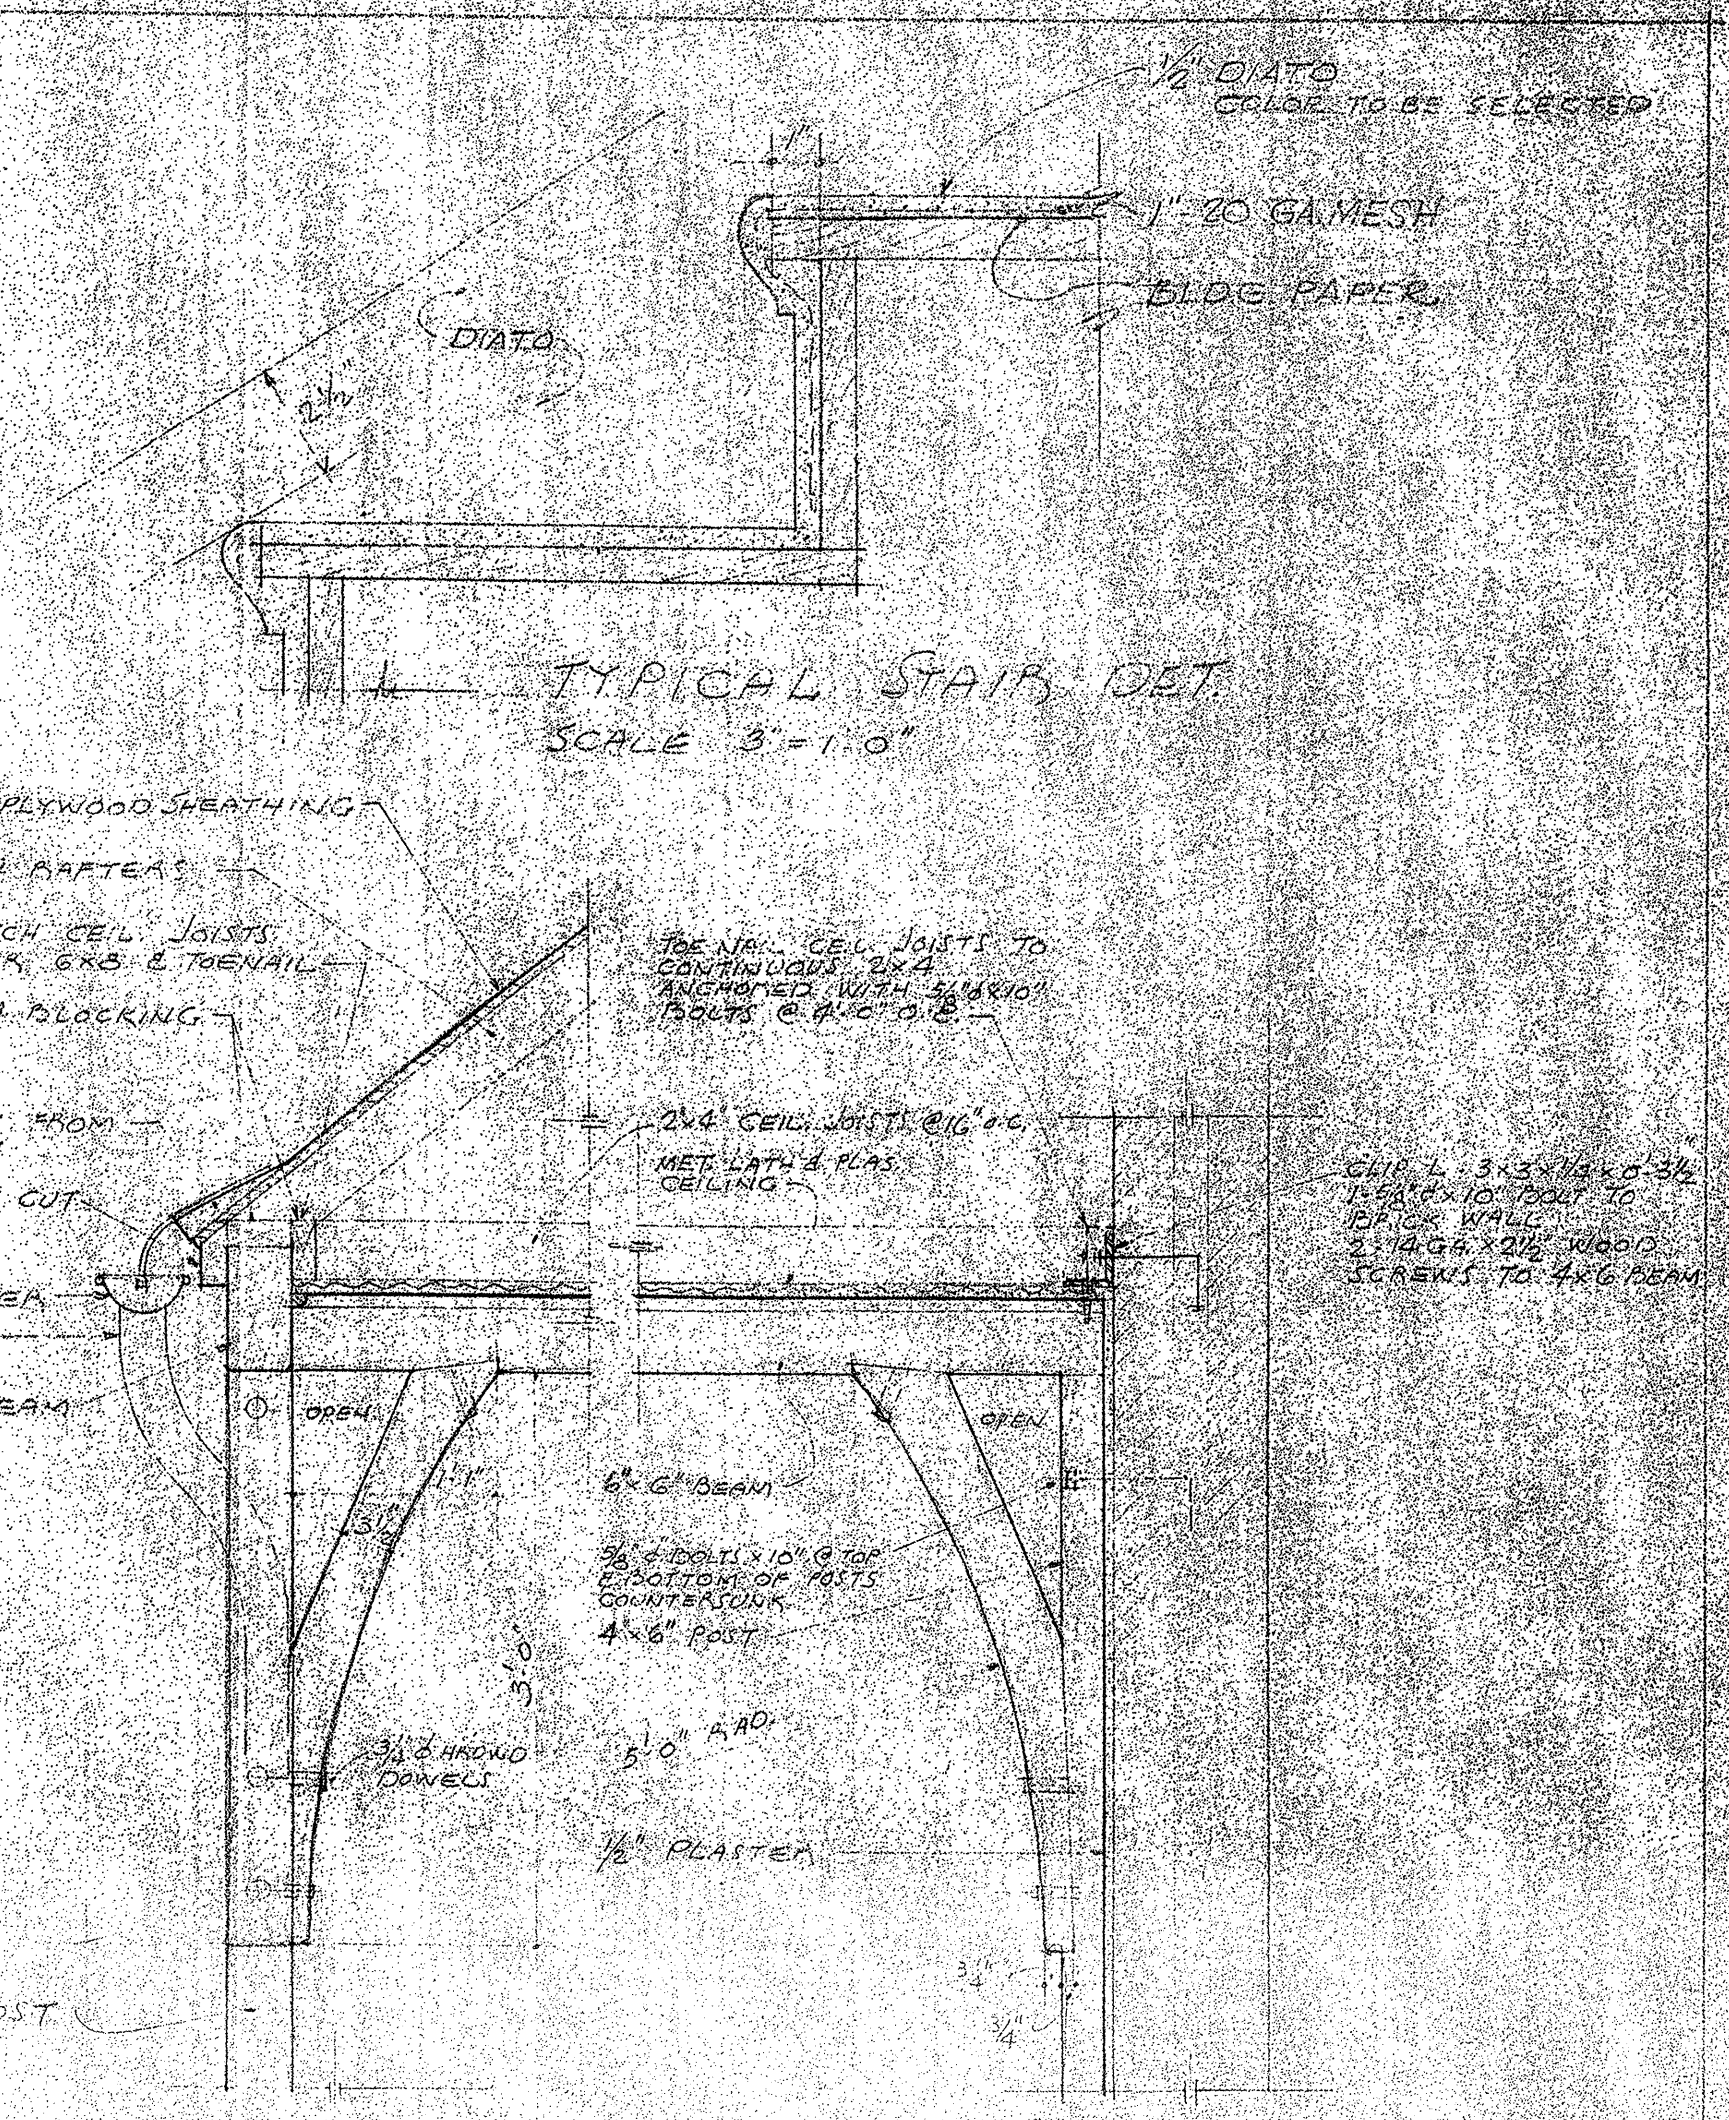

EAVE SECTION

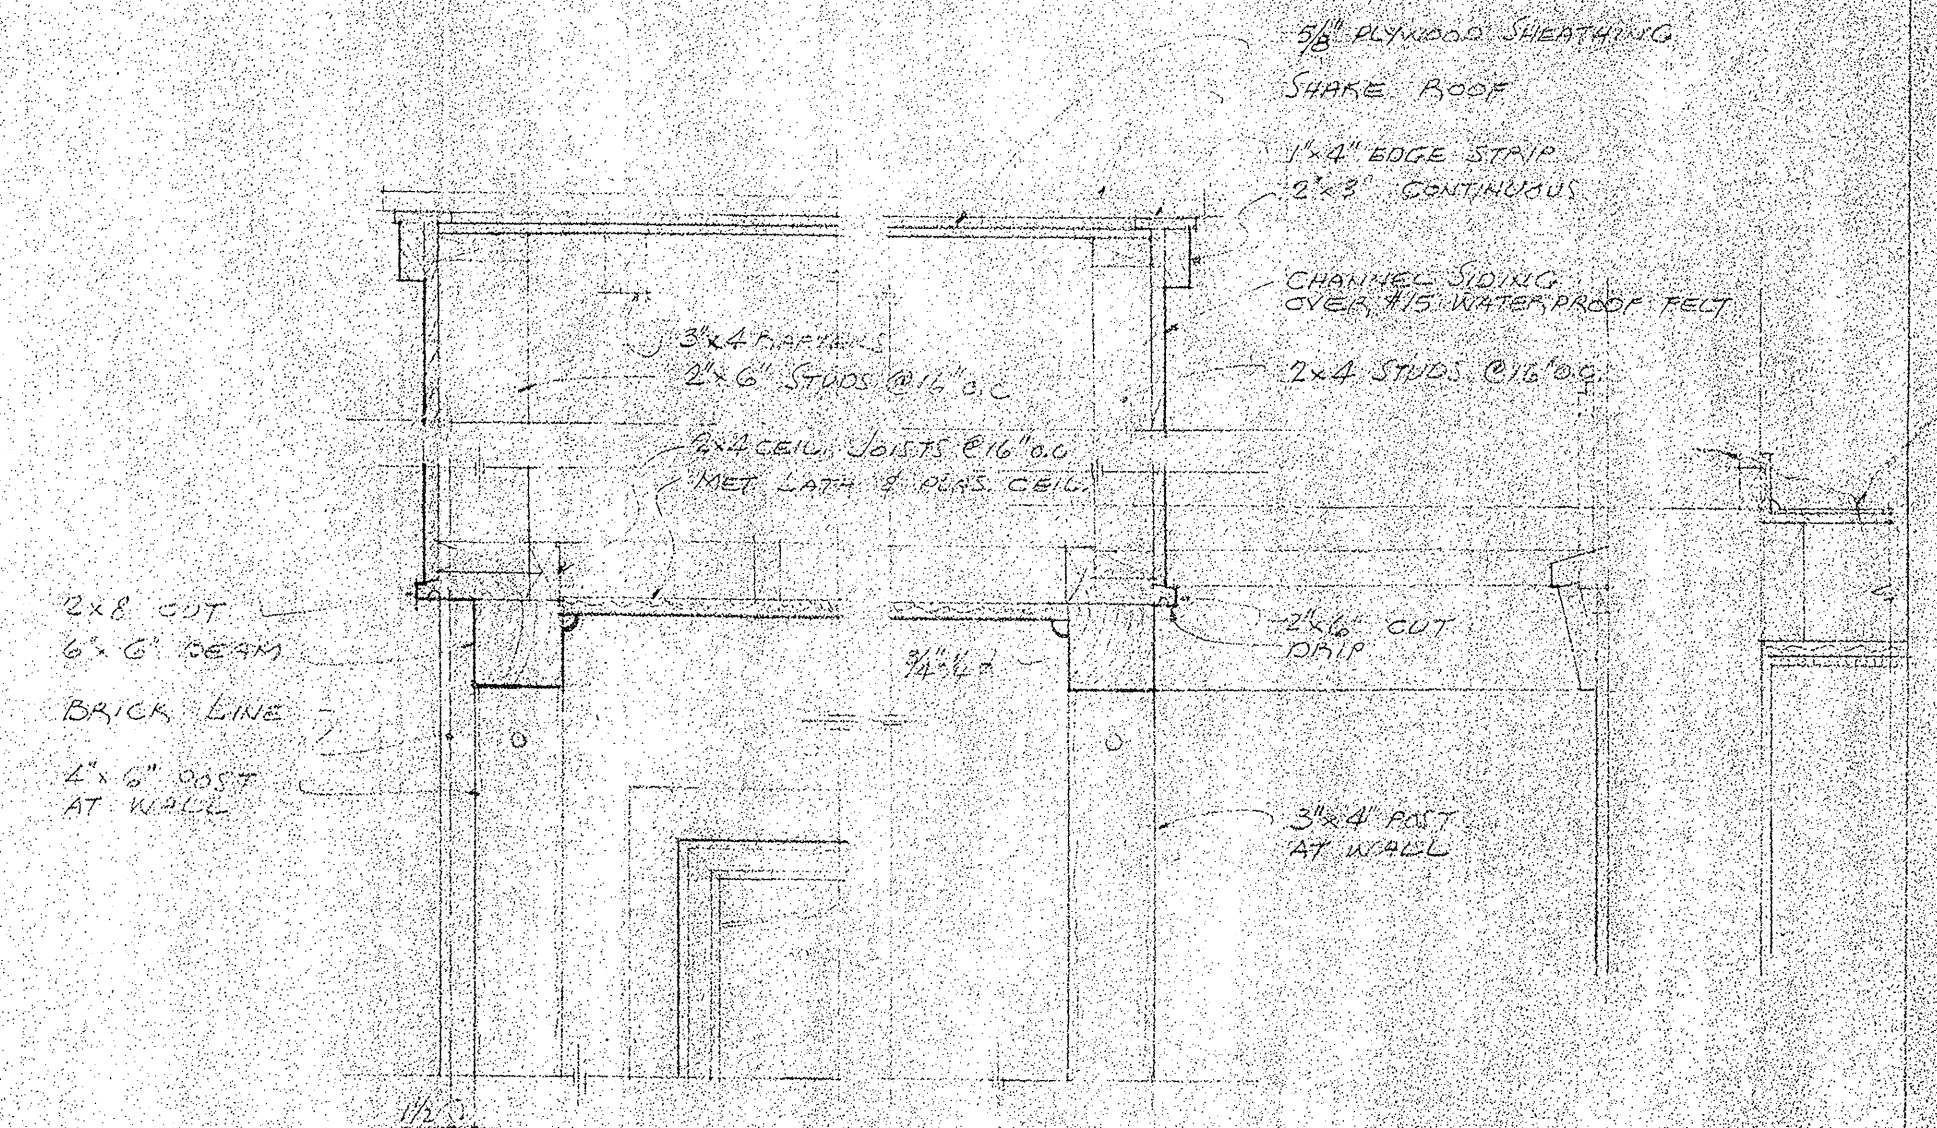

CROSS SECTION
PORCH DETAILS (MAIN ENTRANCE)
SCALE 1"=1'-0"

REVISED JULY 25, 54 J.S.R.

ALTERATIONS & ADDITIONS TO PARISH HALL ST. EDMUND'S EPISCOPAL CHURCH HUNTINGTON DRIVE & SAN GABRIEL AVE SAN MARTINO, CALIF.		DATE 7-1-54
AUSTIN FIELD & FRY Architects d.i.d.		COMM 1157
2311 WEST THIRD STREET LOS ANGELES 5, CALIFORNIA		DRAWN J. DAVIS
DUNKIRK 8-1326		CHECK
		SHEET 3