




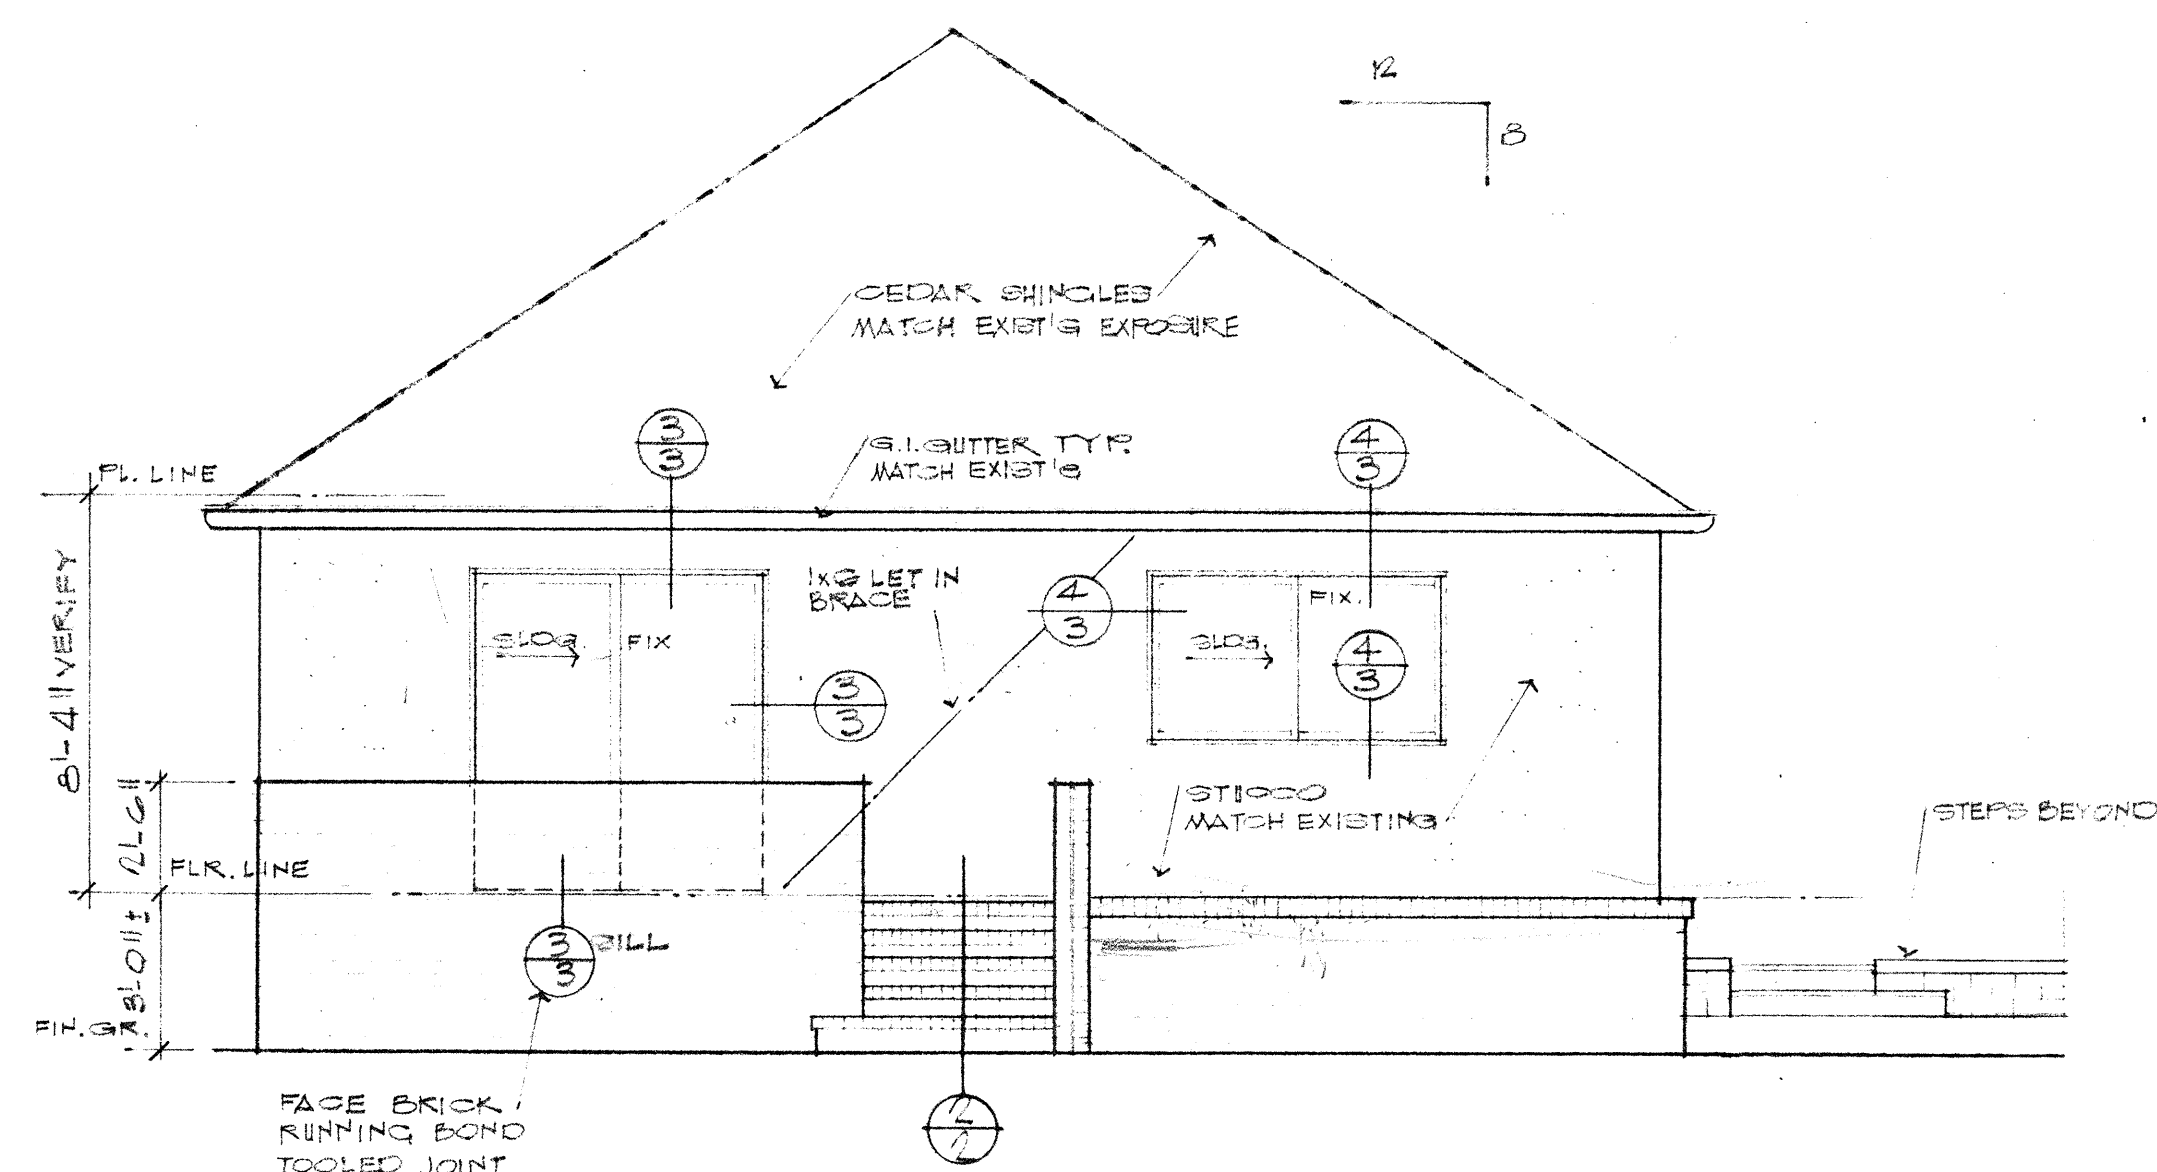


SOUTH ELEVATION
SCALE 1/4"=1'-0"

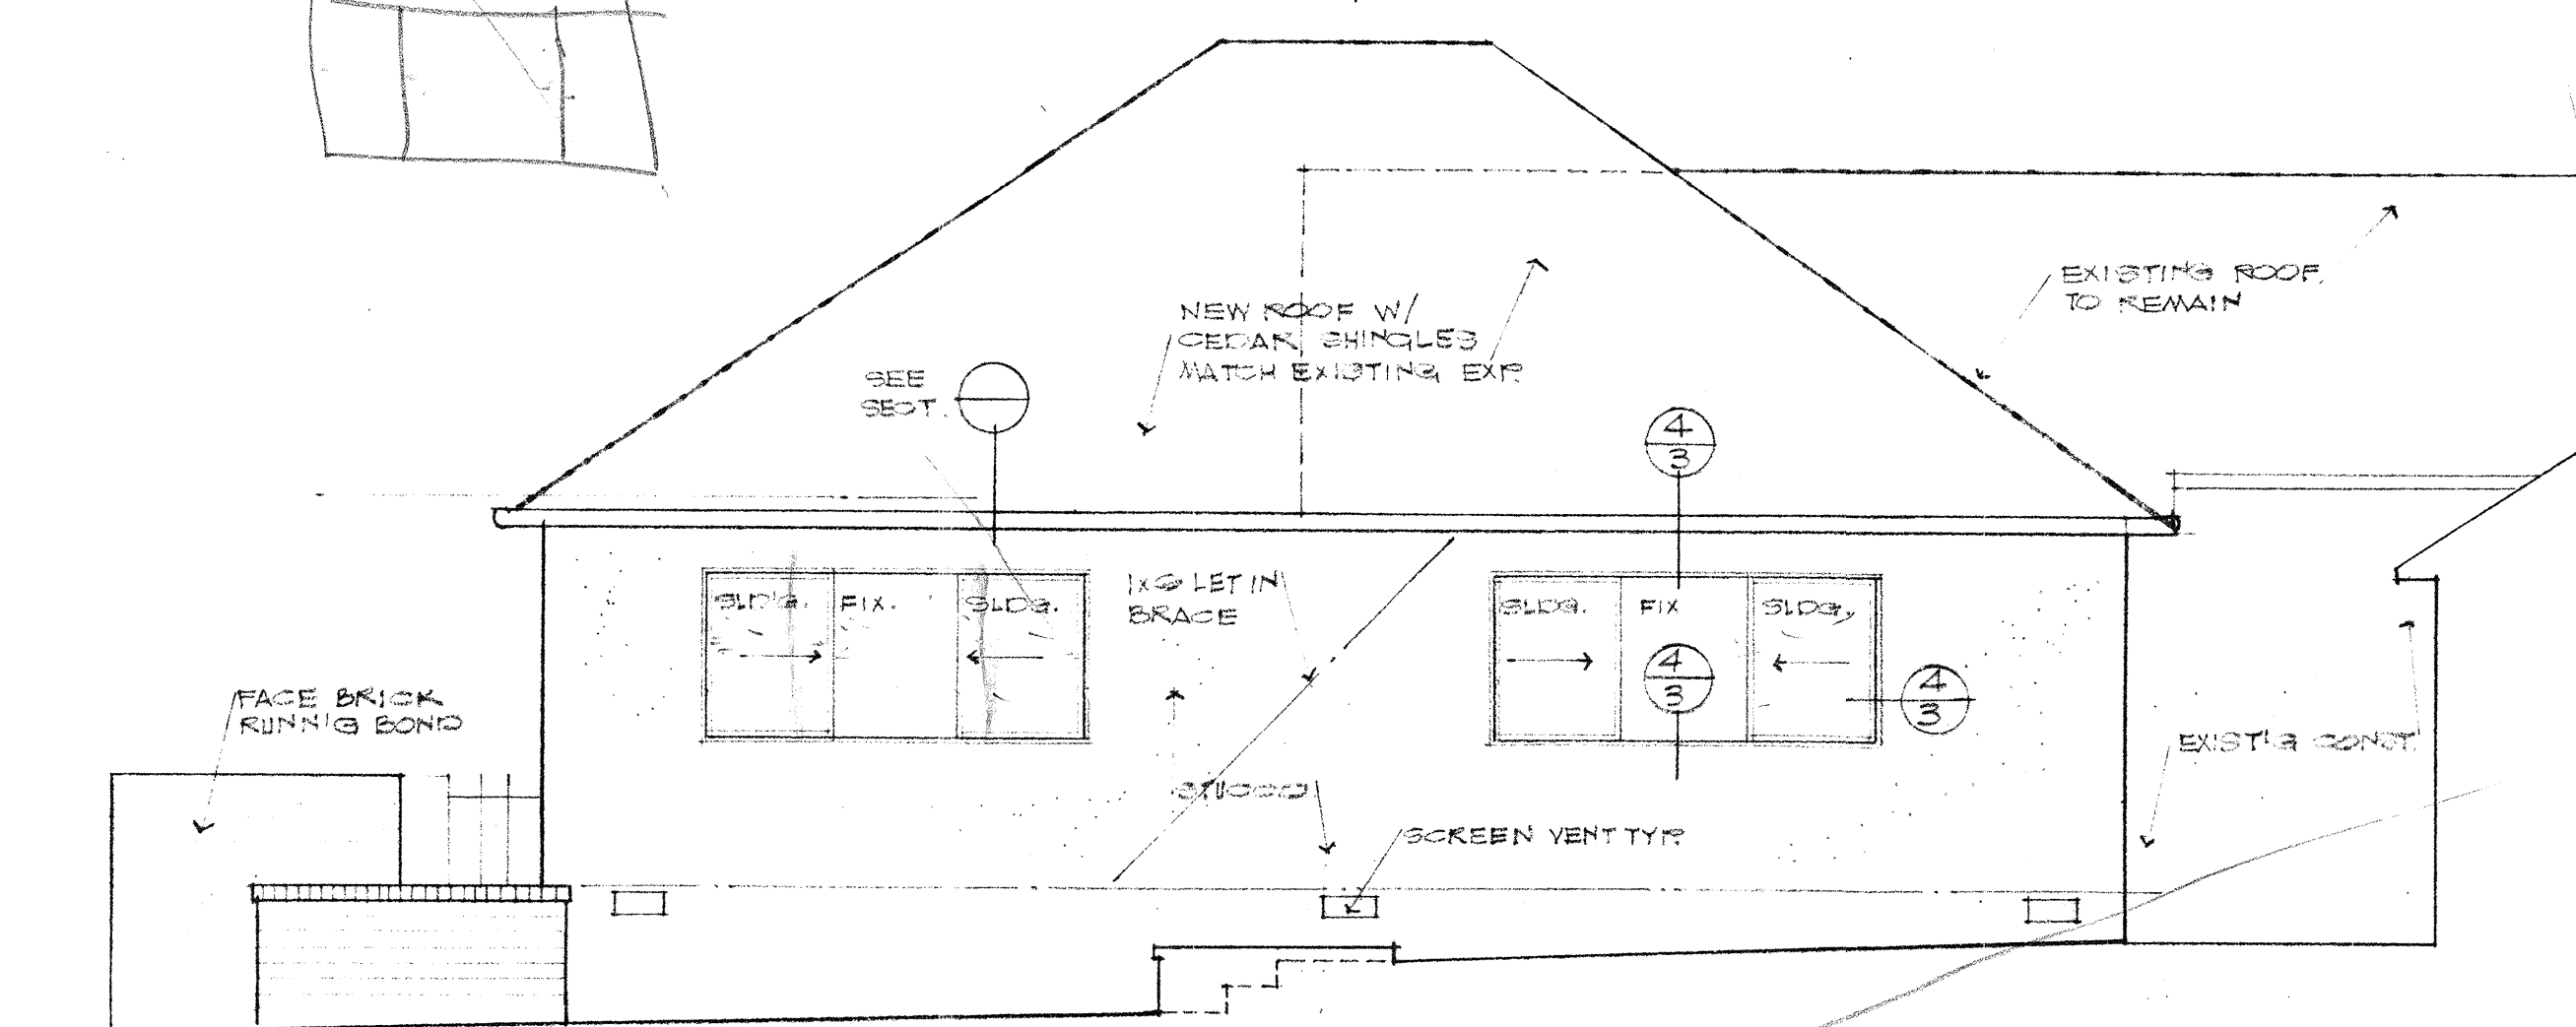


EAST ELEVATION
SCALE 1/4"=1'-0"

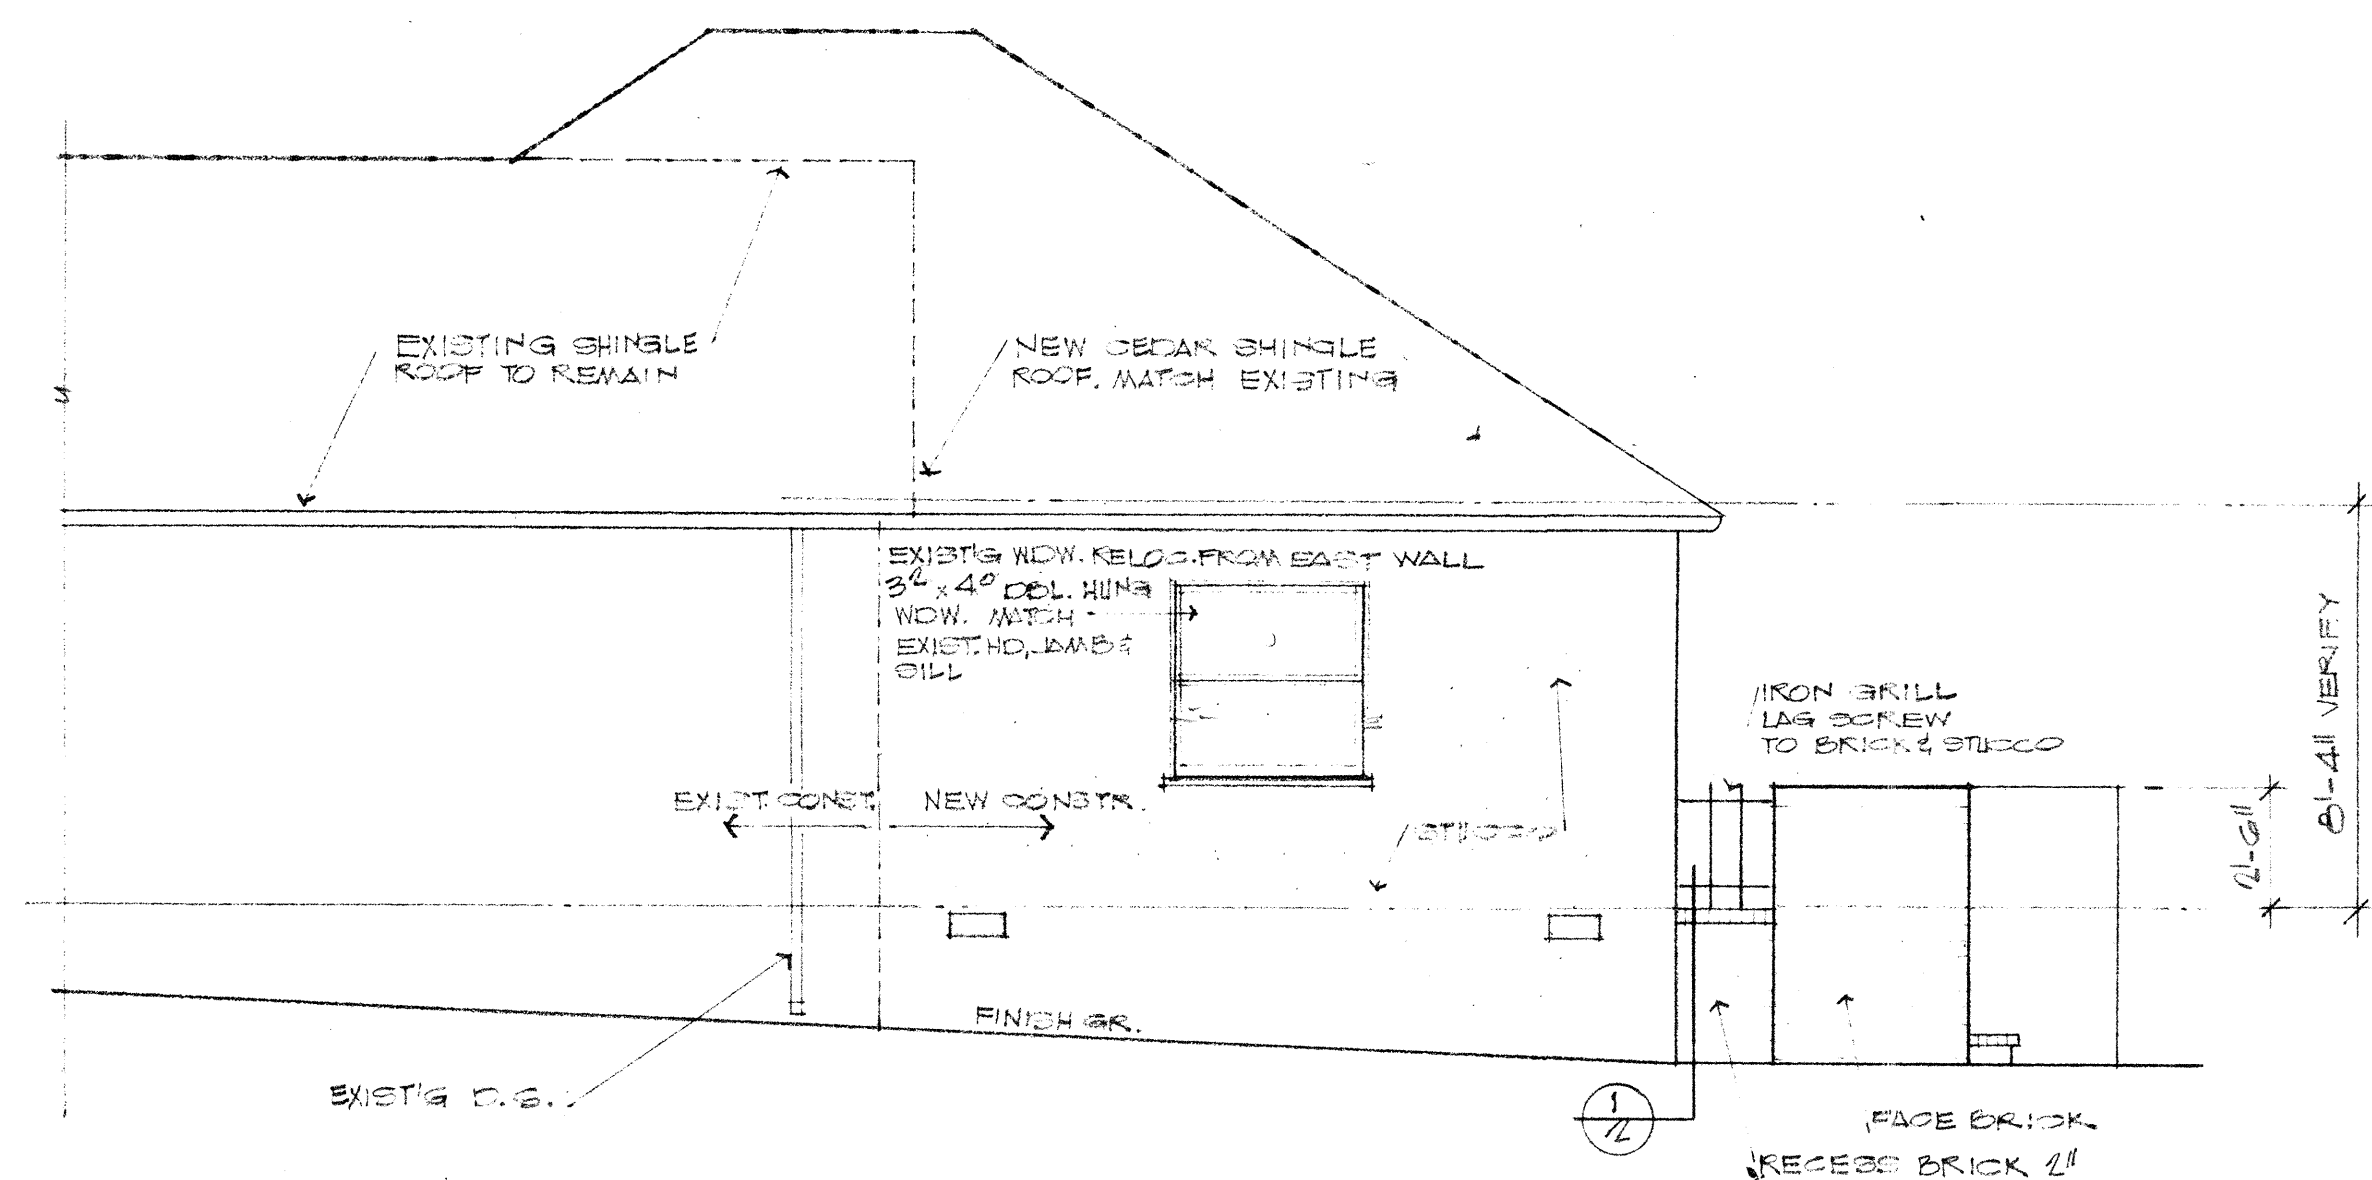


WEST ELEVATION
SCALE 1/4"=1'-0"

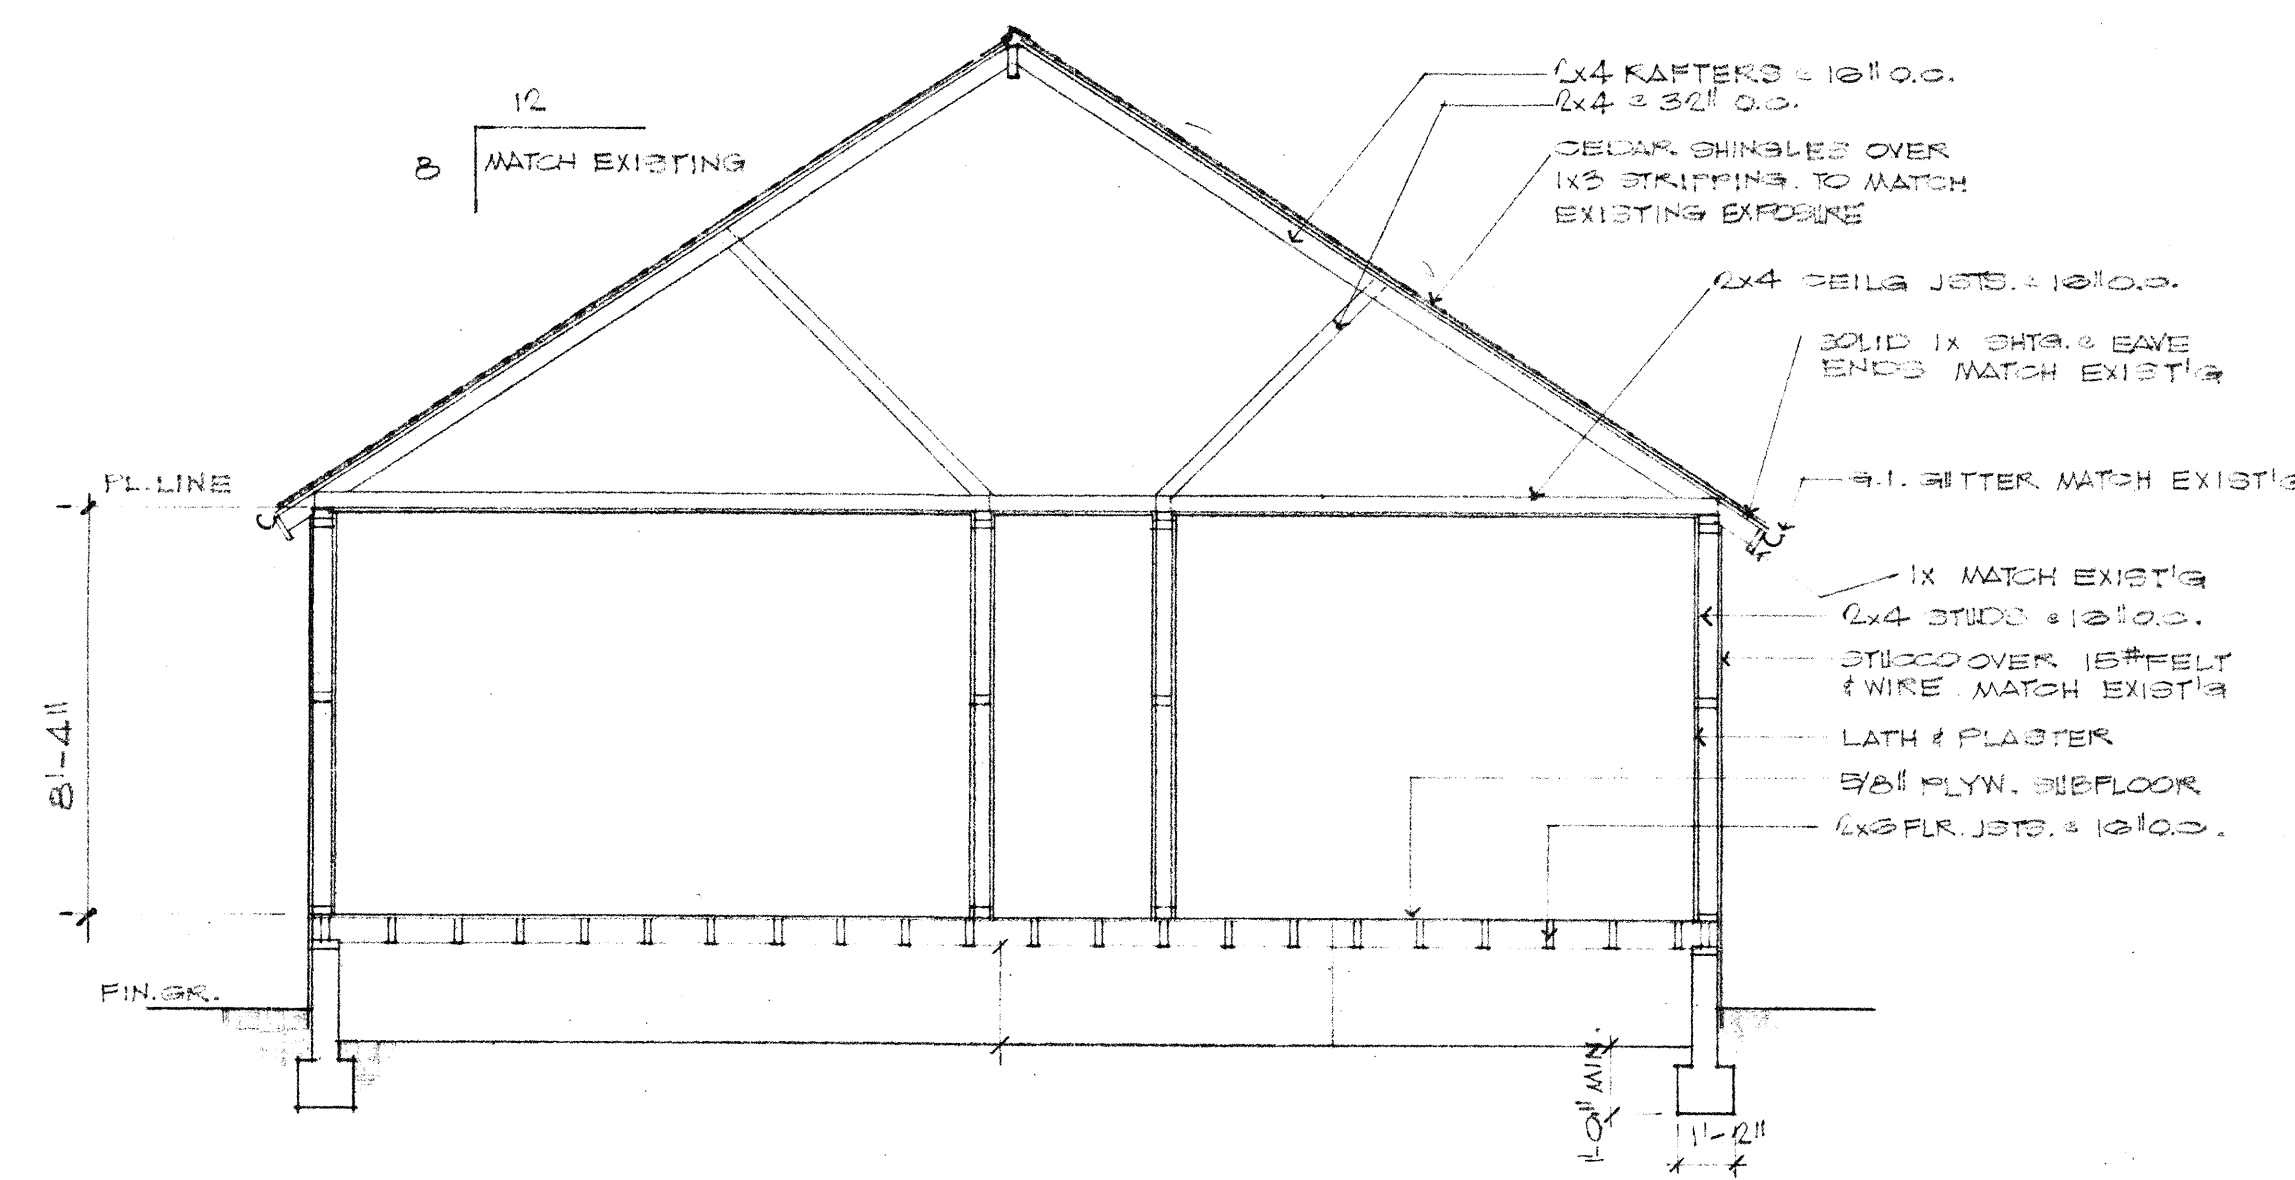


SECTION
SCALE 1/4"=1'-0"

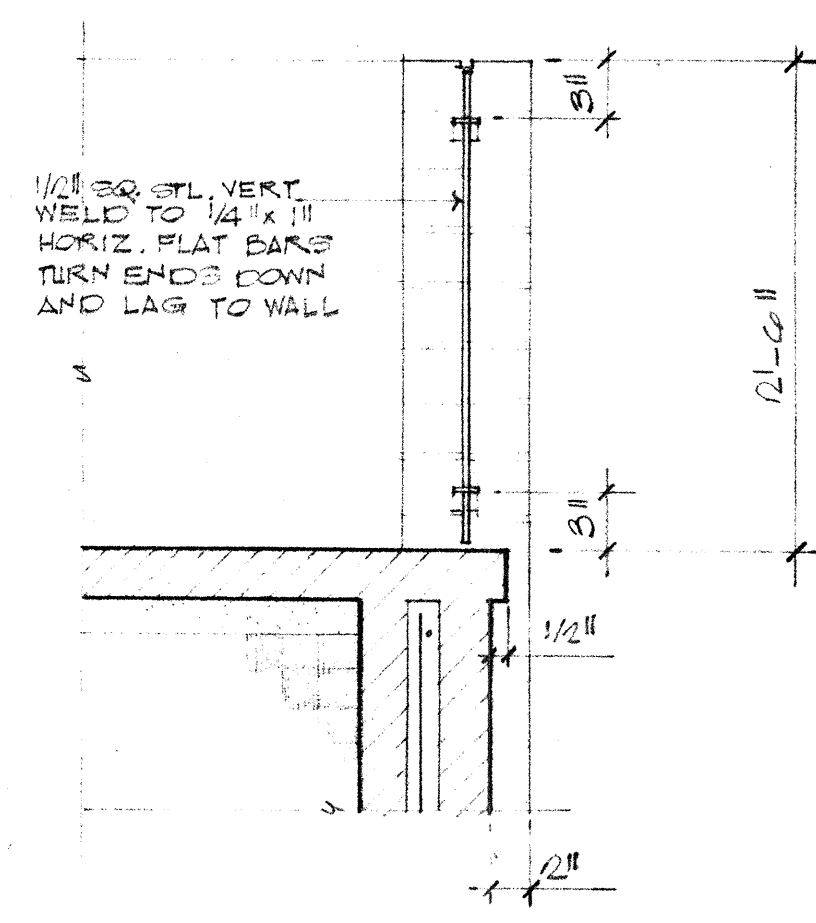


IRON GRILL WALL 1'-0" 1.

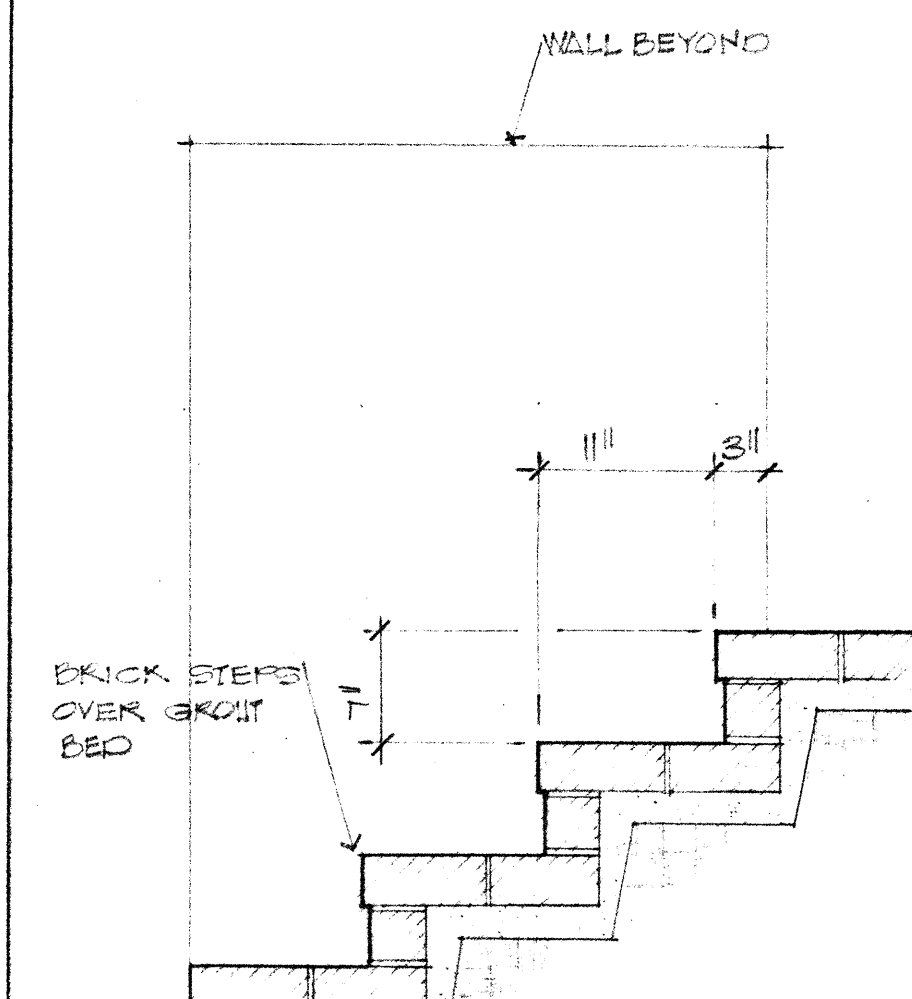

BRICK STEPS 1'-0" 2.

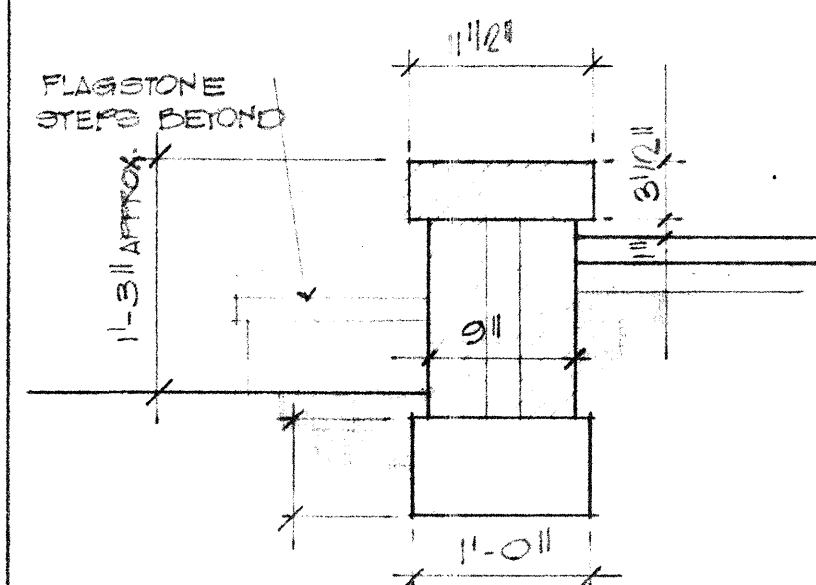

PATIO WALL 1'-0" 3.

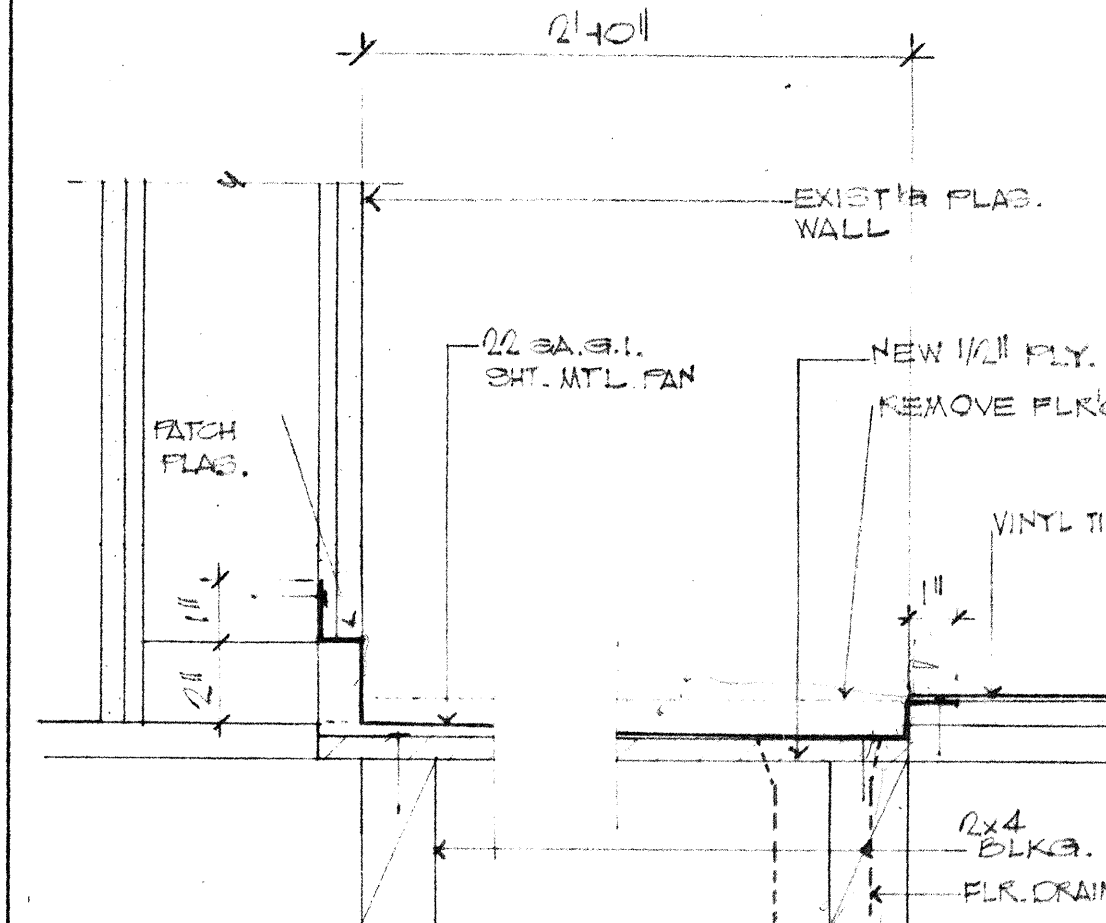

PAN UNDER WSH. & DRYER 3'-0" 4.

3/ Check Print