



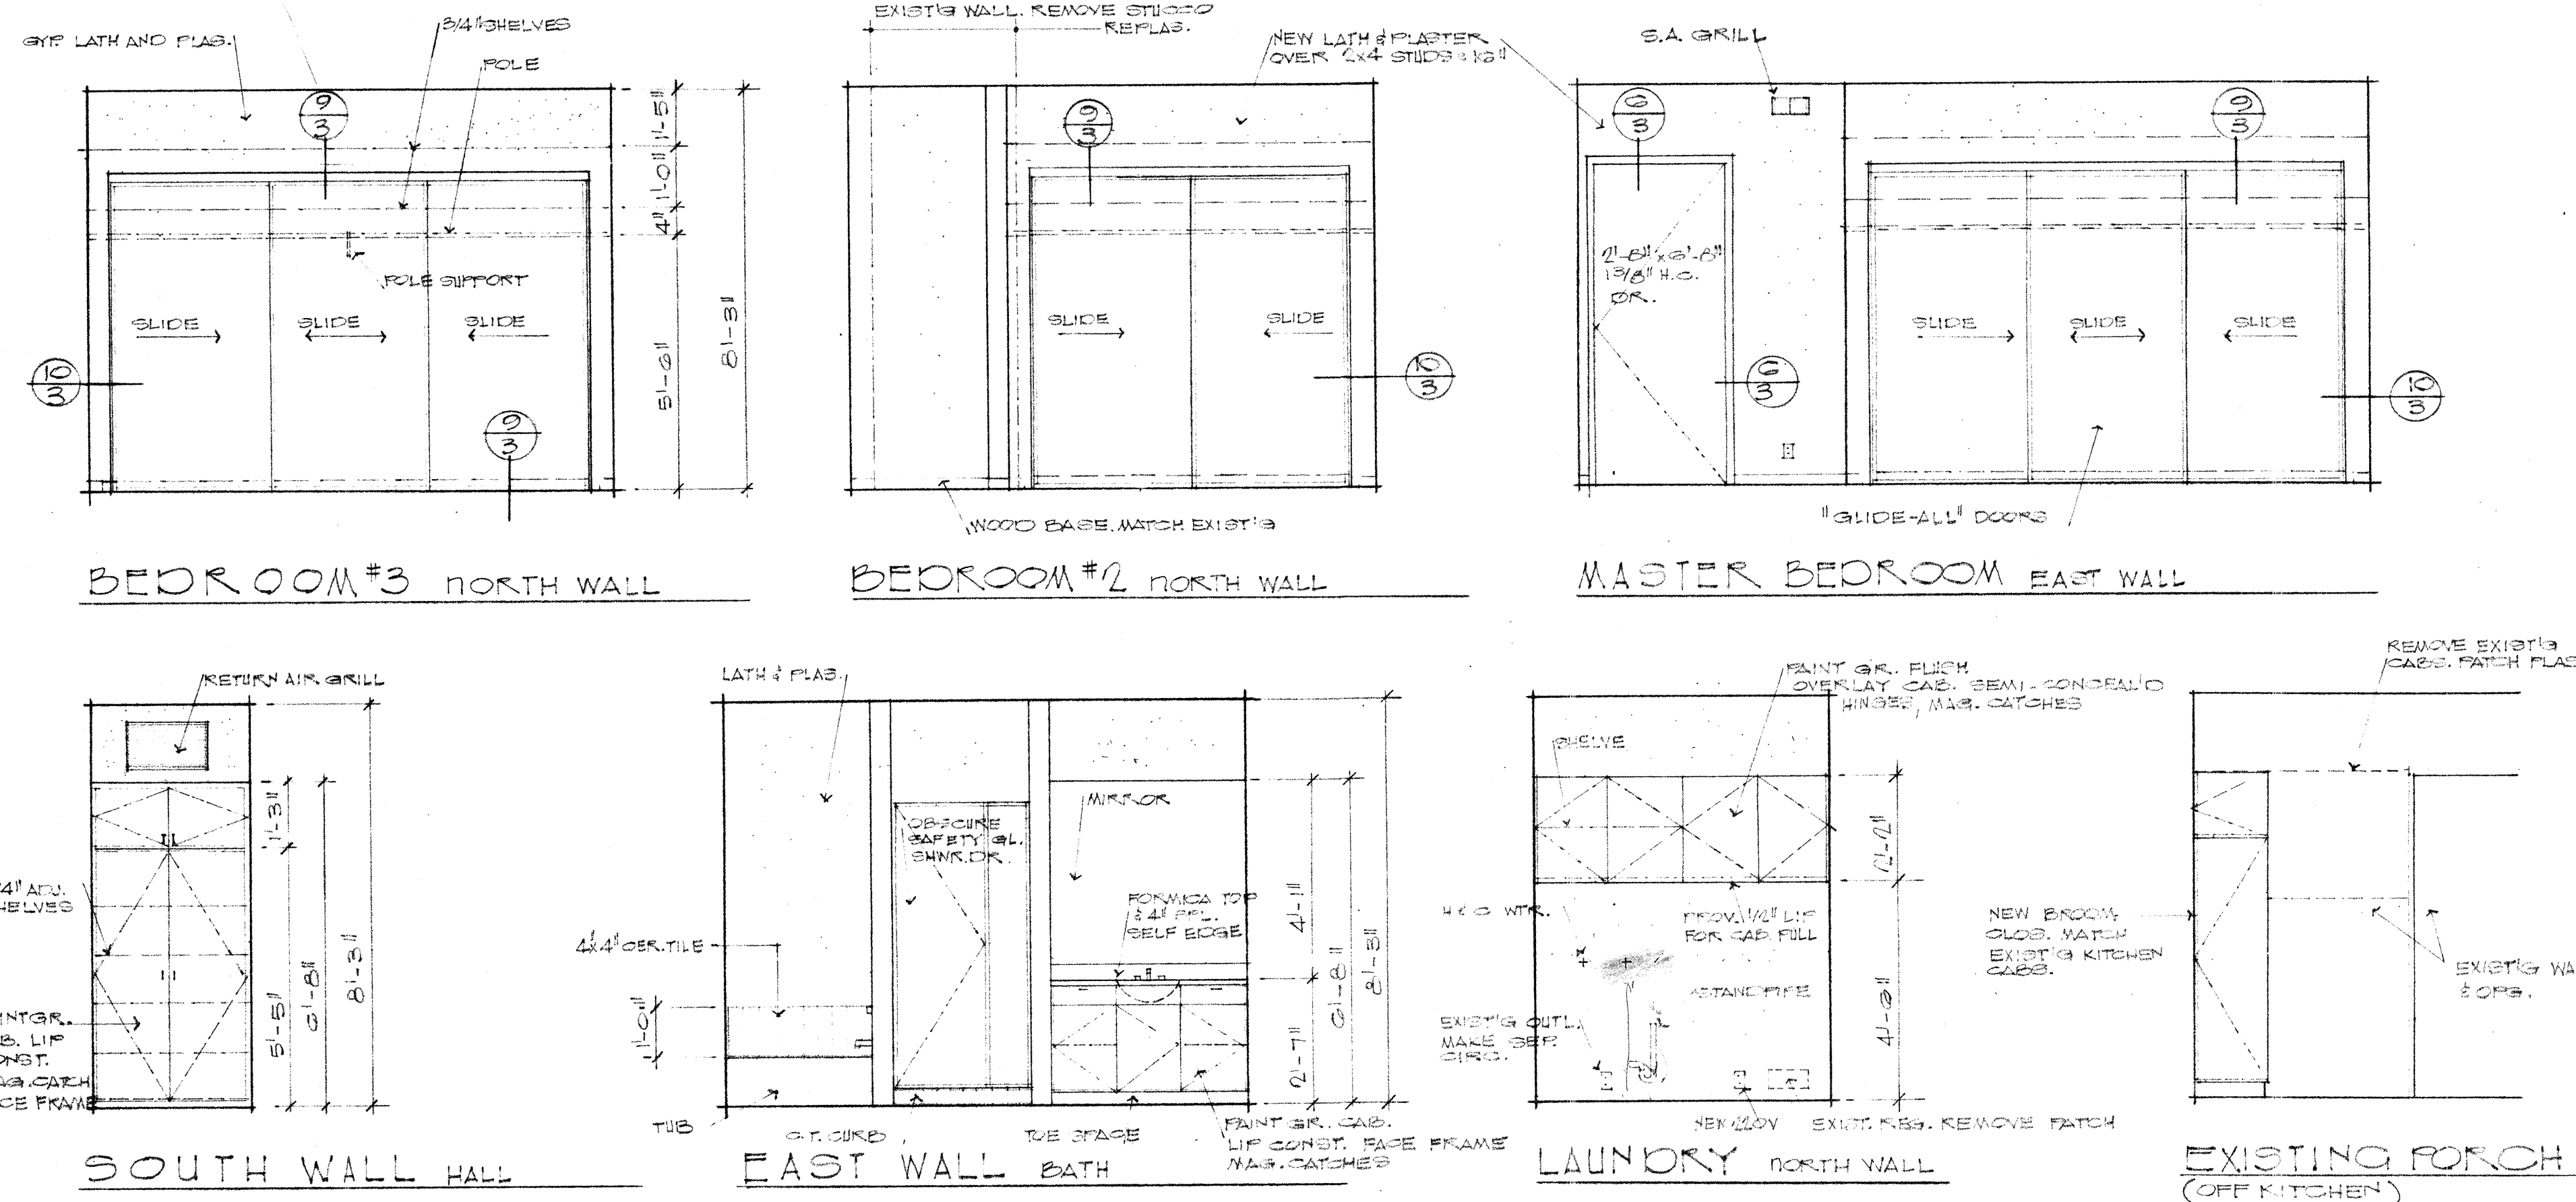


INTERIOR ELEVATIONS

9/8-10 1.

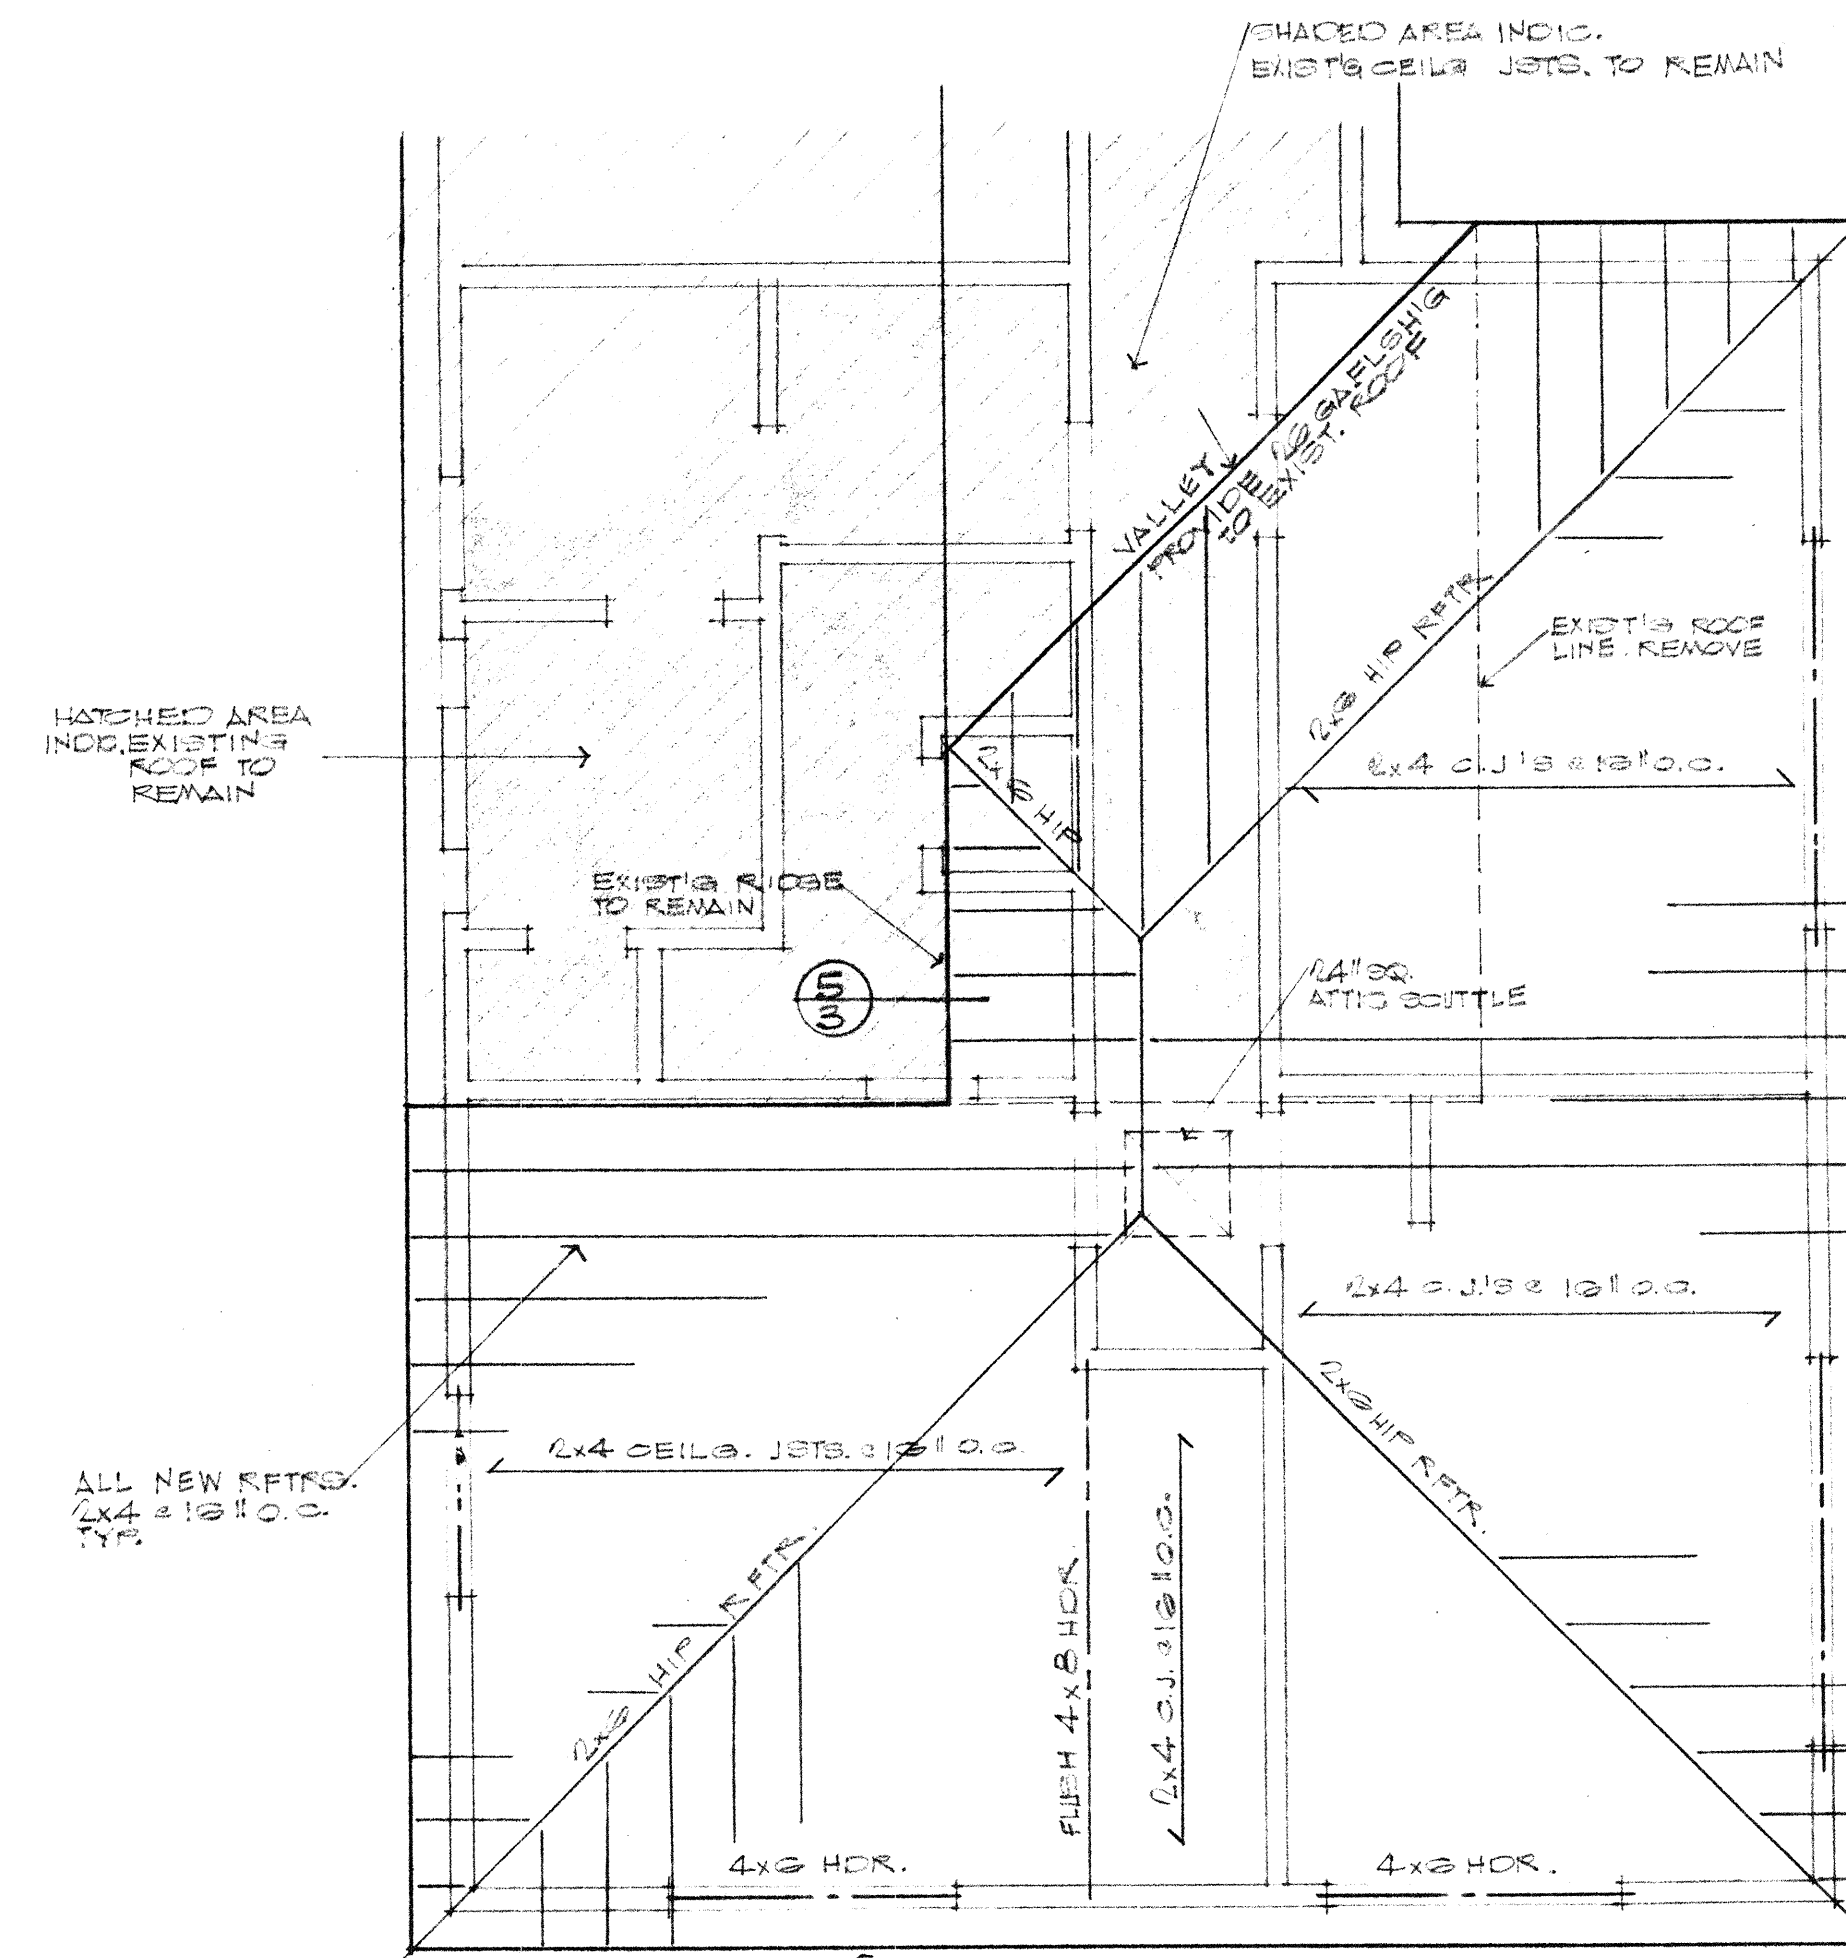


ROOF FRAMING PLAN

14'-0" 2.

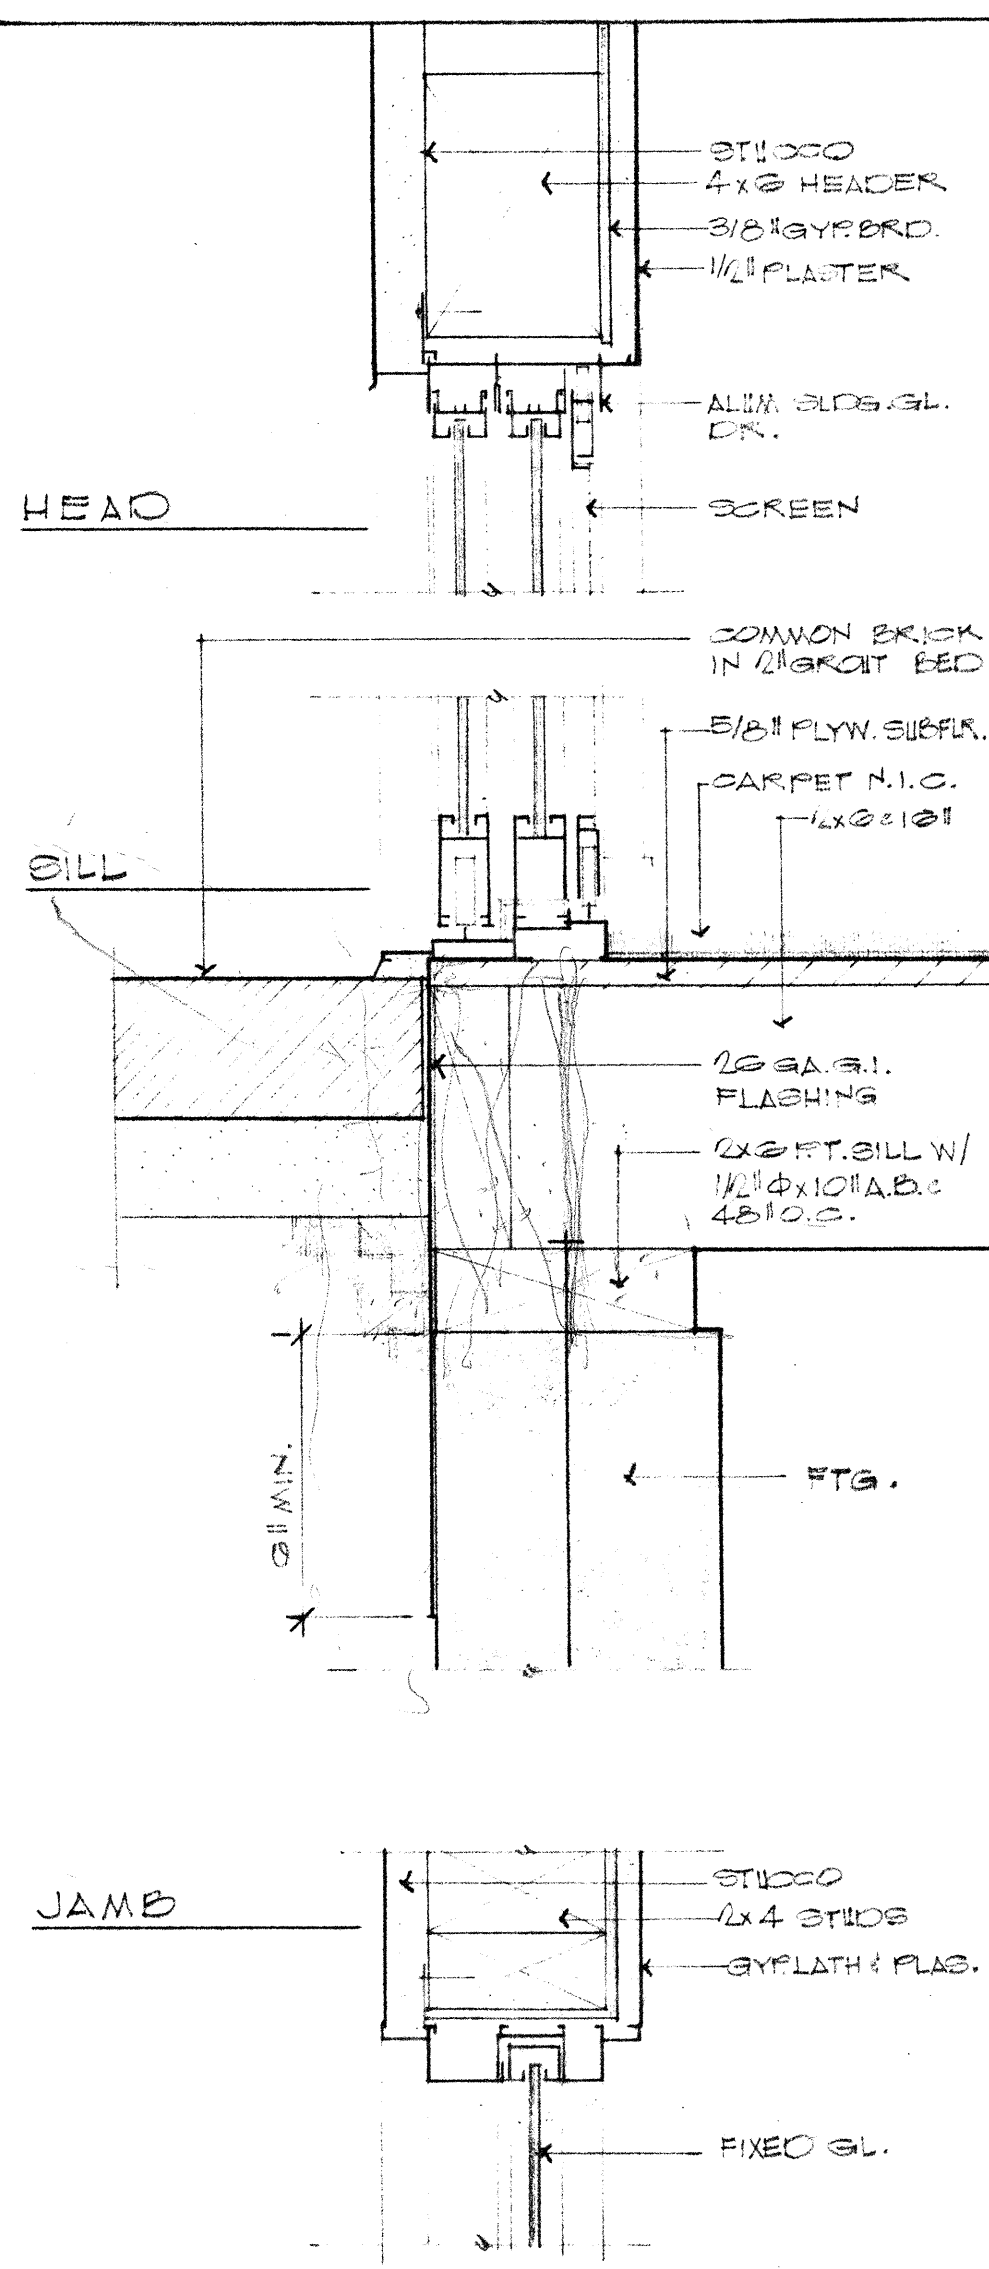


WINDOW DETAILS

3'-0" 4.

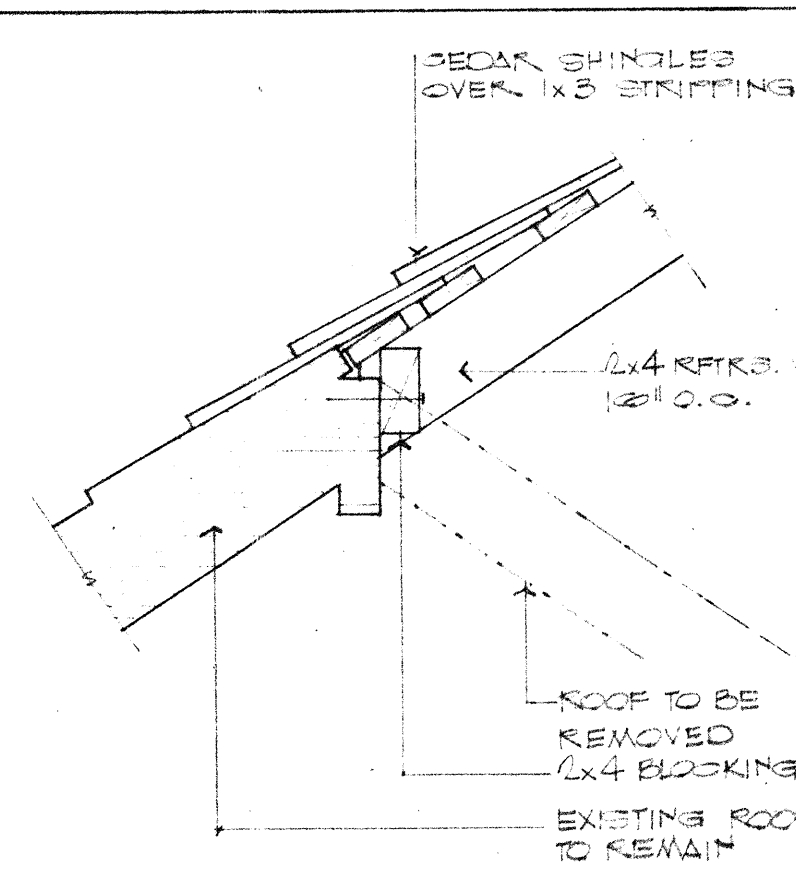


NEW ROOF TO EXISTING

14'-0" 5.

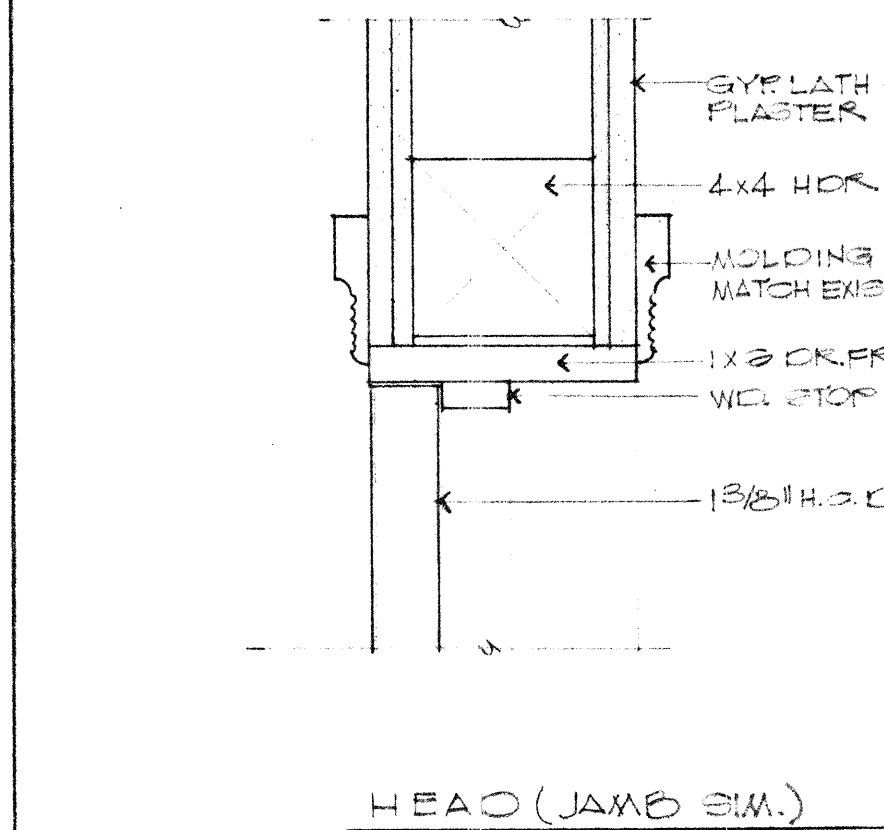


TYP. DOOR DETAIL

3'-0" 6.

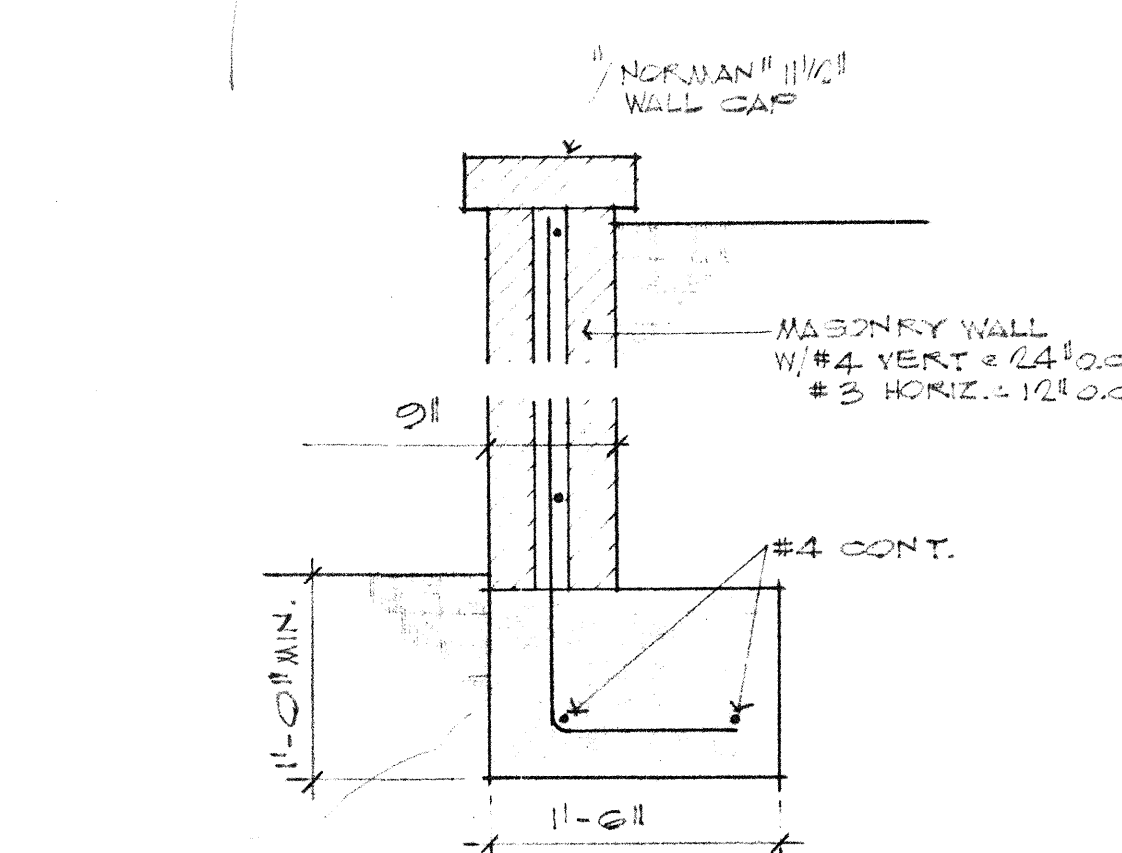

RETAINING WALL

11'-0" 7.

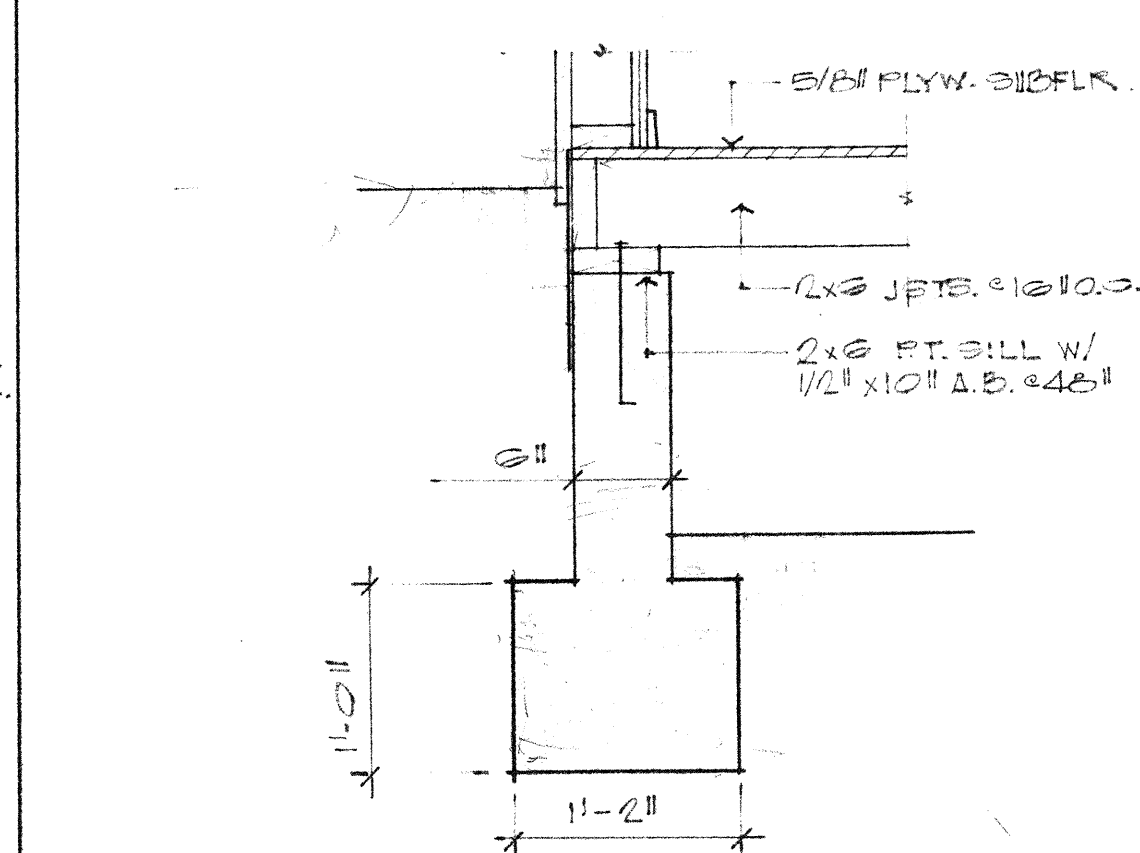

FOOTING

11'-0" 8.

SLOG. DR. DETAILS

WARDROBE DRG.

WARDROBE DRG.

RETAINING WALL

MASONRY WALL

NEW FLOOR TO EXIST'G

Check Print