


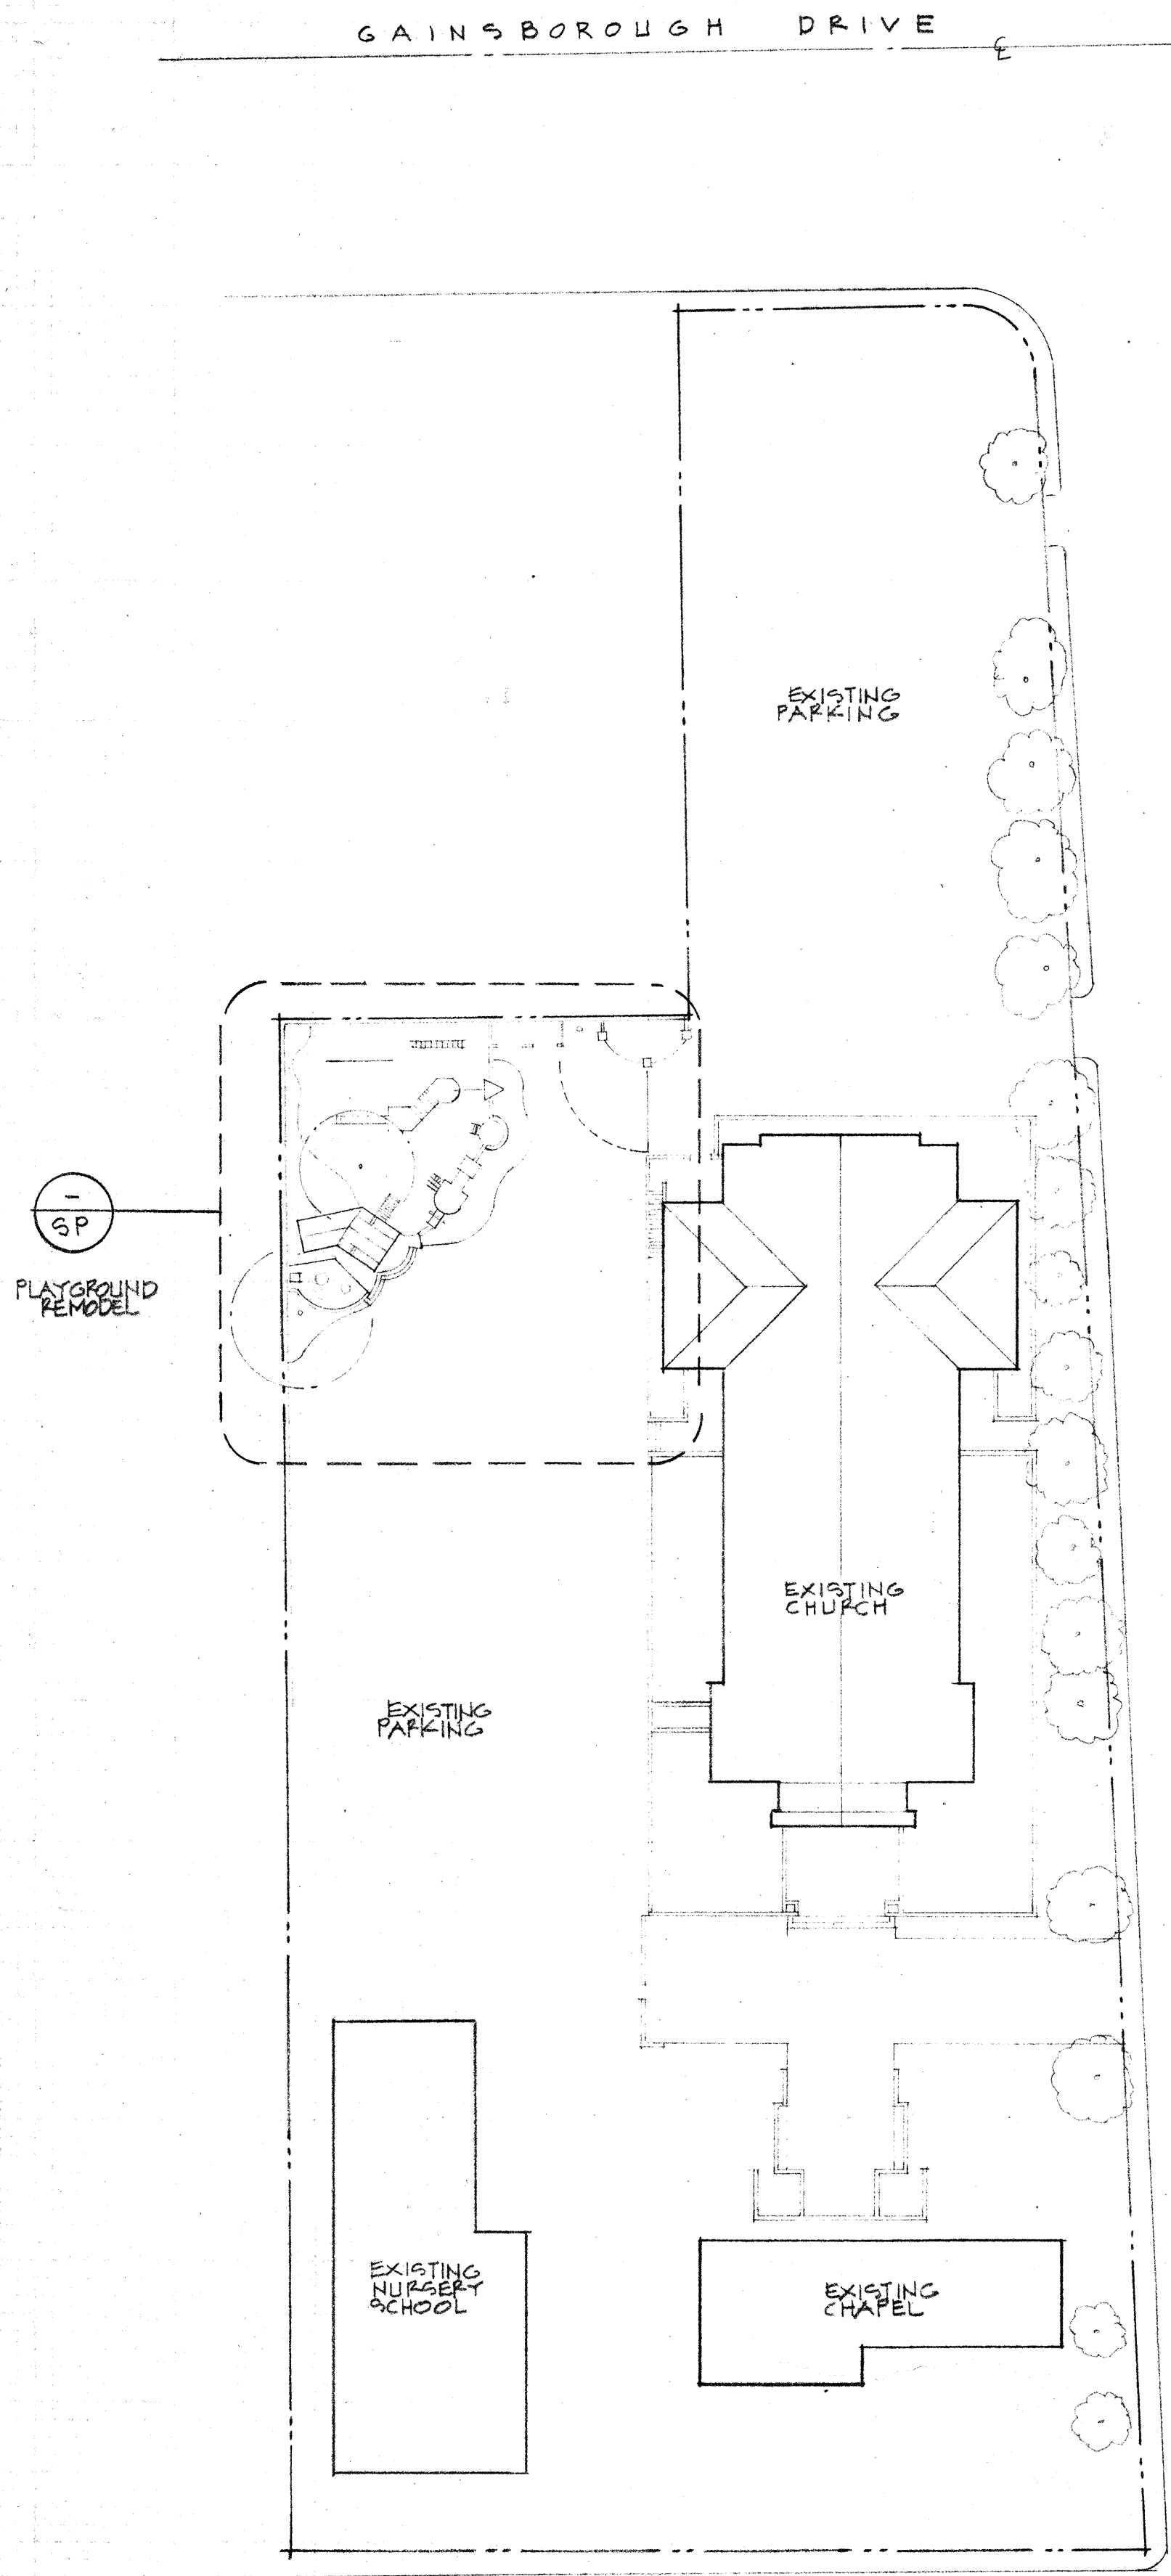

NORTH 1/8" = 1'-0"

Site Plan (Overall)

MATERIAL SPECIFICATIONS

Support Posts: To be select grade 6x6 nominal redwood timbers. All posts shall be surface smooth on all sides. All exposed edges and ends shall be eased by quarter round milling. Finished with linseed oil and petroleum wood sealer.

Railing Posts: To be select grade 4x4 nominal redwood posts. All posts shall be surface smooth on all sides. All exposed edges and ends shall be rounded with a 1/4" radius. Finished with linseed oil and petroleum wood sealer.

Floor Beams: To be selected Douglas Fir (see Calculation and Call Out). All exposed edges shall be rounded with a 1/4" radius.

Platform Decks: Deck planks shall be 3x nominal redwood boards with smooth surface on top. All exposed edges and ends shall be rounded with a 1/4" radius. The planks shall be joined using 1/2" x 4-1/2" lag bolts with 1/2" flat washers countersink heads below finish surface. Finish with linseed oil and petroleum wood sealer.

Redwood Seating Cap At Existing Low C.M.U. Wall: To be select grade redwood 2x12 nominal lumber. All edges shall be rounded with a 1/4" minimum radius, sanded smooth and coated with varathane liquid plastic exterior and marine clear finish.

Top Rails at Balustrades: To be selected grade redwood 2x6 nominal boards. All exposed edges shall be rounded with a 1/4" radius. Finished with linseed oil and petroleum wood sealer.

Shaped Plywood Sheathing Panels: 3/4" plywood, ABX finish grade both sides. Full radius round over all edges. Fasten to top rails, bracing floor joists or timbers with 3/8" x 1-3/4" min. lag bolts with vandal resistant hardware and caps per elevations.

Radius Conical Plywood Sheathing Panels: 3/16" plywood sheets laminated. Outer faces to be finish grade. See Shaped Plywood Sheathing Panels for further specs.

Roof Framing at Play House: To be Douglas Fir Larch No. 2 or better.

Steel Guard Rails, Fire Pole, Climbing Ladder and Hand Rails: Shall provide enclosure, and shall have no gaps greater than 3-1/2" and less than 9", especially between vertical rungs and posts. Rails shall be fabricated from 1-1/2" outside diameter steel pipe. The vertical baluster rungs shall be flattened prior to welding to the horizontal top and bottom rail, and shall be welded around the entire perimeter. Corner brackets and deck mounting plates shall be fabricated from 7 gauge steel and attach to upright posts using 3/8" x 4-1/2" lag bolts.

Painting of Steel Guard Rails, Handrails and Safety Bars: Shall be an electrostatically applied polyester powder coating which shall be cured at temperatures between 400° Fahrenheit and 500° Fahrenheit or equal. The polyester powder shall comply with ASTM standards. Standard color to be determined by Nursery School Playground Committee.

Painting of Douglas Fir: All Douglas Fir framing lumber shall be stained to match the general tone of the ciled redwood. One or two coats of olympic water repellent oil stain shall be used in a semi-transparent color.

Painting of Top Rail Balustrades: The playhouse loft balustrade and stair balustrades on Structure C shall be sanded smooth and the redwood top rail cap shall be painted with Varathane Liquid Plastic Exterior & Marine Clear Finish.

Painting of Plywood Panels: All exposed slots or gaps in plywood laminations and radius edges shall be filled with Bondo and all plywood panels shall be painted with at least two (2) coats of gray oil base primer with special emphasis at all radius panel edges. The finished color coat shall be high gloss acrylic paint in colors to be chosen by the Nursery School Playground Committee.

Painting of Exposed G.I. Flashing: Any G.I. flashing that is going to be exposed shall be painted with Krylon spray paint in semi-gloss finish to match adjacent surfaces or a color to be selected by the Nursery School Playground Committee.

Vandal Resistant Hardware Caps: All lag screws used to attach plywood panels to framing shall have a black nylon protective cap over the exposed hex head. Part No. RH-20 Protective Cap and Washer Clip available through Zal Fastener Supply Company, 4905 Telegraph Road, Los Angeles, CA 90022, Attn: Danny Villanueva, Tel. (213) 262-0259.

Alternative Bid to Redwood: Alaskan Yellow Cedar may be used in place of redwood. Contact Craftsman Millworks, 351 Country Club Drive, San Gabriel, CA 91775, Attn: Robert Kinorid, Tel. (310) 865-5266.

Concrete: fm - 1500 psi

Mortar: Type M or S

Structural Steel: Shapes, Plates and Bars: ASTM A36
Bolts: ASTM A307

Framing Hardware: Simpson Strong Tie Connectors or equal. Unless specified otherwise, all "HL" plates shall have a minimum of four (4) bolts with a bolt edge distance of four (4) bolt diameters minimum (i.e., on a 5/8" bolt the edge distance would be 2-1/2" minimum).

Drawing Index

CS	Cover Sheet - Site Plan (Overall), Specifications, Drawing Index
DP	Demolition Plan
SP	Site Plan
PH - 1.0	Playhouse Floor Plans
PH - 2.0	Playhouse Exterior Elevations
PH - 2.1	Playhouse Sections
PH - 3.0	Playhouse Structural Plans
PH - 4.0	Playhouse Details
PH - 4.1	Playhouse Details
E - 1.0	Painting Easel Details
A - 1.0	Playstructure "A" - Plans and Structural Plans
A - 2.0	Playstructure "A" - Elevations and Sections
A - 4.0	Playstructures "A" and "B" - Details and Sections
B - 1.0	Playstructure "B" - Plans, Structural Plans, Elevations
C - 1.0	Playstructure "C" - Plan, Foundation Plan
C - 2.0	Playstructure "C" - Elevations
C - 2.1	Playstructure "C" - Footing Details, Master Elevations
C - 3.0	Playstructure "C" - Framing Plan, Sections, Details
TS - 1.0	Tricycle Shed - Plan, Section, Elevation, Details
EP - 1.0	Entry Patio - Plan, Section, Elevation, Details

Slide: All metal slide chute Model 612-C designed for a 6' high platform, approximately 12' long. Contact L.A. Steelcraft Products, Inc., 1974 Lincoln Avenue, Pasadena, CA, Tel. (818) 798-7401.

Climbing Net: For a 59" high platform. 3-strand twist nylon rope, 1/2" diameter with 525# work load minimum.

Gear Shift: For use on climbing Structure "A", Model #M533. Contact Kompan, P.O. Box 1010, Forestville, CA 95436, Attn: Cecily Beckwith, (800) 222-9046.

Binoculars: For use on climbing Structure "B", (1) Kompan Model #M547 and (2) Model #M208110.

Water Hen: For use in sandbox near playhouse, Kompan Model #M560.

Rotating Table: For use in sandbox near playhouse, Model #M571, Contact Kompan, P.O. Box 1010, Forestville, CA 95436, Attn: Cecily Beckwith, (800) 222-9046.

Sand Table: For use in sandbox near playhouse, Model #M570, Contact Kompan, P.O. Box 1010, Forestville, CA 95436, Attn: Cecily Beckwith, (800) 222-9046.

"D" Gym Rings With Steel Bearing Connector Clips: Qty. = 5 for use on Structure "C". Contact Playwell, 655 S. Raymond Avenue, Pasadena, CA, Tel. (818) 793-0603.

Steering Wheels: Qty. = 2 tender tuff coated in color to be determined by Nursery School Playground Committee. Contact Playwell, 655 S. Raymond Avenue, Pasadena, CA, Tel. (818) 793-0603.

Note to Builder: Each individual piece of hardware, apparatus and attachment, as well as the layout of the entire play area should be constantly evaluated during construction, with special consideration given to specifications, spacings, openings and protrusions. Guidelines can be found in the "Handbook for Public Playground Safety", Publication #325, U.S. Consumer Product Safety Commission, Washington D.C. 20207, Tel. (800) 638-8270.

ZONING APPROVAL
5-28-97 by [Signature]
date
SAN MARINO BUILDING DEPT.

APPROVED PLAN
5-28-97 by [Signature]
date
SAN MARINO BUILDING DEPT.

Dube'
Donnelly
Designs

Phillip Dube'
Tel: (818) 799-3379
722 Garfield Ave
So Pasadena, Ca 91030

Brian Donnelly
Tel: (310) 371-7701
3644 Del Amo Blvd - C
Torrance, Ca 90503

CREATIVE
Planning & Design

Saint Edmund's Nursery School
Playground Remodel
1175 San Gabriel Boulevard
San Marino, California 91108-8038
Ph: (818) 792-7742

The drawings and specifications are instruments of service and remain the property of Dube' Donnelly Designs whether the project is executed or not. The drawings and specifications shall not be used by the owner on other projects, additions to this project, or for the completion of this project by others, provided that Dube' Donnelly Designs is not in default under this agreement, except by agreement in writing and appropriate compensation to Dube' Donnelly Designs shall be deemed the author of the drawings and specifications and shall retain all common law, including copyright. All rights reserved.

MAY 08 1997
Date
Scale
B.D.
Drawn
ST. EDMUND'S
Job

CS