




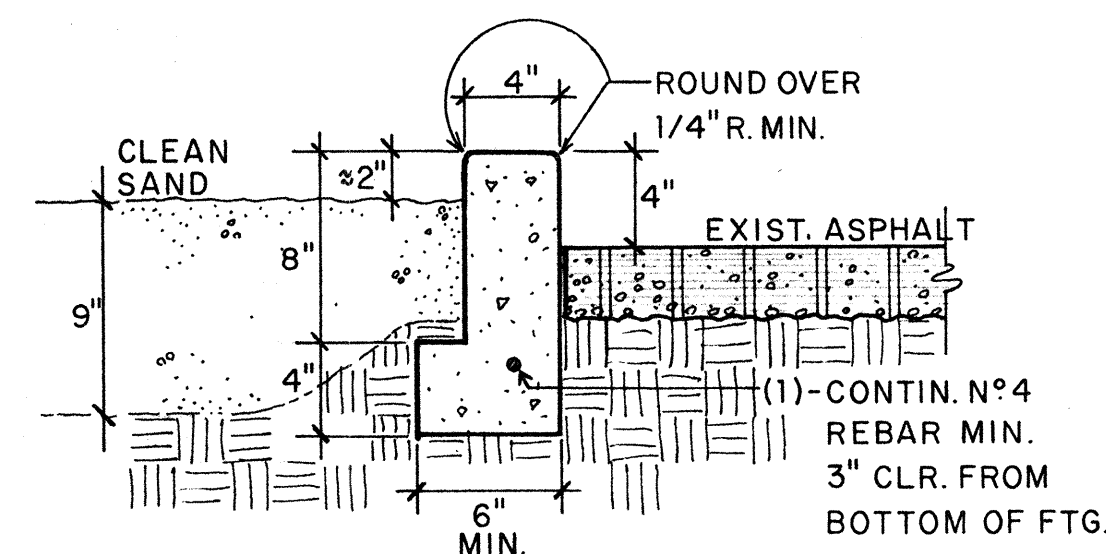


1 UNDULATING CURB DETAIL
1/2" = 1'-0"

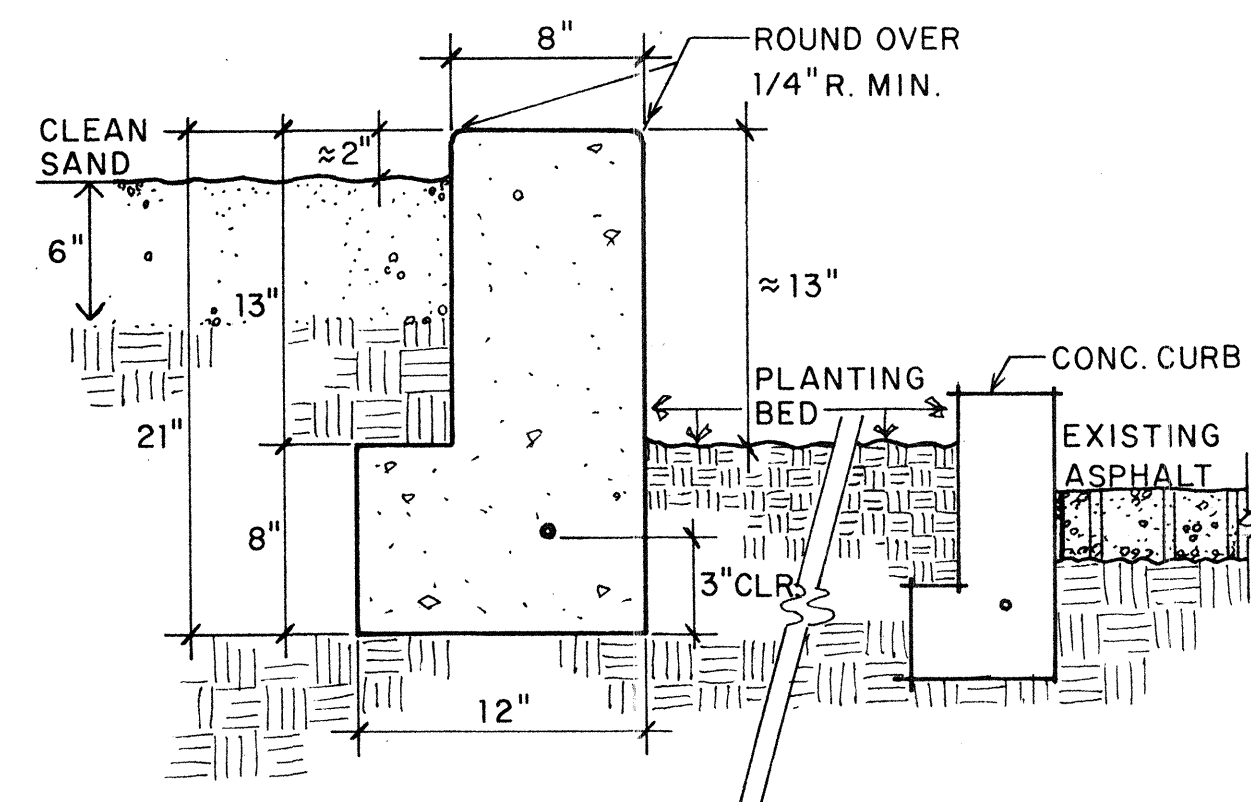


2 WALL DETAIL
1/2" = 1'-0"

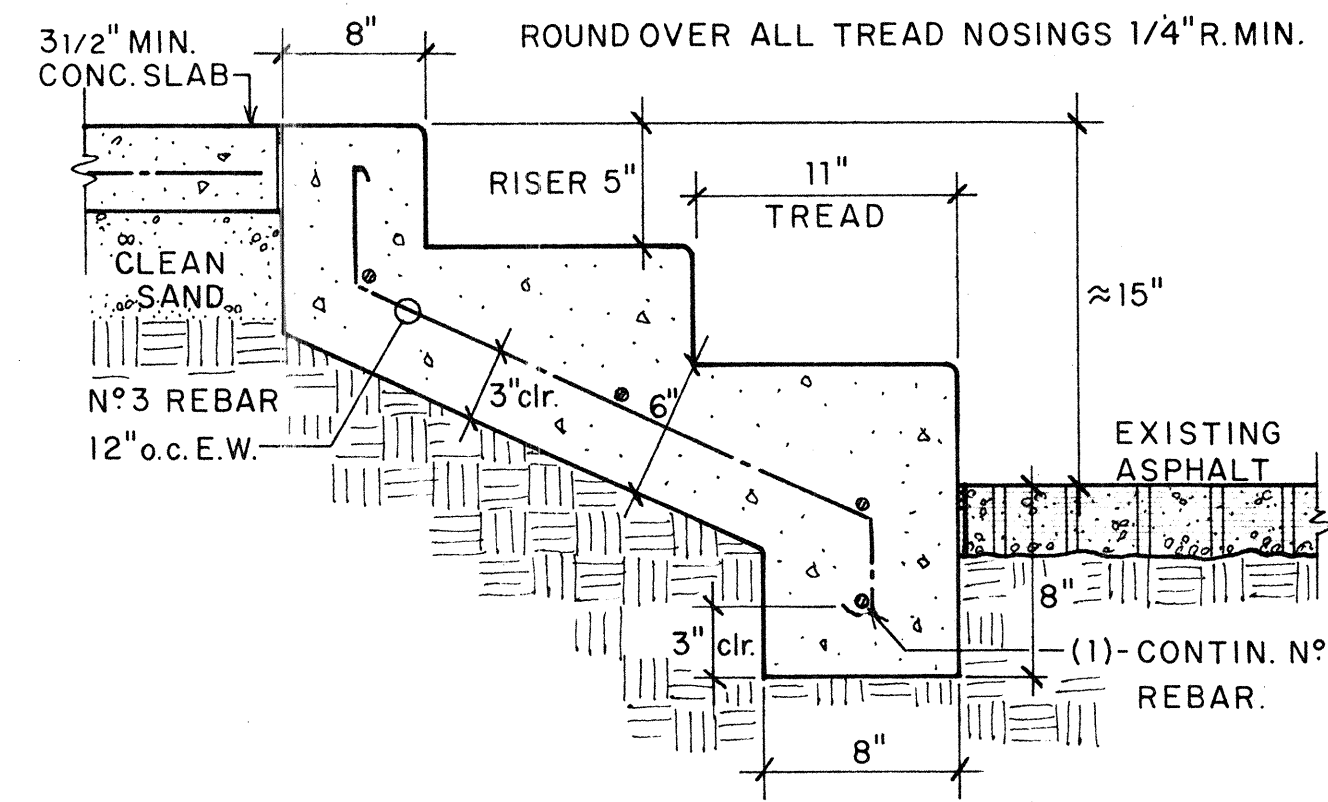


3 CONCRETE STAIR DETAIL
1/2" = 1'-0"

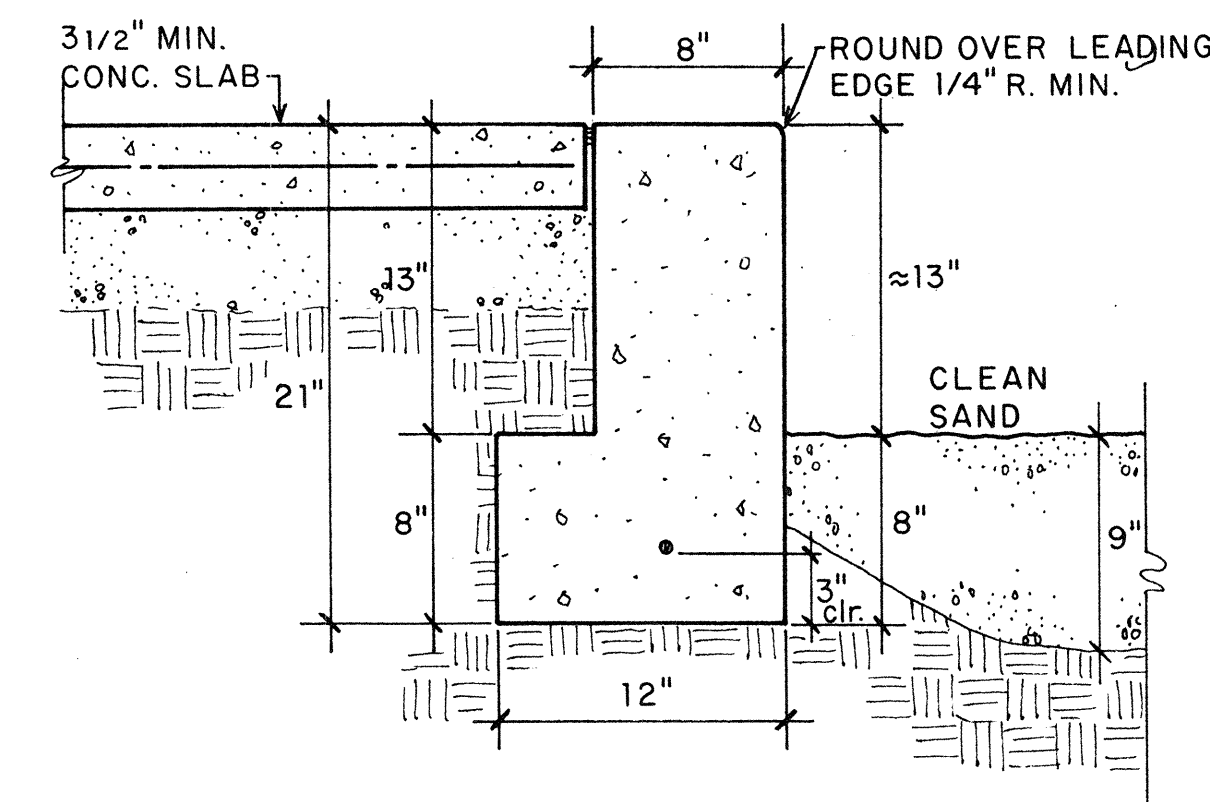

4 WALL DETAIL
1/2" = 1'-0"

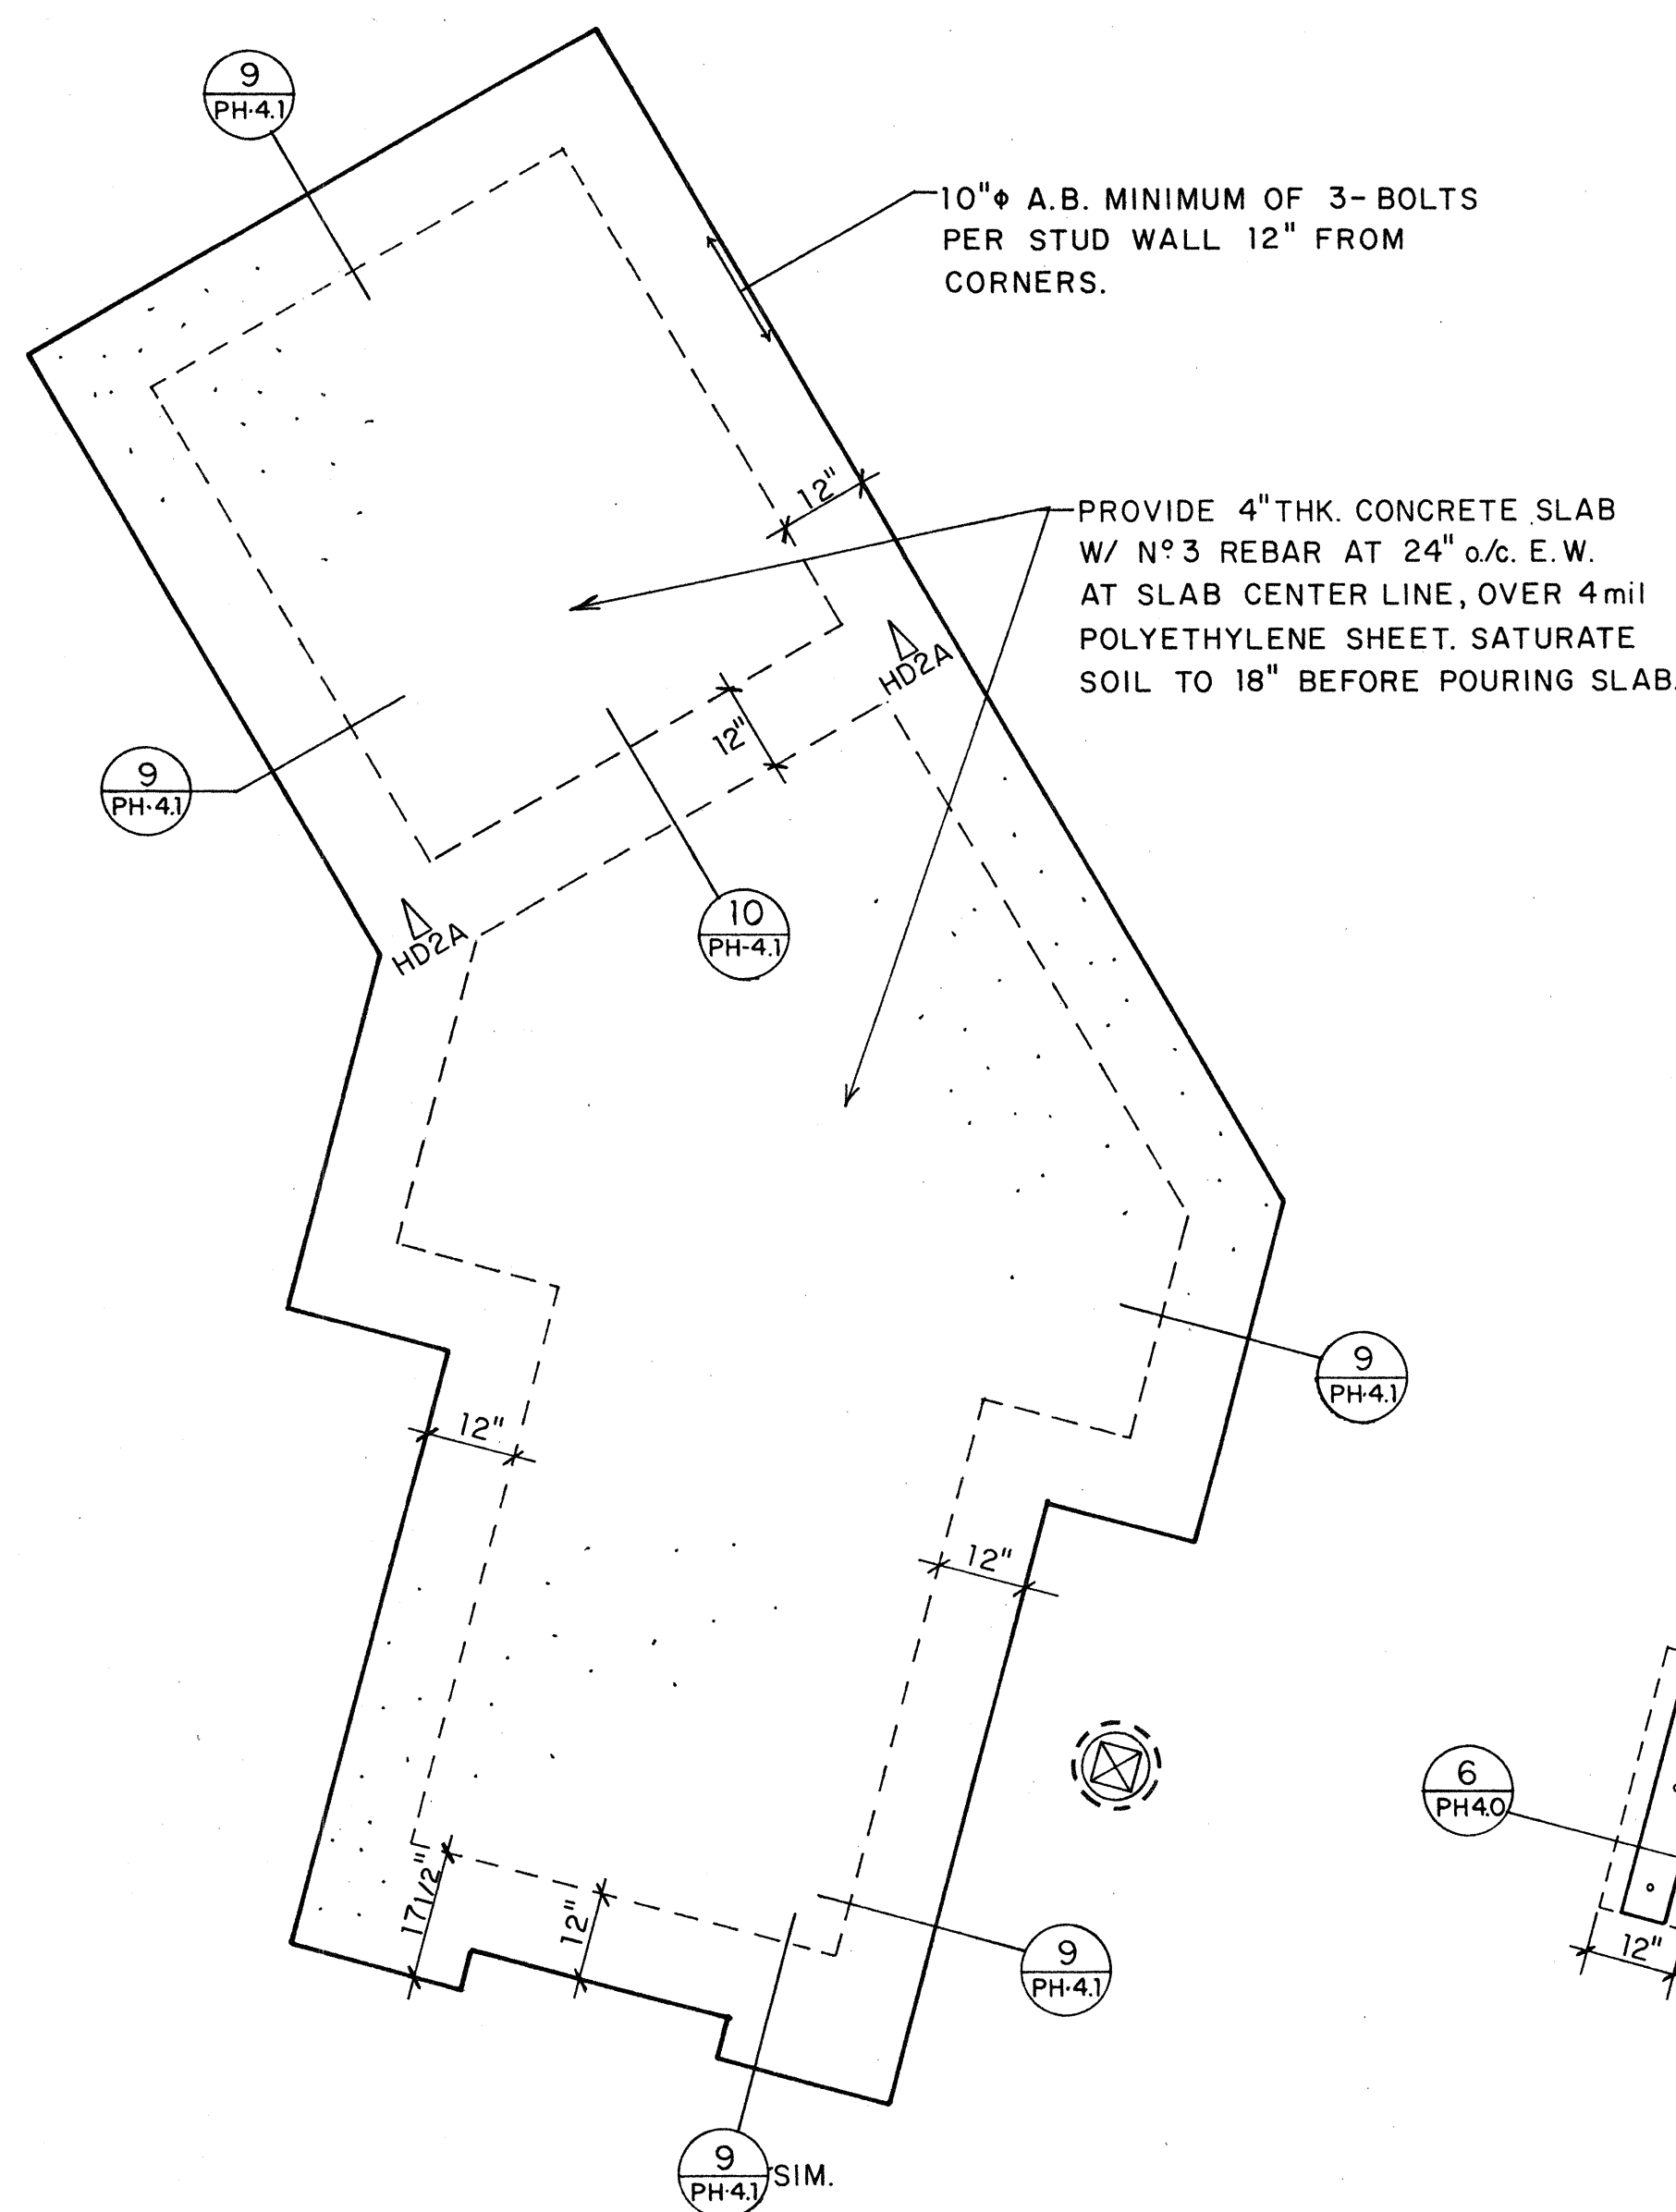

FOUNDATION PLAN
1/2" = 1'-0" north

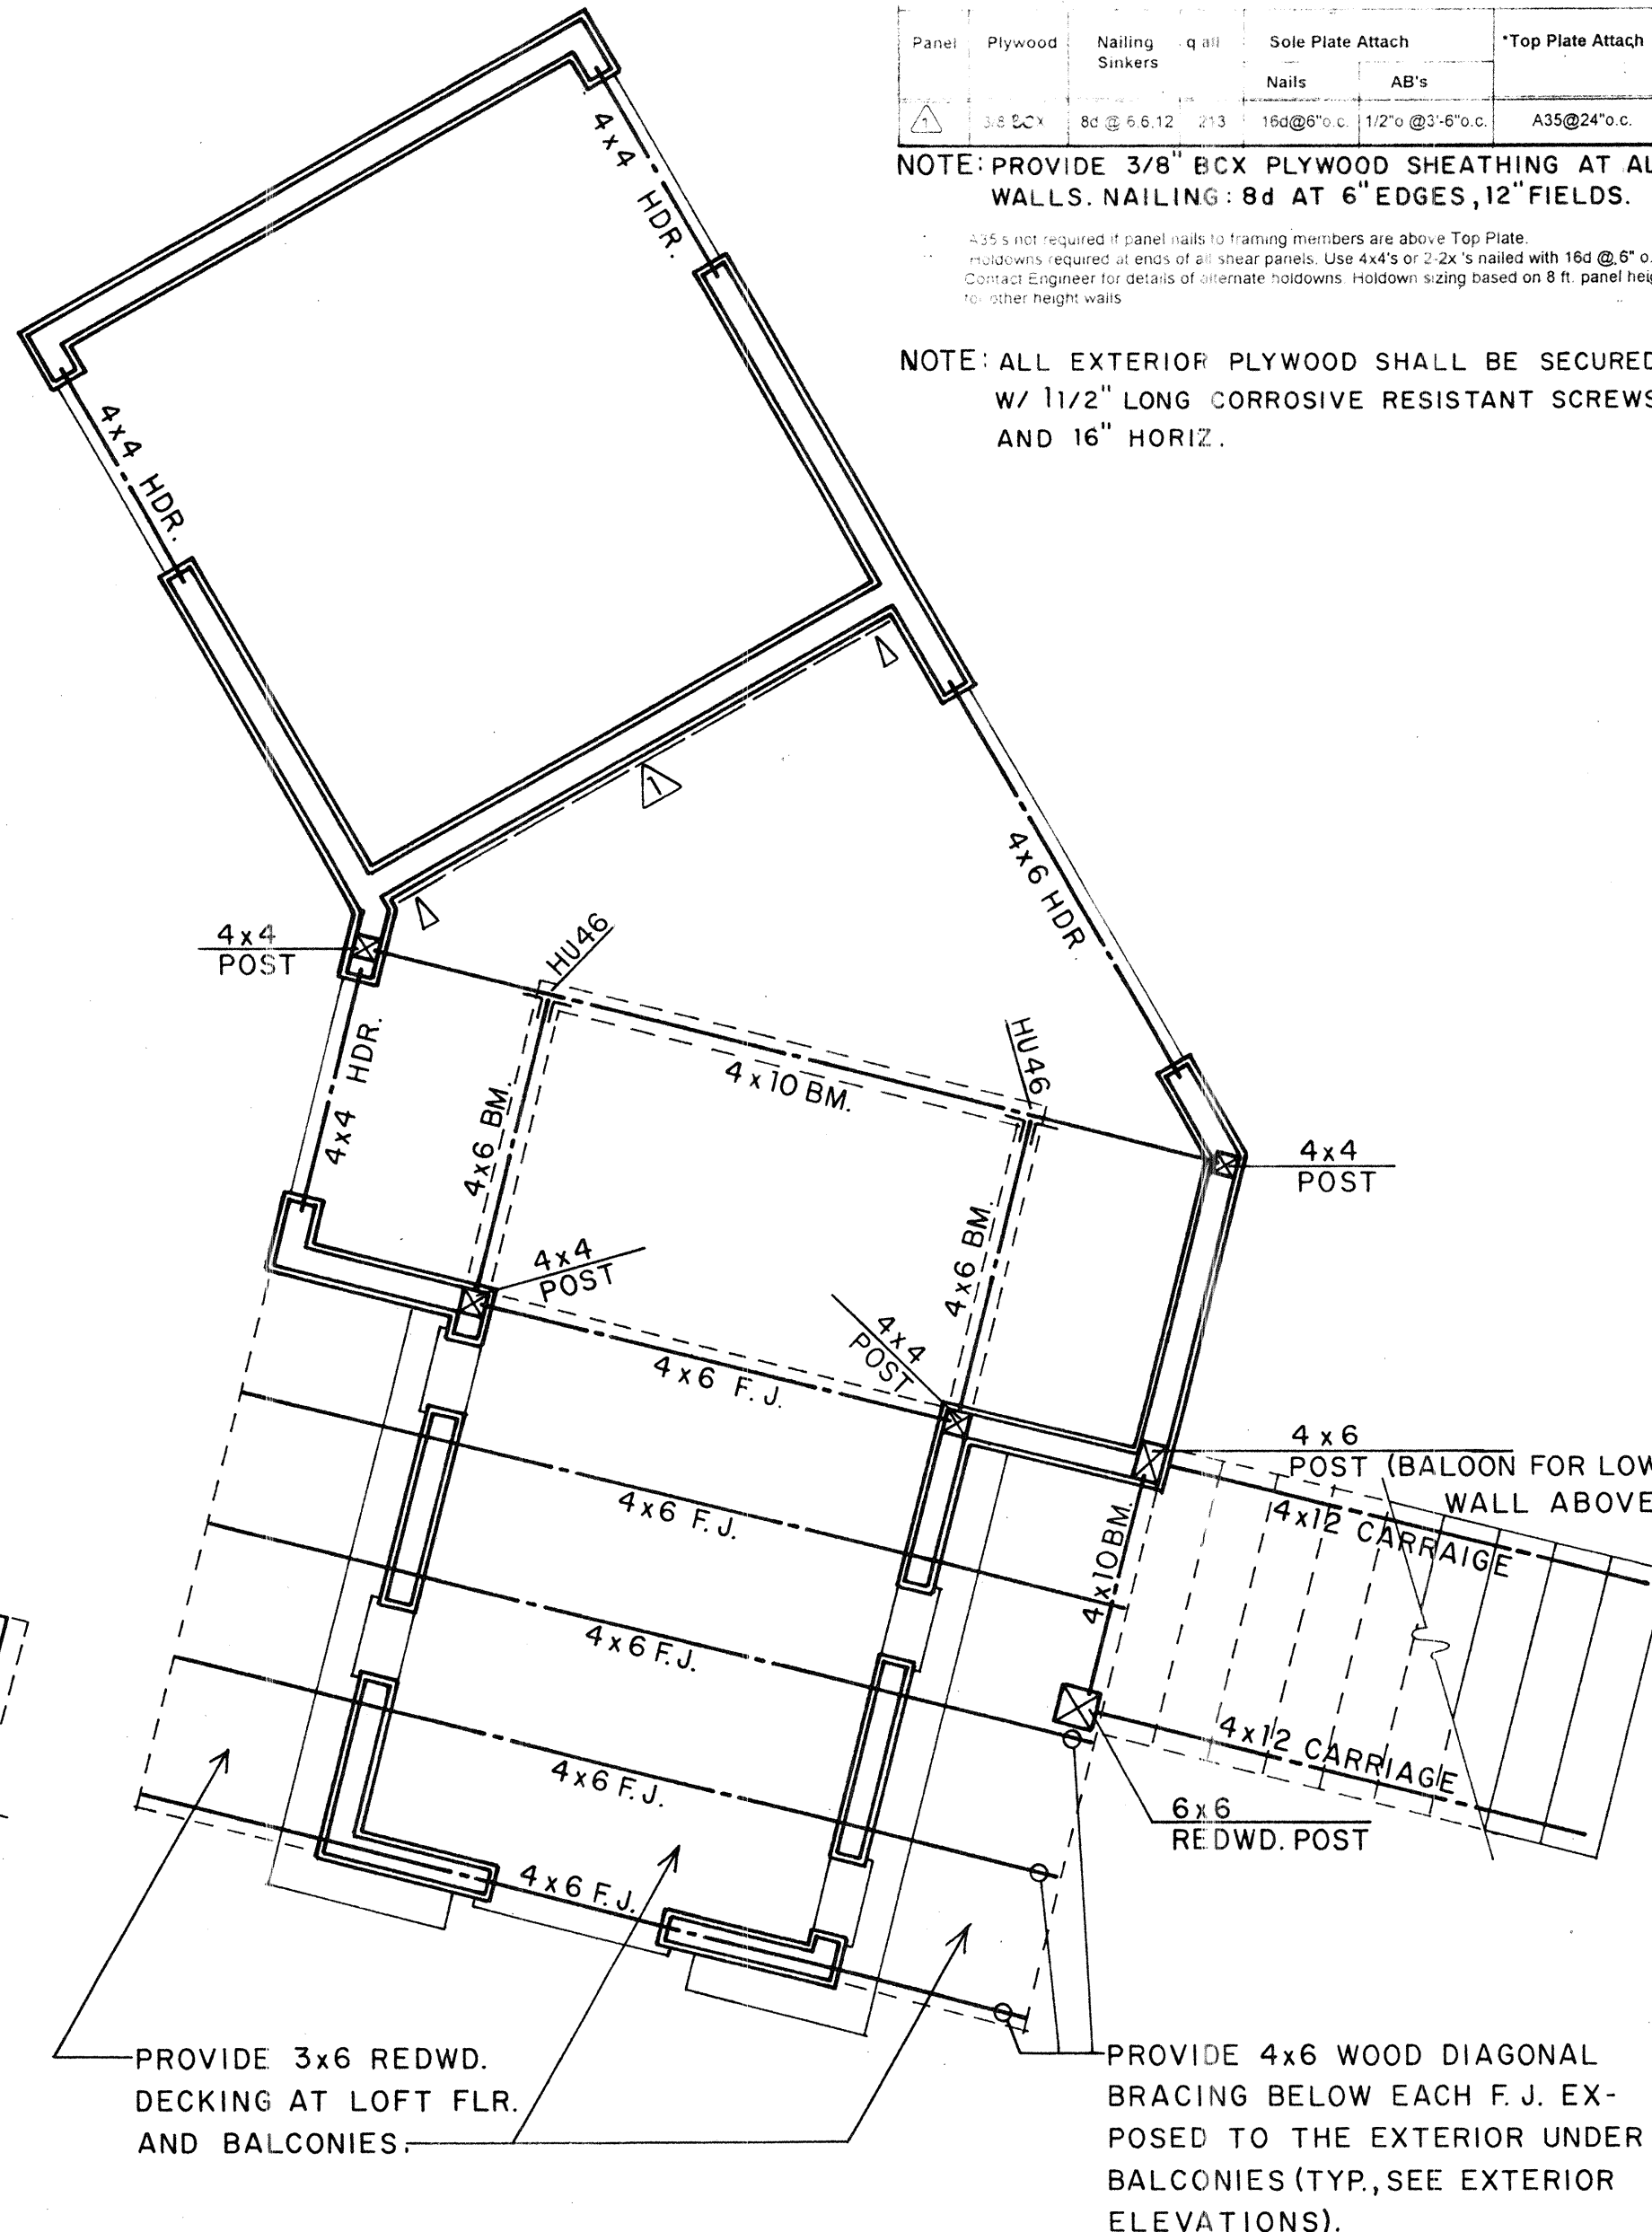


FRAMING PLAN
1/2" = 1'-0" north

Shear Panel Schedule

Panel	Plywood	Nailing Sinks	q all	Sole Plate Attach	Top Plate Attach	**Holddown
1	3/8 CDX	8d @ 6" o/c	2/3	16d @ 6" o/c	12" o @ 3'-6" o/c	A35 @ 24" o/c
2	3/8 CDX	8d @ 6" o/c	2/3	16d @ 6" o/c	12" o @ 3'-6" o/c	A35 @ 24" o/c


NOTE: PROVIDE 3/8" BCX PLYWOOD SHEATHING AT ALL INTERIOR WALLS. NAILING: 8d AT 6" EDGES, 12" FIELDS.

NOTE: ALL EXTERIOR PLYWOOD SHALL BE SECURED TO FRAMING W/ 11/2" LONG CORROSIVE RESISTANT SCREWS AT 12" VERT. AND 16" HORIZ.

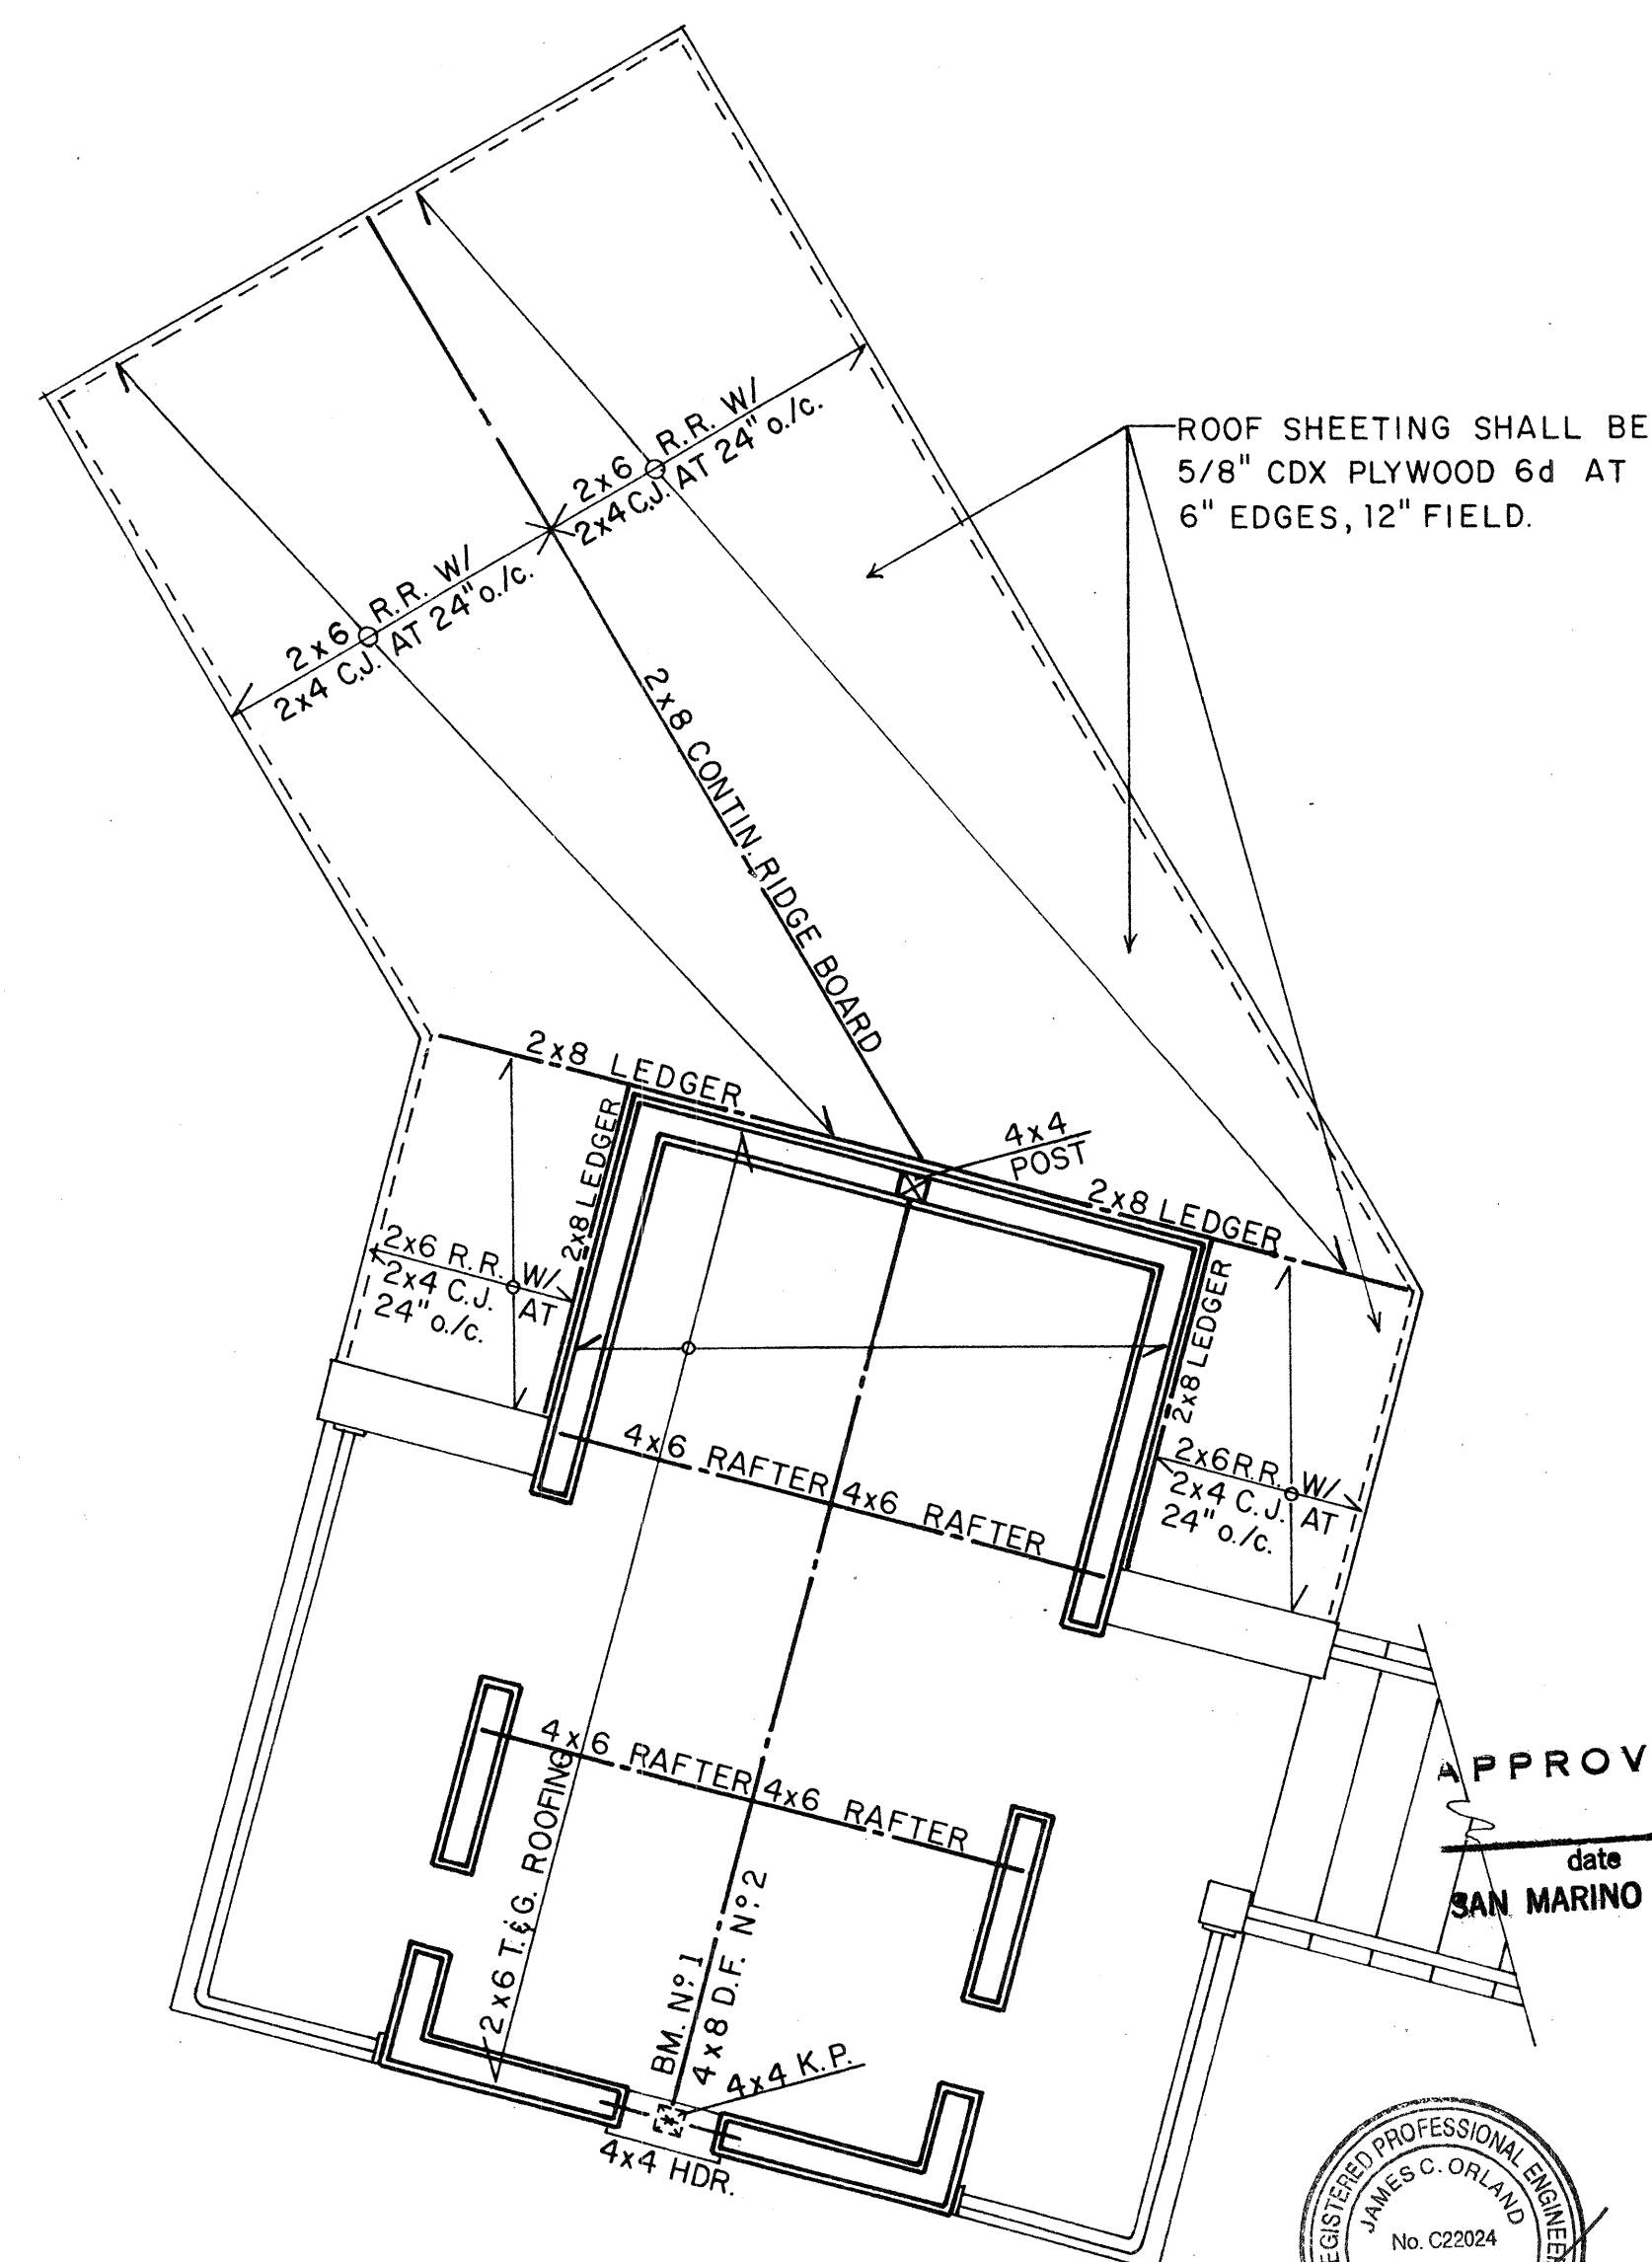

ROOF FRAMING PLAN
1/2" = 1'-0" north

APPROVED PLAN
date
SAN MARINO BUILDING DEPT.

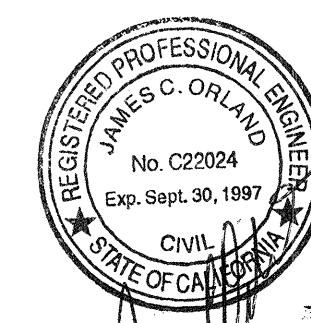

Dube' Donnelly Designs

Phillip Dube'
Tel: (818) 799-3379
722 Garfield Ave.
So. Pasadena, Ca. 91030

Brian Donnelly
Tel: (310) 371-7701
3644 Del Amo Blvd. - C
Torrance, Ca. 90503

CREATIVE Planning & Design

Saint Edmund's Nursery School
Playground Remodel
1175 San Gabriel Boulevard
San Marino, California 91108-8038
Ph: (818) 792-7742

The drawings and specifications are instruments of service and remain the property of Dube' Donnelly Designs whether the project is executed or not. The drawings and specifications shall not be used by the owner on other projects, additions to this project, or for the completion of this project by others, provided that Dube' Donnelly Designs is not in default under this agreement, except by agreement in writing and appropriate compensation to Dube' Donnelly Designs shall be deemed the author of the drawings and specifications; and shall retain all common law, including copyright. All rights reserved.

MAY 08 1997
Date
Scale NOTED
Drawn PSD
Job SENS

PH-3.0