




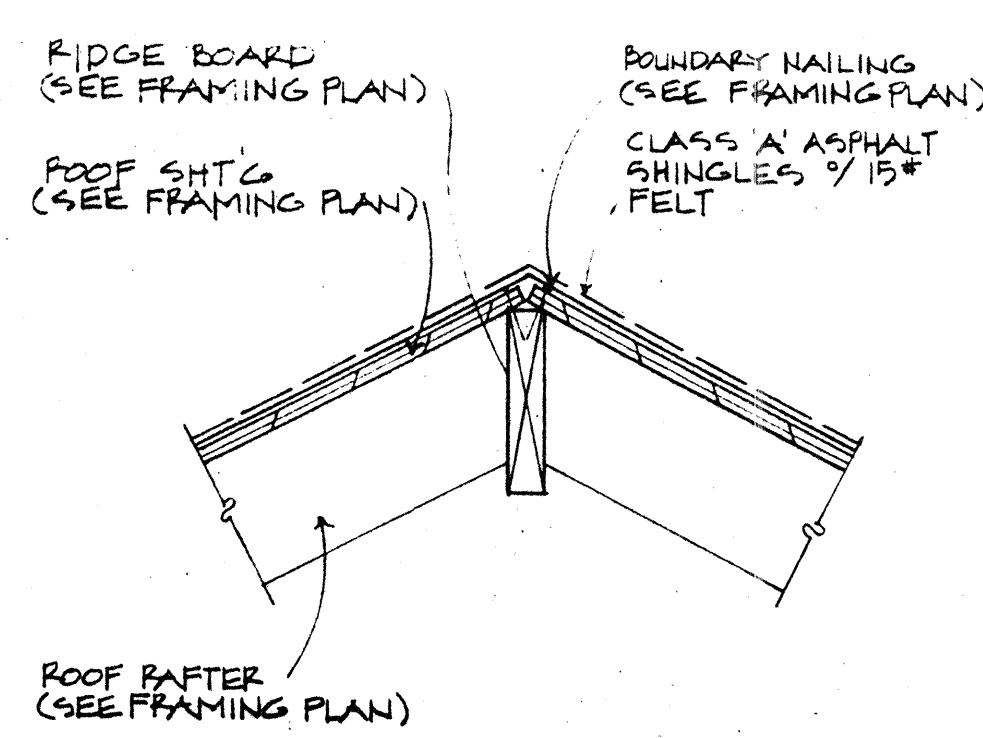


7 RIDGE DETAIL
1/2" = 1'-0"

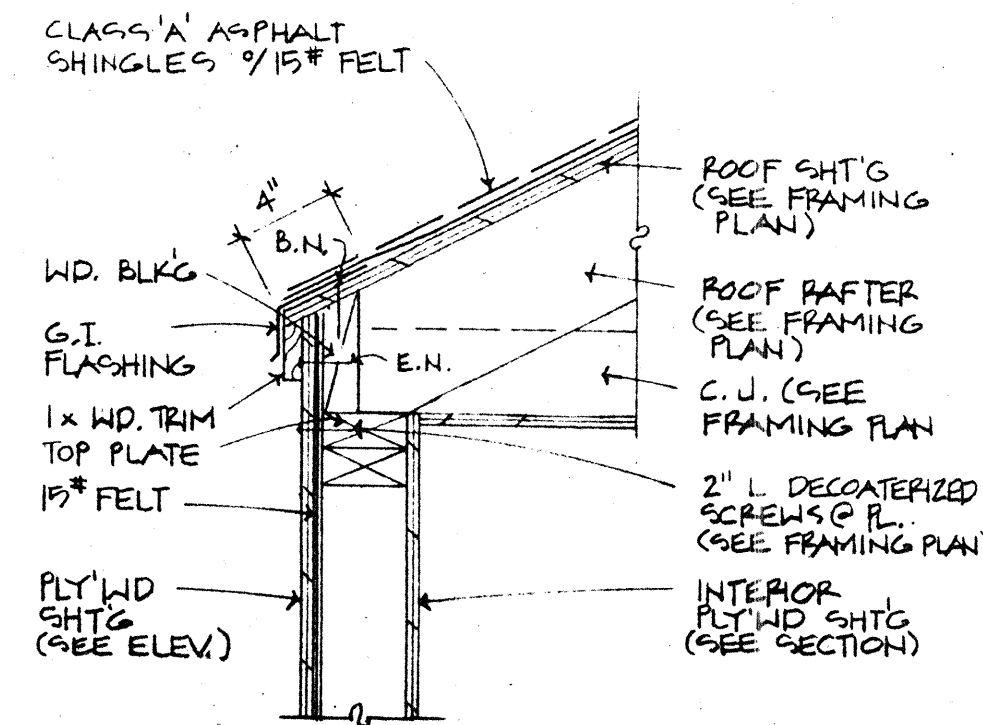


8 EAVE DETAIL
1/2" = 1'-0"

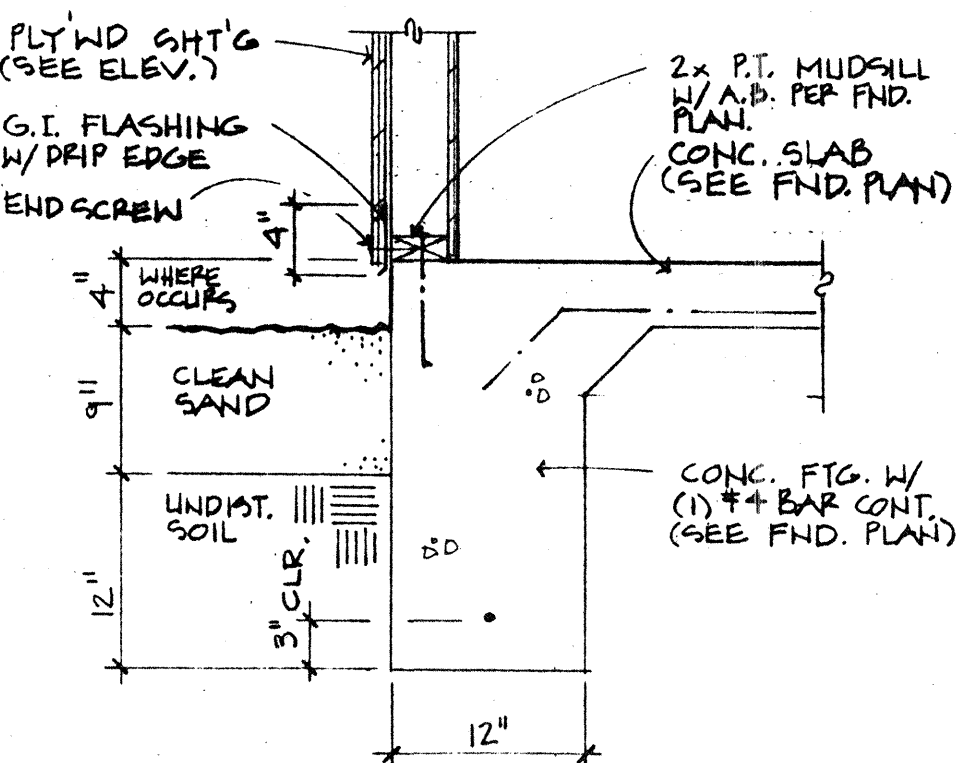


9 FTG DETAIL
1" = 1'-0"

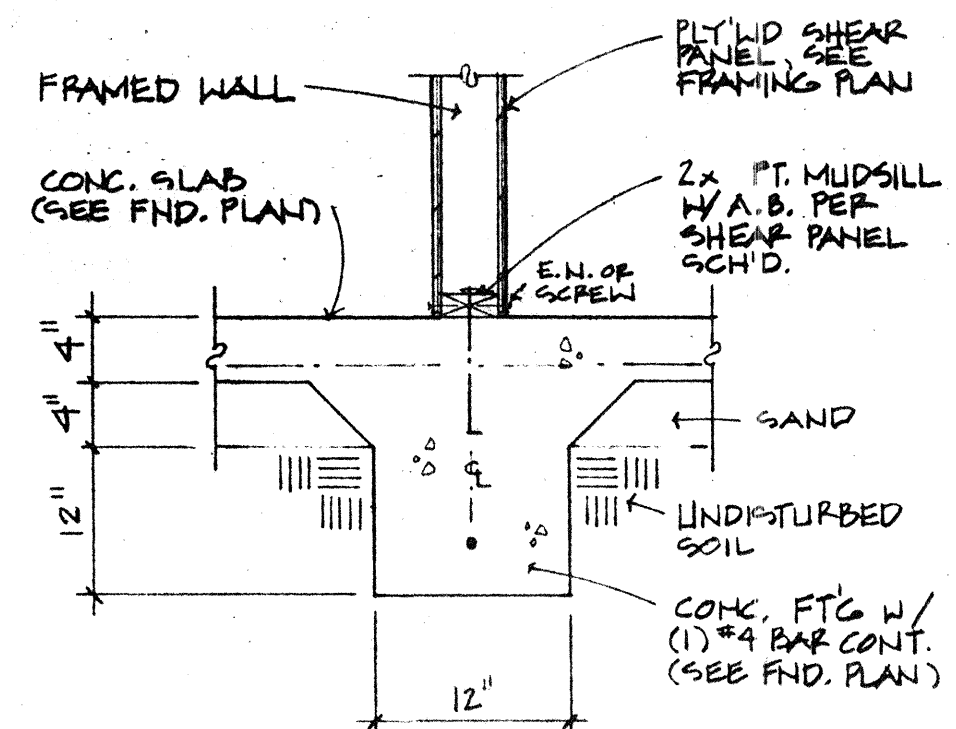


10 FTG DETAIL
1" = 1'-0"

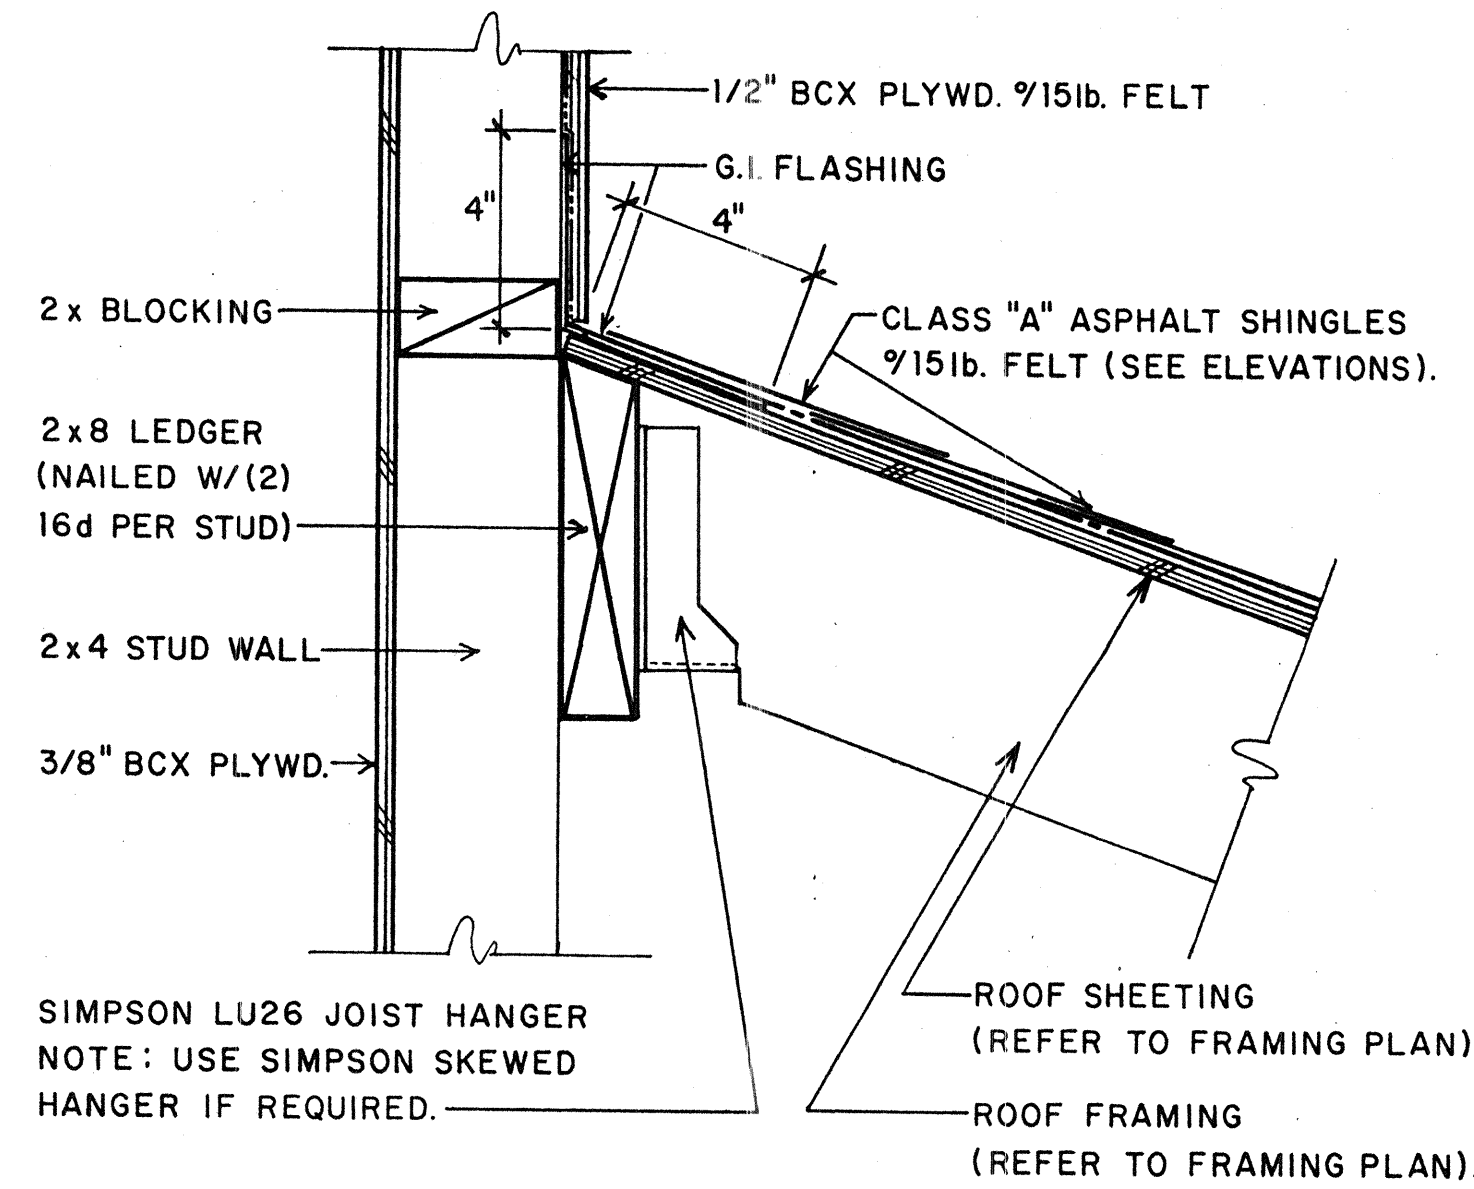


4 WALL TO ROOF DETAIL
3" = 1'-0"

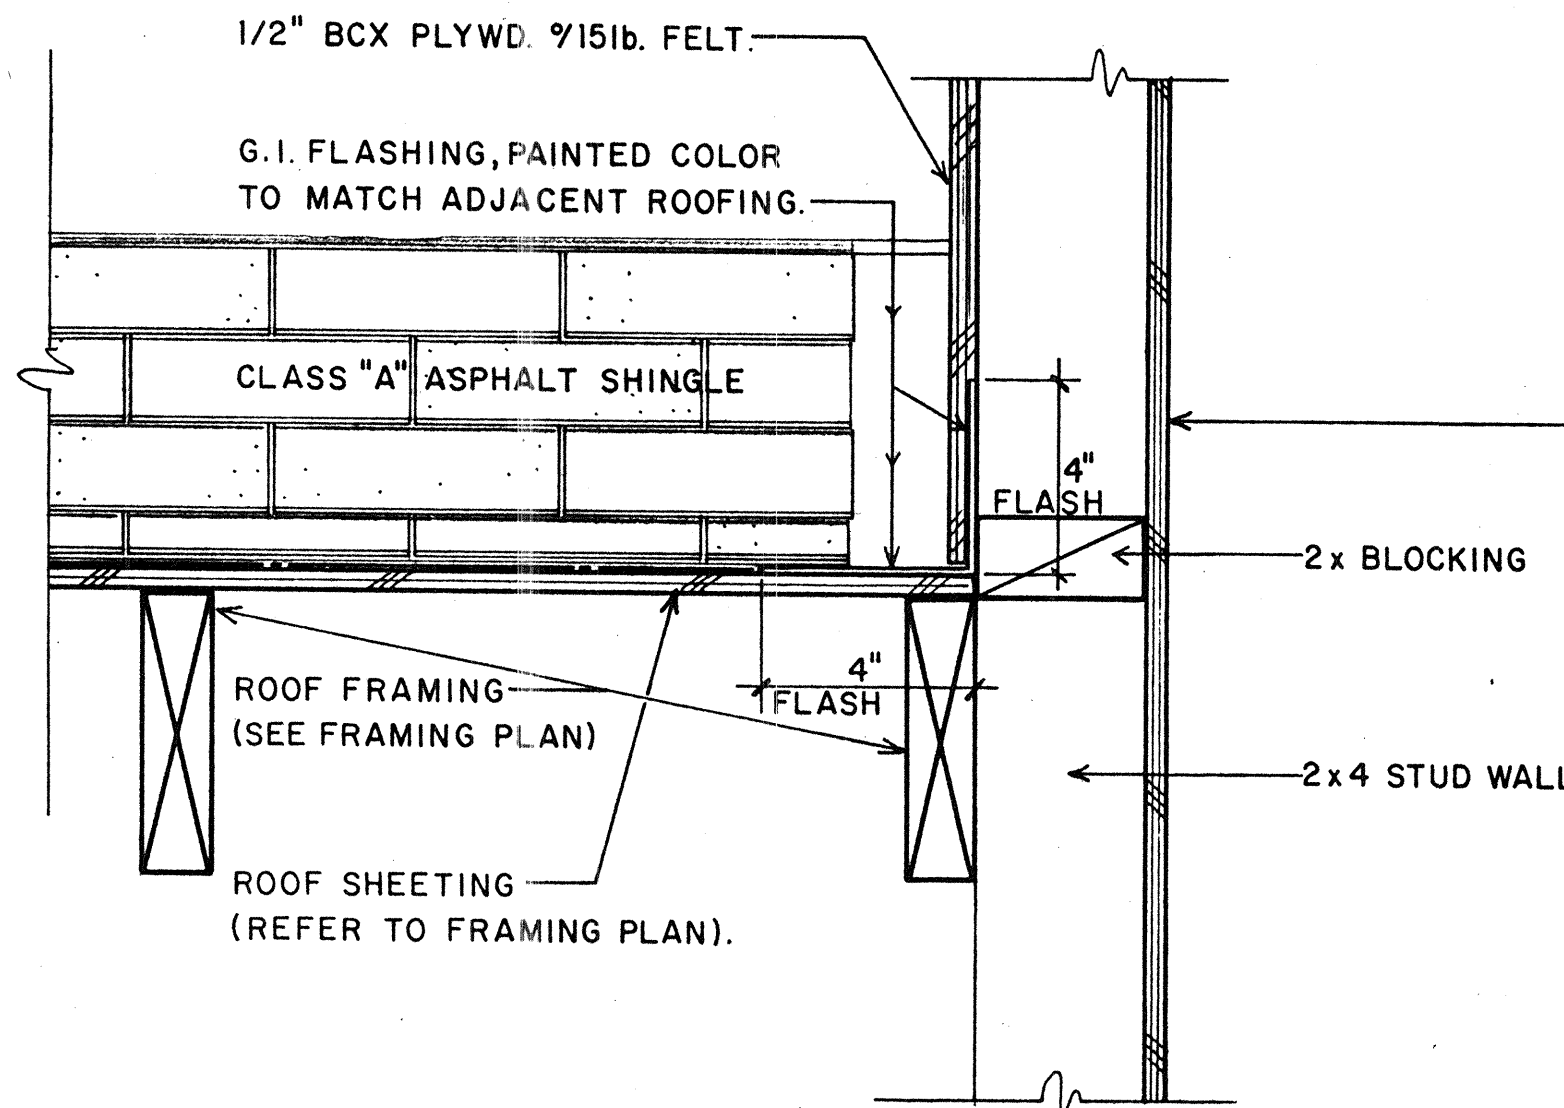


5 WALL TO ROOF RAKE DETAIL
3" = 1'-0"

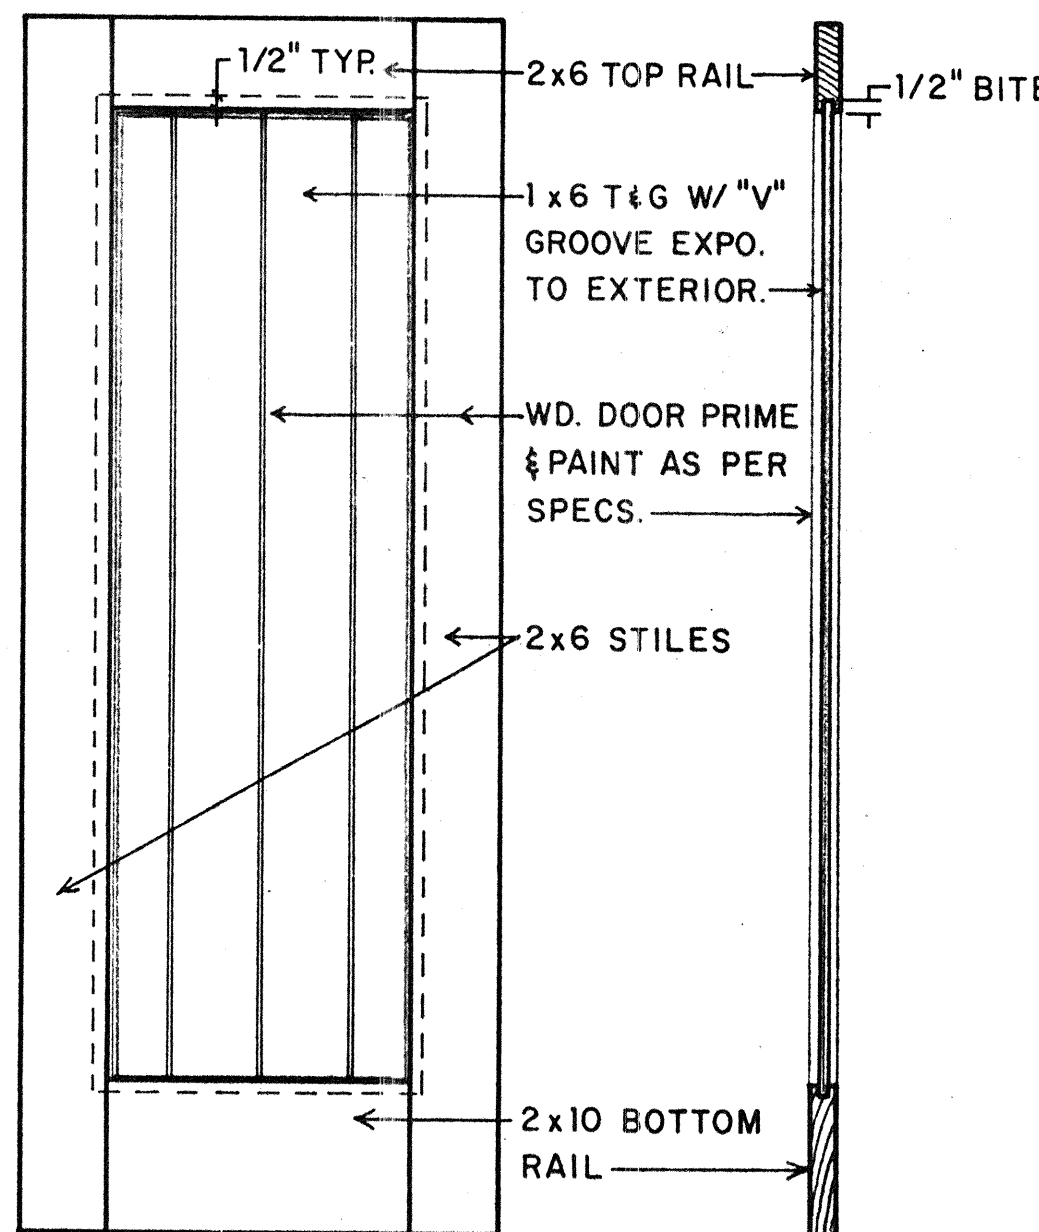


6 TYPICAL BATTEN DOOR DETAIL
1" = 1'-0"

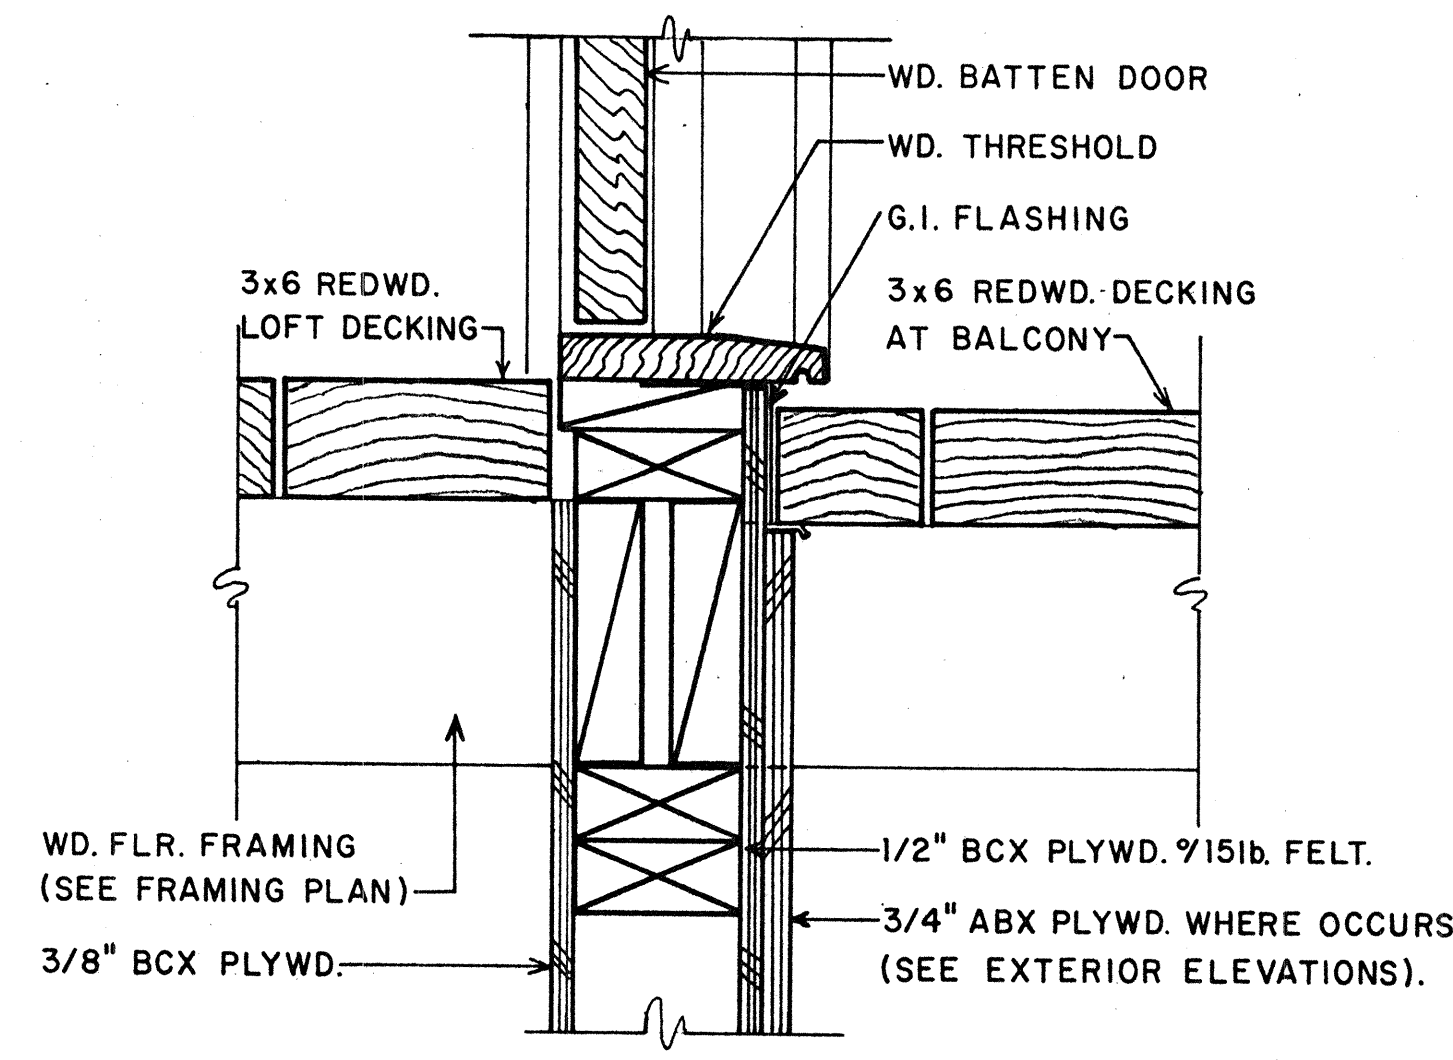

1 LOFT DOOR THRESHOLD DETAIL
3" = 1'-0"

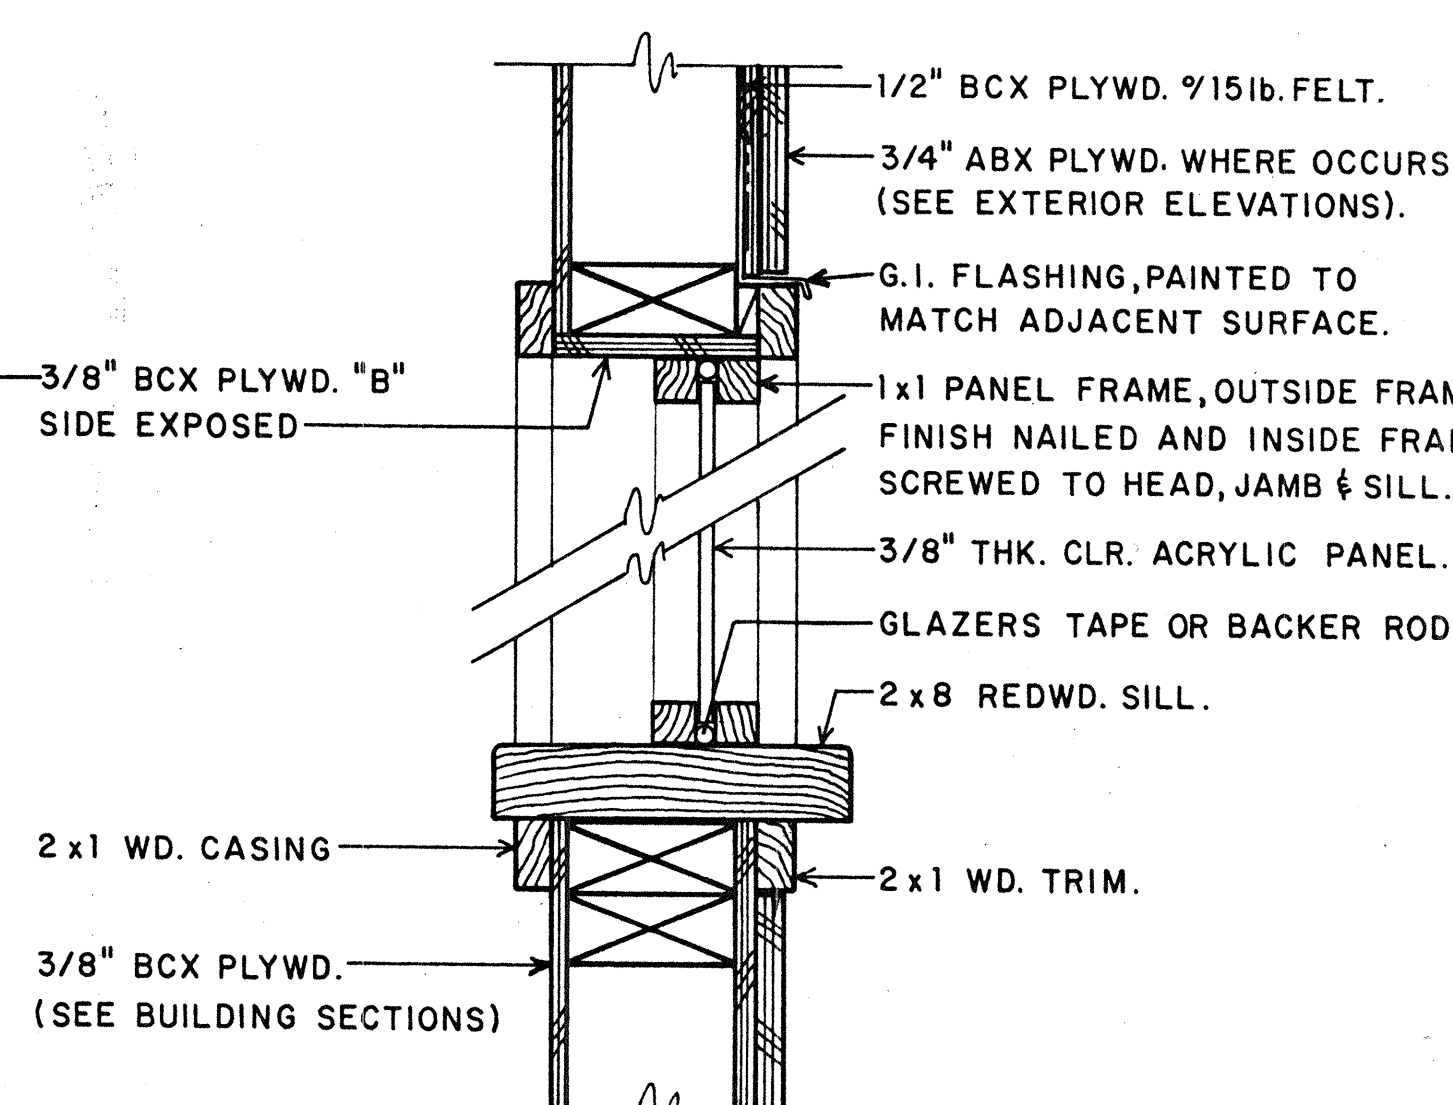

2 TYPICAL WINDOW DETAIL
3" = 1'-0"

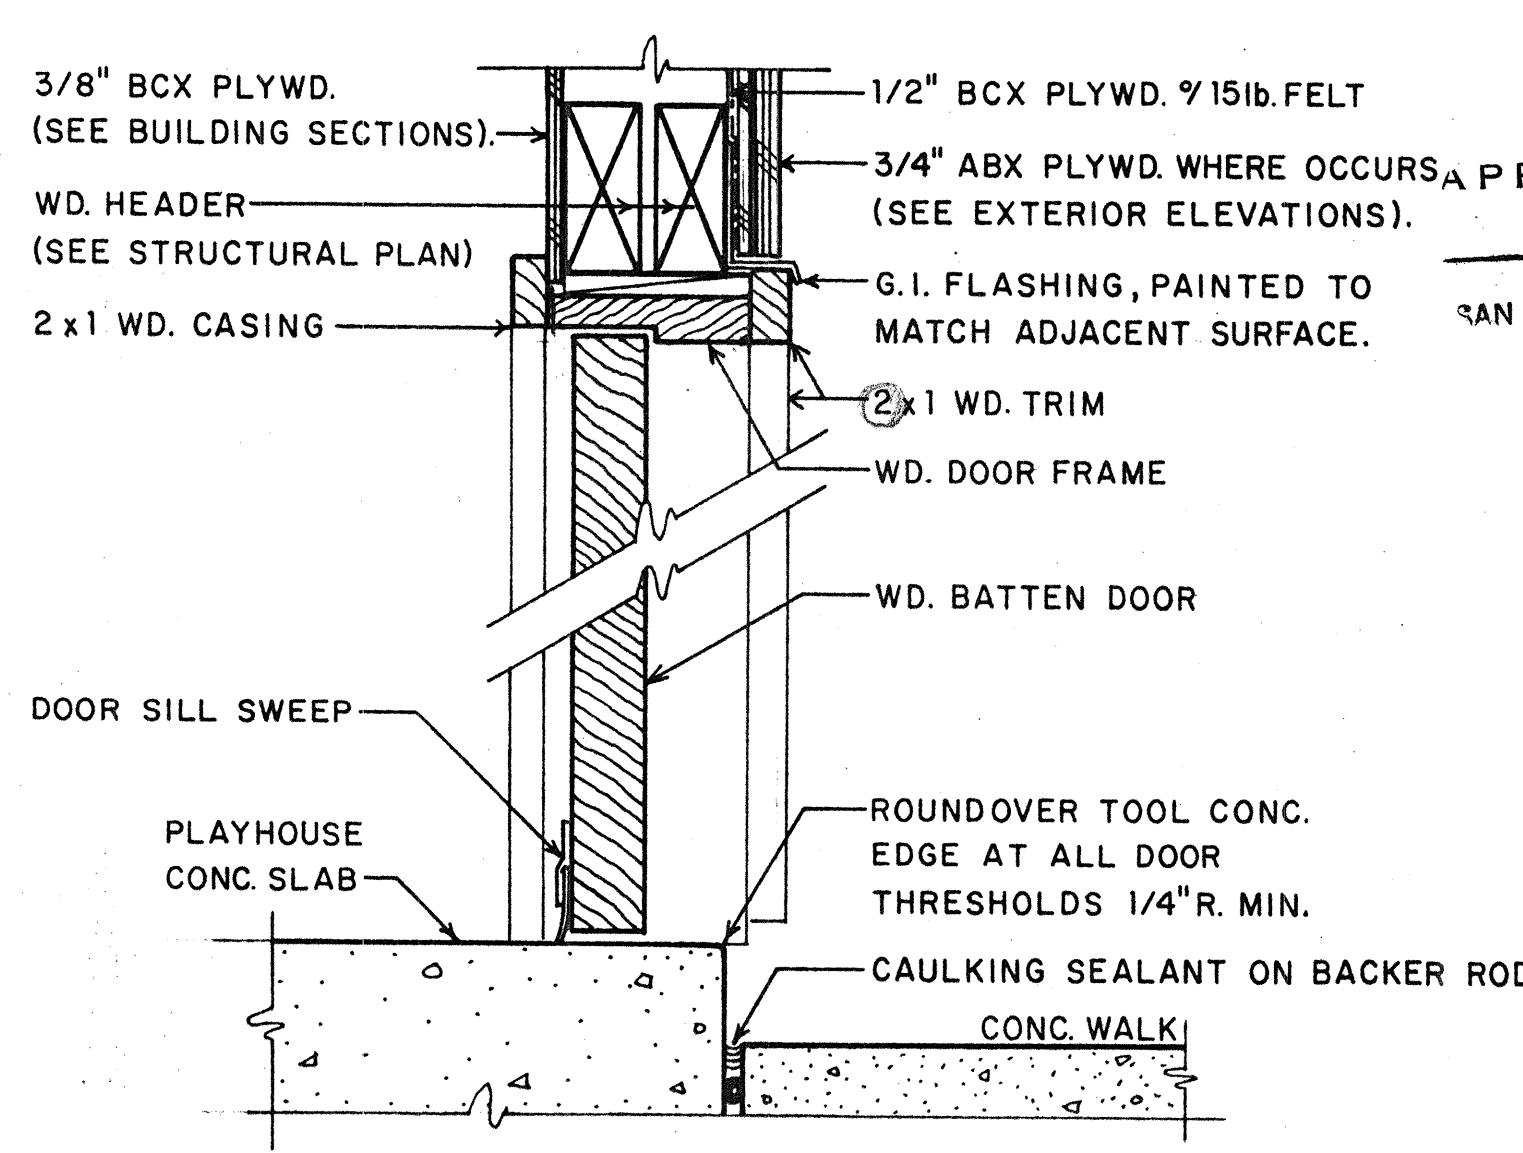

3 TYPICAL DOOR DETAIL
3" = 1'-0"

**Dube'
Donnelly
Designs**

Phillip Dube'
Tel: (818) 799-3379
722 Garfield Ave.
So. Pasadena, Ca. 91030

Brian Donnelly
Tel: (310) 371-7701
3644 Del Amo Blvd. - C
Torrance, Ca. 90503

**CREATIVE
Planning & Design**

Saint Edmund's Nursery School
Playground Remodel
1175 San Gabriel Boulevard
San Marino, California 91108-8038
Ph: (818) 792-7742

APPROVED PLAN
date
SAN MARINO BUILDING DEPT.

The drawings and specifications are instruments of service and remain the property of Dube' Donnelly Designs whether the project is executed or not. The drawings and specifications shall not be used by the owner on other projects, additions to this project, or for the completion of this project by others, provided that Dube' Donnelly Designs is not in default under this agreement, except by agreement in writing and appropriate compensation to Dube' Donnelly Designs shall be deemed the author of the drawings and specifications and shall retain all common law, including copyright. All rights reserved.

MAY 08 1997
Date

Scale NOTED

Drawn PSD & BPD

Job SENS

PH 4.1