


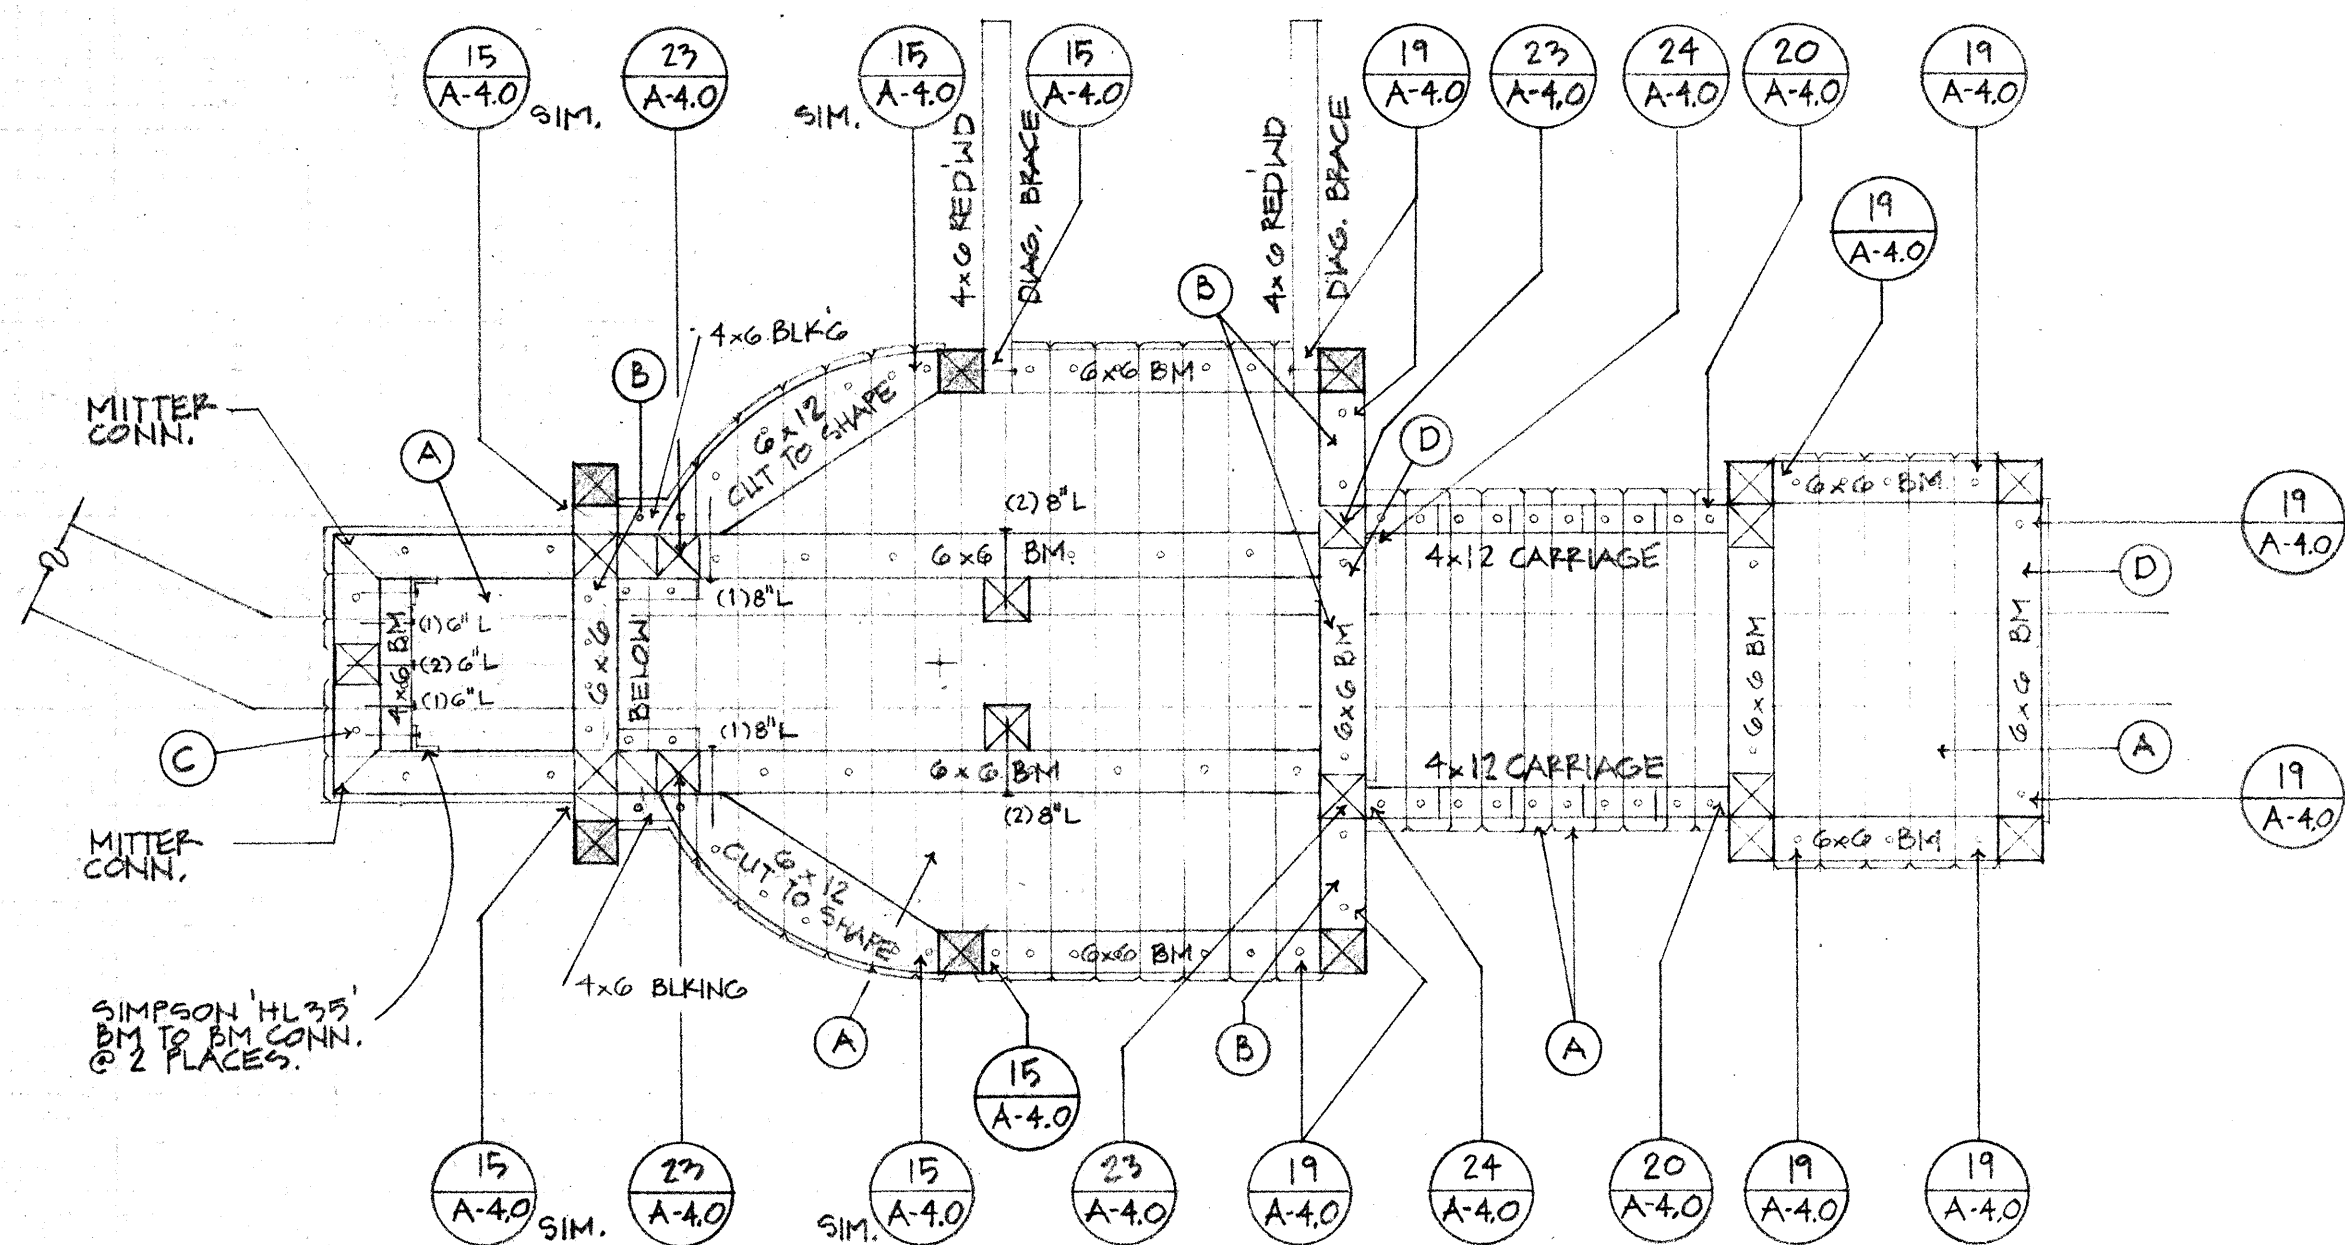


#### FRAMING LEGEND

- ☒ 6x6 REDWD POST - CONNECTED TO PIER FOUNDATION BELOW
- ☒ 6x6 REDWD POST - POST INTO NATURAL GRADE OR RAILING POST SUPPORT
- LAG BOLT(S) - SEE SPECS. & DETAILS
- ANGLES & GUSSETS - SEE SPECS & DETAILS
- (A) 3x6 REDWD DECKING - WITH COUNTERSUNK LAG BOLTS. FOR LOCATION OF LAGS SEE PLAN, FOR SIZE SEE SPECS.
- (B) 6x6 WD. BLKING - BETWEEN POSTS. BLOCKING THAT OCCURS ABOVE DECKING TO BE REDWD, U.N.O.
- (C) LAG BOLT LOCATIONS, COUNTERSUNK


NOTE: ALL 'HL' PLATES SHALL HAVE A MIN. OF (4) BOLTS W/ A BOLT EDGE DISTANCE OF (4) BOLT DIAMETERS. MIN. (I.E. ON A 5/8" BOLT THE EDGE DISTANCE WOULD BE 2 1/2" MIN.) U.N.O.

- (D) 3x8 REDWD DECK BOARD - WITH COUNTERSUNK LAG BOLTS. RIPPED TO SIZE IF REQUIRED. FOR LOCATION OF LAGS SEE PLAN, FOR SIZE SEE SPECS.

**Framing Plan**

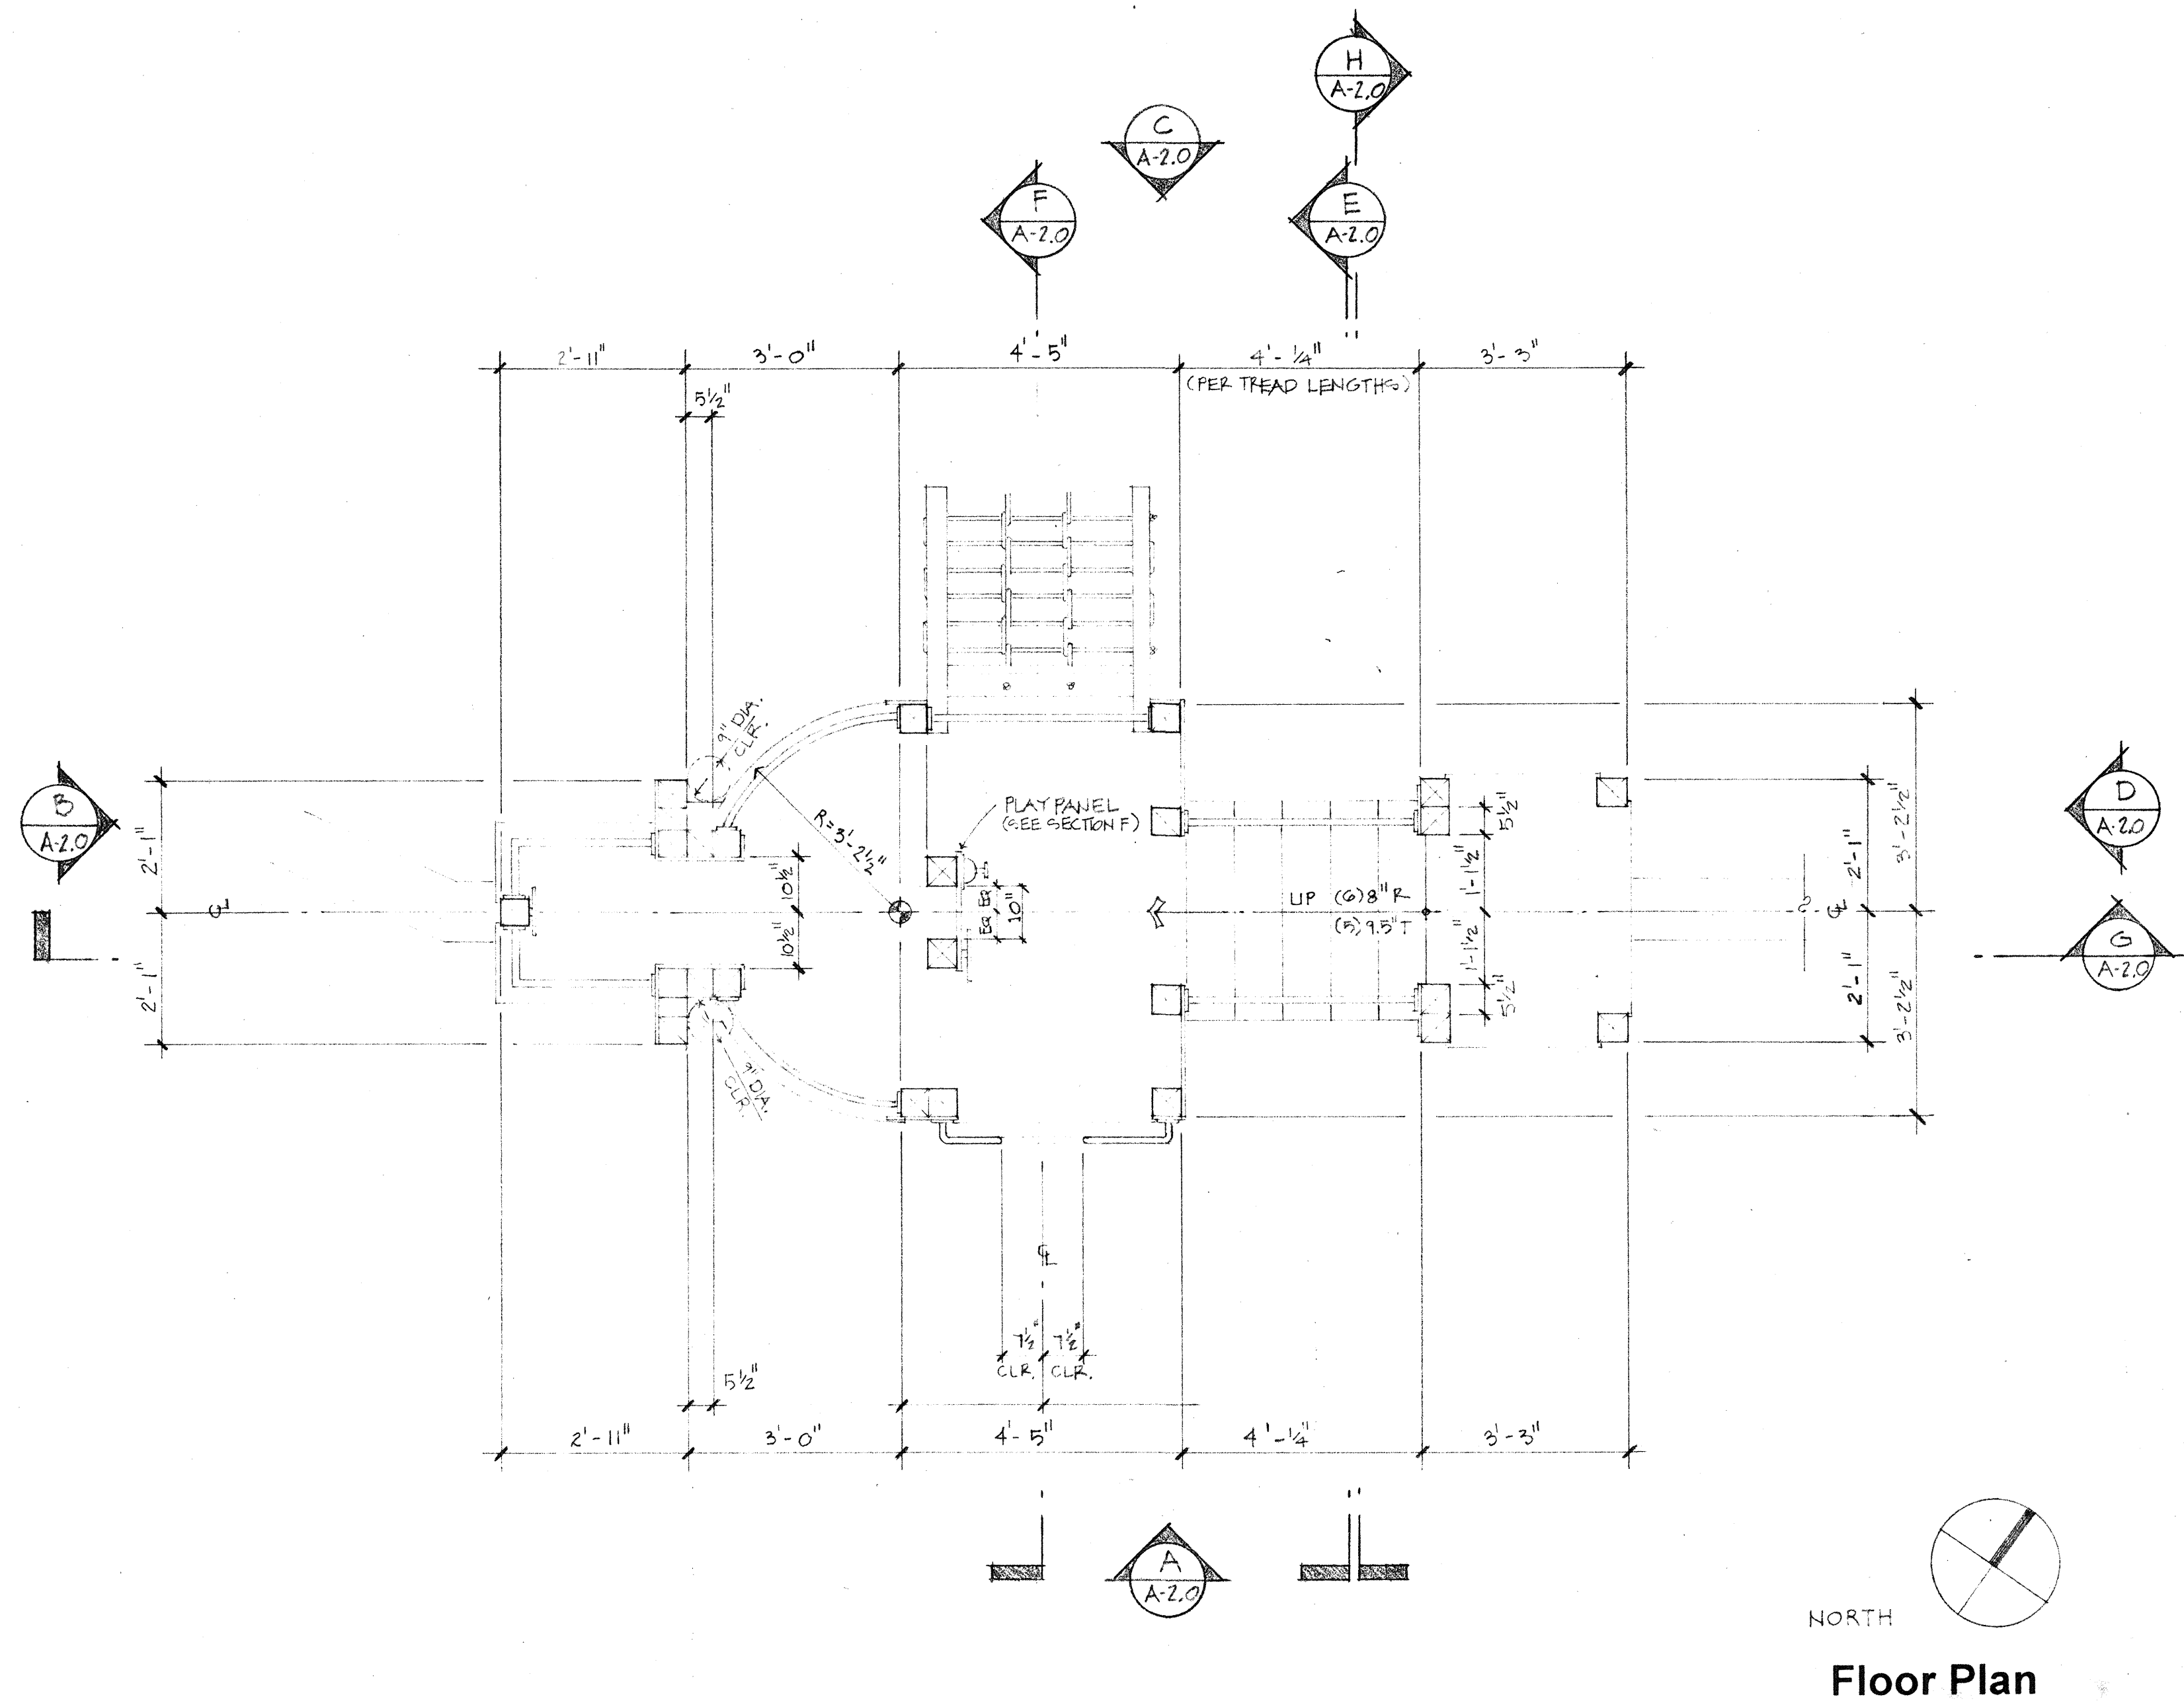


**Floor Plan**

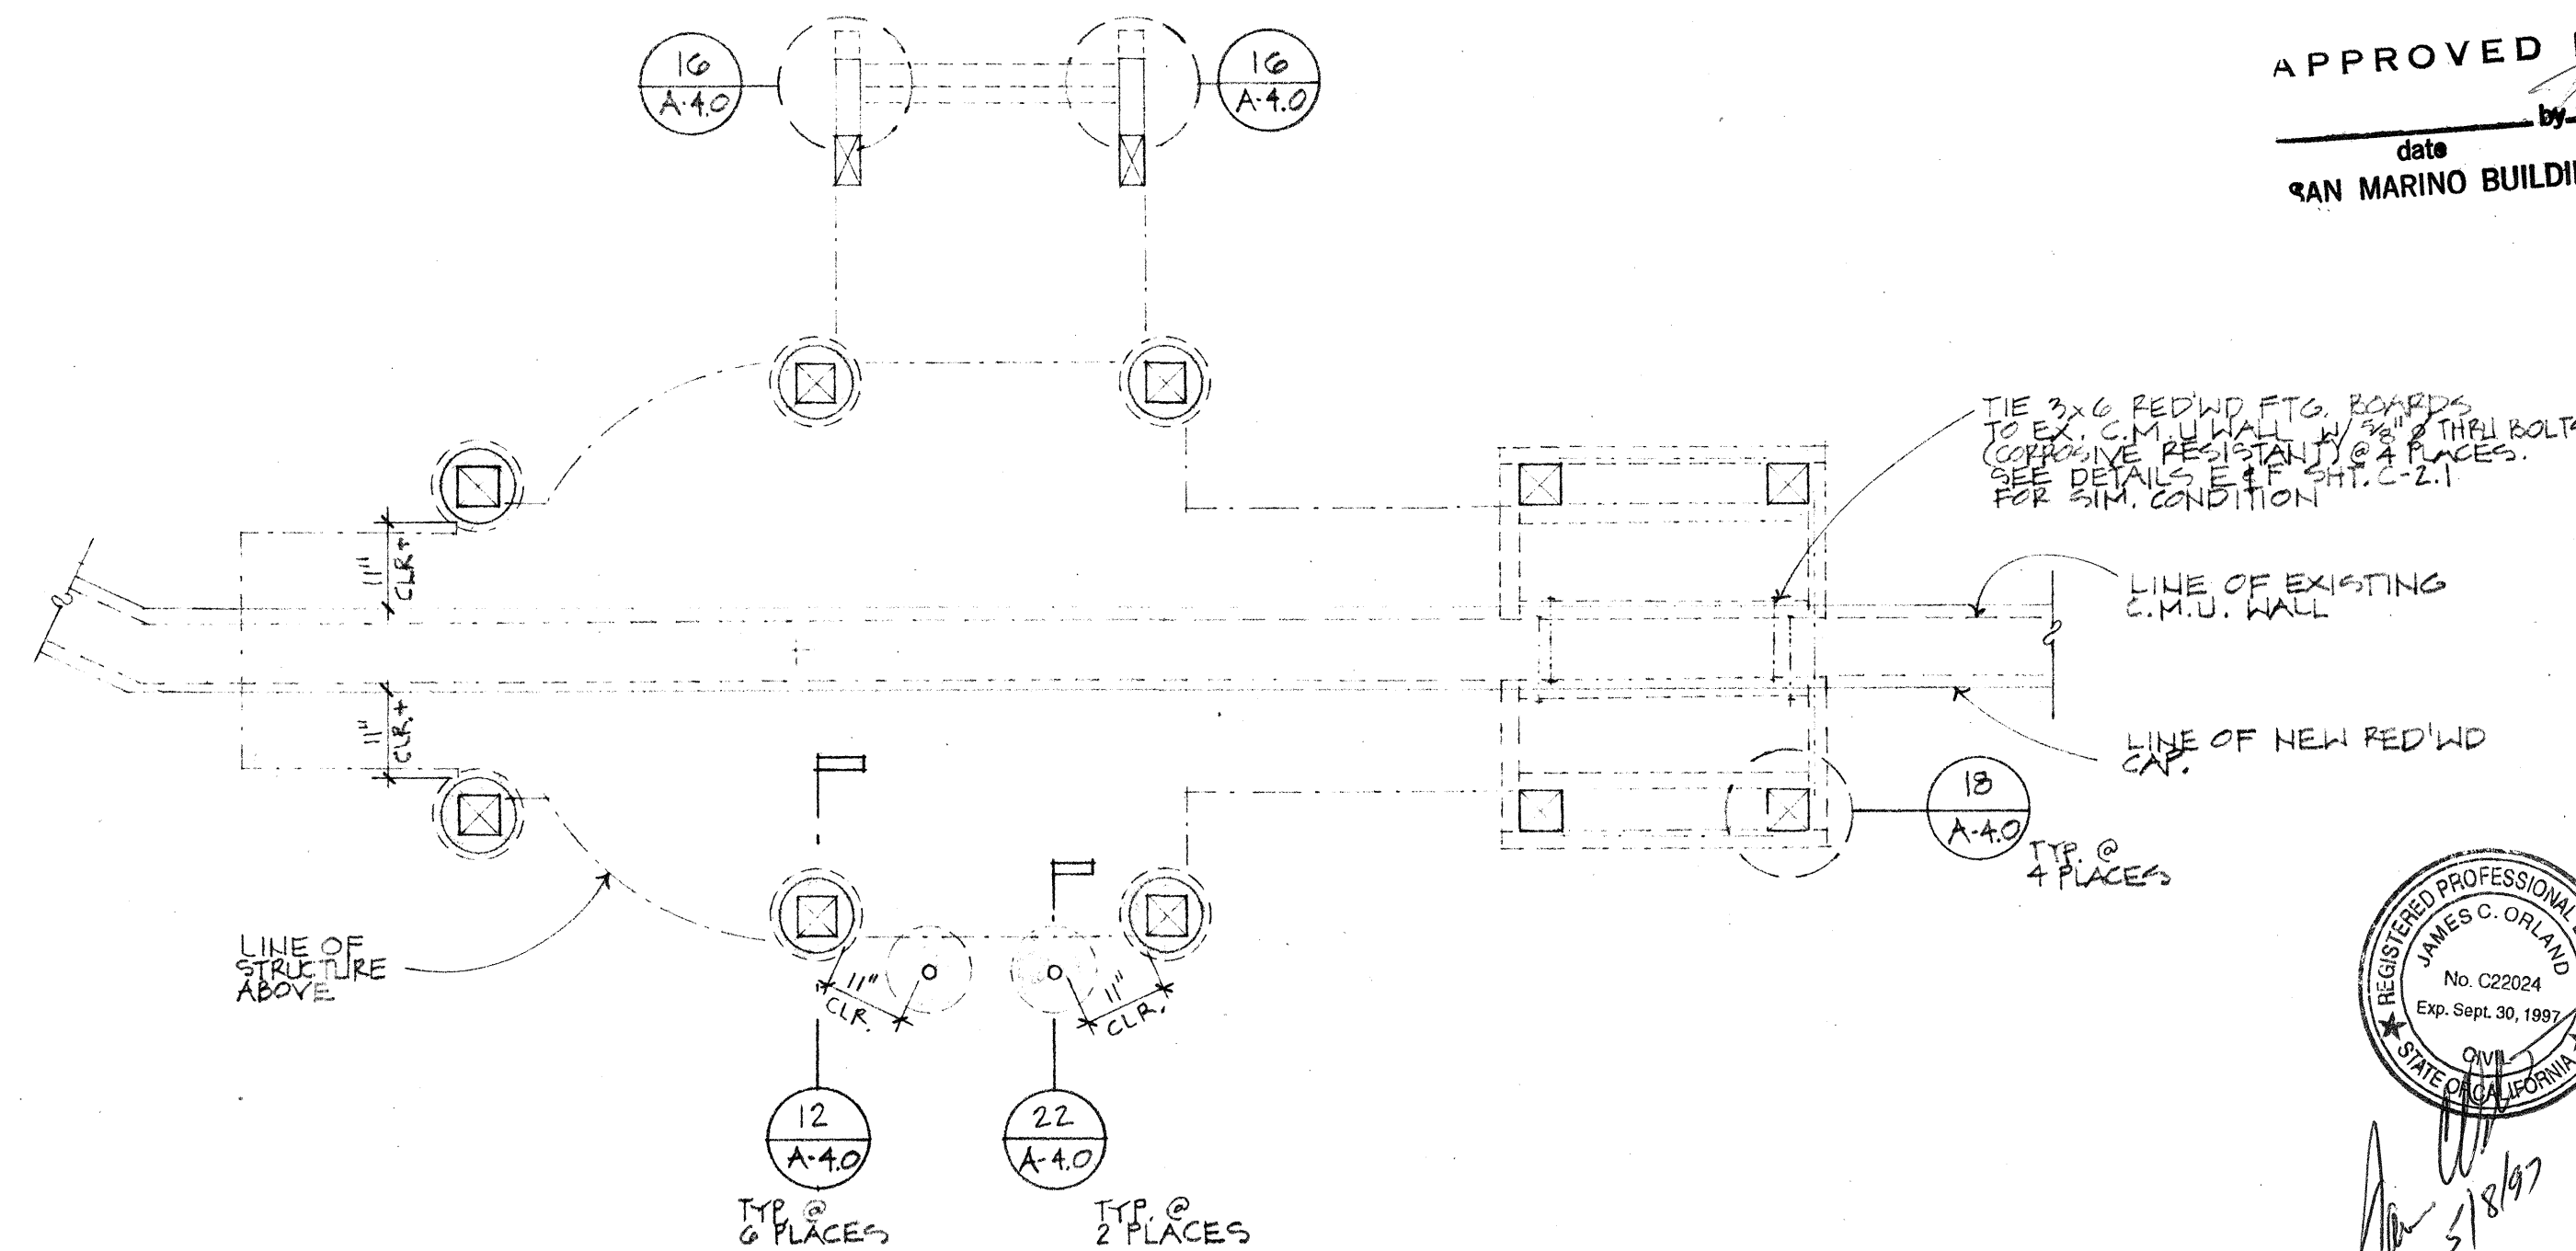

**Foundation Plan**

APPROVED PLAN  
date \_\_\_\_\_  
SAN MARINO BUILDING DEPT.

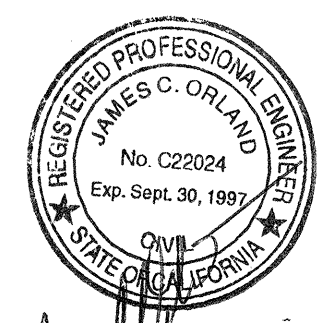

**Dube'  
Donnelly  
Designs**

Phillip Dube'  
Tel: (818) 799-3379  
722 Garfield Ave  
So Pasadena, Ca. 91030

Brian Donnelly  
Tel: (310) 371-7701  
3644 Del Amo Blvd - C  
Torrance, Ca. 90503

**CREATIVE  
Planning & Design**

Saint Edmund's Nursery School  
**Playground Remodel**  
1175 San Gabriel Boulevard  
San Marino, California 91108-8038  
Ph: (818) 792-7742

The drawings and specifications are instruments of service and remain the property of Dube' Donnelly Designs whether the project is executed or not. The drawings and specifications shall not be used by the owner on other projects, additions to this project, or for the completion of this project by others, provided that Dube' Donnelly Designs is not in default under this agreement, except by agreement in writing and appropriate compensation to Dube' Donnelly Designs shall be deemed the author of the drawings and specifications and shall retain all common law, including copyright. All rights reserved.

**MAY 08 1997**  
Date  
1/2" = 1'-0"  
Scale  
b.d.  
Drawn  
ST. EDMUNDS  
Job

**A-1.0**