




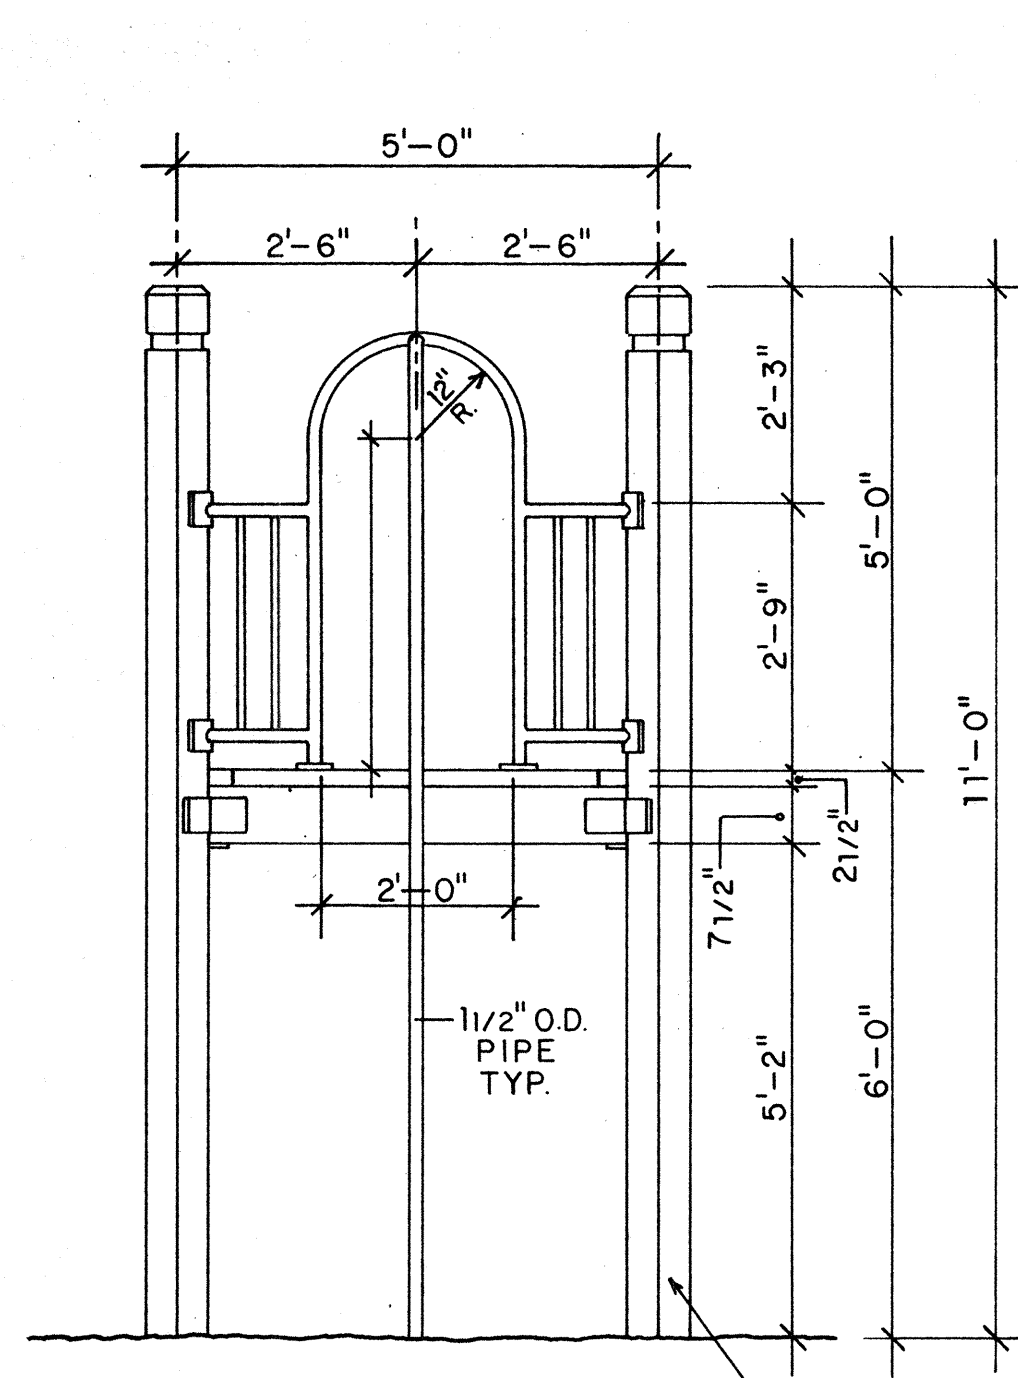


ELEVATION 1

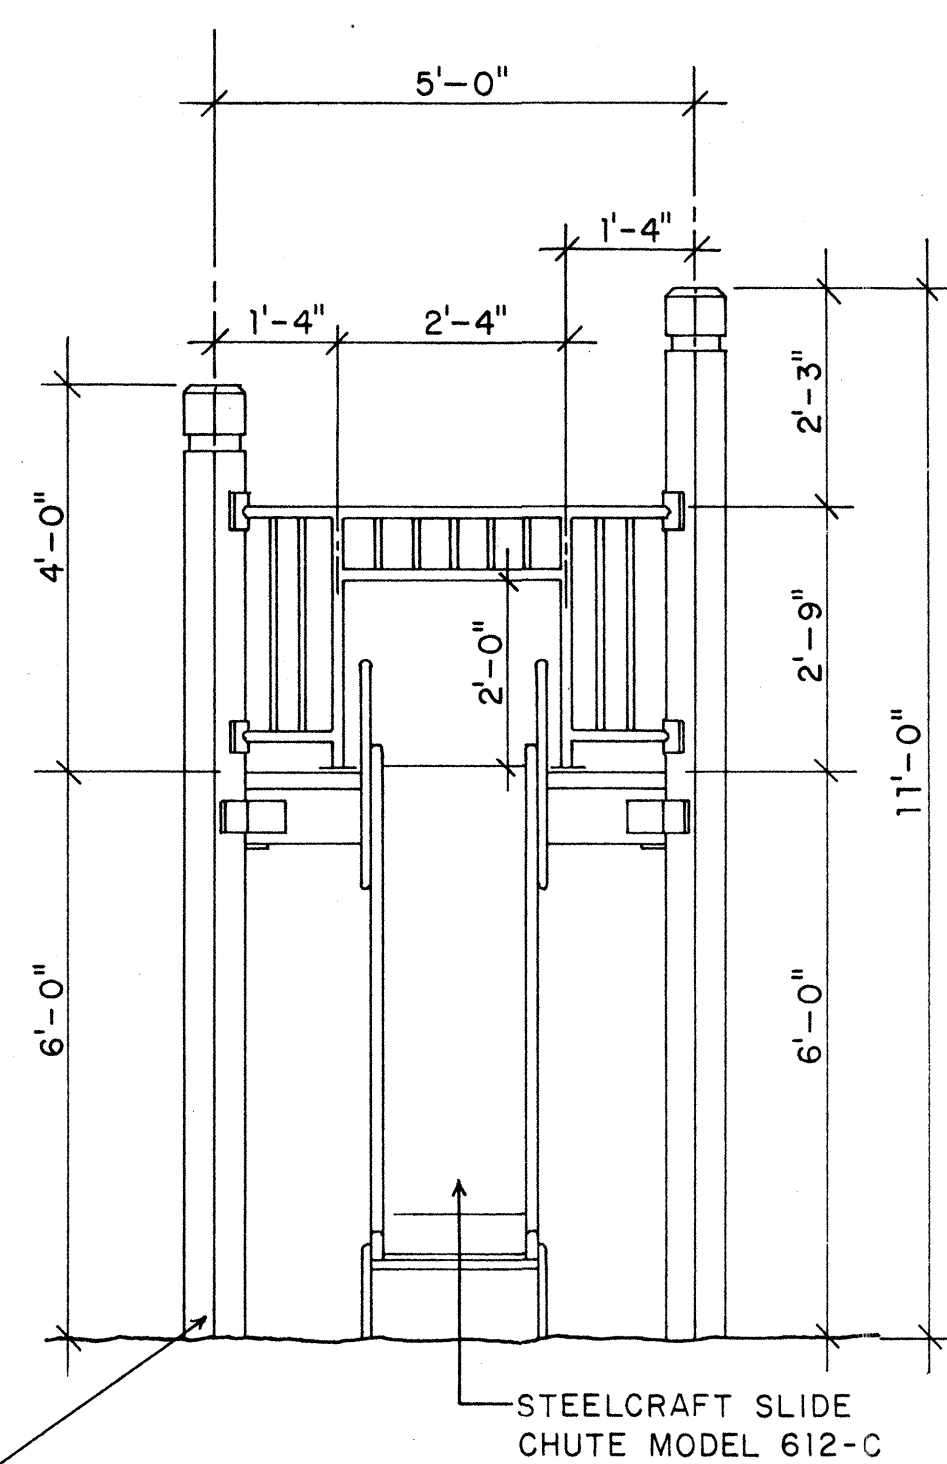


ELEVATION 2

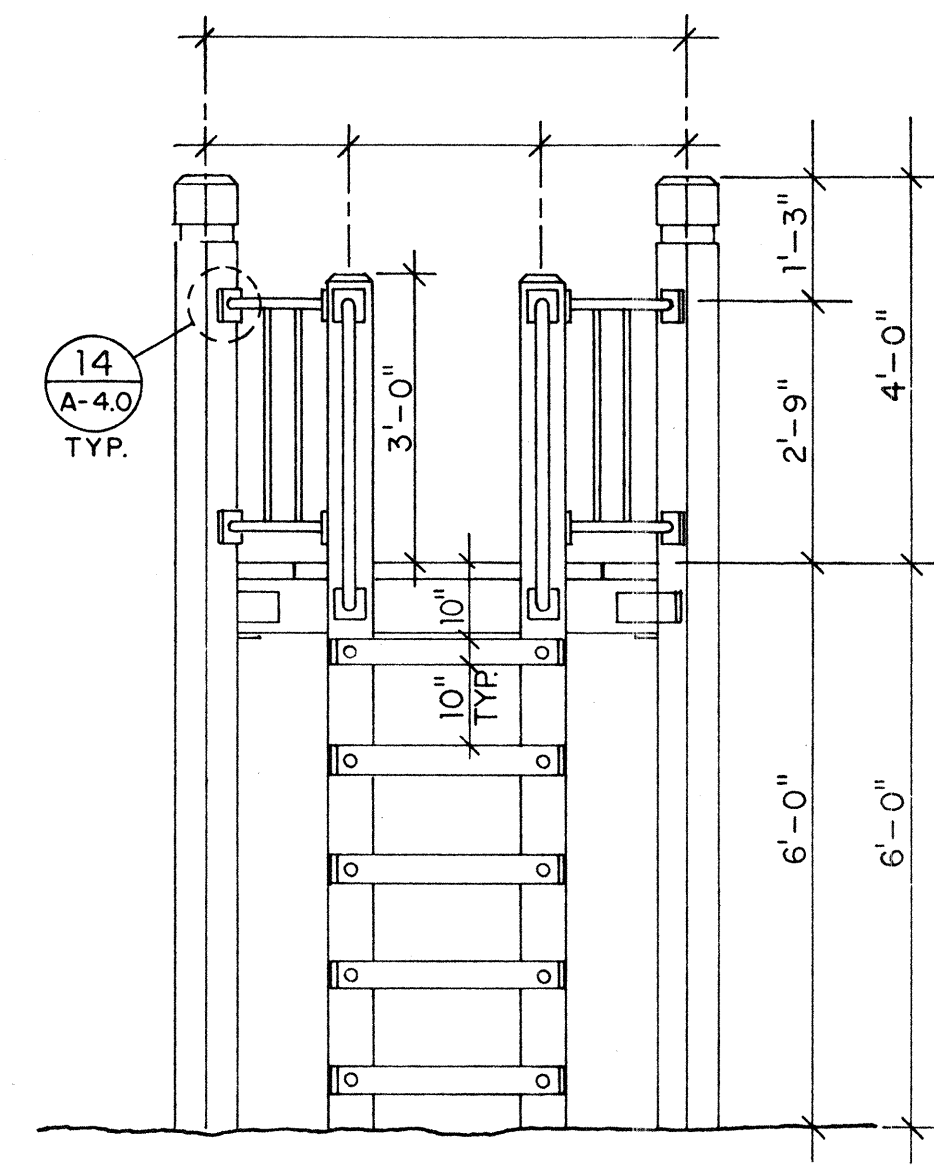


ELEVATION 3

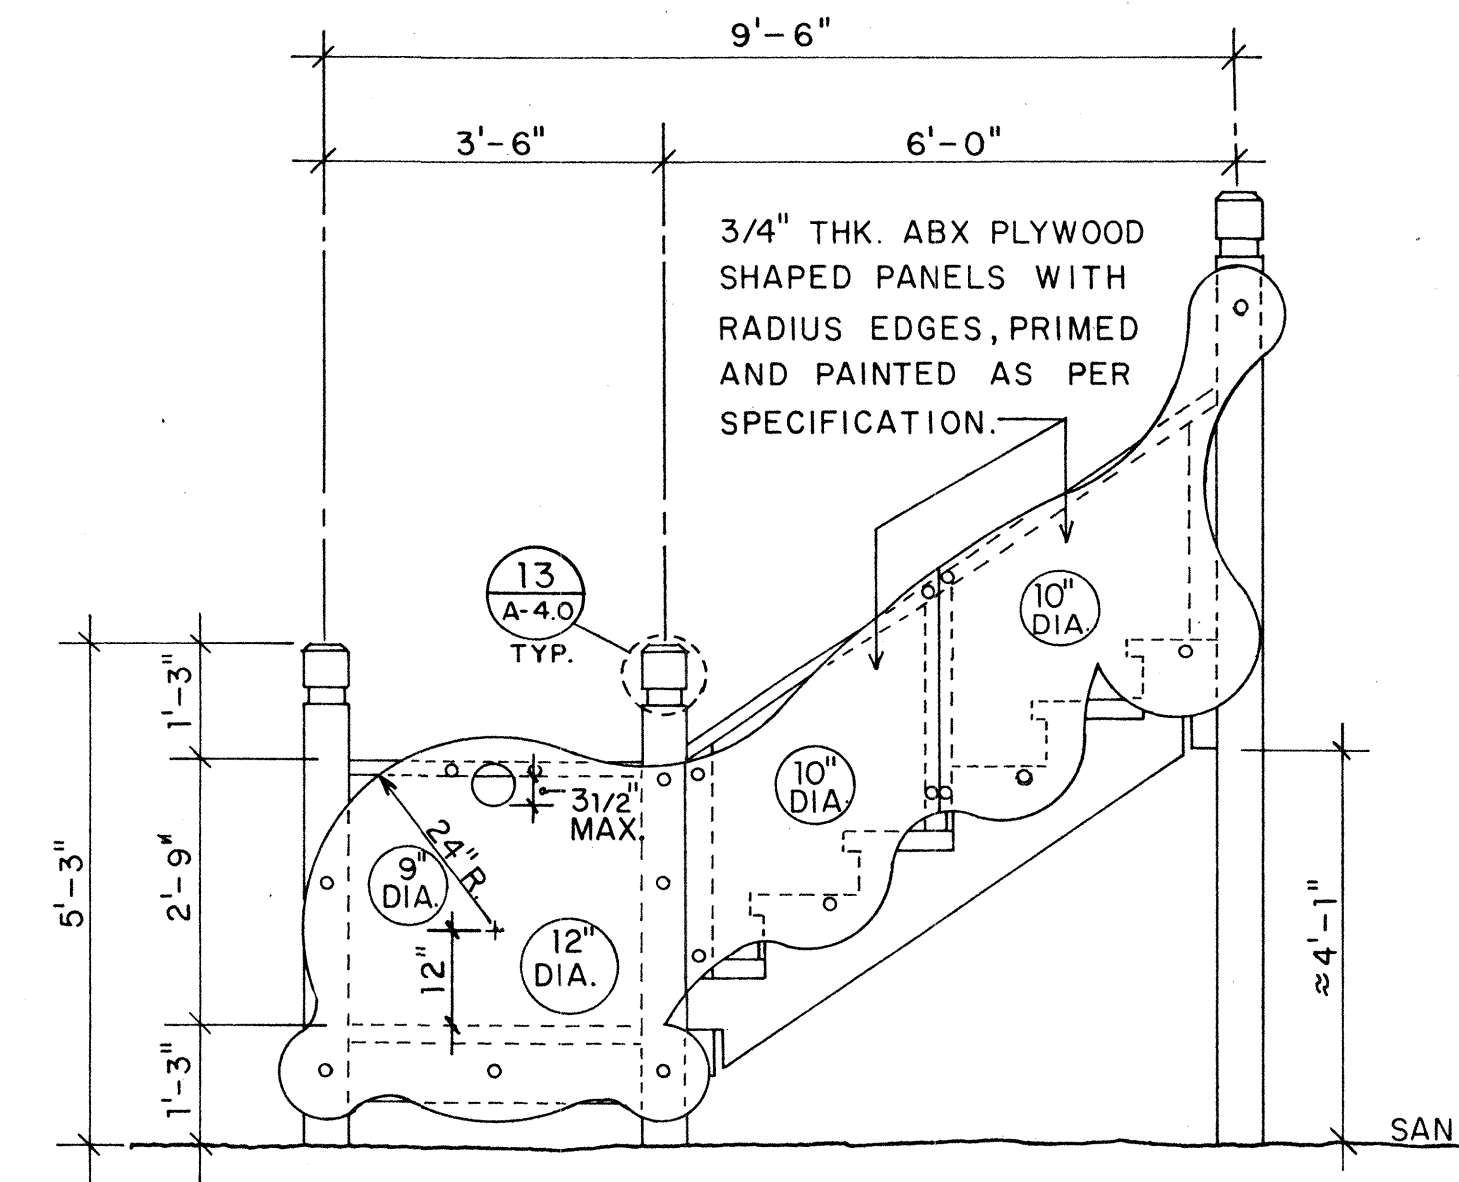


ELEVATION 4

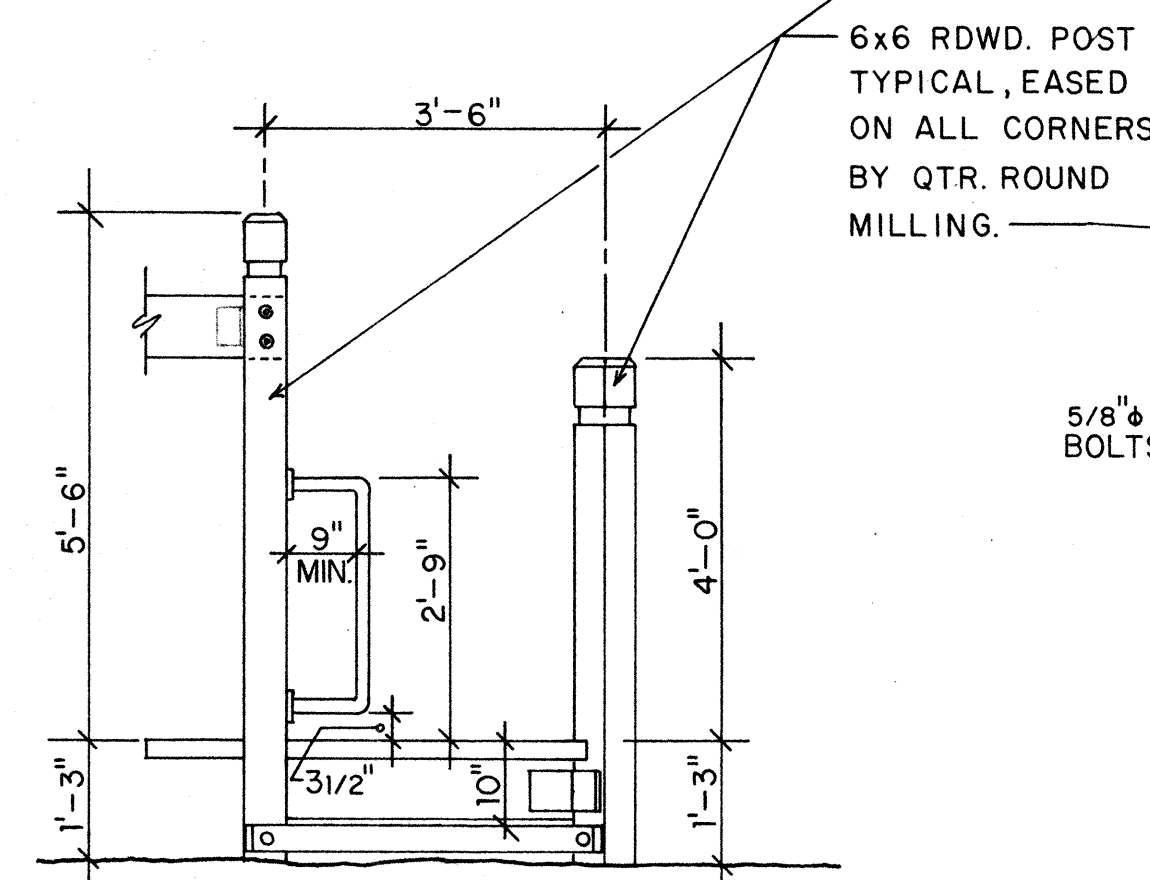


ELEVATION 5

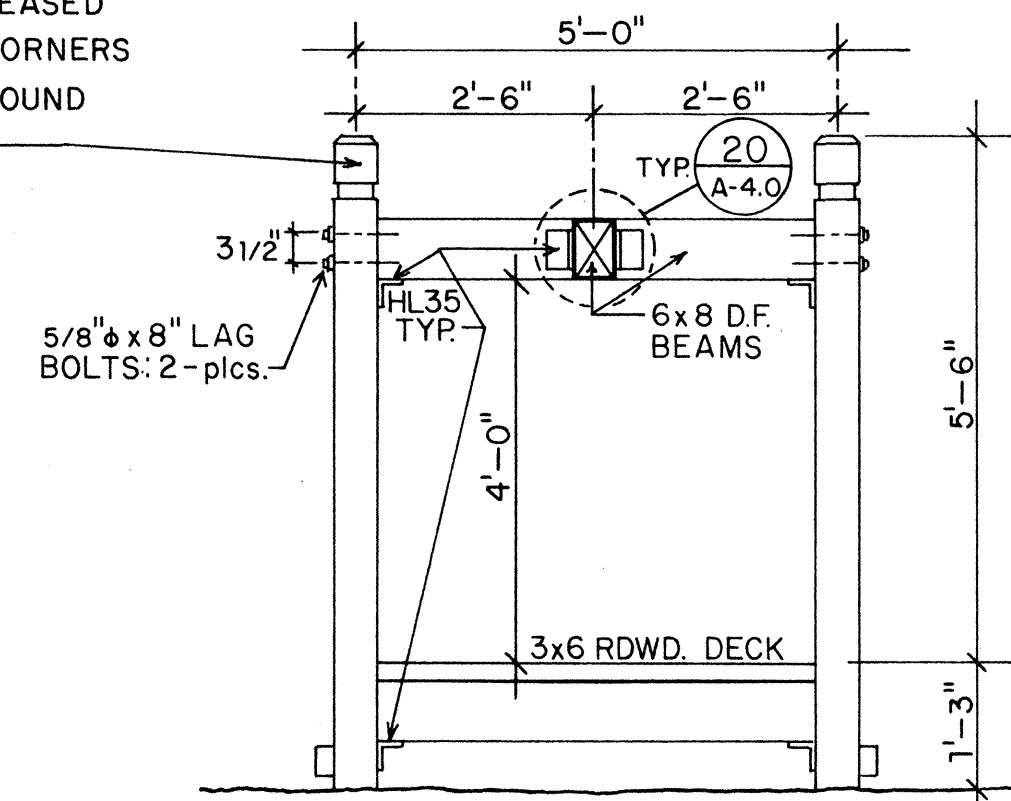


ELEVATION 6

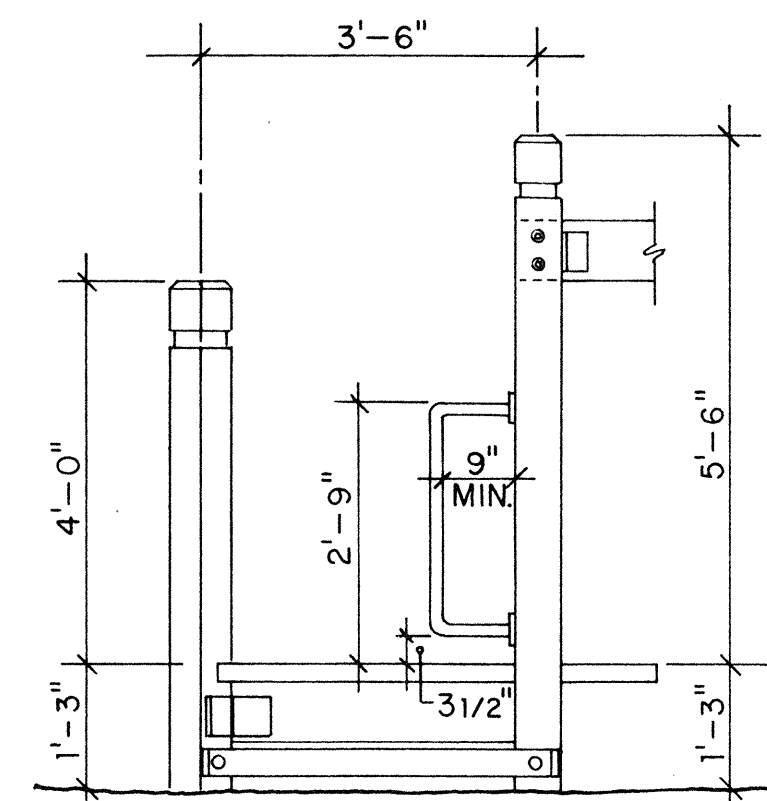


ELEVATION 7

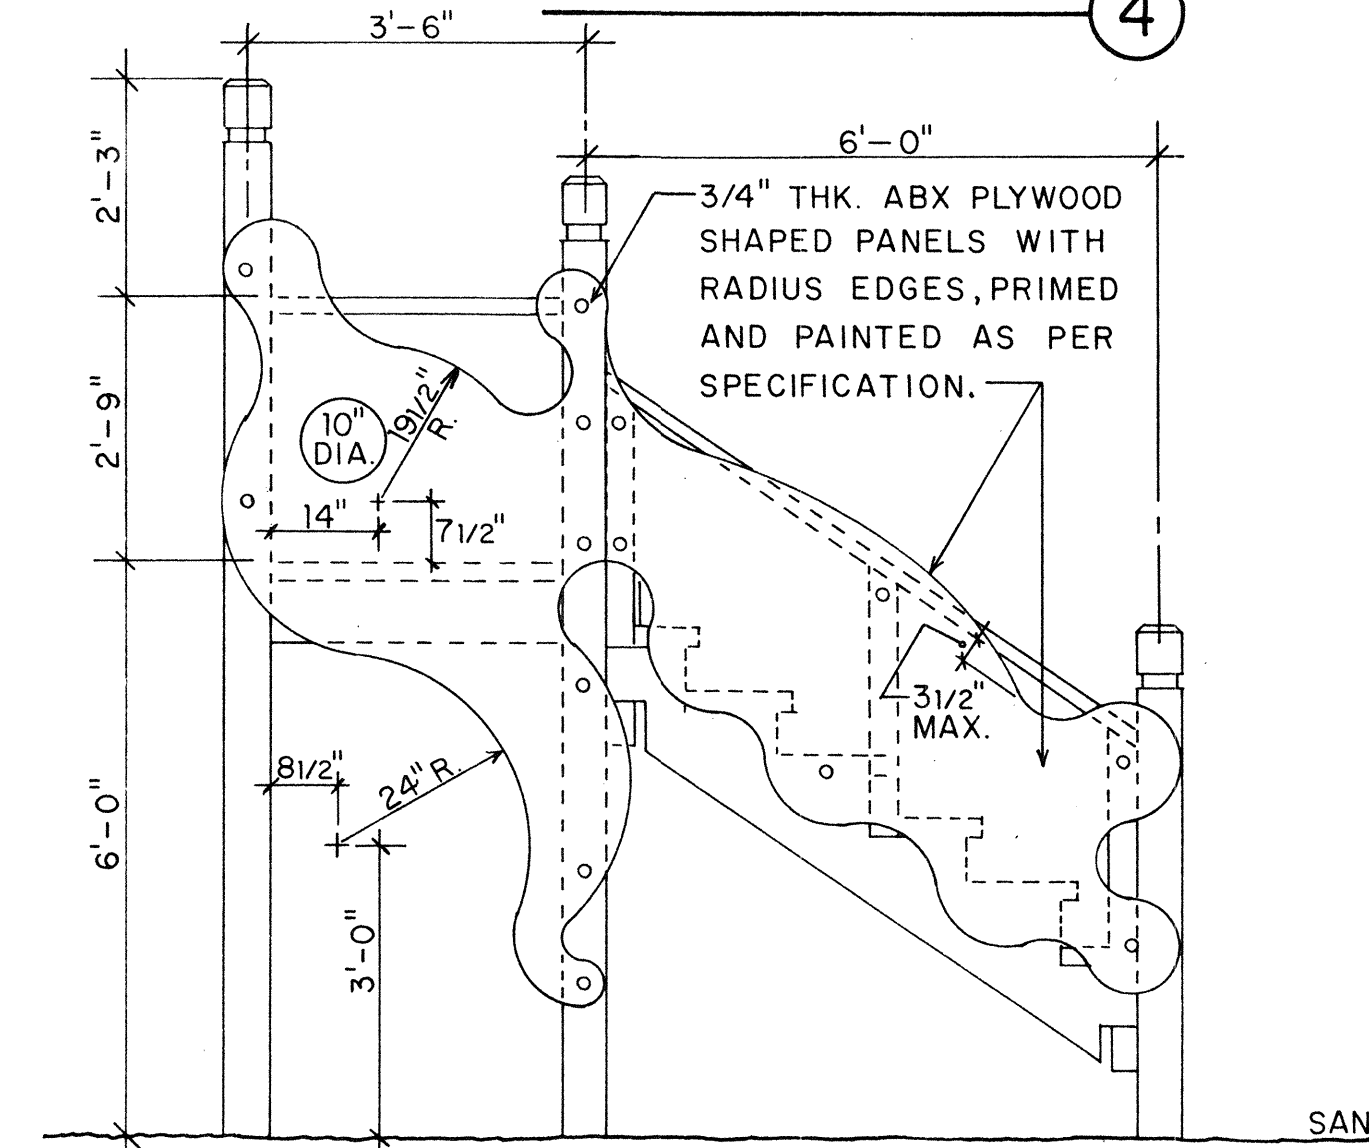


ELEVATION 8

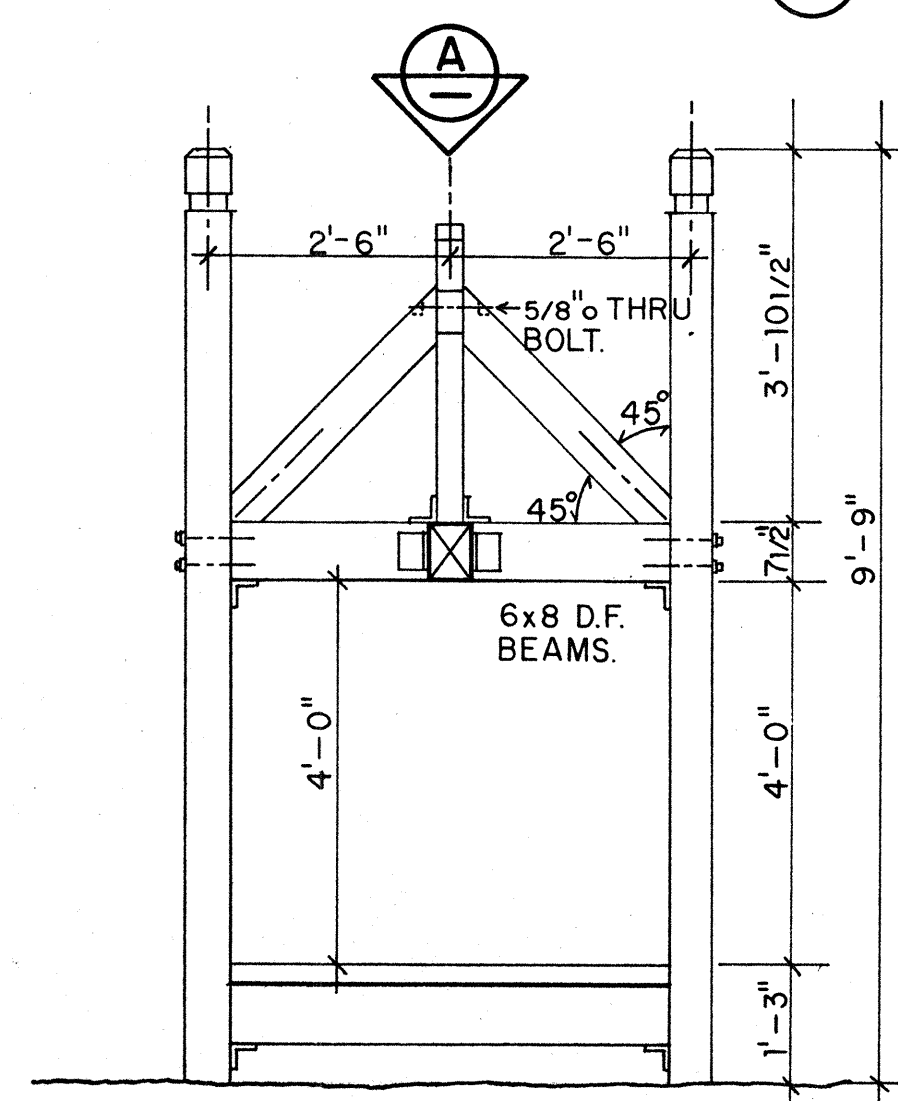


ELEVATION 9

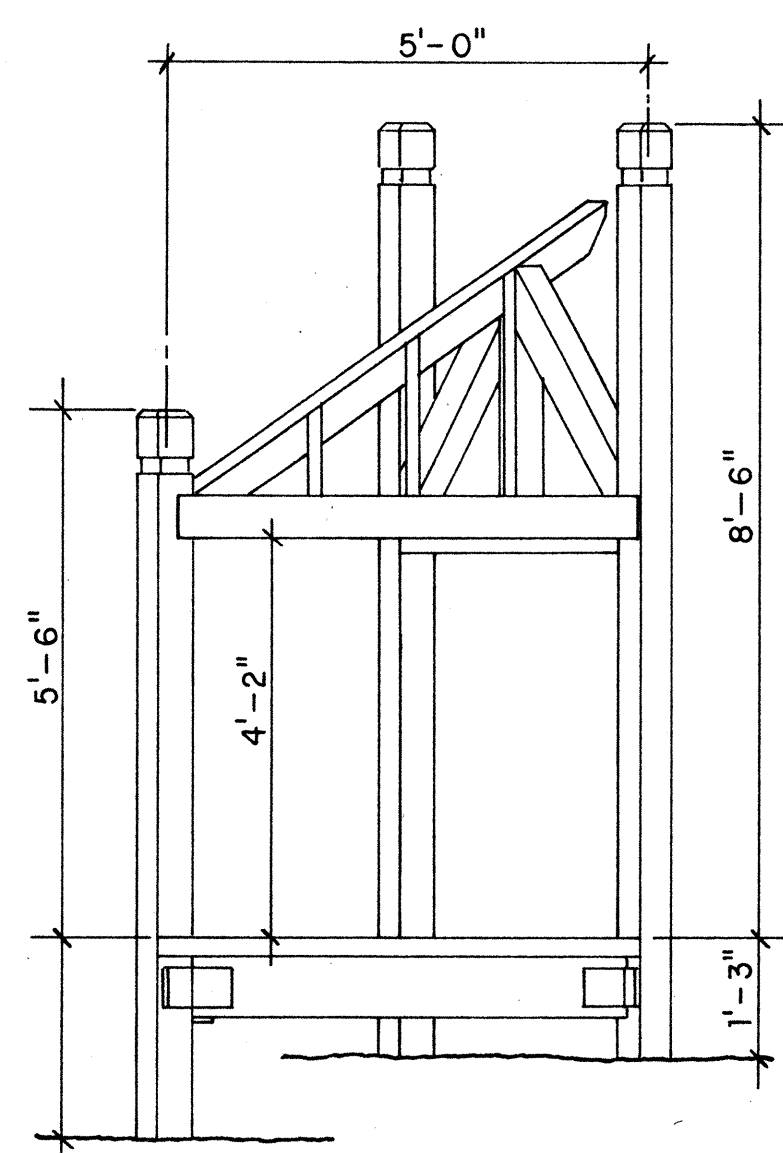

ELEVATION 10

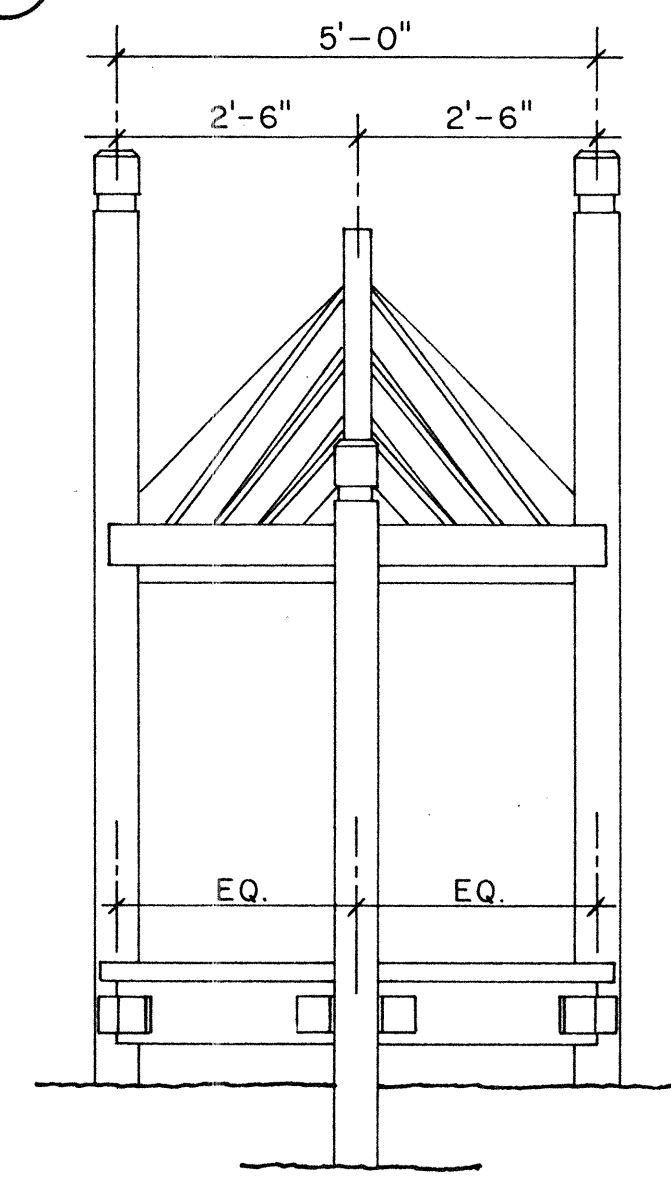


ELEVATION 11

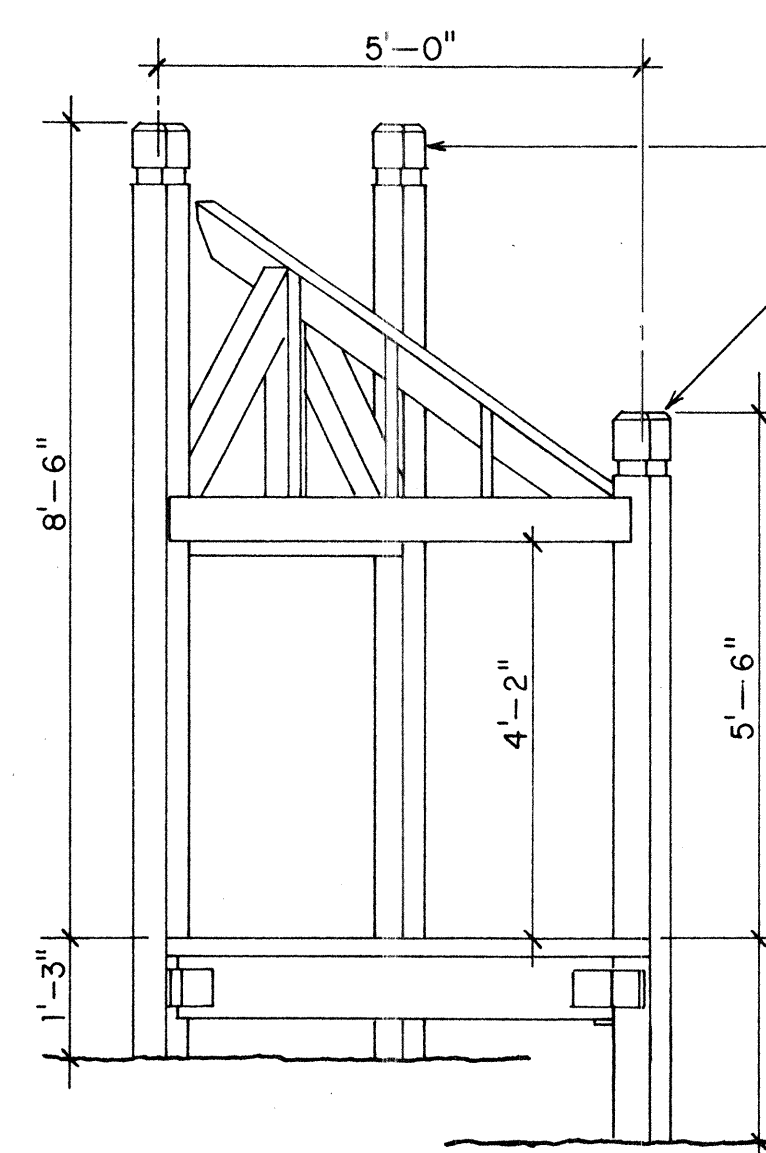


ELEVATION 12

6x6 RDWD. POST TYPICAL, EASED ON ALL EDGES BY QTR. ROUND MILLING.

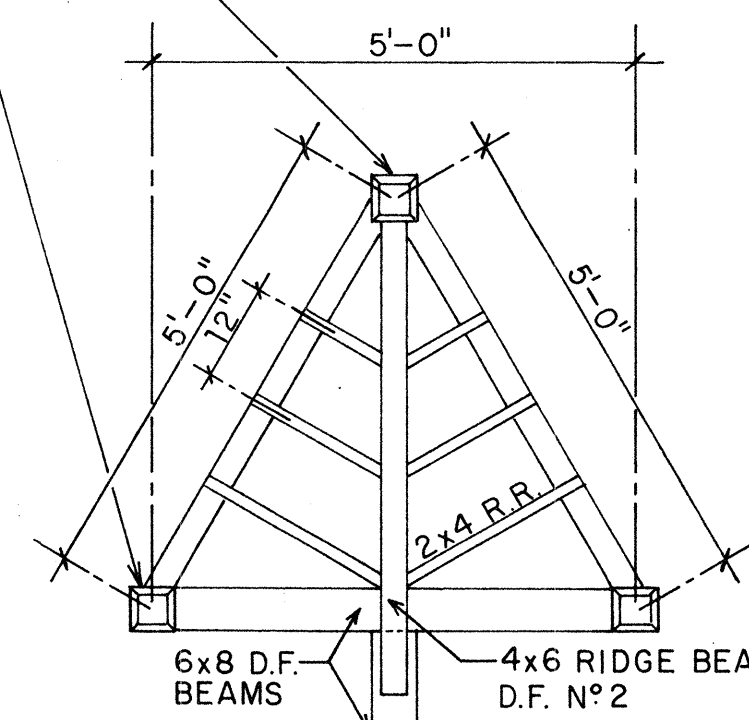

"ROOF" FRAMING

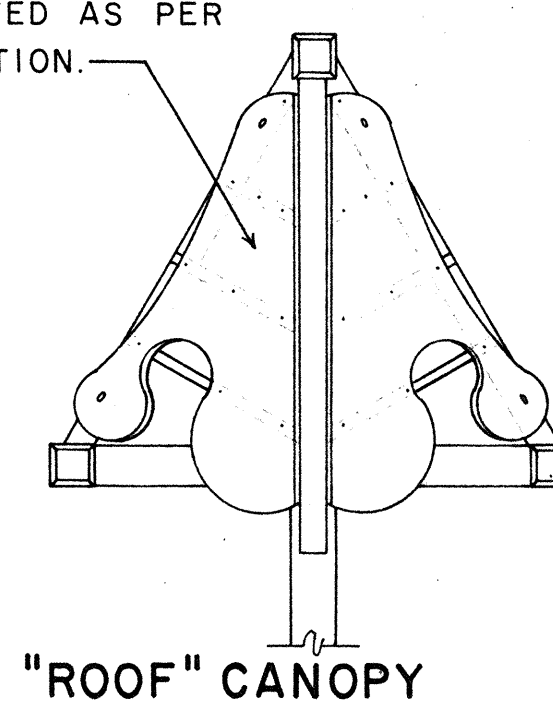

"ROOF" CANOPY

ROOF PANELS:  
3/4" THK. ABX PLYWOOD SHAPED PANELS WITH RADIUS EDGES, PRIMED AND PAINTED AS PER SPECIFICATION.

APPROVED PLAN  
date by  
SAN MARINO BUILDING DEPT.

NOTE:  
ROOF PANELS REMOVED FOR FRAMING CLARITY.

Dube'  
Donnelly  
Designs

Phillip Dube'  
Tel: (818) 799-3379  
722 Garfield Ave.  
So. Pasadena, Ca. 91030

Brian Donnelly  
Tel: (310) 371-7701  
3644 Del Amo Blvd. - C  
Torrance, Ca. 90503

CREATIVE  
Planning & Design

Saint Edmund's Nursery School  
Playground Remodel  
1175 San Gabriel Boulevard  
San Marino, California 91108-8038  
Ph: (818) 792-7742

The drawings and specifications are instruments of service and remain the property of Dube' Donnelly Designs whether the project is executed or not. The drawings and specifications shall not be used by the owner on other projects, additions to this project, or for the completion of this project by others, provided that Dube' Donnelly Designs is not in default under this agreement, except by agreement in writing and appropriate compensation to Dube' Donnelly Designs shall be deemed the author of the drawings and specifications and shall retain all common law, including copyright. All rights reserved.

MAY 08 1997  
Date

Scale 1/2" = 1'-0"

Drawn PSD

Job 5EN3

(2-2.0)