



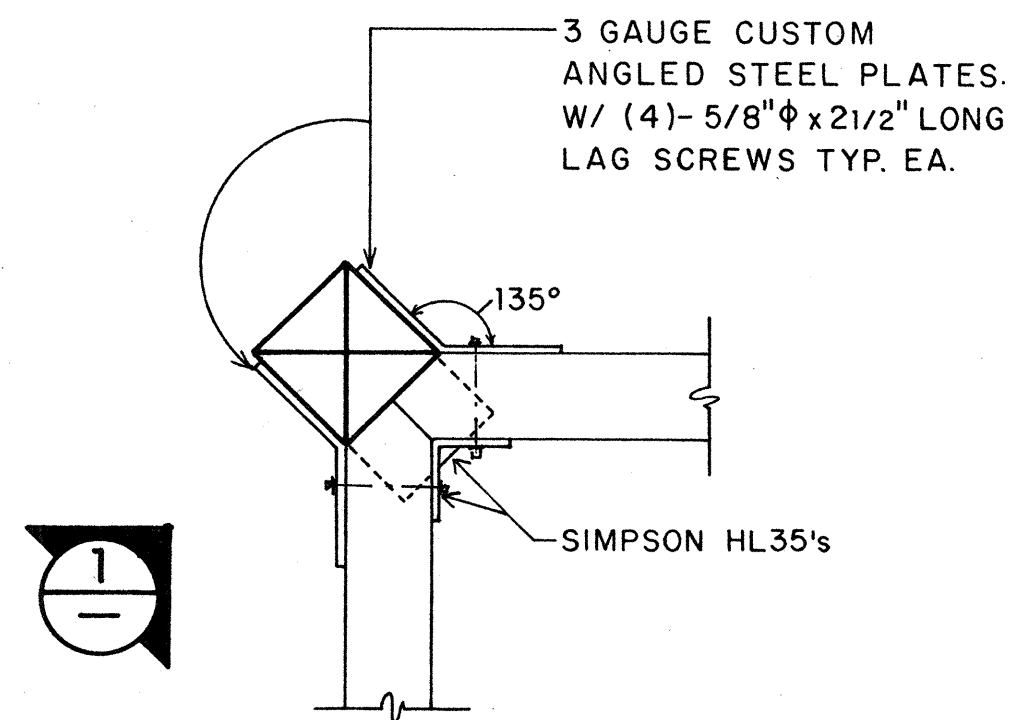


FRAMING DETAIL

1 1/2" = 1'-0" A

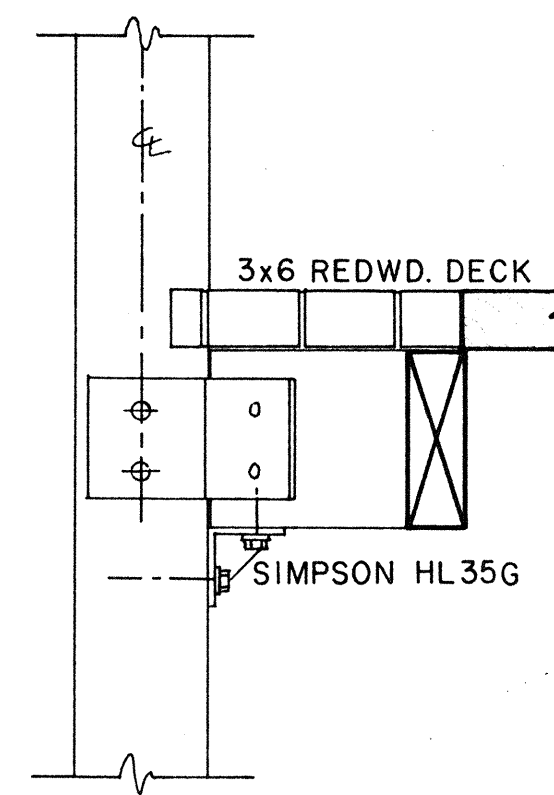


ELEVATION DETAIL

1 1/2" = 1'-0" 1

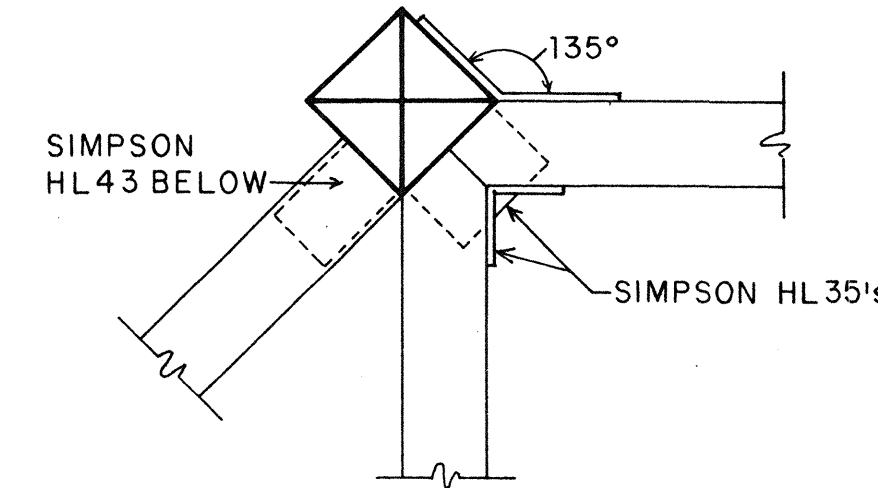


FRAMING DETAIL

1 1/2" = 1'-0" B

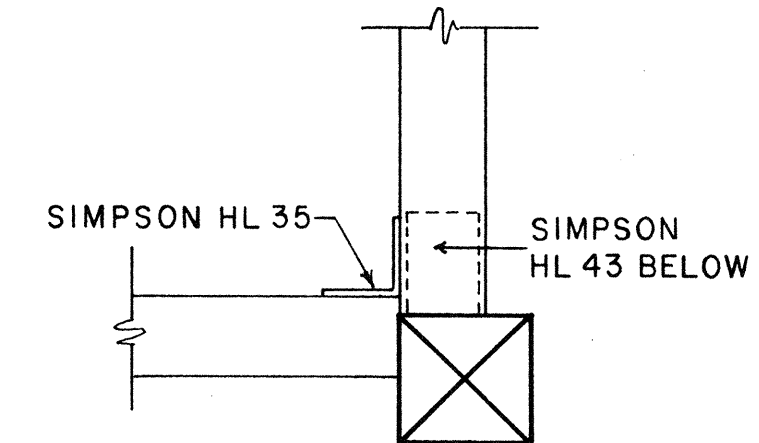


FRAMING DETAIL

1 1/2" = 1'-0" C

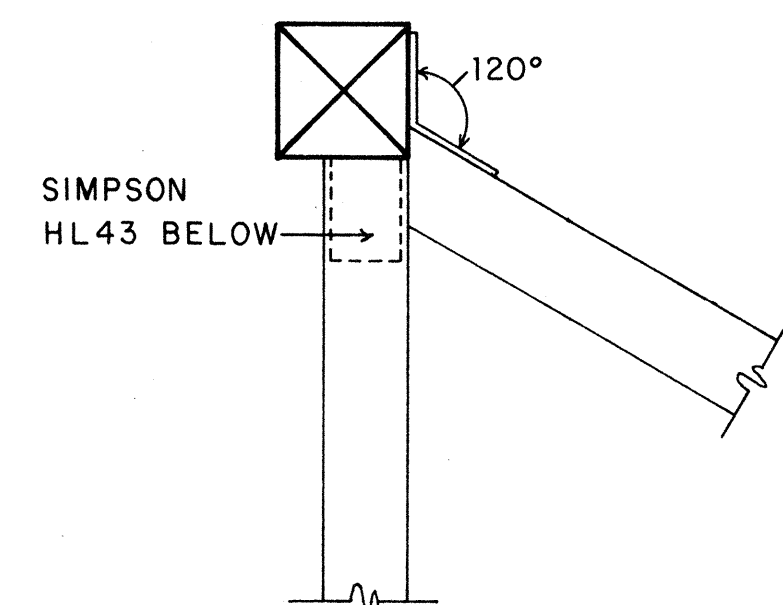


FRAMING DETAIL

1 1/2" = 1'-0" D

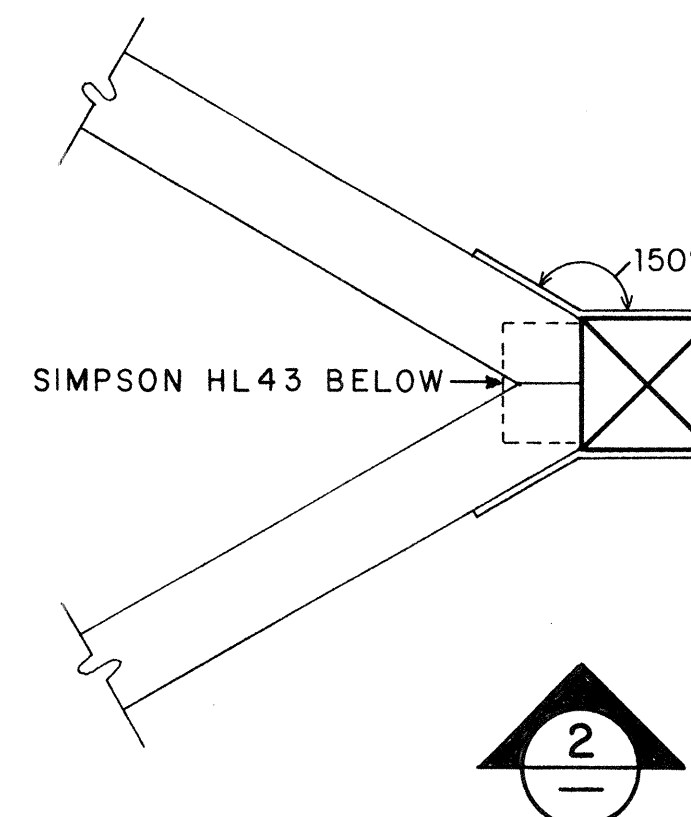


FRAMING DETAIL

1 1/2" = 1'-0" E

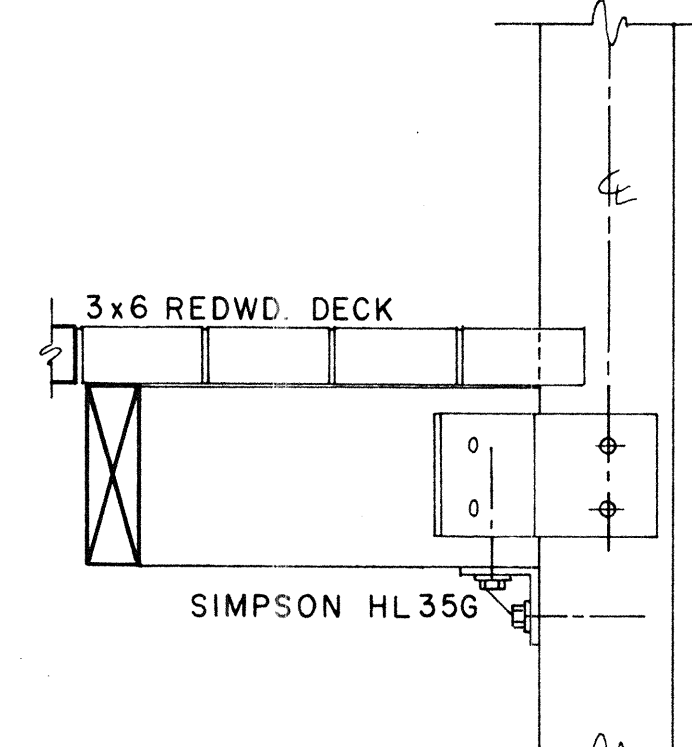


ELEVATION DETAIL

1 1/2" = 1'-0" 2

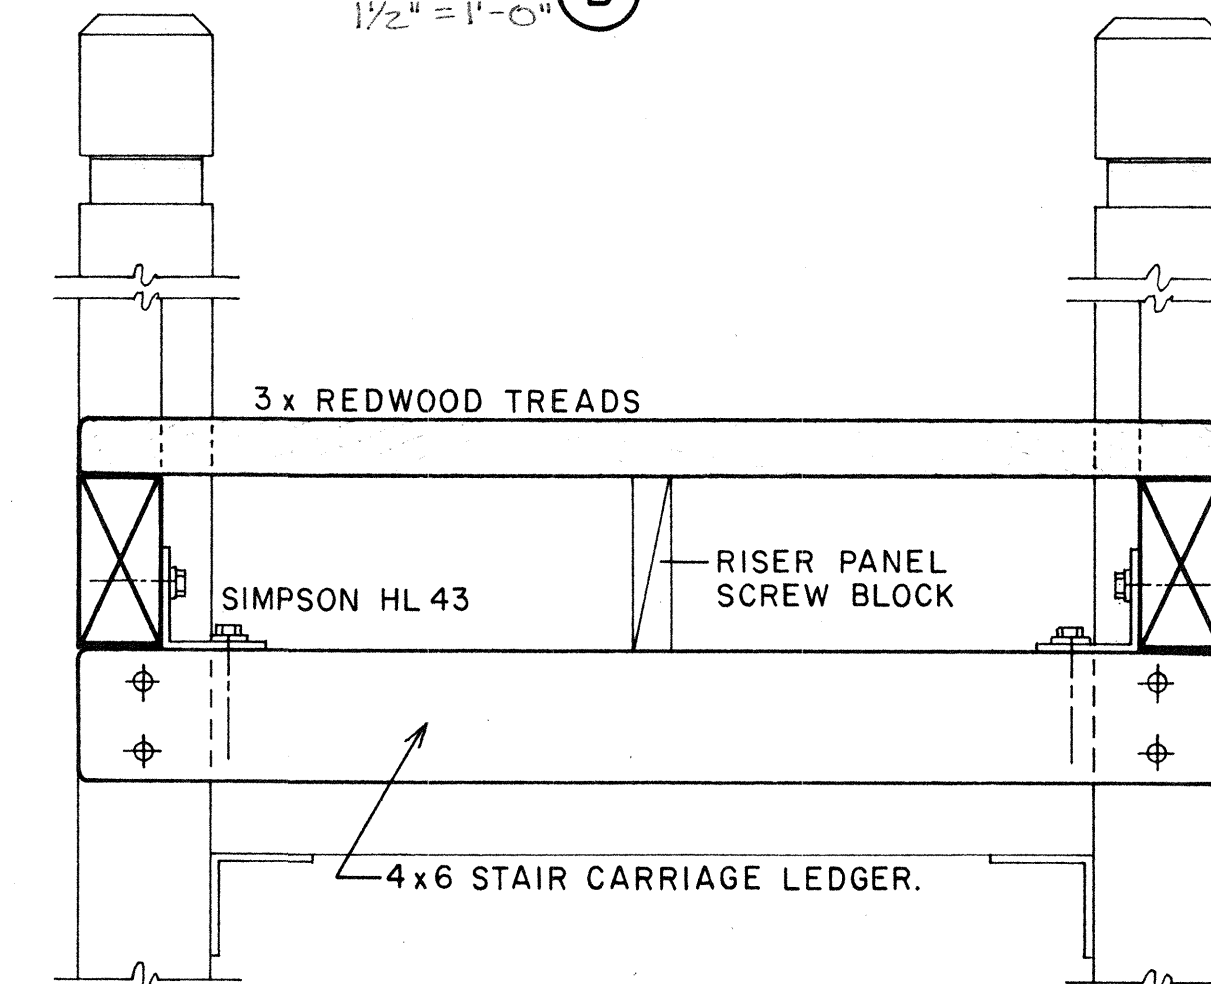


TRANSVERSE STAIR SECTION

1 1/2" = 1'-0" 3

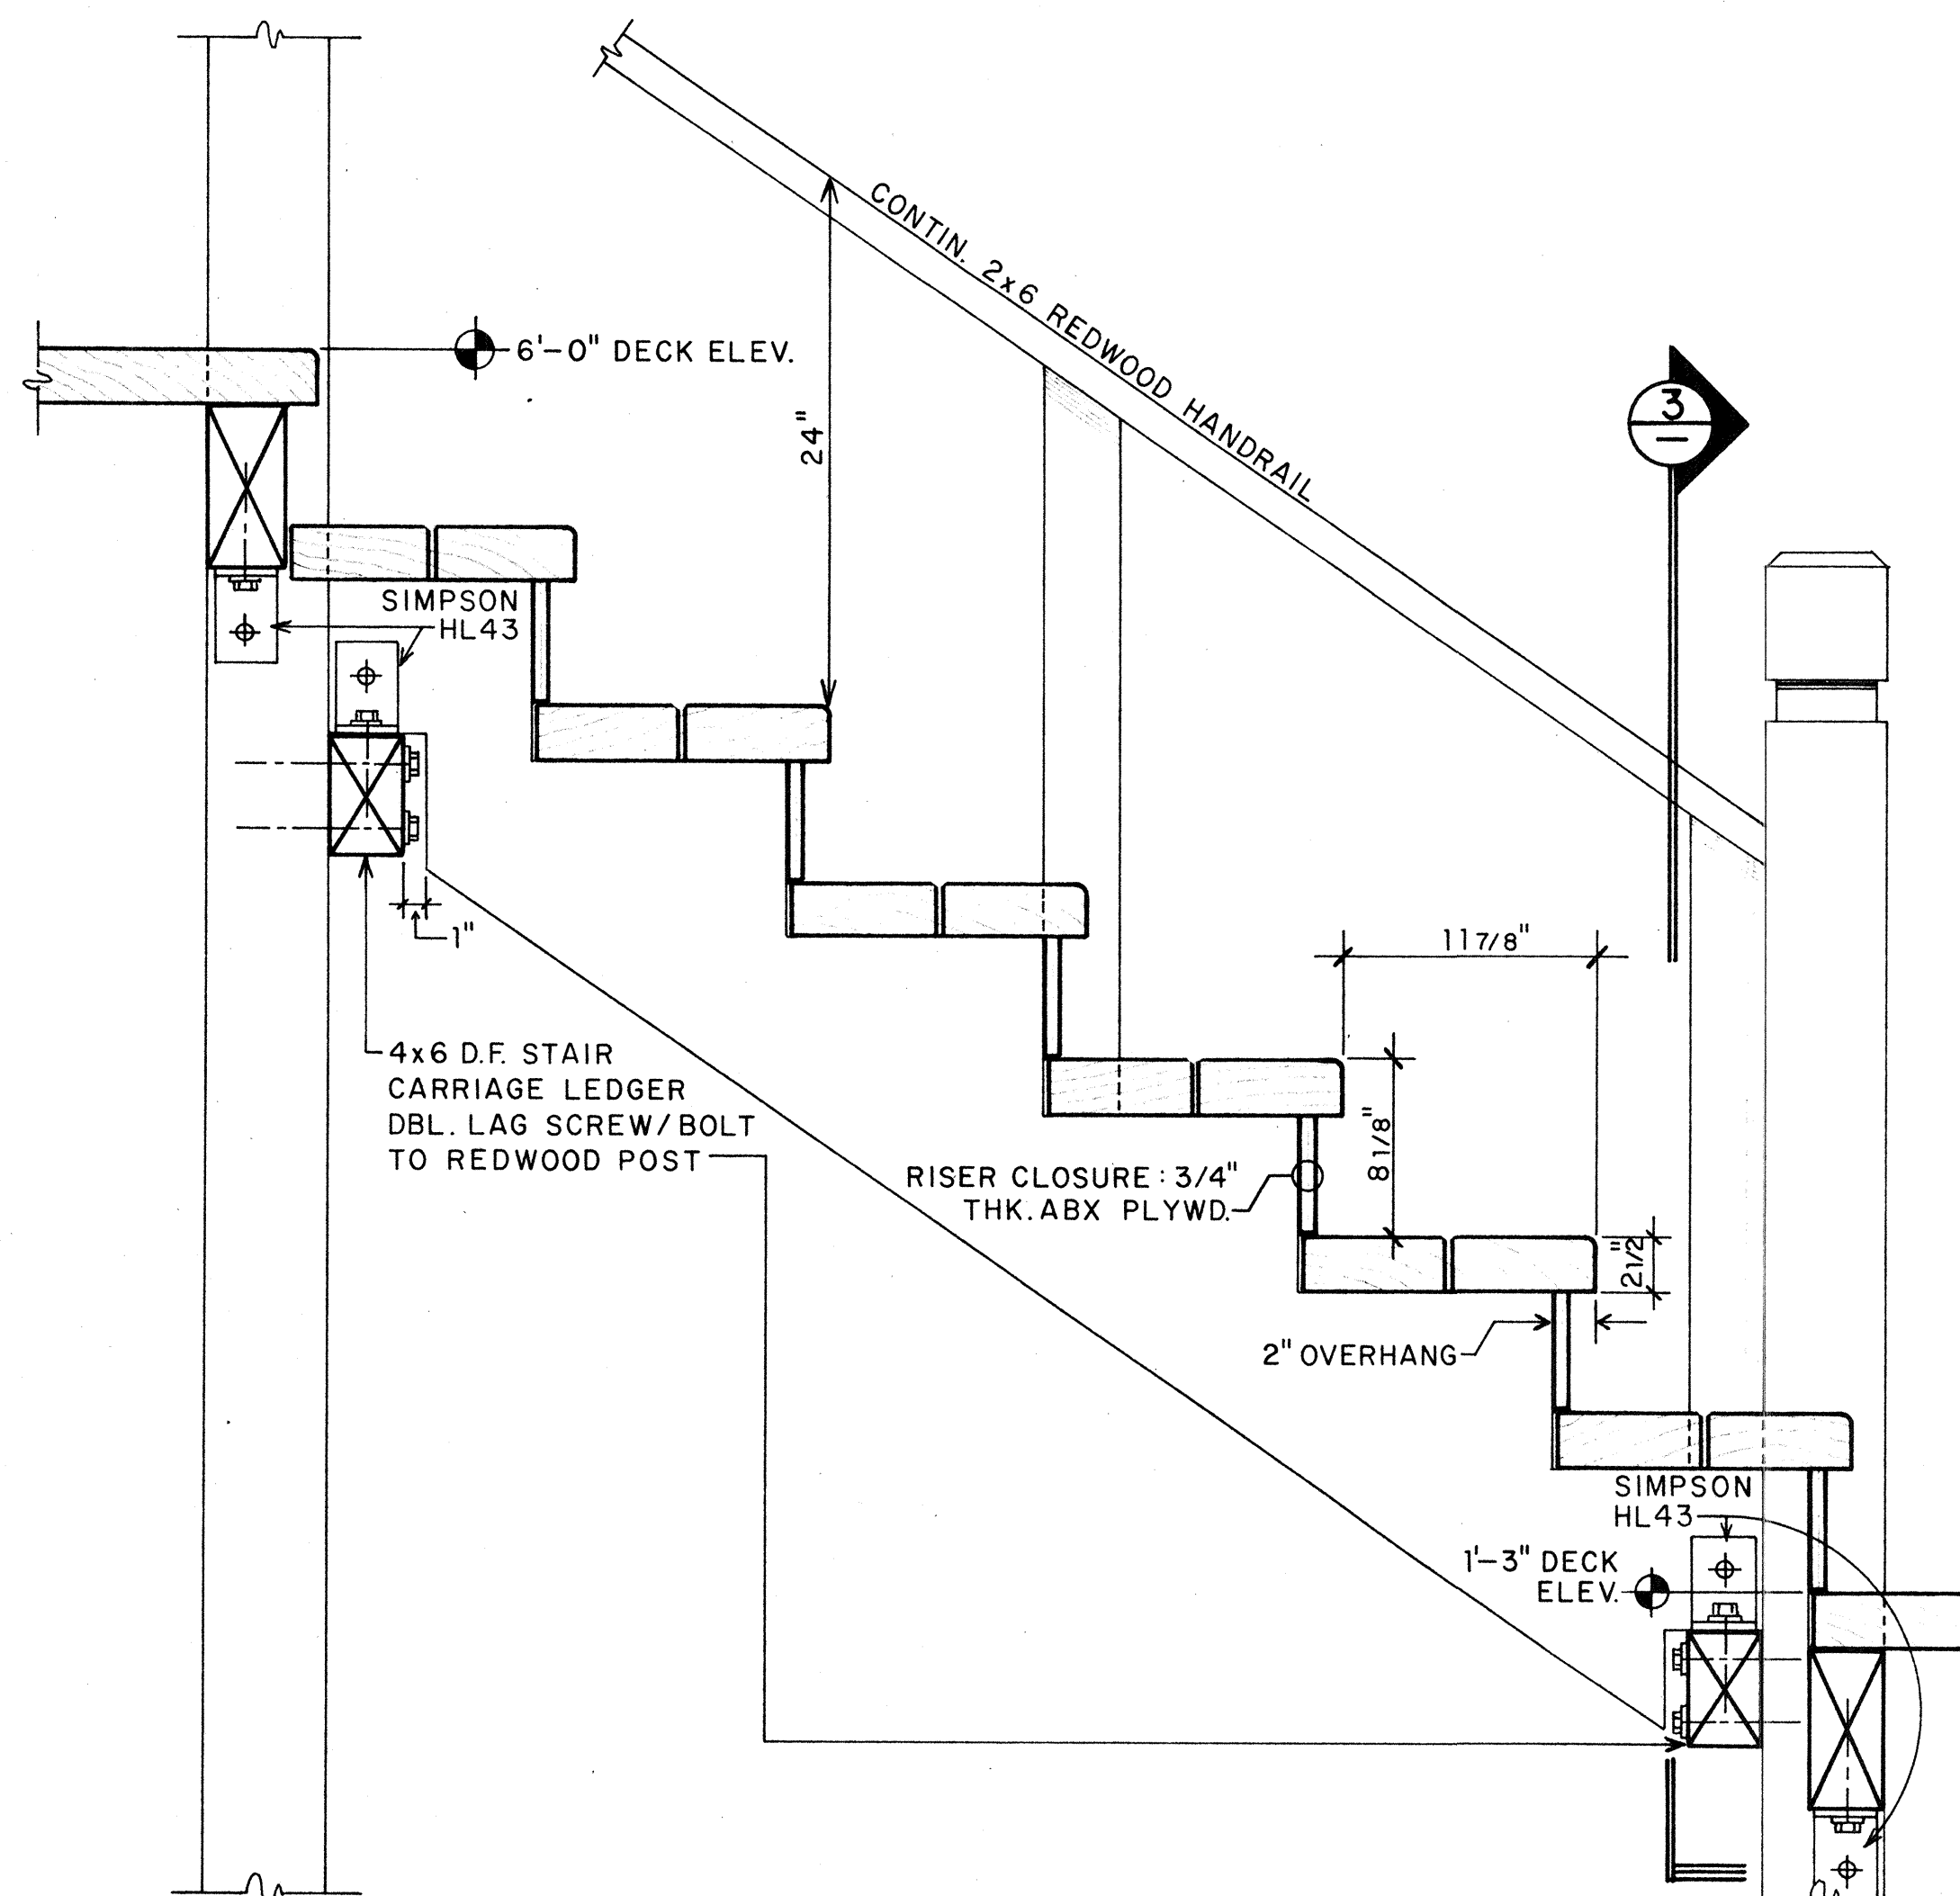

LONGITUDINAL STAIR SECTION

1 1/2" = 1'-0" F

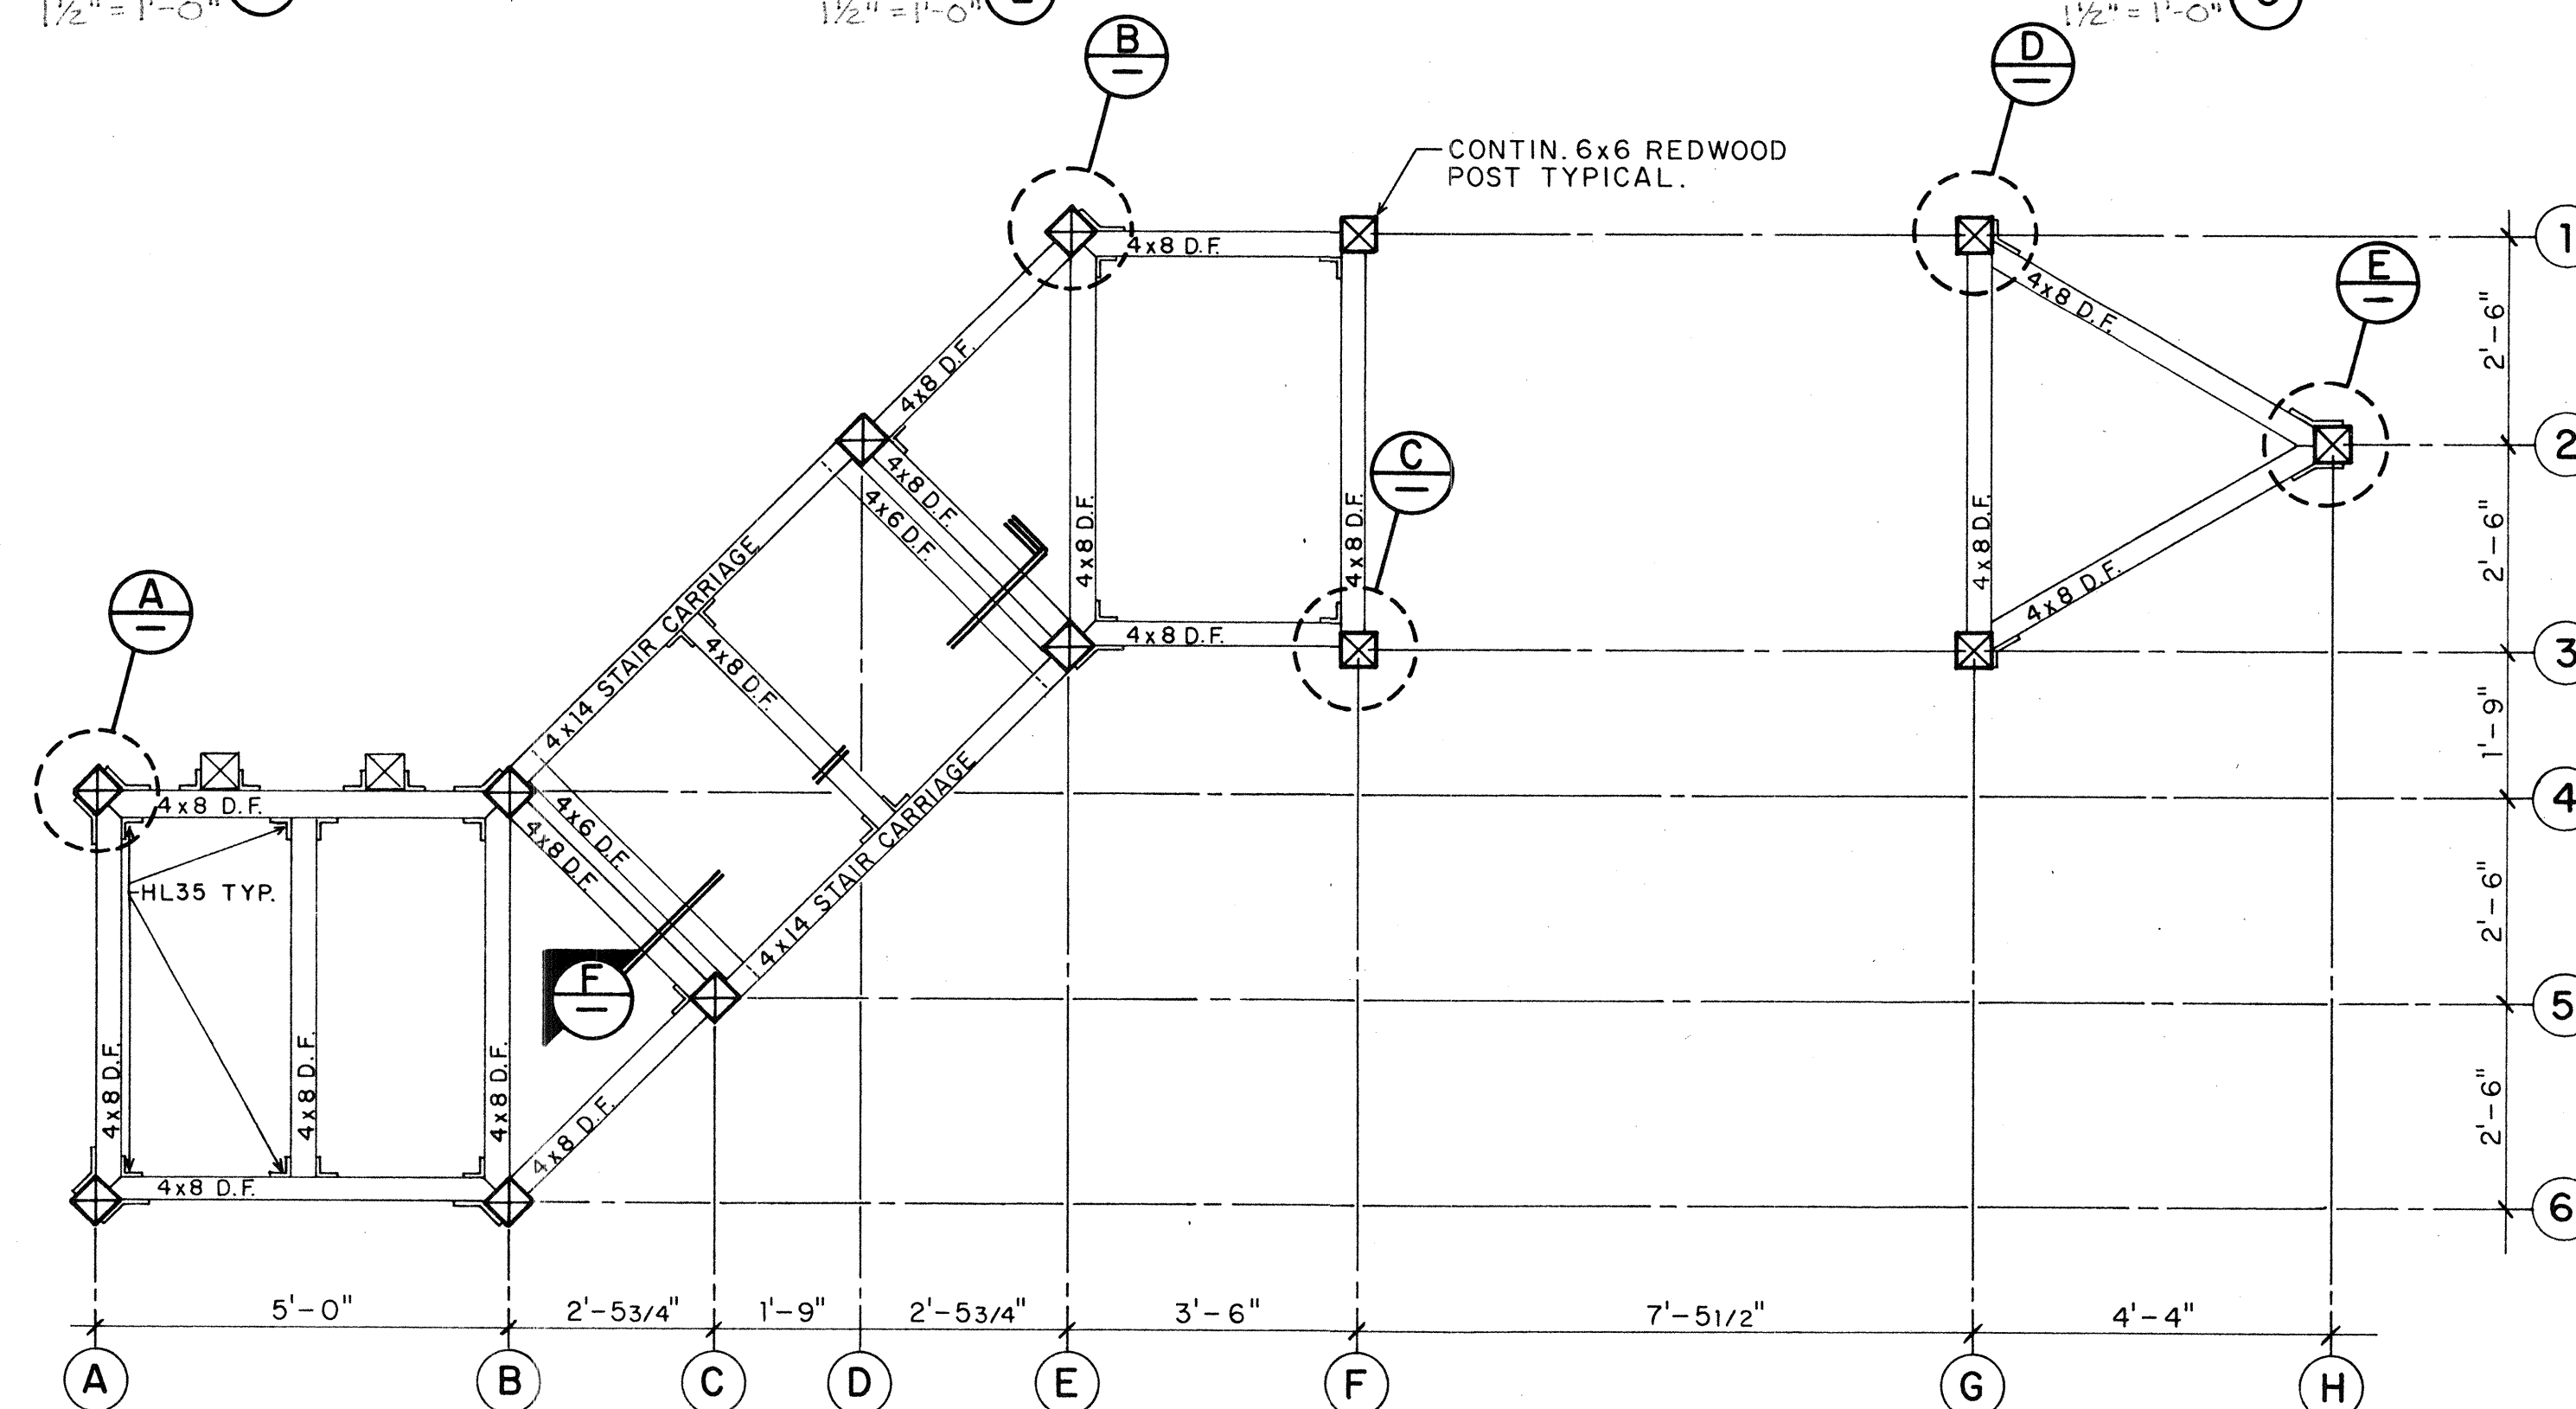

STRUCTURE "C" DECK FRAMING PLAN

1 1/2" = 1'-0"

APPROVED PLAN

date
SAN MARINO BUILDING DEPT.

Saint Edmund's Nursery School
Playground Remodel
1175 San Gabriel Boulevard
San Marino, California 91108-8038
Ph: (818) 792-7742

Dube' Donnelly Designs

Phillip Dube'
Tel: (818) 799-3379
722 Garfield Ave.
So. Pasadena, Ca. 91030

Brian Donnelly
Tel: (310) 371-7701
3644 Del Amo Blvd. - C
Torrance, Ca. 90503

CREATIVE
Planning & Design


The drawings and specifications are instruments of service and remain the property of Dube' Donnelly Designs. The drawings and specifications shall not be used by the owner on other projects, additions to this project, or for the completion of this project by others, provided that Dube' Donnelly Designs is not in default under this agreement, except by agreement in writing and appropriate compensation to Dube' Donnelly Designs. The author of the drawings and specifications shall retain all common law, including copyright. All rights reserved.

MAY 08 1997
Date

Scale NOTED

Drawn PSD

Job SENS

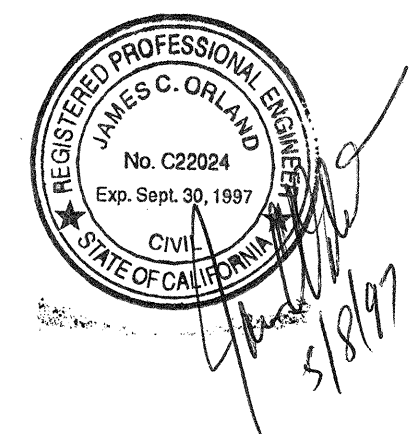

(0-3.0)