



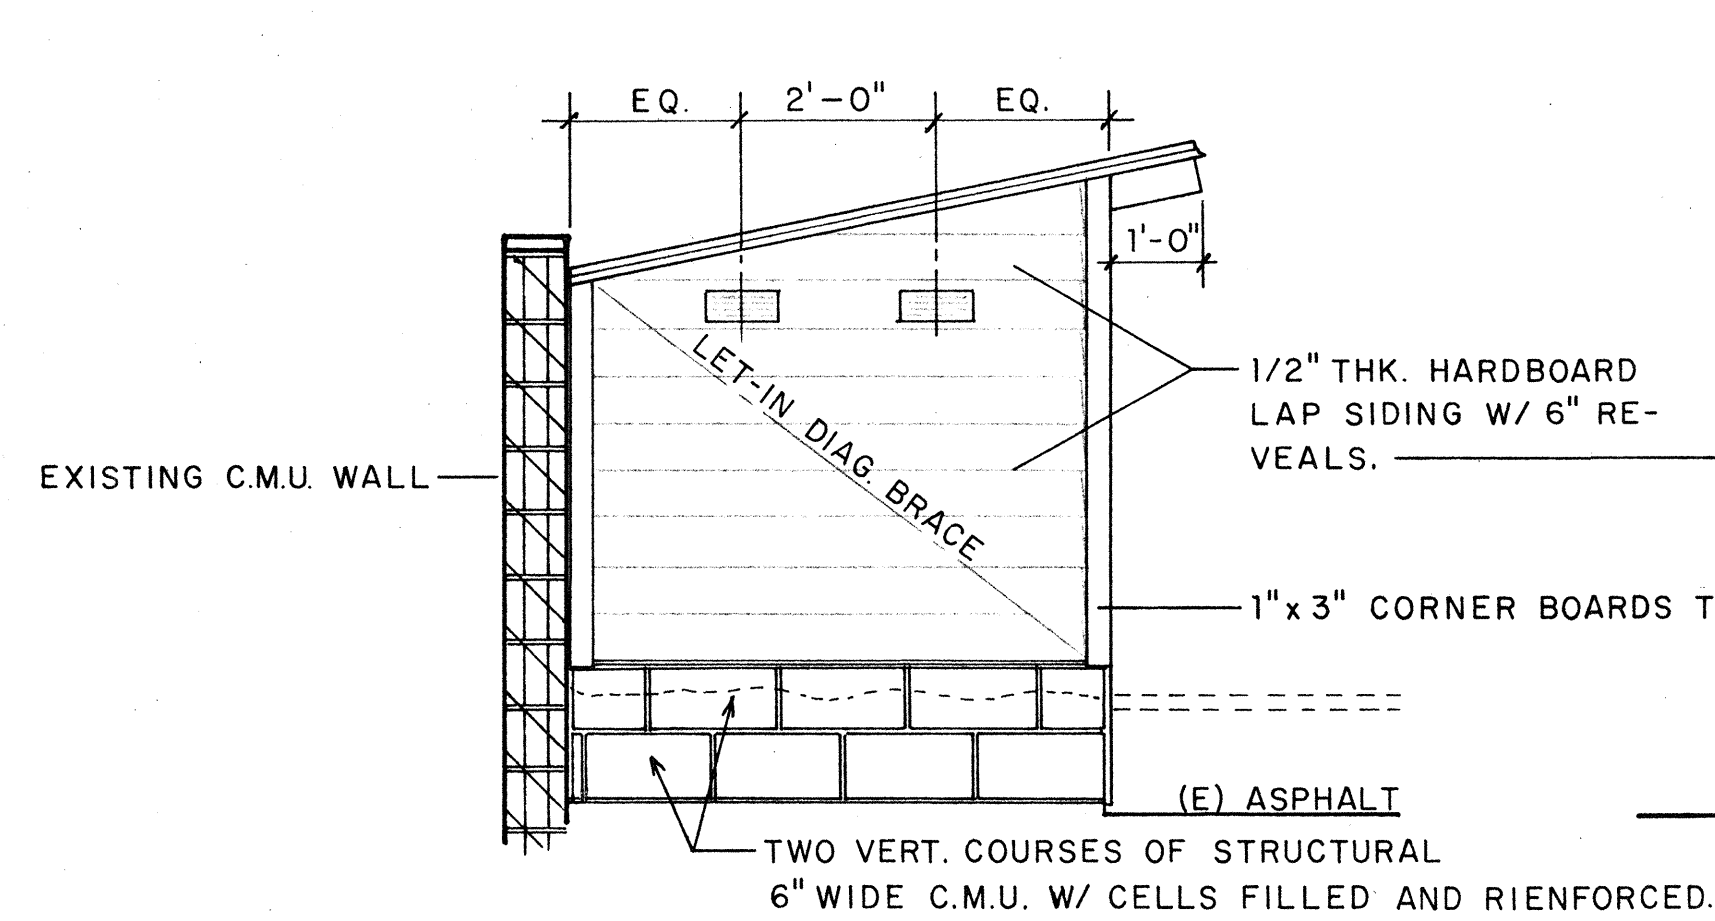


WEST SIDE ELEVATION

1/2" = 1'-0"

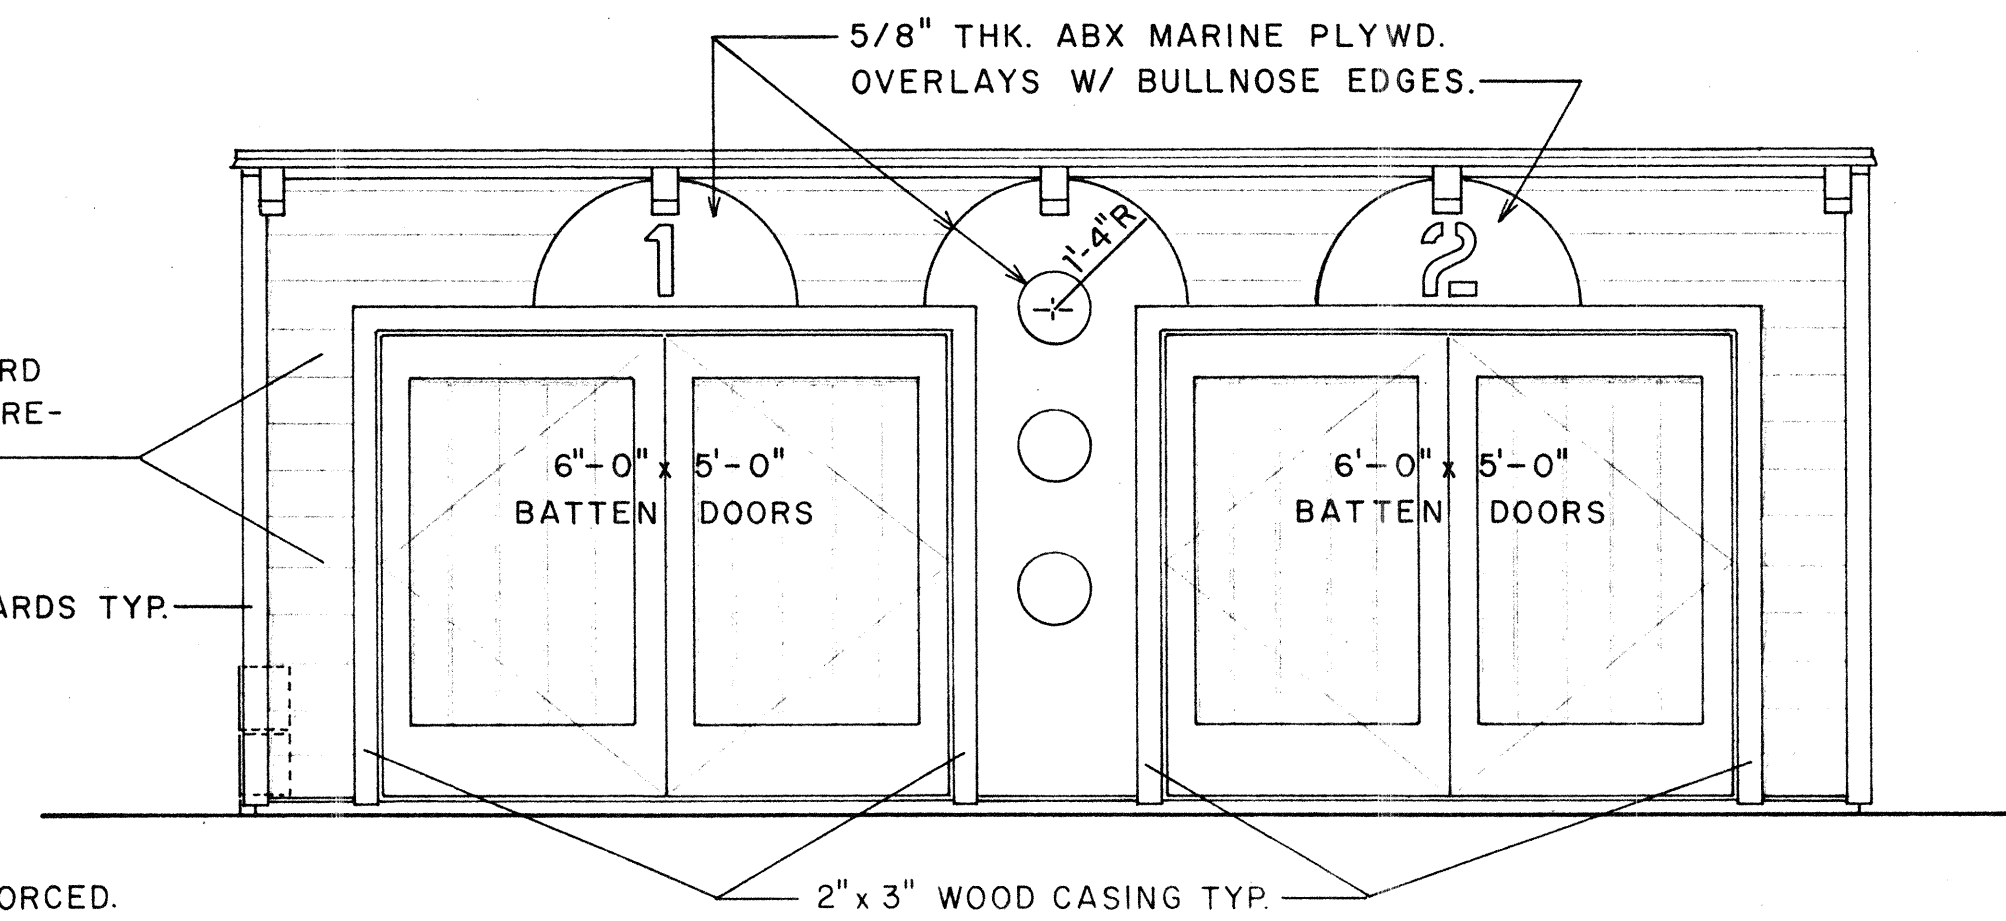


SOUTH ELEVATION OF TRICYCLE SHED

1/2" = 1'-0"

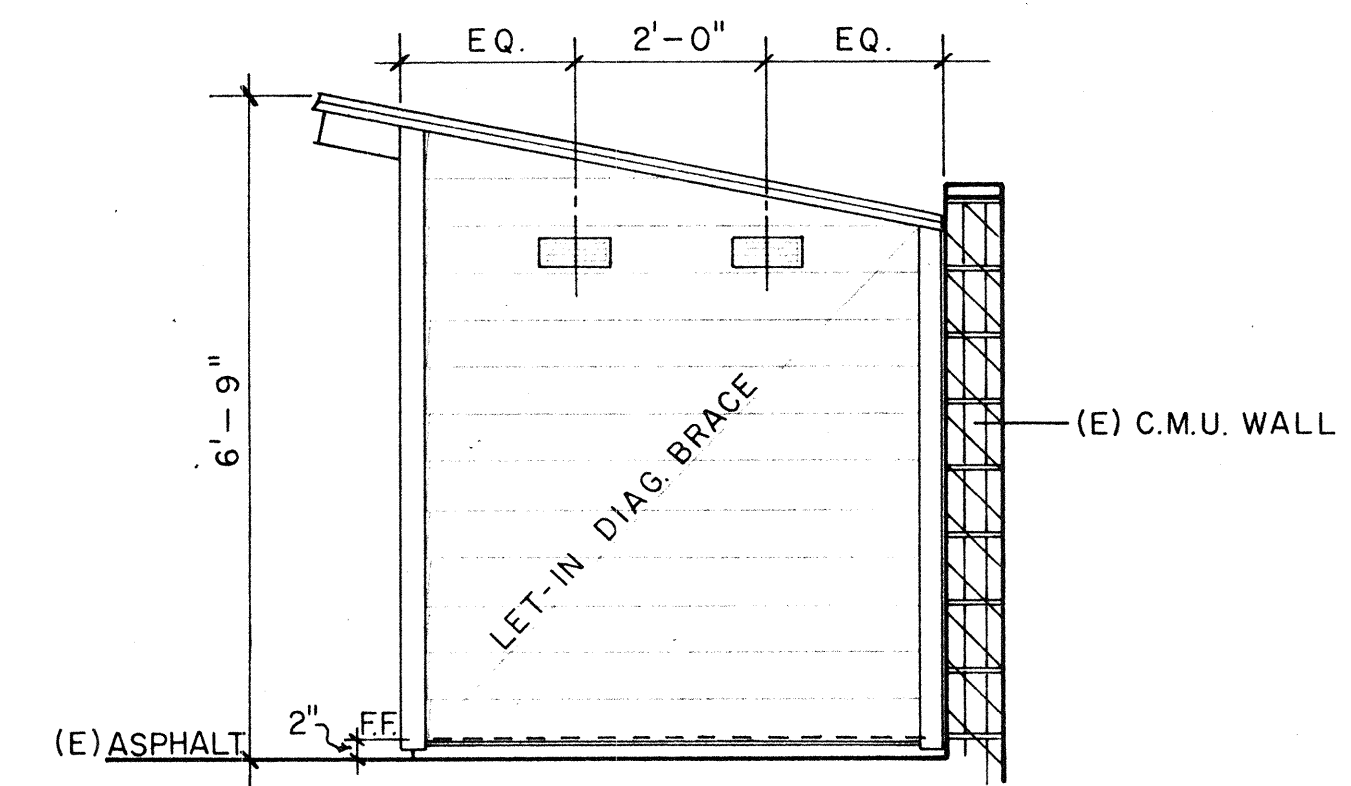


EAST SIDE ELEVATION

1/2" = 1'-0"

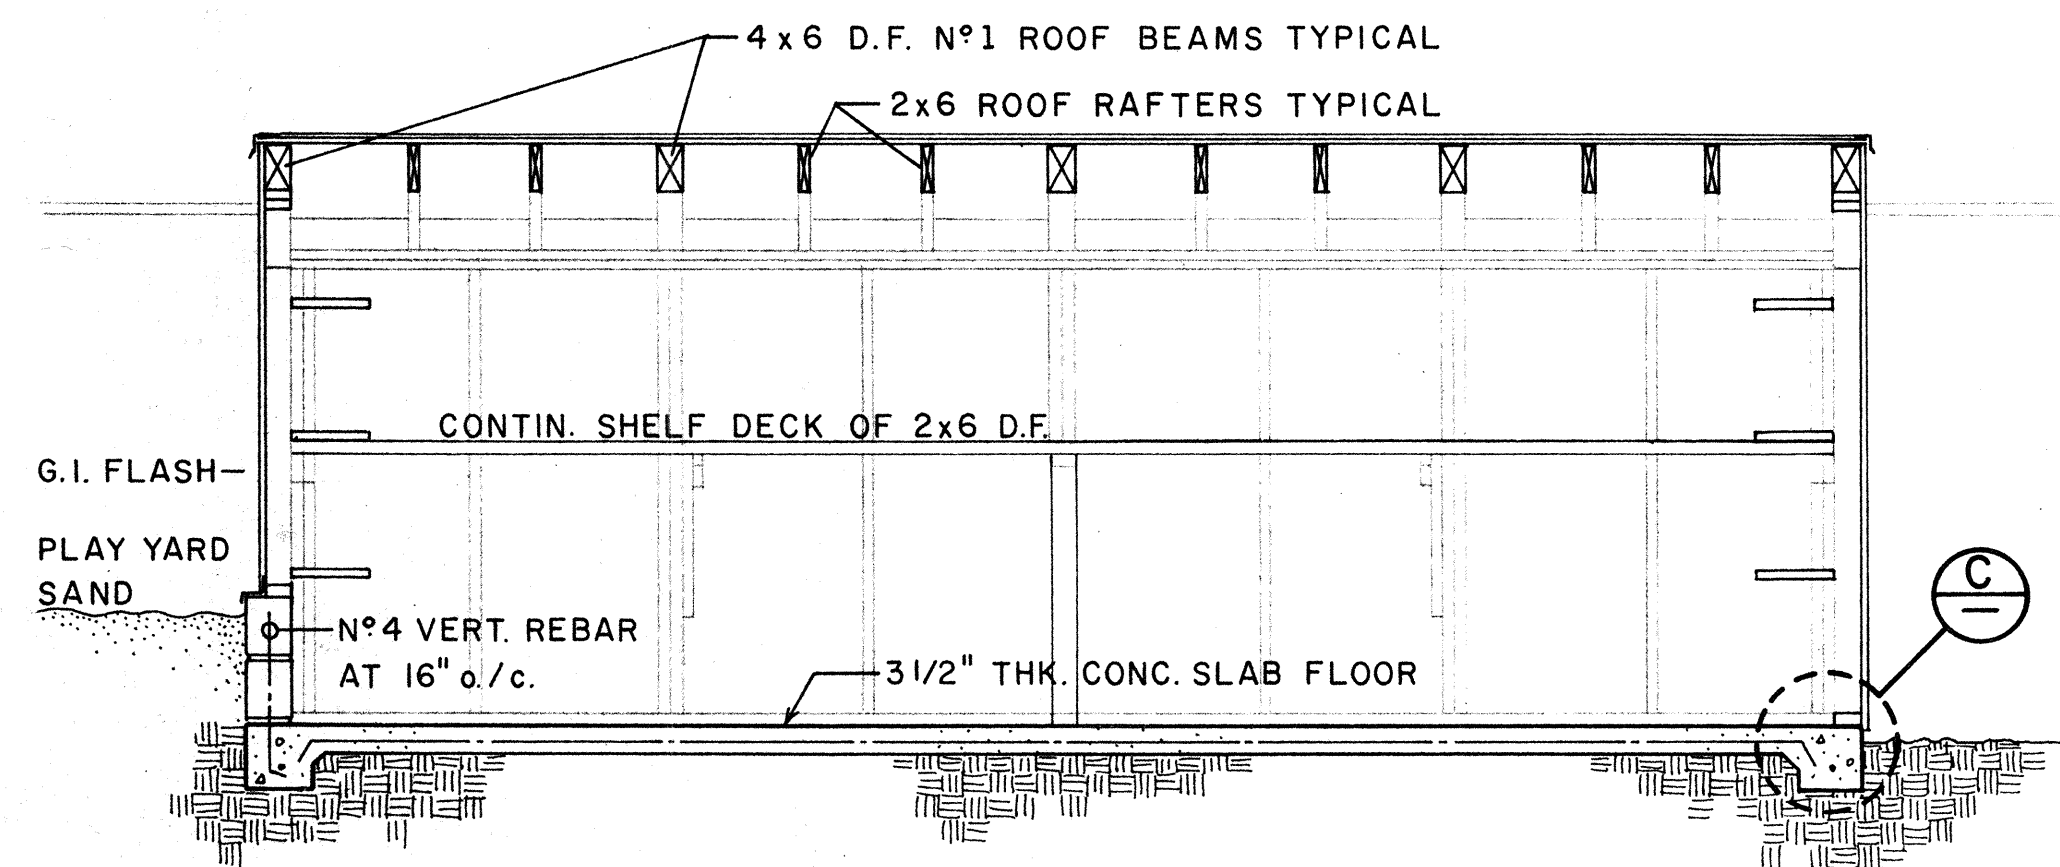


LONGITUDINAL SECTION

1/2" = 1'-0"

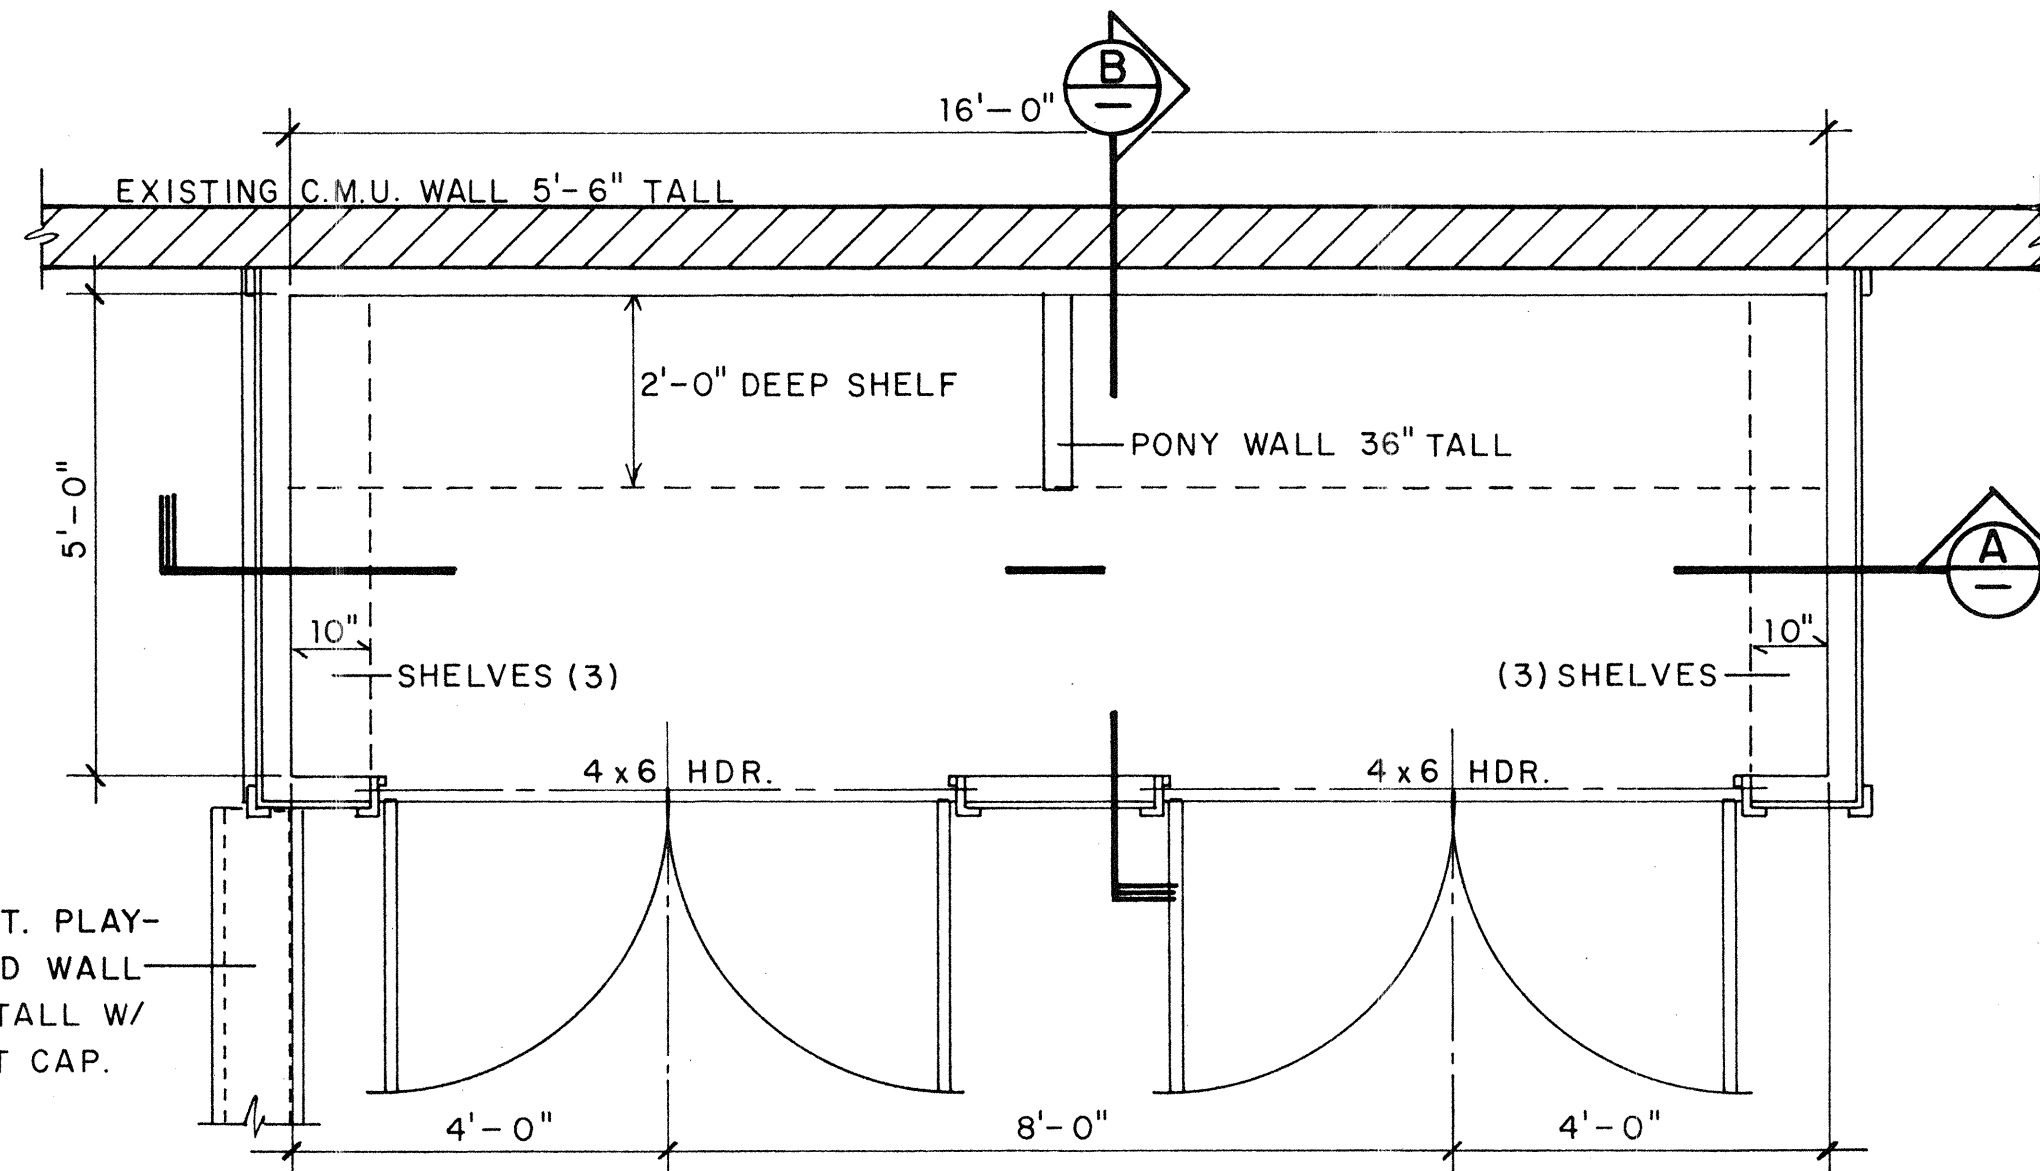


FLOOR PLAN OF TRICYCLE SHED

1/2" = 1'-0"

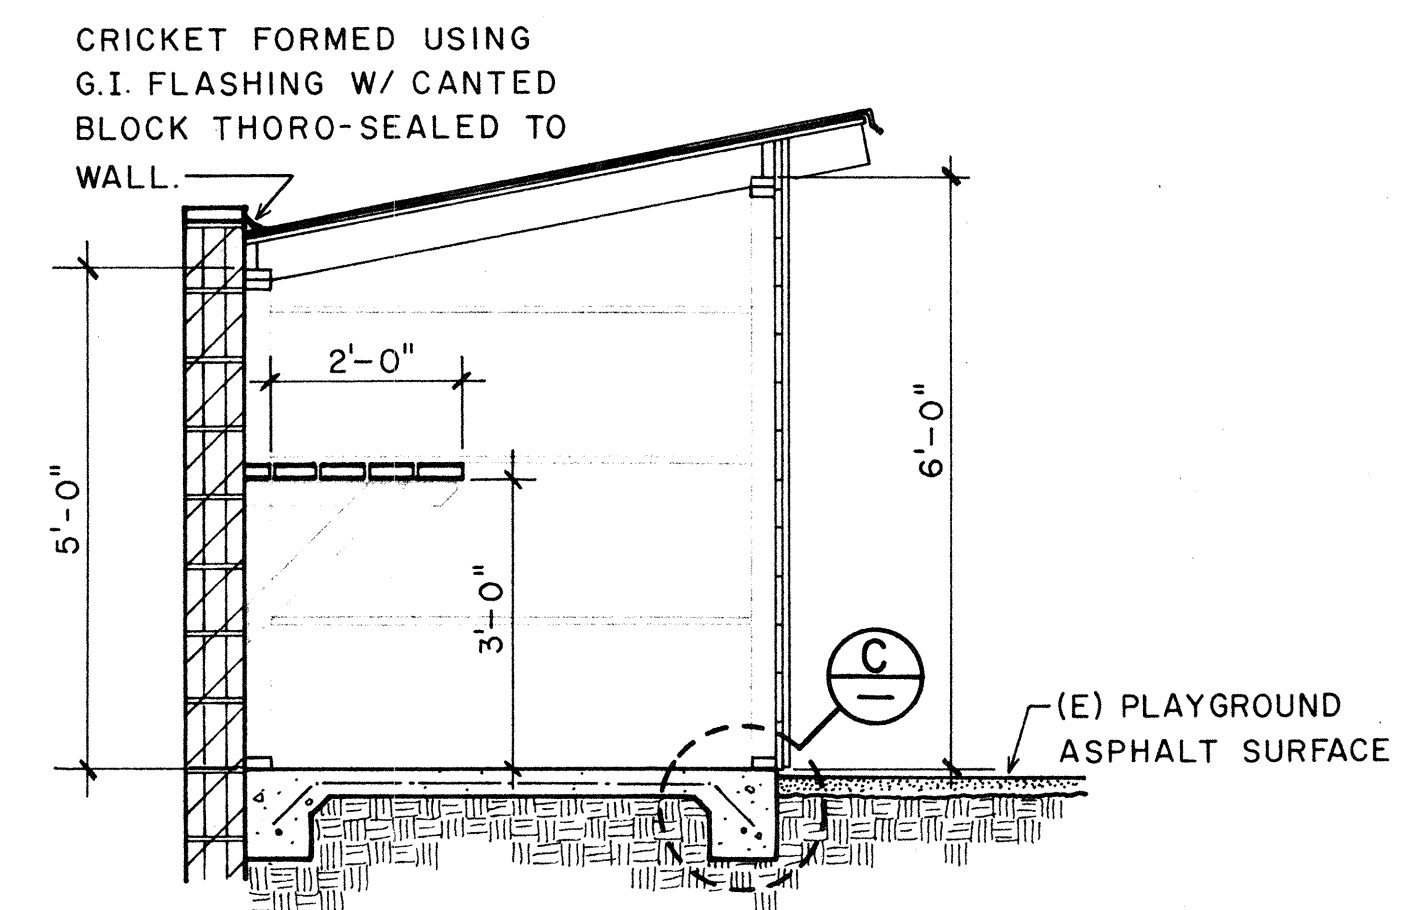


TRANSVERSE SECTION

1/2" = 1'-0"

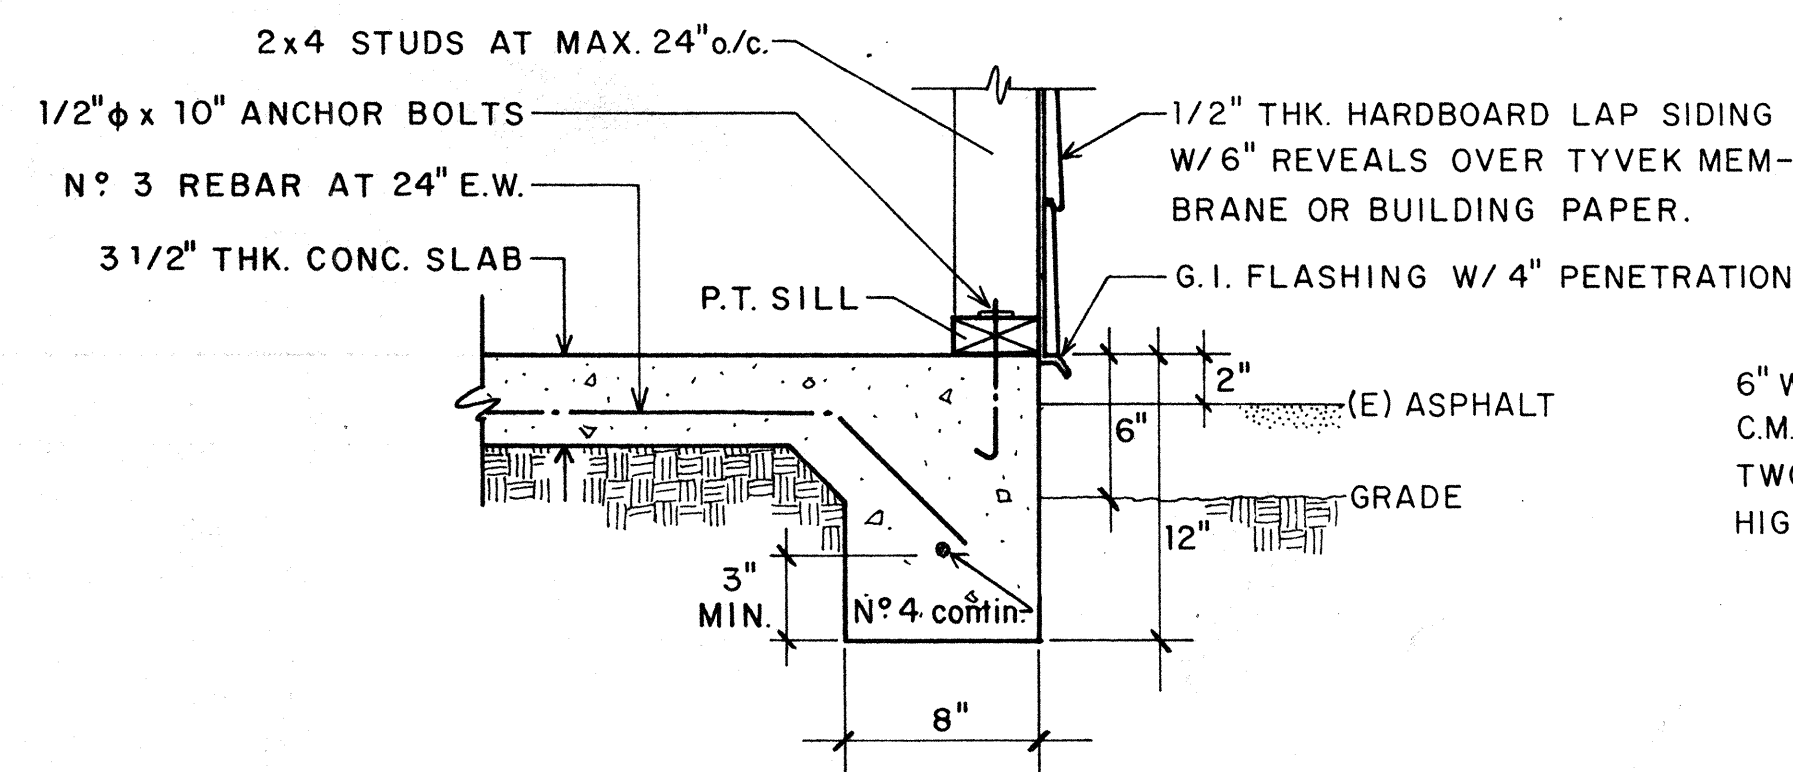


FOUNDATION DETAIL

1/2" = 1'-0"

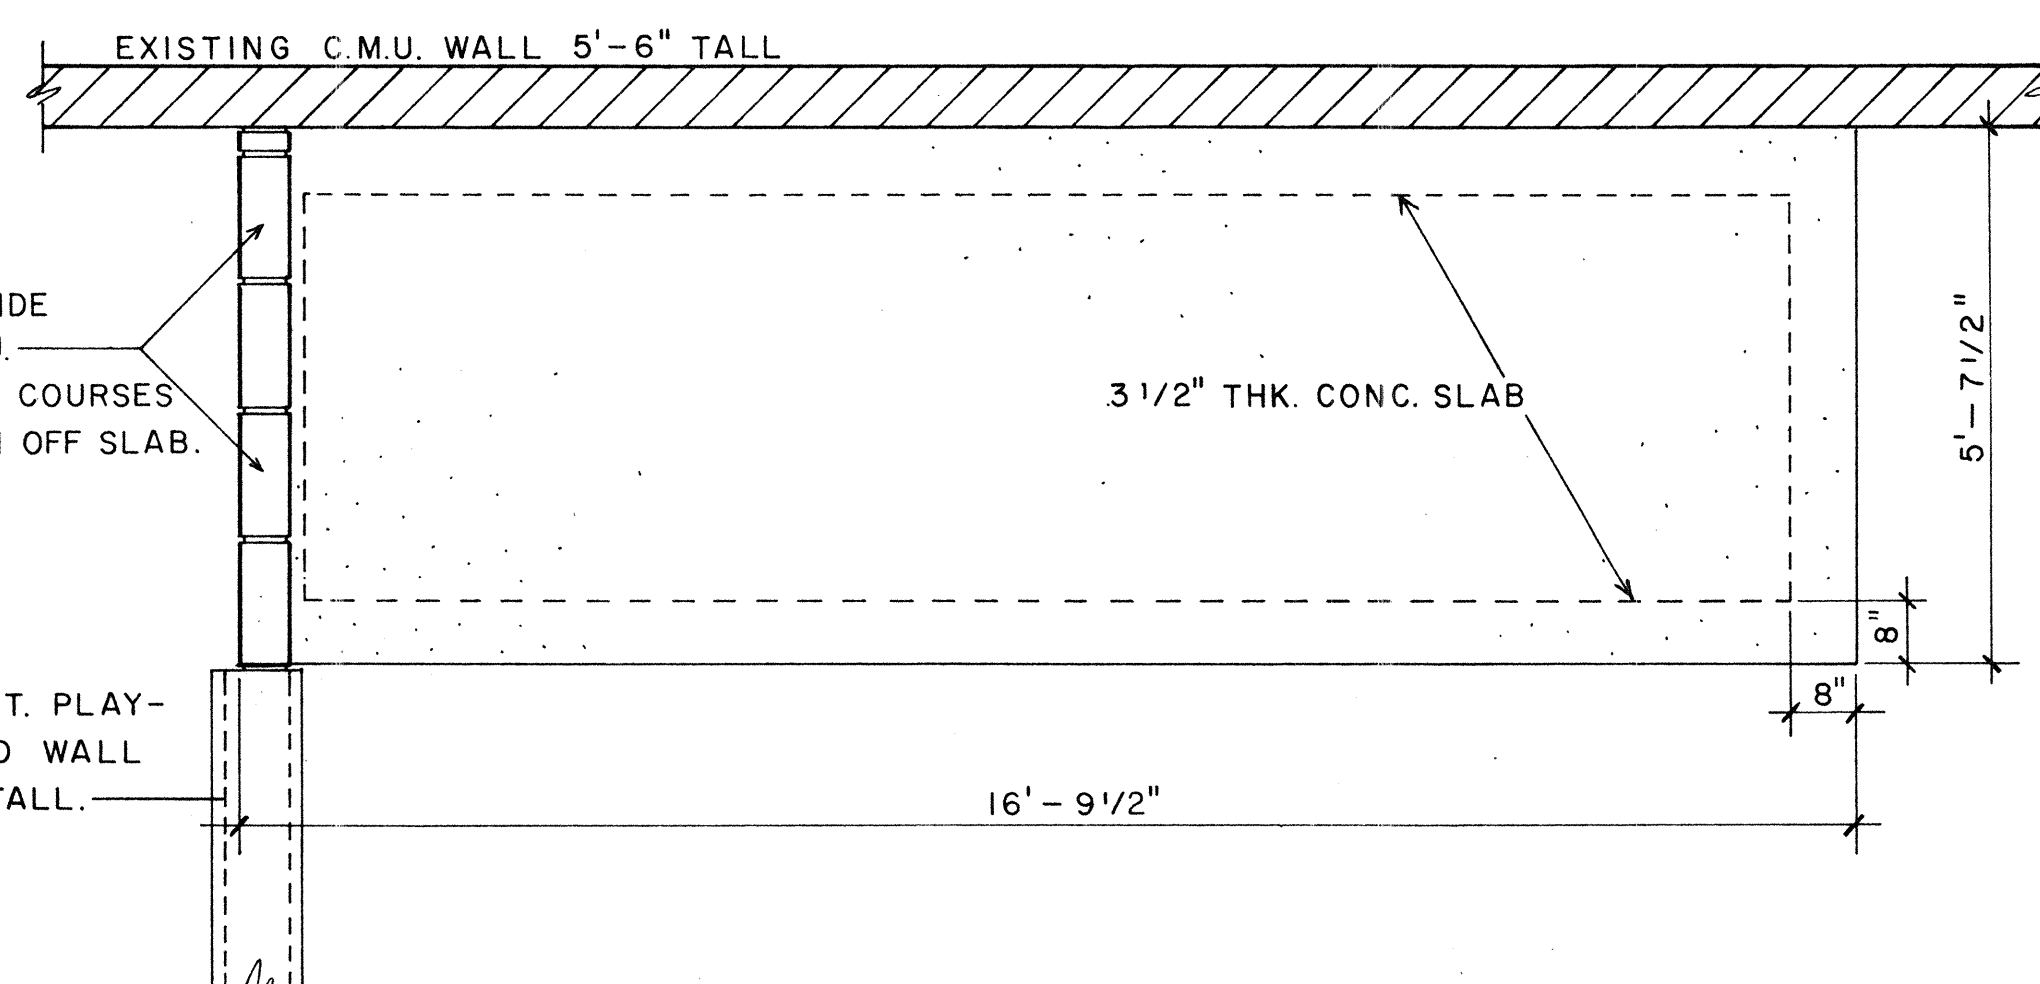

FOUNDATION PLAN

1/2" = 1'-0"

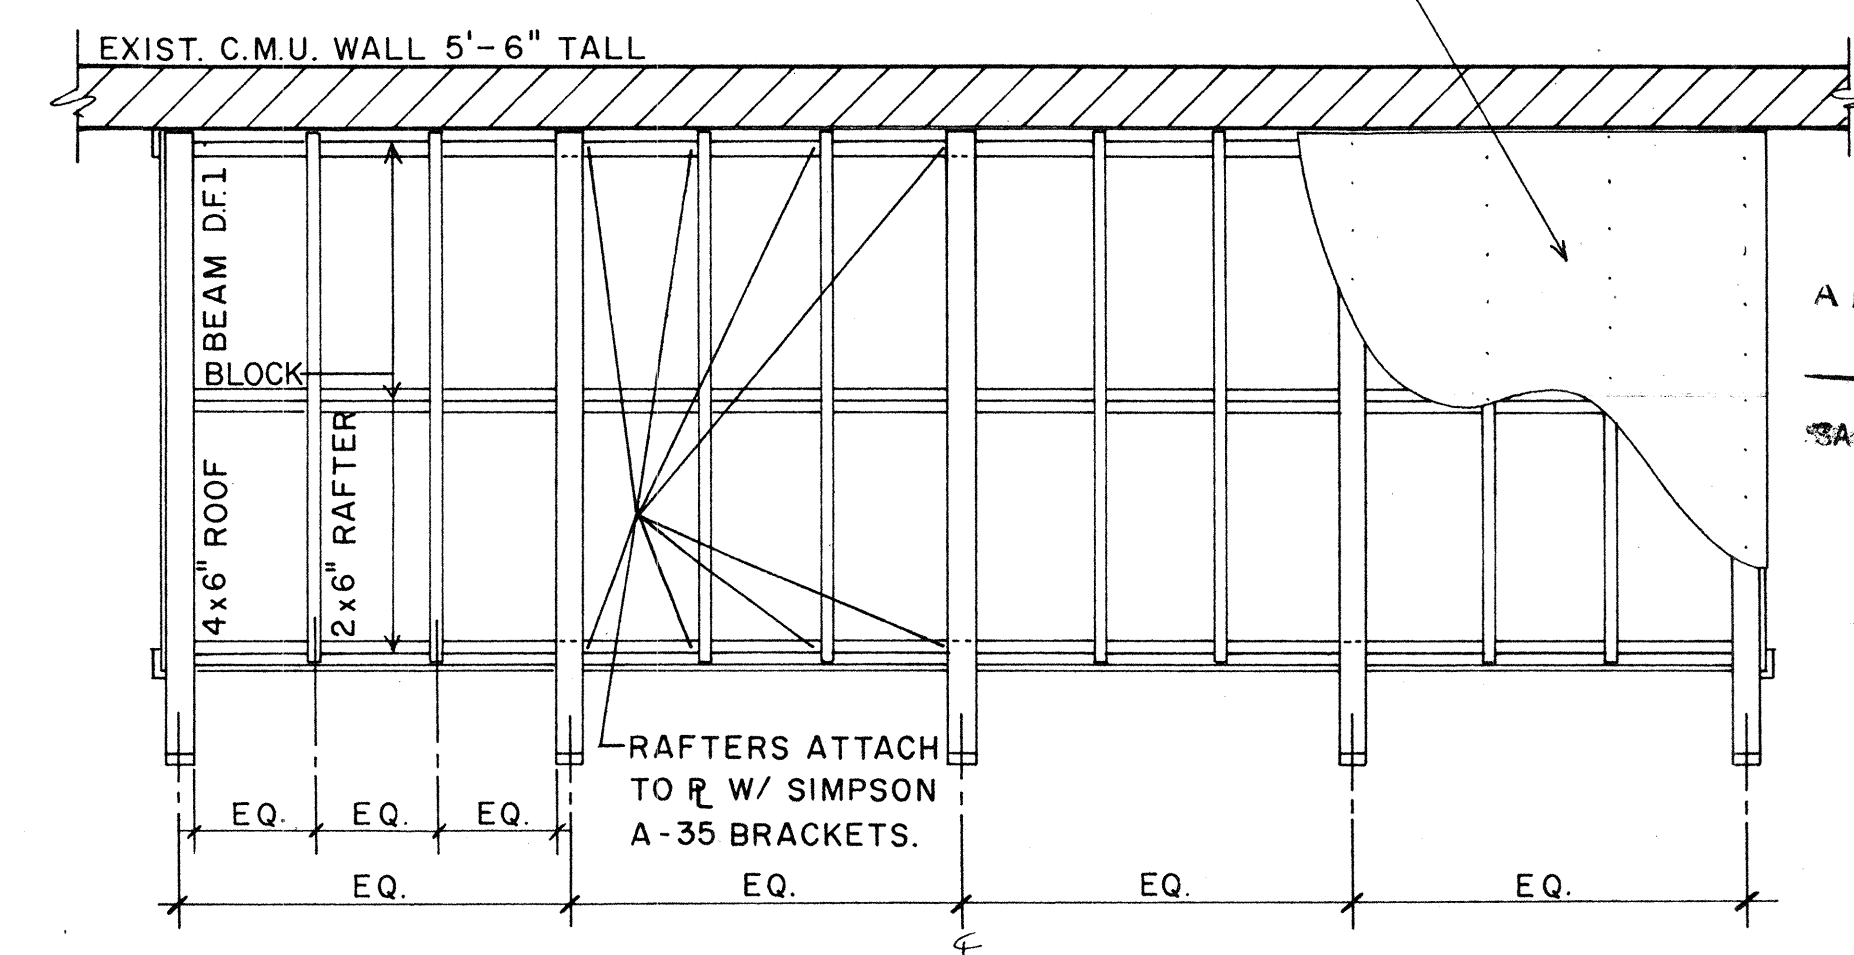

ROOF FRAMING PLAN

1/2" = 1'-0"

NOTE:

ALL EXPOSED WOOD EXCEPT DOORS AND ROOF BEAMS SHALL BE PRIMED W/ 2-COATS OF GREY OIL BASED PRIMER AND PAINTED W/ A TOP COAT OF ACRYLIC PAINT (COLORS TO BE CHOSEN BY OWNER). DOORS AND ROOF BEAMS SHALL BE CLEAR SEALED W/ OLYMPIC WATER REPELANT STAIN.

Dube' Donnelly Designs

Phillip Dube'
Tel: (818) 799-3379
722 Garfield Ave.
So. Pasadena, Ca. 91030

Brian Donnelly
Tel: (310) 371-7701
3644 Del Amo Blvd. - C
Torrance, Ca. 90503

CREATIVE
Planning & Design

Saint Edmund's Nursery School
Playground Remodel
1175 San Gabriel Boulevard
San Marino, California 91108-8038
Ph: (818) 792-7742

APPROVED PLAN
date 8/8/97
SAN MARINO BUILDING DEPT.

The drawings and specifications are instruments of service and remain the property of Dube' Donnelly Designs whether the project is executed or not. The drawings and specifications shall not be used by the owner on other projects, additions to this project, or for the completion of this project by others, provided that Dube' Donnelly Designs is not in default under this agreement, except by agreement in writing and appropriate compensation to Dube' Donnelly Designs shall be deemed the author of the drawings and specifications and shall retain all common law, including copyright. All rights reserved.

MAY 08 1997

Date

Scale NOTED

Drawn PJD

Job SENS

T 3-1.0