

ST. EDMUNDS CHURCH & PRESCHOOL

1175 San Gabriel Blvd







Project : Replace Failed/ Condemned Brick Wall on East Property Line

Demolition / Construction Notes :

1. NOTHING CONTAINED IN THESE DRAWINGS OR ANY ACCOMPANYING CONTRACT DOCUMENTS SHALL CREATE ANY CONTRACTUAL RELATIONSHIP BETWEEN THE CONTRACTOR AND/OR ANY OF HIS SUB-CONTRACTORS AND ALPINE DESIGN GROUP.
2. THE CONTRACTOR SHALL FURNISH ALL LABOR, EQUIPMENT, AND MATERIALS ETC. NECESSARY TO PROVIDE A COMPLETE FINISHED PROJECT INCLUDING ALL ITEMS NOT SHOWN ON THESE DRAWINGS BUT REQUIRED TO PROVIDE A COMPLETE PROJECT CONSISTENT WITH THE INTENT OF THE CONTRACT DOCUMENTS.
3. ALL WORK SHALL BE ACCOMPLISHED IN A PROFESSIONAL WORKMANSHIP LIKE MANNER USING ONLY HIGH QUALITY MATERIALS CONSISTENT WITH THE CONTRACT DOCUMENTS. ALL WORK SHALL COMPLY WITH ALL APPLICABLE BUILDING CODES.
4. THE GENERAL CONTRACTOR SHALL VERIFY ALL DIMENSIONS AND SITE CONDITIONS BEFORE STARTING WORK. ALPINE DESIGN GROUP SHALL BE NOTIFIED OF ANY DISCREPANCY.
5. NOTES AND DETAILS ON DRAWINGS SHALL TAKE PRECEDENCE OVER THESE GENERAL NOTES.
6. ALL MATERIAL AND WORKMANSHIP SHALL CONFORM TO THE CALIFORNIA AND UNIFORM BUILDING CODE, LATEST EDITION.
7. THE DESIGN, ADEQUACY AND SAFETY OF ERECTION BRACING, SHORING, TEMPORARY SUPPORTS, ETC. IS THE SOLE RESPONSIBILITY OF THE CONTRACTOR AND HAS NOT BEEN CONSIDERED BY MGA DESIGN GROUP OR ANY OTHER CONSULTING ENGINEERS. THE CONTRACTOR IS RESPONSIBLE.
8. ALL EXISTING MAN GATES (WROUGHT IRON) TO BE PROTECTED AND REINSTALLED AFTER DEMOLITION PHASE IS COMPLETE.
9. PARTIAL DEMOLITION TO ELIMINATE CONDEMNATION INCLUDES: SAW CUTTING THE EXISTING WALL SEGMENTS AS INDICATED PERMANENTLY DEMOLISHING ALL BRICK MATERIALS ABOVE THE SAW CUT, CAPPING THE WALL WITH DEMOLISHED BRICKS. AFTER THE WALL HAS HAD ANY REMAINING CRACKED MORTAR JOINTS REPAIRED AND REINFORCED.
10. FULLY DEMOLISHED SECTION OF WALL TO BE REPLACED WITH STANDARD RETAINING WALL. 6' FOOTING PER DETAIL 6 FROM SAN MARINO. THE NEW CMU WALL WILL THEN BE TREATED WITH MIM BRICK VENEER. BRICK VENEER COLOR SELECTION TO CLOSELY MATCH EXISTING BRICK. WALL SECTIONS THAT REMAIN FINAL COLOR CHOICE WILL BE MADE BY REPRESENTATIVES OF THE CHURCH AND THE CITY OF SAN MARINO.
11. EXISTING PLASTER FEATURES TO BE TIED INTO NEW CMU REINFORCEMENT THROUGH THE USE OF DRILLED IN & ERODED EMBEDMENT BULBS.
12. INSTALL BRICK CAP TO EXISTING WALL. SECTION PREPARE THE WALL AS REQUIRED TO RECEIVE NEW CAP BRICK.
13. EASTERN PROPERTY LINE MEASURED FROM CENTERLINE OF SAN GABRIEL BLVD. VARYING WIDTH OF BLVD. RESULTS IN PROPERTY LINE MARKERS BEING EITHER 50 FT TO 45 FT FROM CENTERLINE.
14. TO INSURE NEWLY CONSTRUCTED WALL MAINTAINS SAME PROPERTY LINE. PLACEMENT, FINISHED SURFACE OF NEW WALL MUST MATCH EXISTING OUTSIDE SURFACE FACING SAN GABRIEL BLVD.
15. PER CFC SECTION 506: (2) KEY BOXES (KNOX BOXES) WILL BE PLACED IN PROXIMITY OF FIRE RESCUE VEHICLE ACCESS POINTS. PROPERTY OWNER TO PURCHASE, INSTALL AND COORDINATE WITH CITY FIRE MARSHALL AS TO THE KEYS AND KEYCODES TO BE PLACED IN EACH BOX.
16. PER CFC SECTION 503: (2) DESIGNATED FIRE ACCESS ROADS WILL BE MAINTAINED AND KEPT CLEAR AT ALL TIMES. DUE TO LOW OVERHEAD CLEARANCE AT THE SOUTH DRIVEWAY, CITY WILL DESIGNATE 30 FT OF NO PARKING AT THE CURB IMMEDIATELY IN FRONT OF THE CHAPEL ENTRANCE AND THE FIRE DEPARTMENT STAND PIPE.
17. PER CFC SECTION 503.2.5.2: A 2,700 SF SAFE EVACUATION ZONE WILL BE MAINTAINED. AND PERIODIC FIRE DRILLS COORDINATED WITH THE CITY FIRE DEPARTMENT. THE EVACUATION AREA WILL BE DESIGNATED IN PAINT TO FACILITATE CLEAR CONTROL OF CHILDREN IN AN EMERGENCY.

Construction Legend

- EXISTING CONSTRUCTION TO BE REMOVED
- EXISTING CONSTRUCTION TO REMAIN
- NEW BRICK CLAD REINFORCED CMU RETAINING WALL CONSTRUCTION
- LIGHT FIXTURE - EXISTING TO REMAIN
- JUNCTION BOX - EXISTING TO REMAIN
- DETAIL CALLOUT SHEET LOCATION
- CONSTRUCTION NOTE CALLOUT
- ELEVATION CALLOUT
- PROPERTY BOUNDARY MARKER
- TYPICAL SECTION/CALL OUT

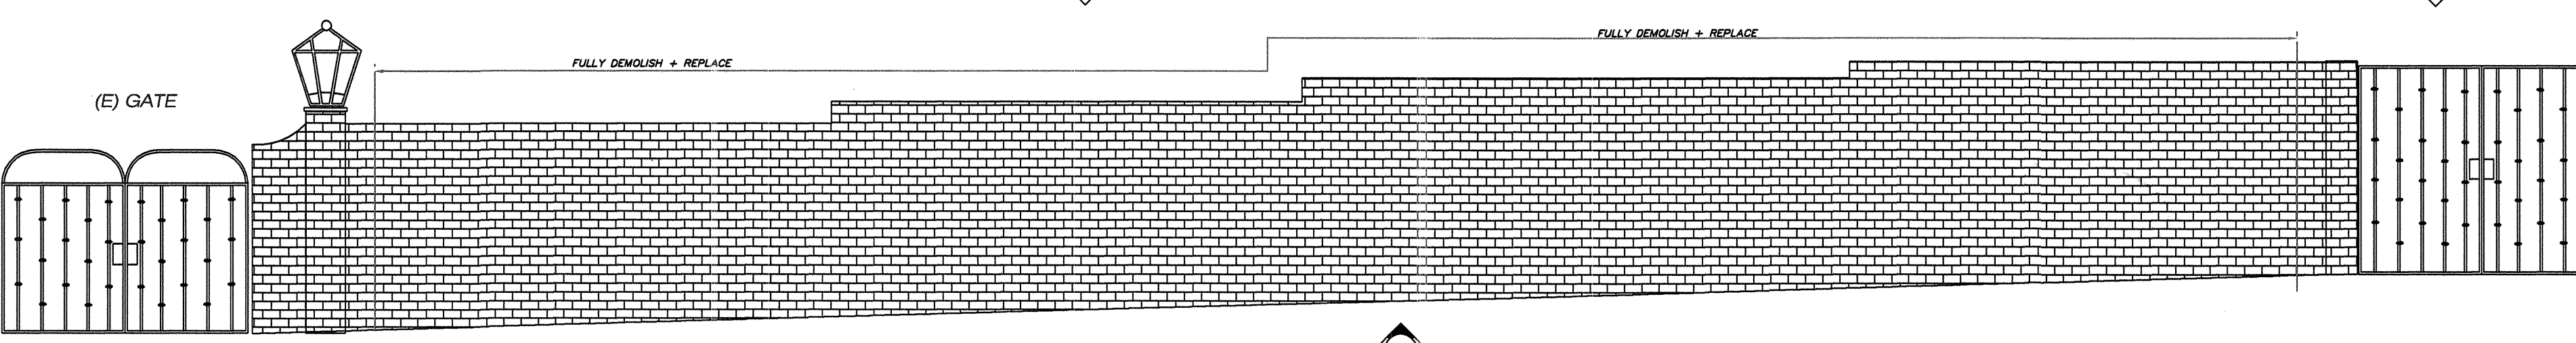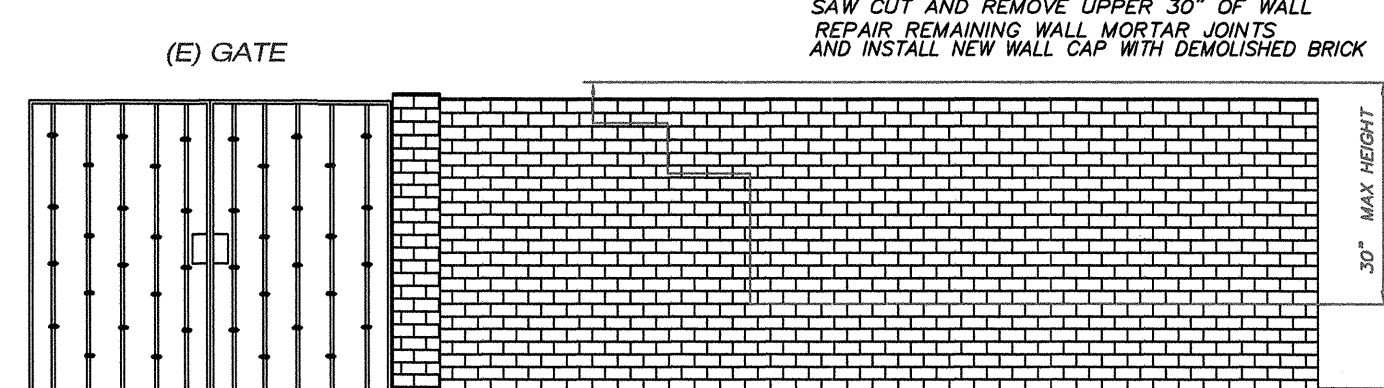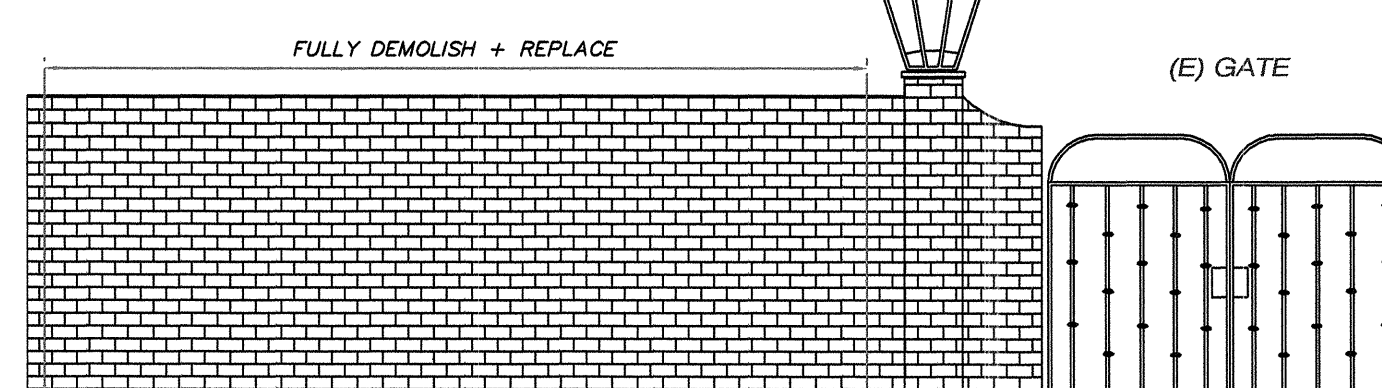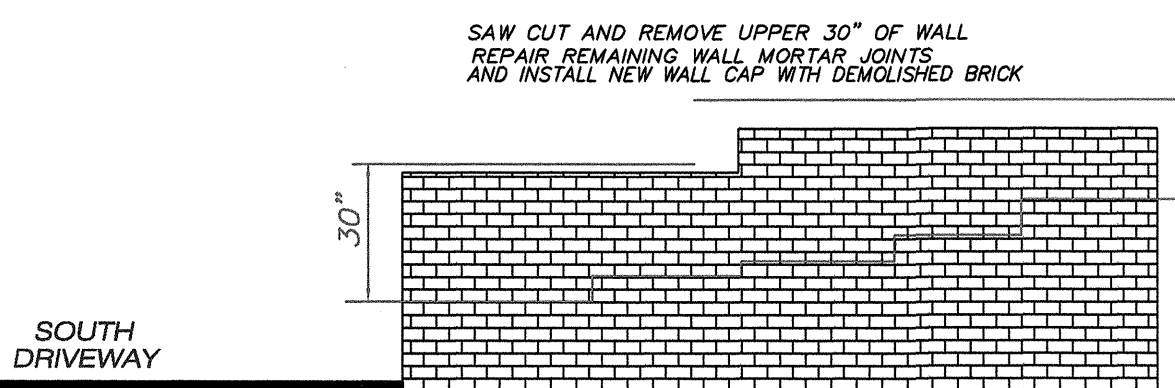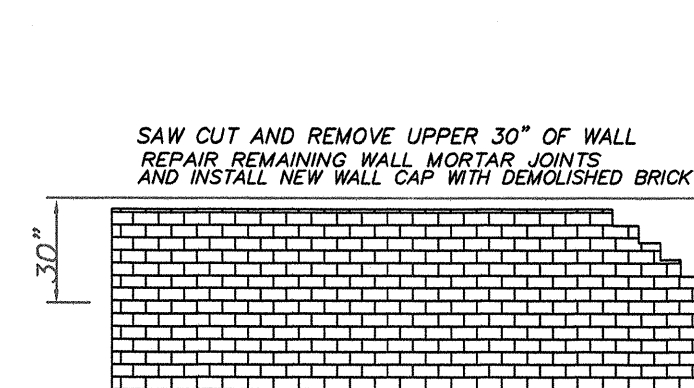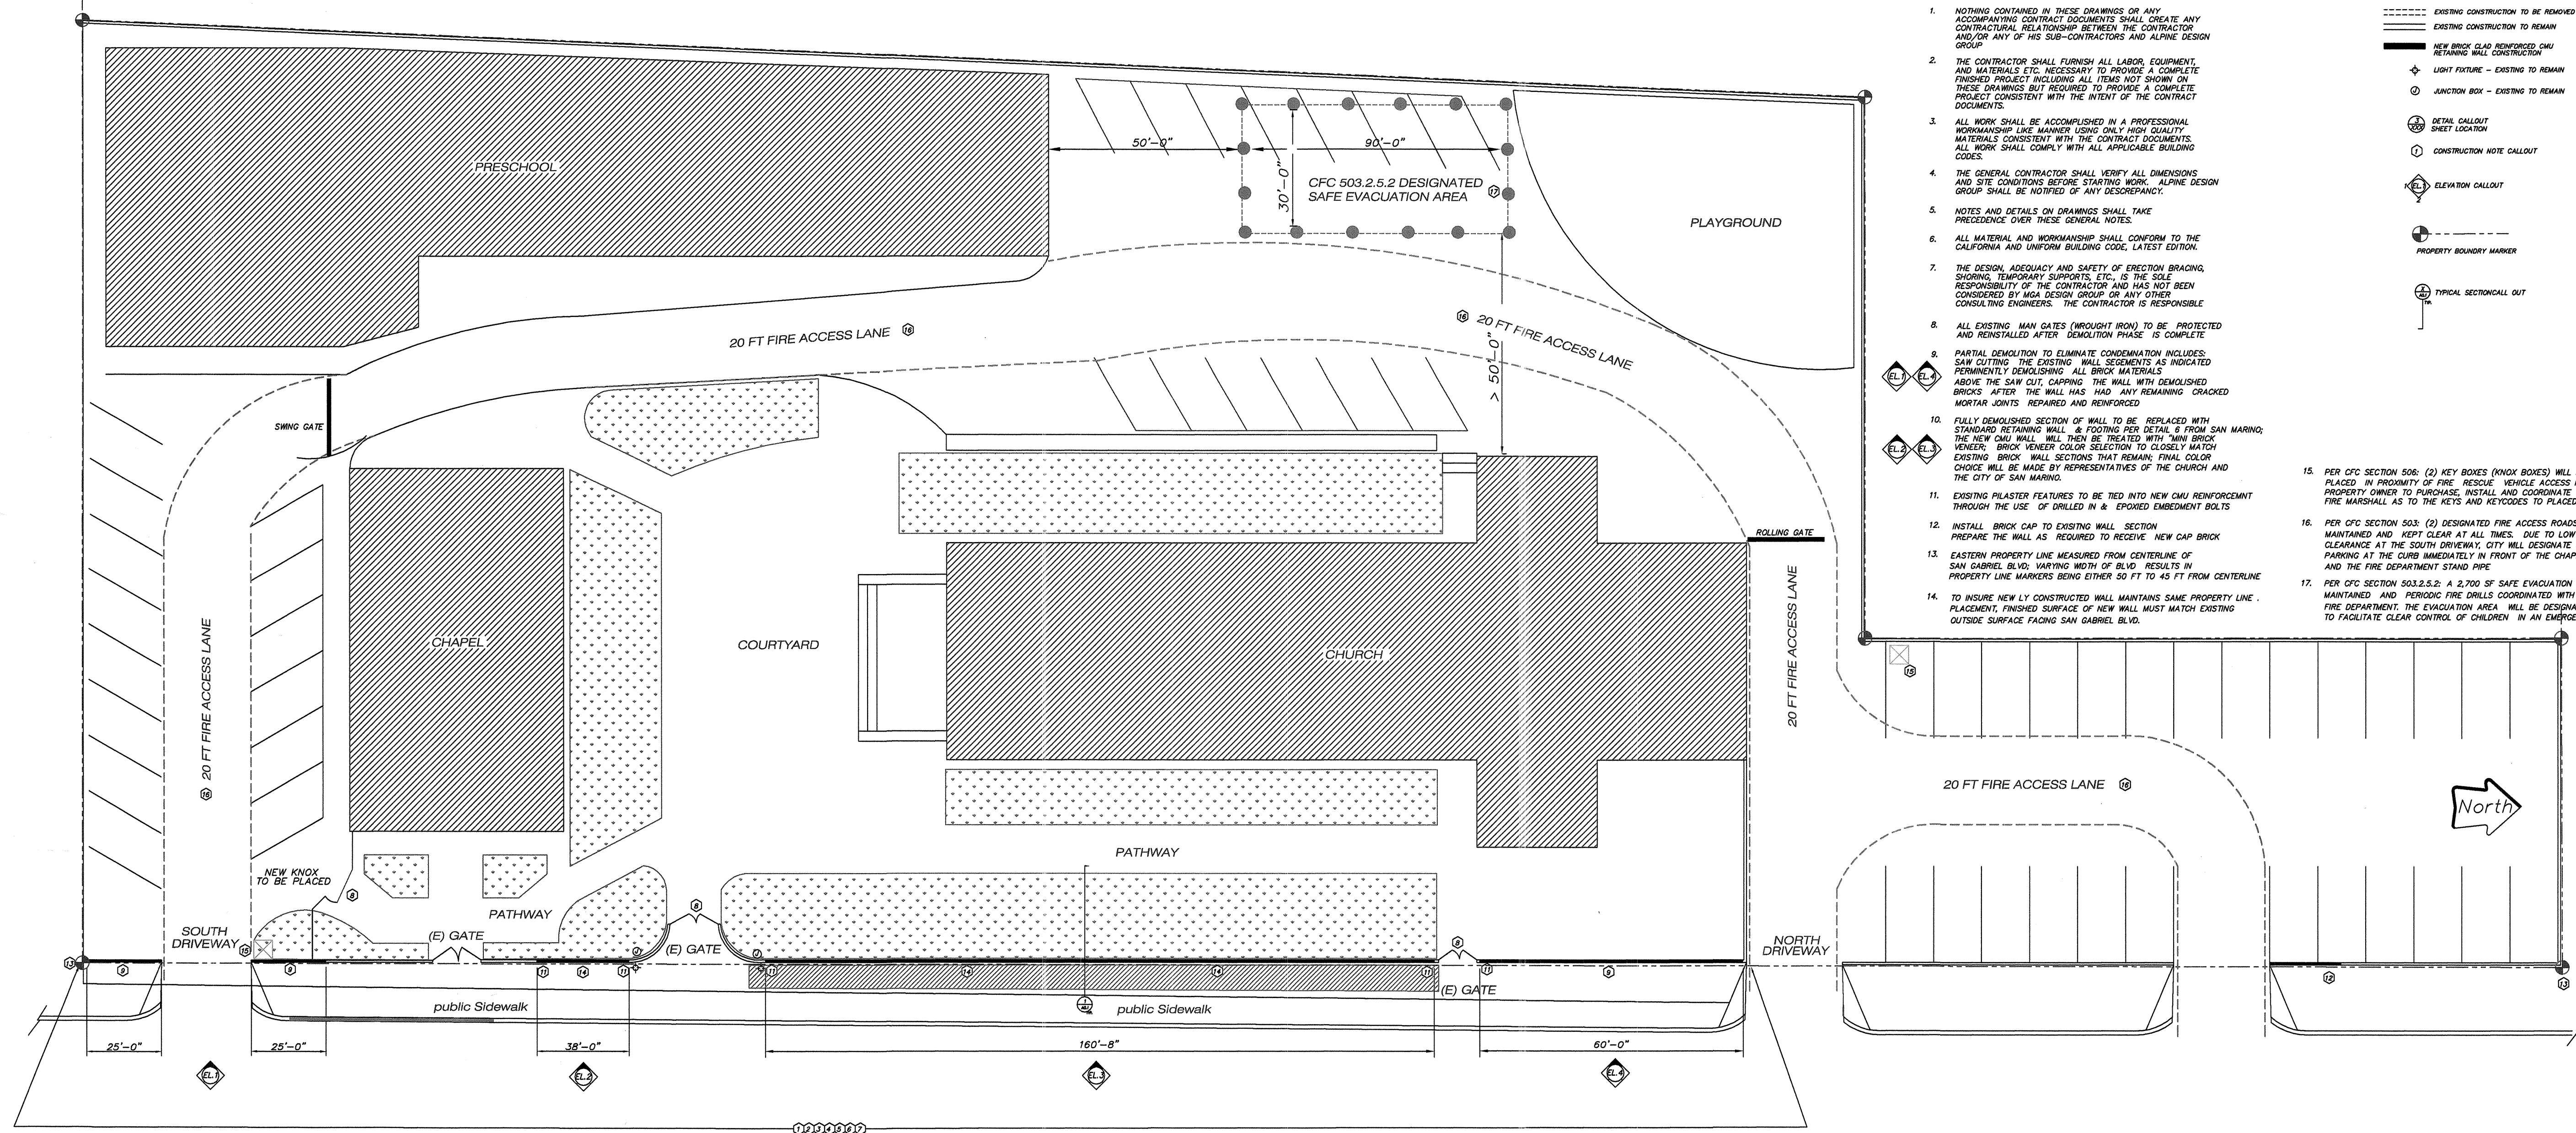

Alpine Group
2275 Huntington Drive Suite 414
SAN MARINO, CALIFORNIA 91768
PHONE (909) 286-1941 / FACSIMILE (909) 286-0699

REGISTERED PROFESSIONAL ENGINEER
CHARLES S. YOUNG, C.E.
No. C 048081
Exp. 4-12
STATE OF CALIFORNIA

ST. EDMUNDS CHURCH & PRESCHOOL
RETAINING WALL & MISC WALL REPAIRS
REPAIR BY REPLACEMENT PROJECT
1175 San Gabriel Blvd.
San Marino, California 91768

REV.	DATE	DESCRIPTION

SHEET TITLE
Demolition Plan, Dimension Plan
Construction Plan,
Information, Vicinity Map

REVIEWED AND APPROVED
SIGNATURE
DATE

SCALE
As Noted

DATE
08/5/13

JOB NO.
130805

REV. SHEET

SHEET NO.
A3.1